

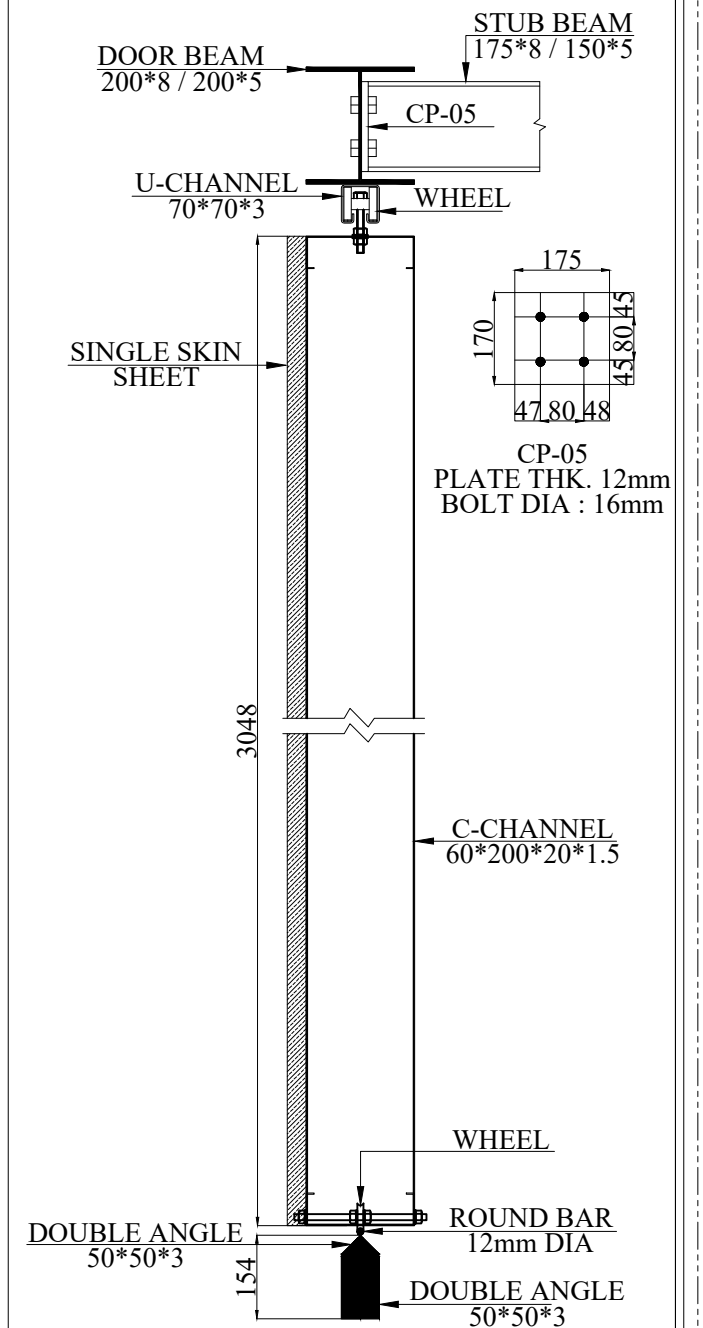


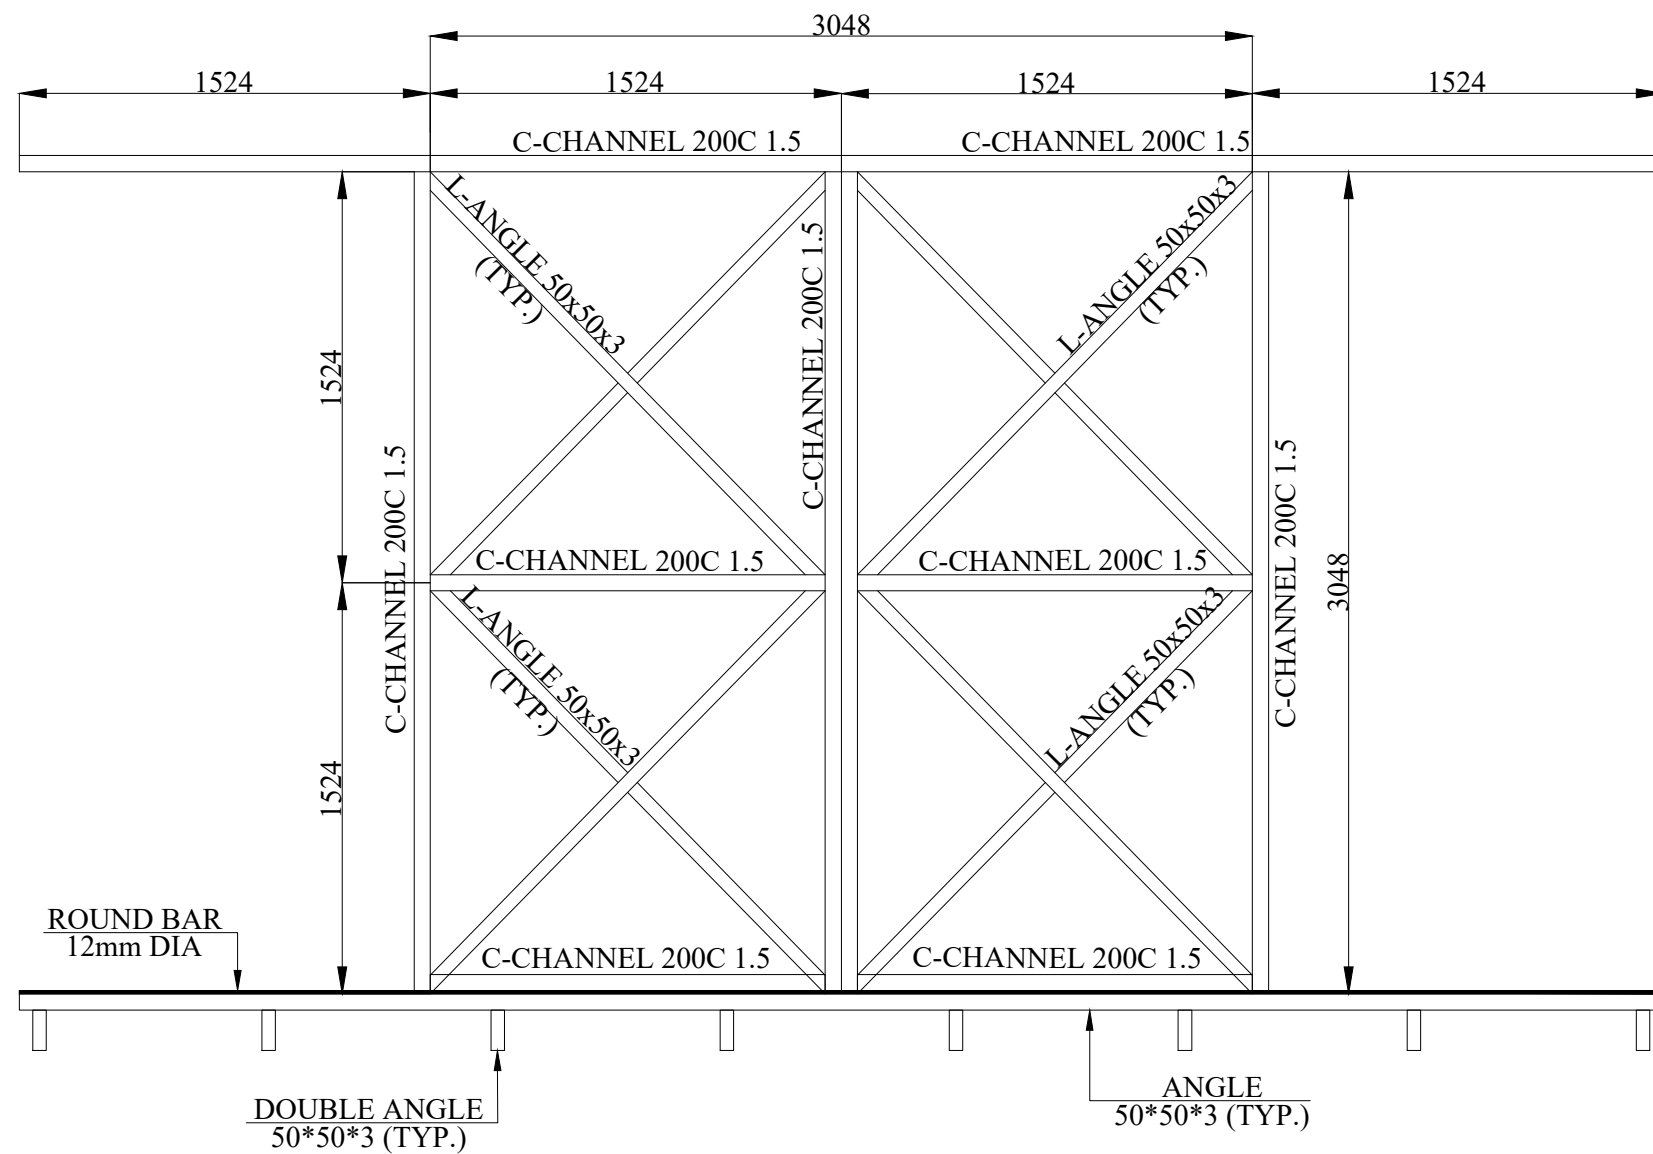


DOUBLE SLIDING DOOR
SECTION DETAILS

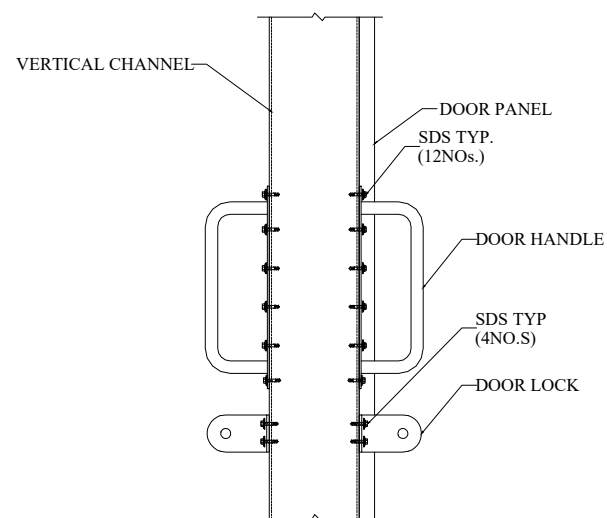

DOOR LOCK AND HANDLE DETAIL

S.NO	Description	Rev.	DATE
0.			
1.			
2.			

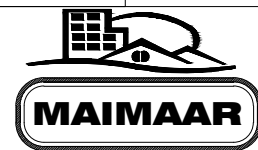

MAIMAAR STEEL Pvt.Ltd
238, Raiwind Road, Thokar Niaz Baig, Lahore, Pakistan
E-mail: nasir.abbas@maimaargroup.com
E-mail: maimaar.steel@gmail.com
Website: www.maimaargroup.com
E-mail: info@maimaargroup.com
Mob-1 : +(92-300) 807 4017 ,+(92-333) 807 1115

Drawing Title
DOOR DETAIL'S (TYP.)

LOCATION KASUR

REV	DESCRIPTION	DRAWN BY	CHK BY	APR BY
00	ISSUED FOR APPROVAL	IUMR	S.SAQ	S.SAQ
JOB NO .	MSPL-242	BUILDING #	DATE	DWG NO.
CLIENT	STARCH PACK	01	15-04-26	11