




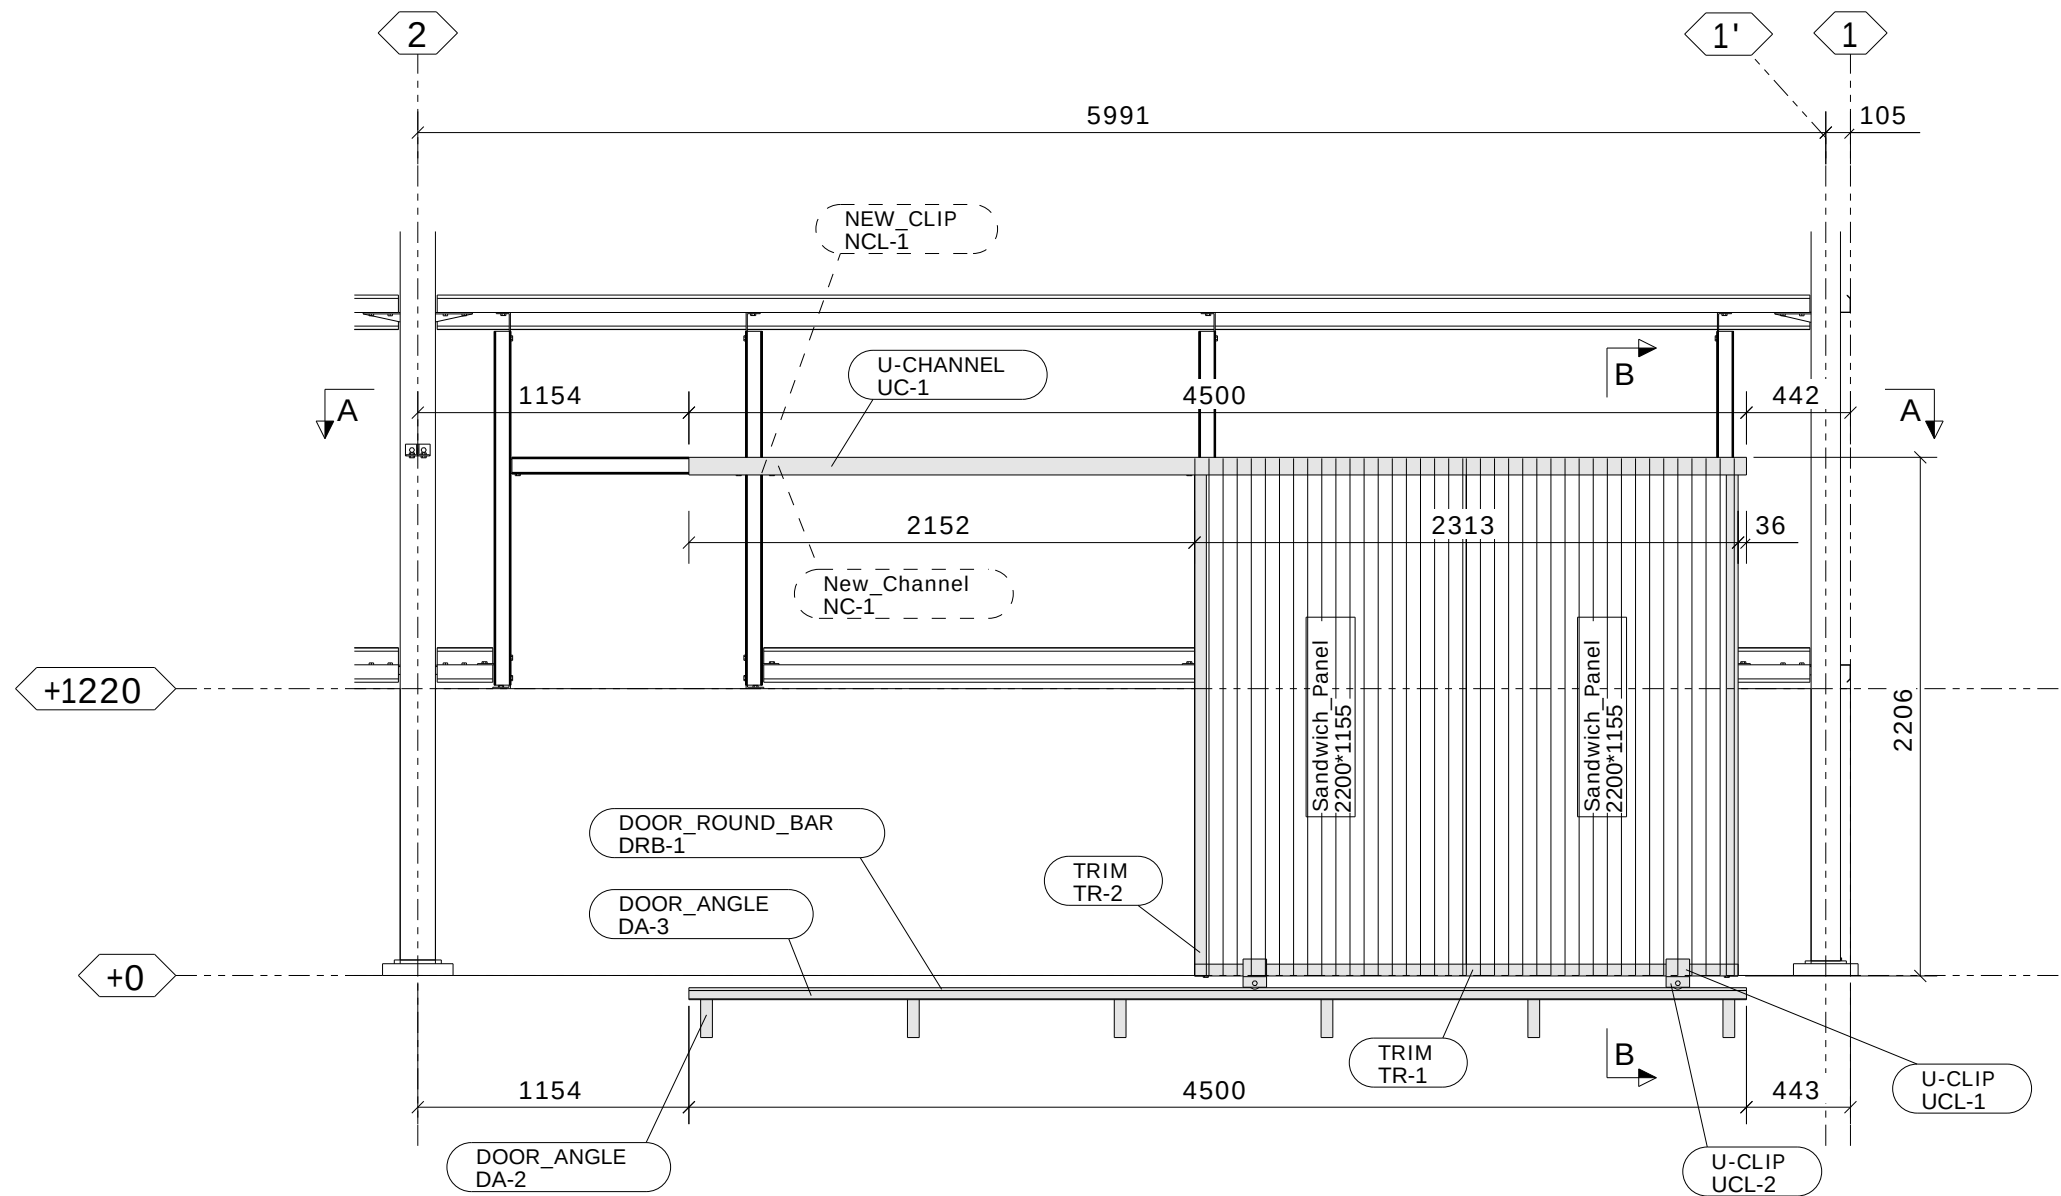

SINGLE SLIDING DOOR ELEVATION

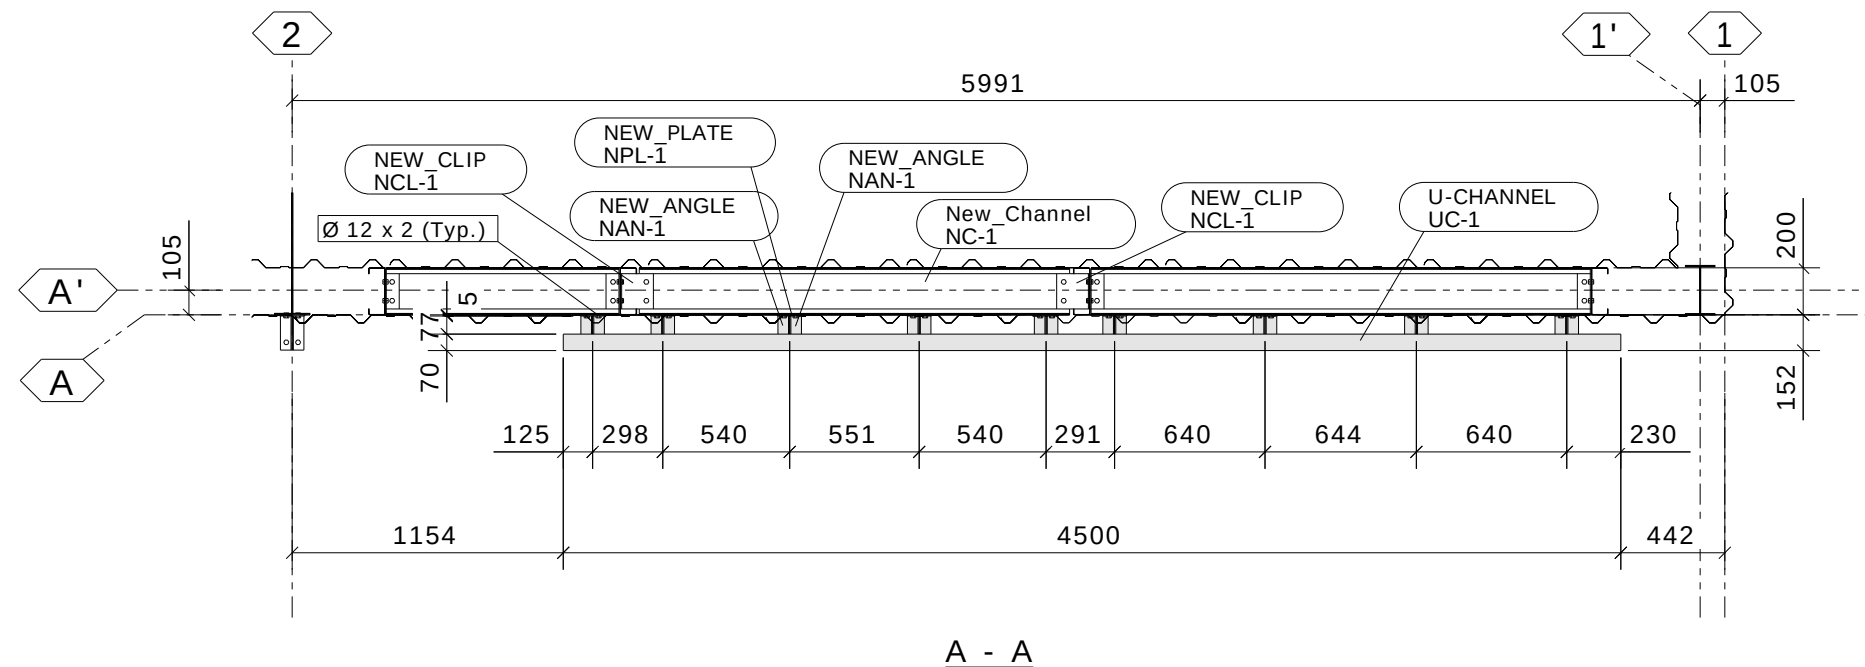

A - A

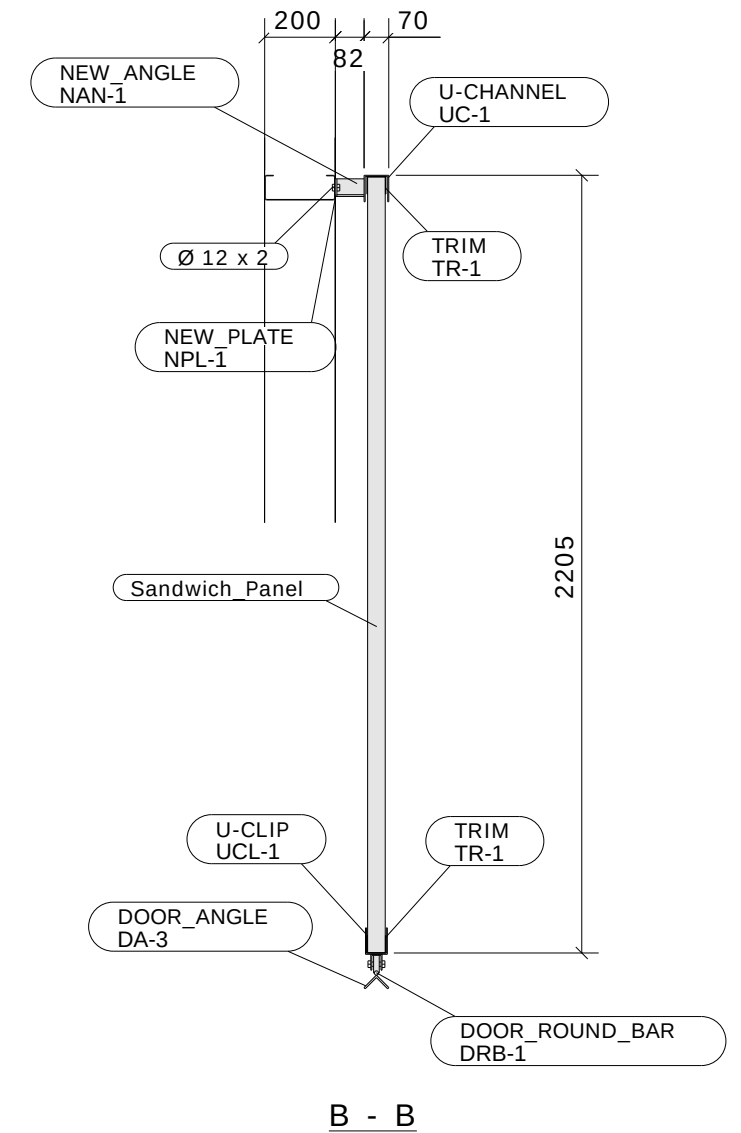

B - B

00	ISSUED FOR ERECTION	05-NOV-21
REV.	DESCRIPTION.	DATE
DRAWING TITLE:		
SINGLE SLIDING DOOR		
		
PROJECT NO.	DRAWING NO.	DRAWING TYPE.
MSPL-027-	SSD-01	ERECTION DRAWING
FILE PATH:	DATE:	
MSPL-027- Awan Sports_Bhan Stitching Hall No. 02 (Rev-0)	06.11.2021	