




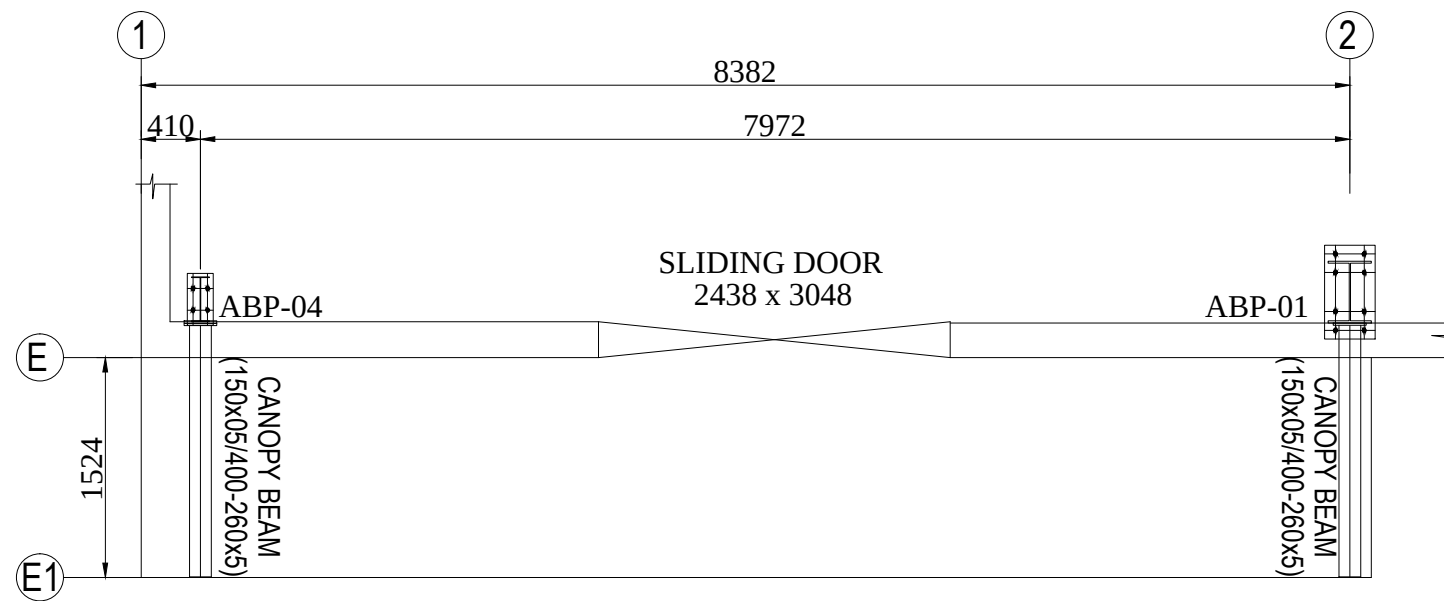

CANOPY LAYOUT PLAN

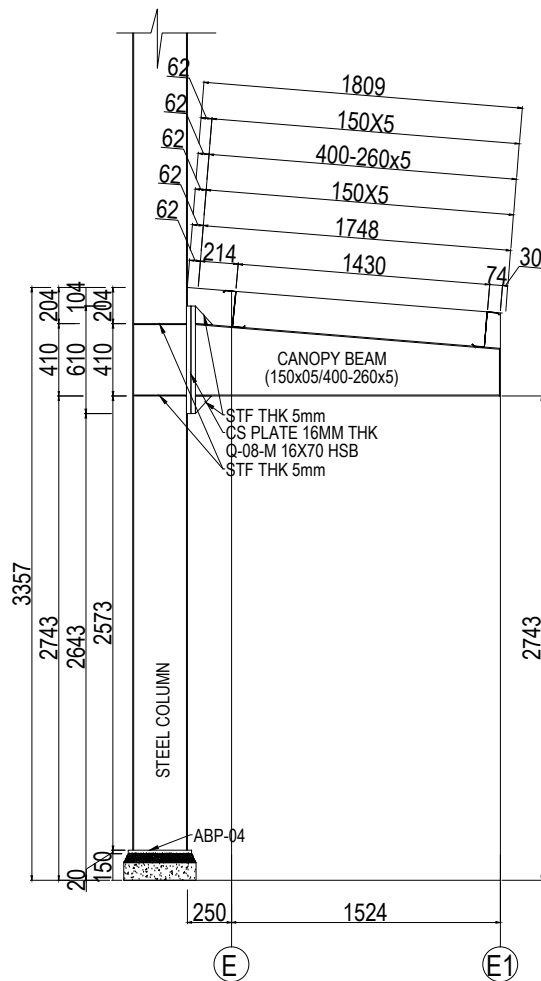

CANOPY CROSS SECTION @ 01
DETAIL (A-A)

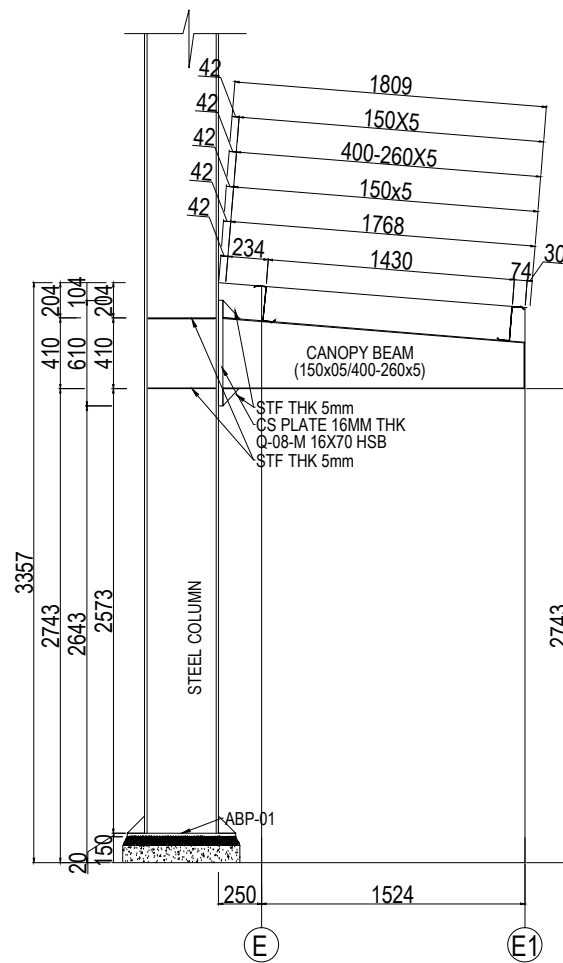

CANOPY CROSS SECTION @ 02
DETAIL (B-B)

STAIR CROSS SECTION

01	19-01-22	ISSUED FOR APPROVAL	R.A	YEA	YEA
00	11-11-21	ISSUED FOR APPROVAL	R.A	YEA	YEA
REV.	DATE	DESCRIPTION	DRWN BY	CHK BY	APR BY



MAIMAAR STEEL Pvt.Ltd
238, Raiwind Road, Thokar Niaz Baig ,LAHORE, Pakistan
E-mail: nasir.abbas@maimaargroup.com
E-mail: maimaar.steel@gmail.com
Website: www.maimaargroup.com
E-mail: nasir.abbas@maimaargroup.com
Mob-1 : +(92-300) 807 4017 , +(92-333) 807 1115

JOB NO./QUOTE NO.	MSPL-030	BLDG #.	01
PROJECT NAME	INITIAL PADDLE SANDING HALL		
CUSTOMER	AWAN SPORTS		
JOBSITE LOCATION	SIALKOT		
STAIR 02 PLAN AND SECTION			DWG. NO.
			18

FOR APPROVAL :

IN ORDER TO SCHEDULE THIS PROJECT
IN AN EFFICIENT MANNER , KINDLY
RETURN THESE DRAWINGS WITH YOUR
ANY CHANGES MADE AFTER THE
COMMENTS MARKED IN RED

APPROVAL OF THESE DRAWINGS MAY
DELAY THE FABRICATION SCHEDULE AND
SUBSEQUENTLY THE DELIVERY OF THE
BUILDING.

PLEASE TICK MARK ONLY ONE OF THE FOLLOWING

☐ " APPROVED AS IS "

☐ " APPROVED AS NOTED "

☐ " RESUBMIT AS NOTED "

APPROVE : _____

SIGNATURE: _____

DATE : _____