


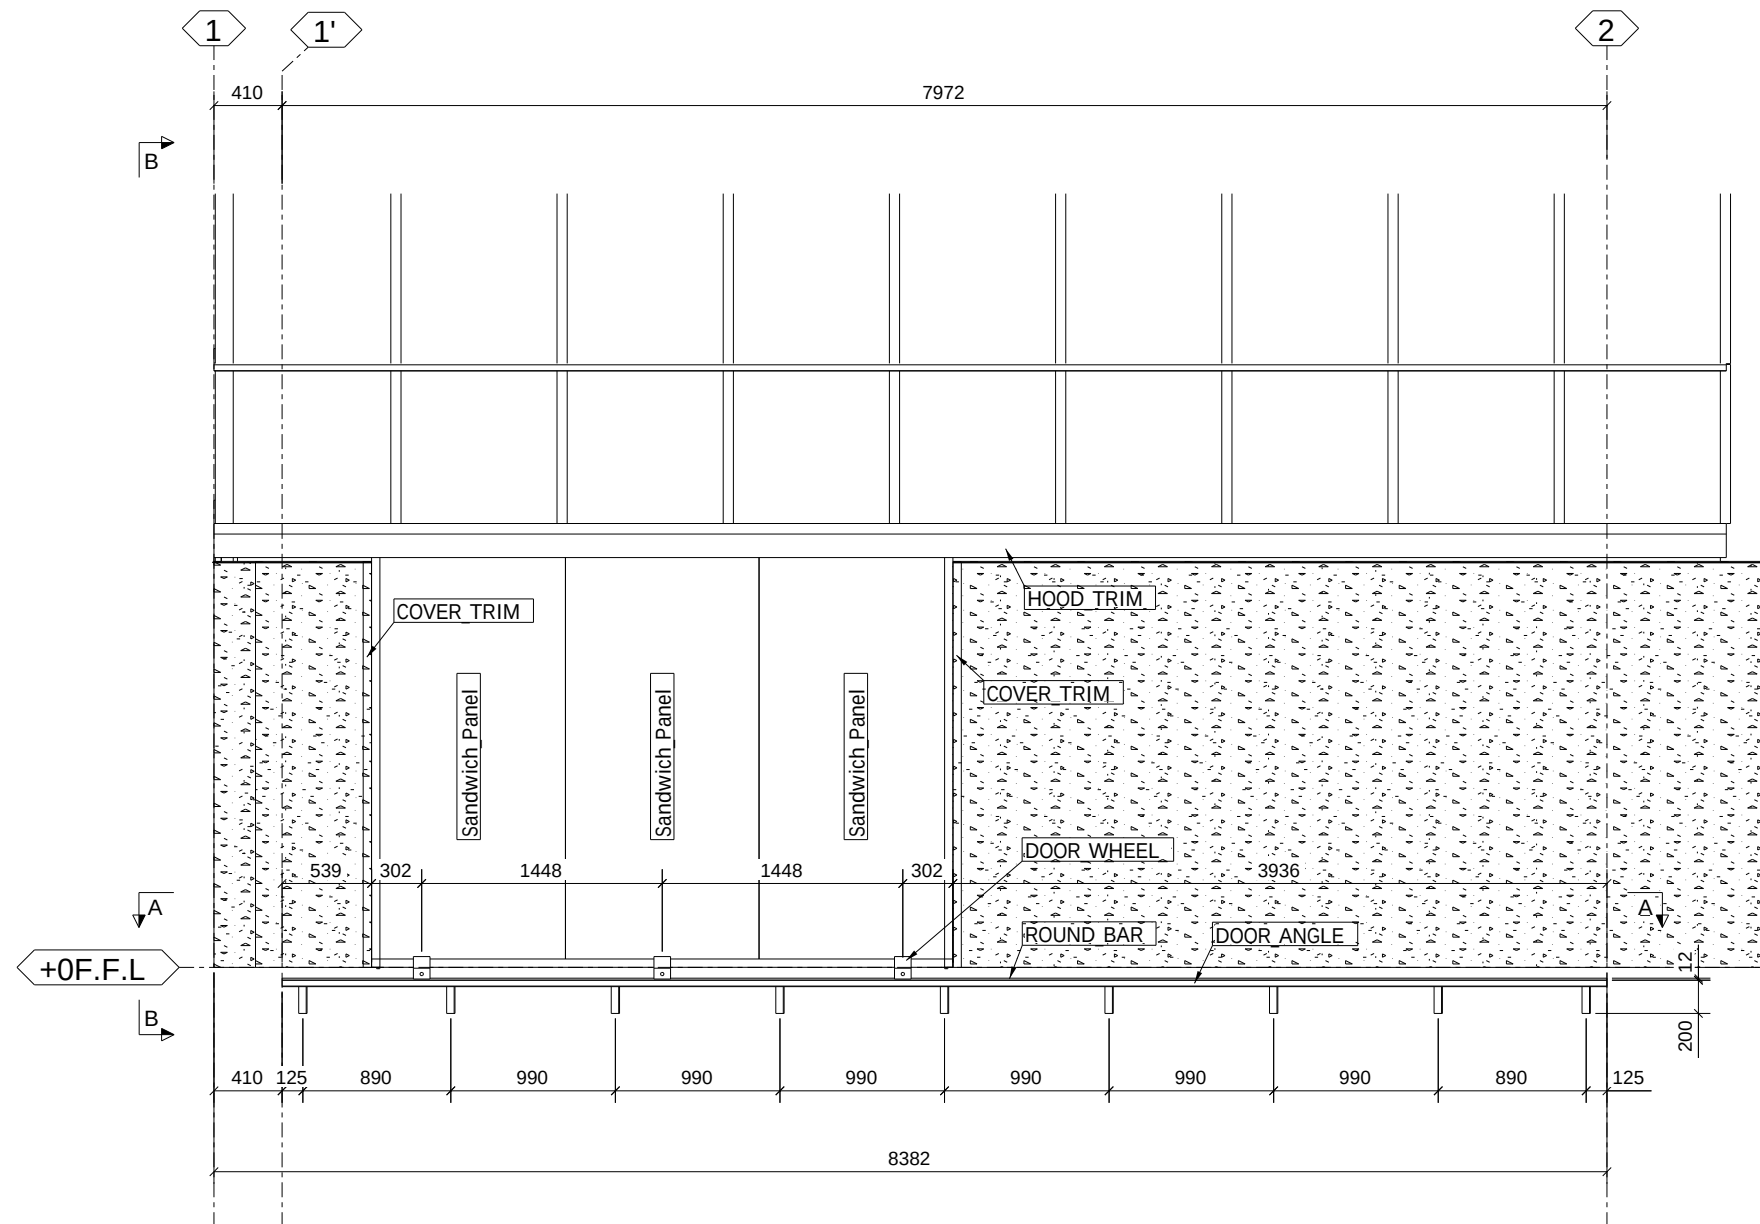


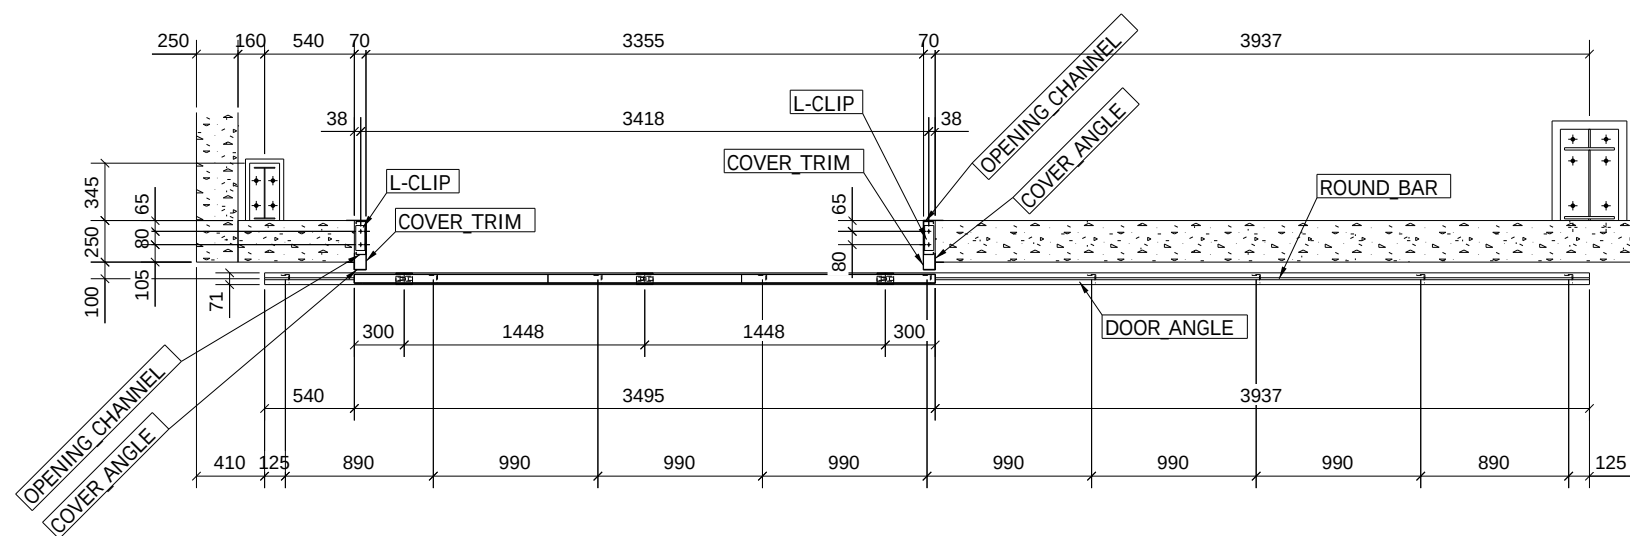

SLIDING DOOR ELEVATION

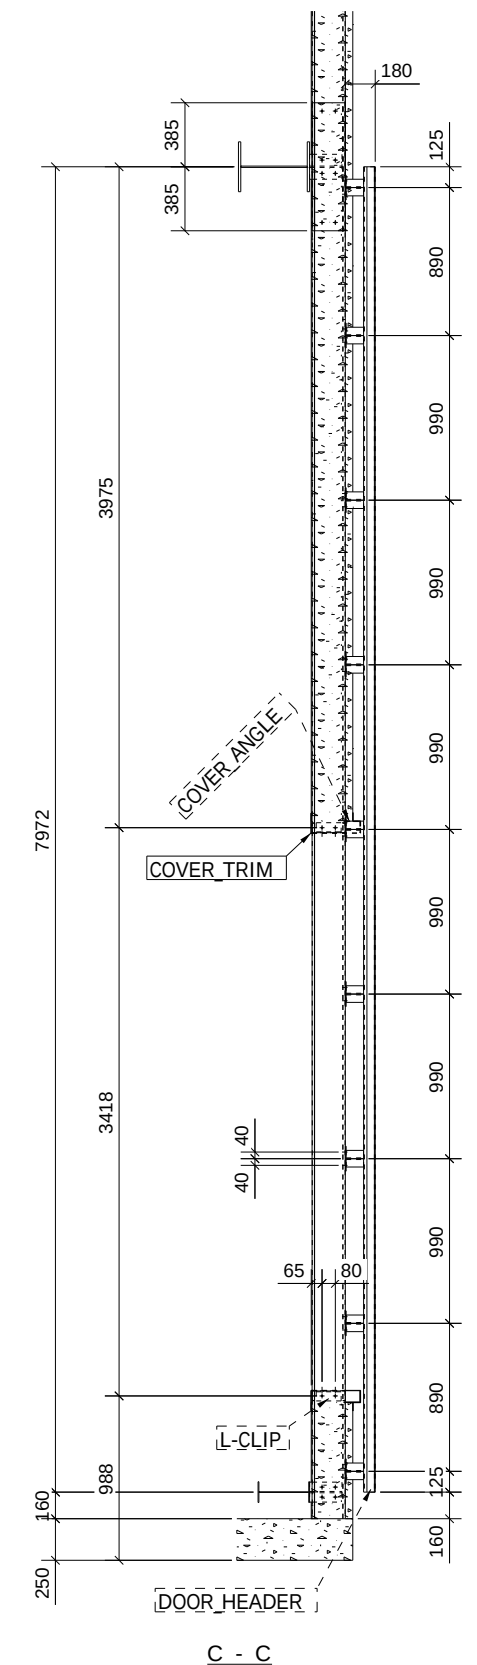

A - A

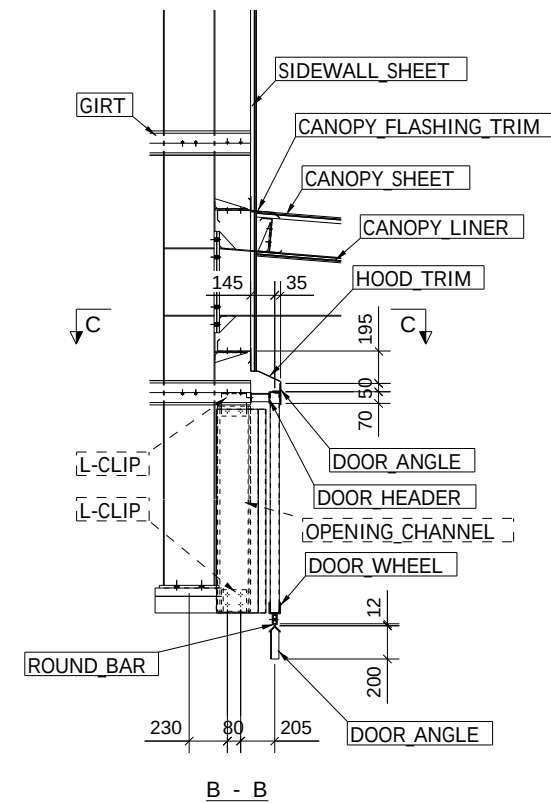

00	ISSUED FOR ERECTION	01-04-2022
REV.	DESCRIPTION.	DATE
DRAWING TITLE: SLIDING DOOR ELEVATION & SECTIONS		
 MAIMAAR ENGINEERS & CONTRACTORS		
PROJECT NO. MSPL-030	DRAWING NO. SDS-01	DRAWING TYPE. ERECTION DRAWING
FILE PATH: MSP-030-Awan Sports (Initial Paddie Sanding Hall) -IF		DATE: 01.04.2022