


PROPOSAL NO.	MSPL-002
APPROVAL NO.	MSPL-121




(MAIMAAR STEEL Pvt.Ltd)

238, First Floor Lalazar Commercial Area
Raiwind Road, Thokar Niaz Baig ,Lahore, Pakistan
E-mail: nasir.abbas@maimaargroup.com
E-mail: maimaar.steel@gmail.com


Website: www.maimaargroup.com
E-mail: nasir.abbas@maimaargroup.com
Mob-1 : +(92-300) 807 4017 ,+(92-333) 807 1115

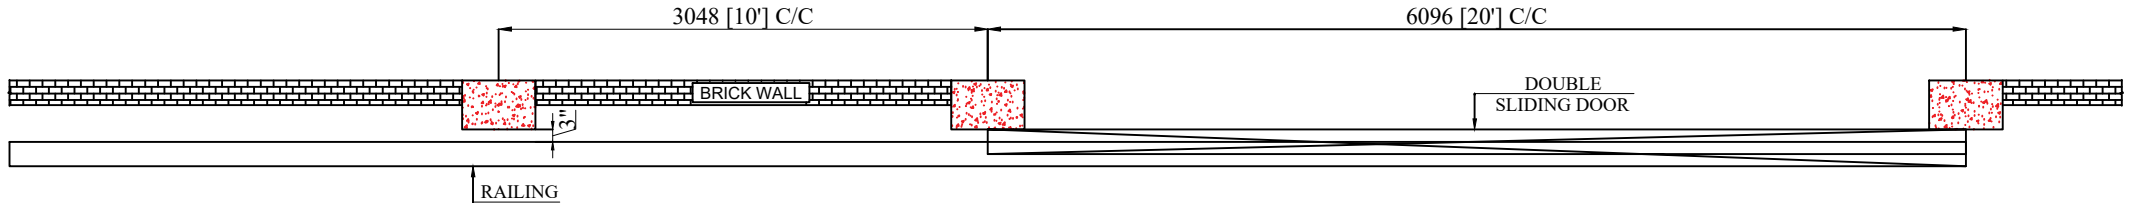

DOOR PLAN

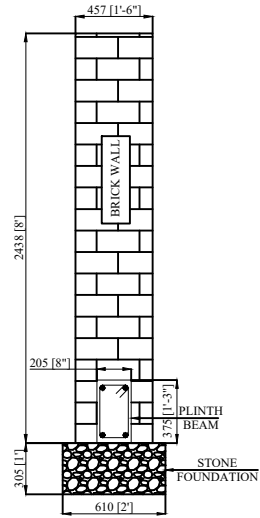

CROSS SECTION

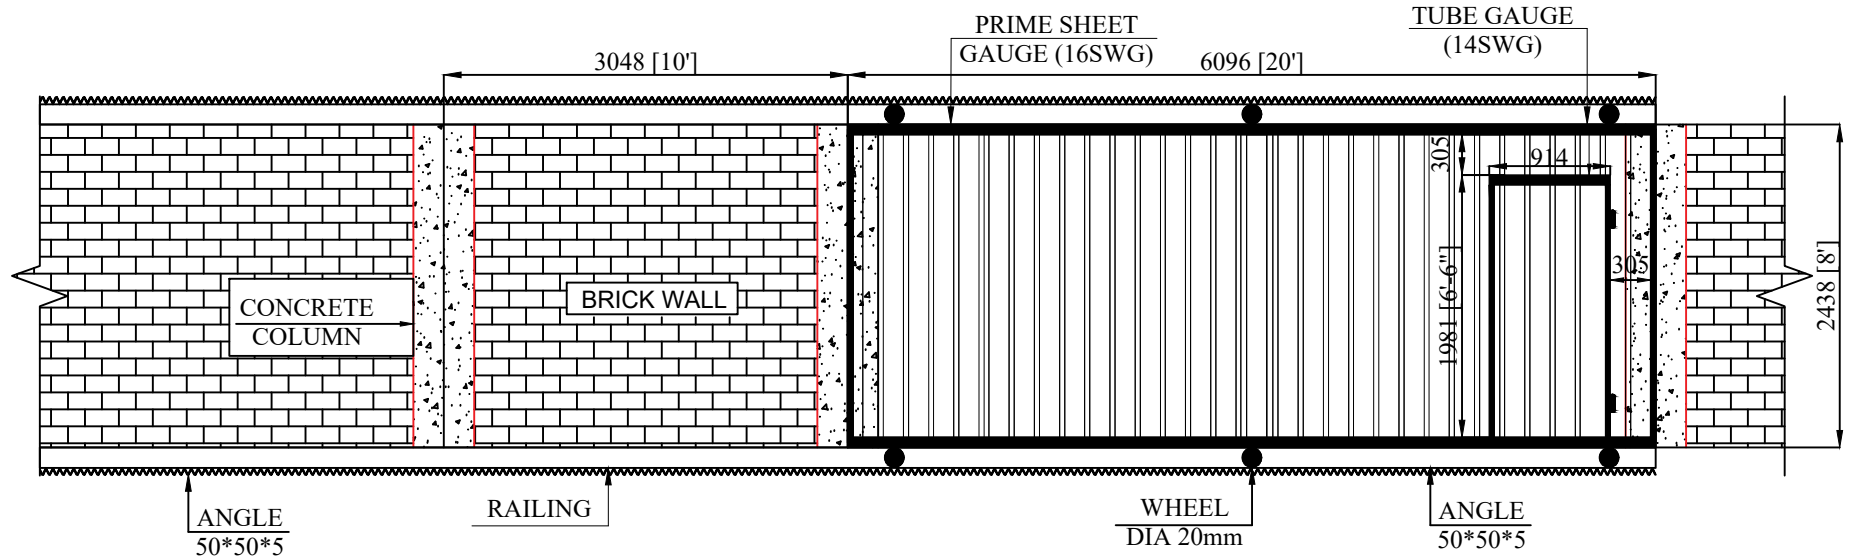

DOOR ELEVATION

DOOR DETAILS

FOR APPROVAL :

IN ORDER TO SCHEDULE THIS PROJECT
IN AN EFFICIENT MANNER , KINDLY
RETURN THESE DRAWINGS WITH YOUR
ANY CHANGES MADE AFTER THE
COMMENTS MARKED IN RED
APPROVAL OF THESE DRAWINGS MAY
DELAY THE FABRICATION SCHEDULE AND
SUBSEQUENTLY THE DELIVERY OF THE
BUILDING.
PLEASE TICK MARK ONLY ONE OF THE FOLLOWING

- ☐ " APPROVED AS IS "
- ☐ " APPROVED AS NOTED"
- ☐ " RESUBMIT AS NOTED "

APPROVE : _____

SIGNATURE: _____

DATE : _____

REV.	DATE	DESCRIPTION	DRWN BY	CHK BY	APR BY
00	28-Jun-24	ISSUED FOR APPROVAL	I.U	KAS	NAS



MAIMAAR STEEL Pvt.Ltd
238, Raiwind Road, Thokar Niaz Baig ,LAHORE, Pakistan
E-mail: nasir.abbas@maimaargroup.com
E-mail: maimaar.steel@gmail.com
Website: www.maimaargroup.com
E-mail: nasir.abbas@maimaargroup.com
Mob-1 : +(92-300) 807 4017 ,+(92-333) 807 1115

JOB NO.	MSPL-121	BLDG #.	01
PROJECT NAME	FRUITS PROCESSING COLD STORE FACILITY		
CUSTOMER	45 ENGINEER DIVISION		
JOBSITE LOCATION	SAKARDU		

DOOR DETAILS

DWG. NO.

01