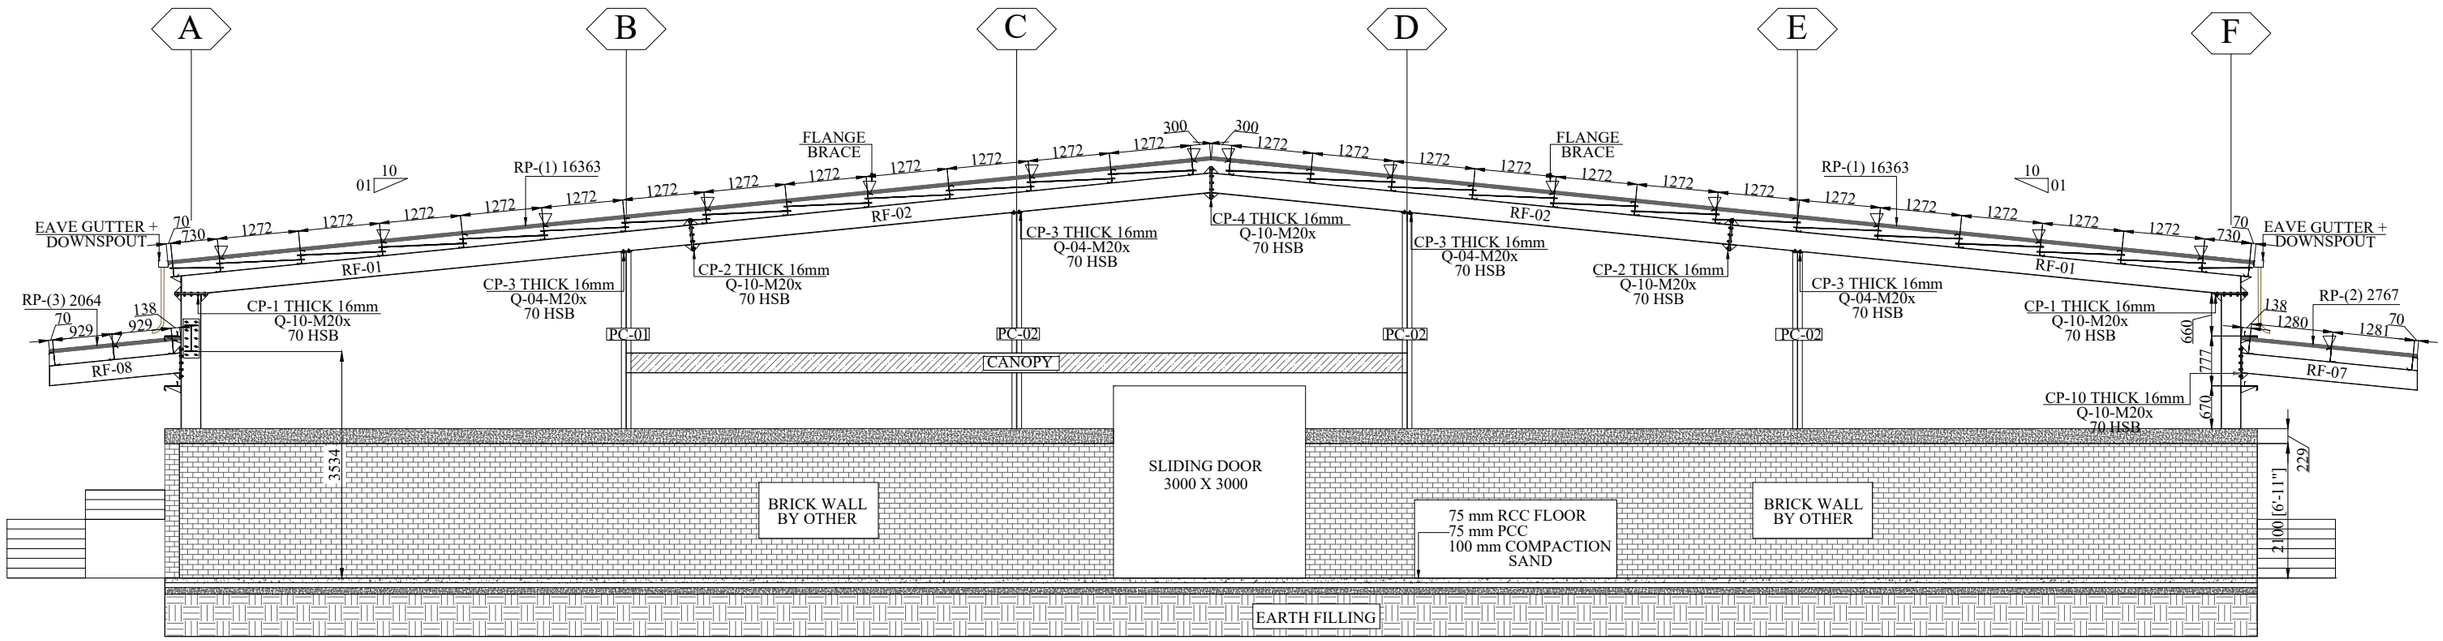

ELEVATION @ GRID-07

FOR APPROVAL :

IN ORDER TO SCHEDULE THIS PROJECT IN AN EFFICIENT MANNER , KINDLY RETURN THESE DRAWINGS WITH YOUR ANY CHANGES MADE AFTER THE COMMENTS MARKED IN RED APPROVAL OF THESE DRAWINGS MAY DELAY THE FABRICATION SCHEDULE AND SUBSEQUENTLY THE DELIVERY OF THE BUILDING.

PLEASE TICK MARK ONLY ONE OF THE FOLLOWIMG

☐ " APPROVED AS IS "
☐ " APPROVED AS NOTED"
☐ " RESUBMIT AS NOTED "

APPROVE : _____

SIGNATURE: _____

DATE : _____

REV	DATE	DESCRIPTION	DRAWN BY	CHK BY	APR BY
06	05-Sep-24	ISSUED FOR APPROVAL	IU	KAS	NAS

MAIMAAR

MAIMAAR STEEL Pvt.Ltd
238, Raiwind Road, Thokar Niaz Baig, Lahore, Pakistan
E-mail: nasir.abbas@maimaargroup.com
E-mail: maimaar.steel@gmail.com
Website: www.maimaargroup.com
E-mail: info@maimaargroup.com
Mob-1 : +(92-300) 807 4017 ,+(92-333) 807 1115

JOB NO./QUOTE NO.	MSPL-135	BUILDING #	01
PROJECT NAME	DRY FRUITS PROCESSING DERA ISMAIL KHAN		
CUSTOMER	45 ENGINEER DIVISION		
JOB SITE LOCATION	DERA ISMAIL KHAN		

ELEVATION @ GRID-07

DWG NO. E05