


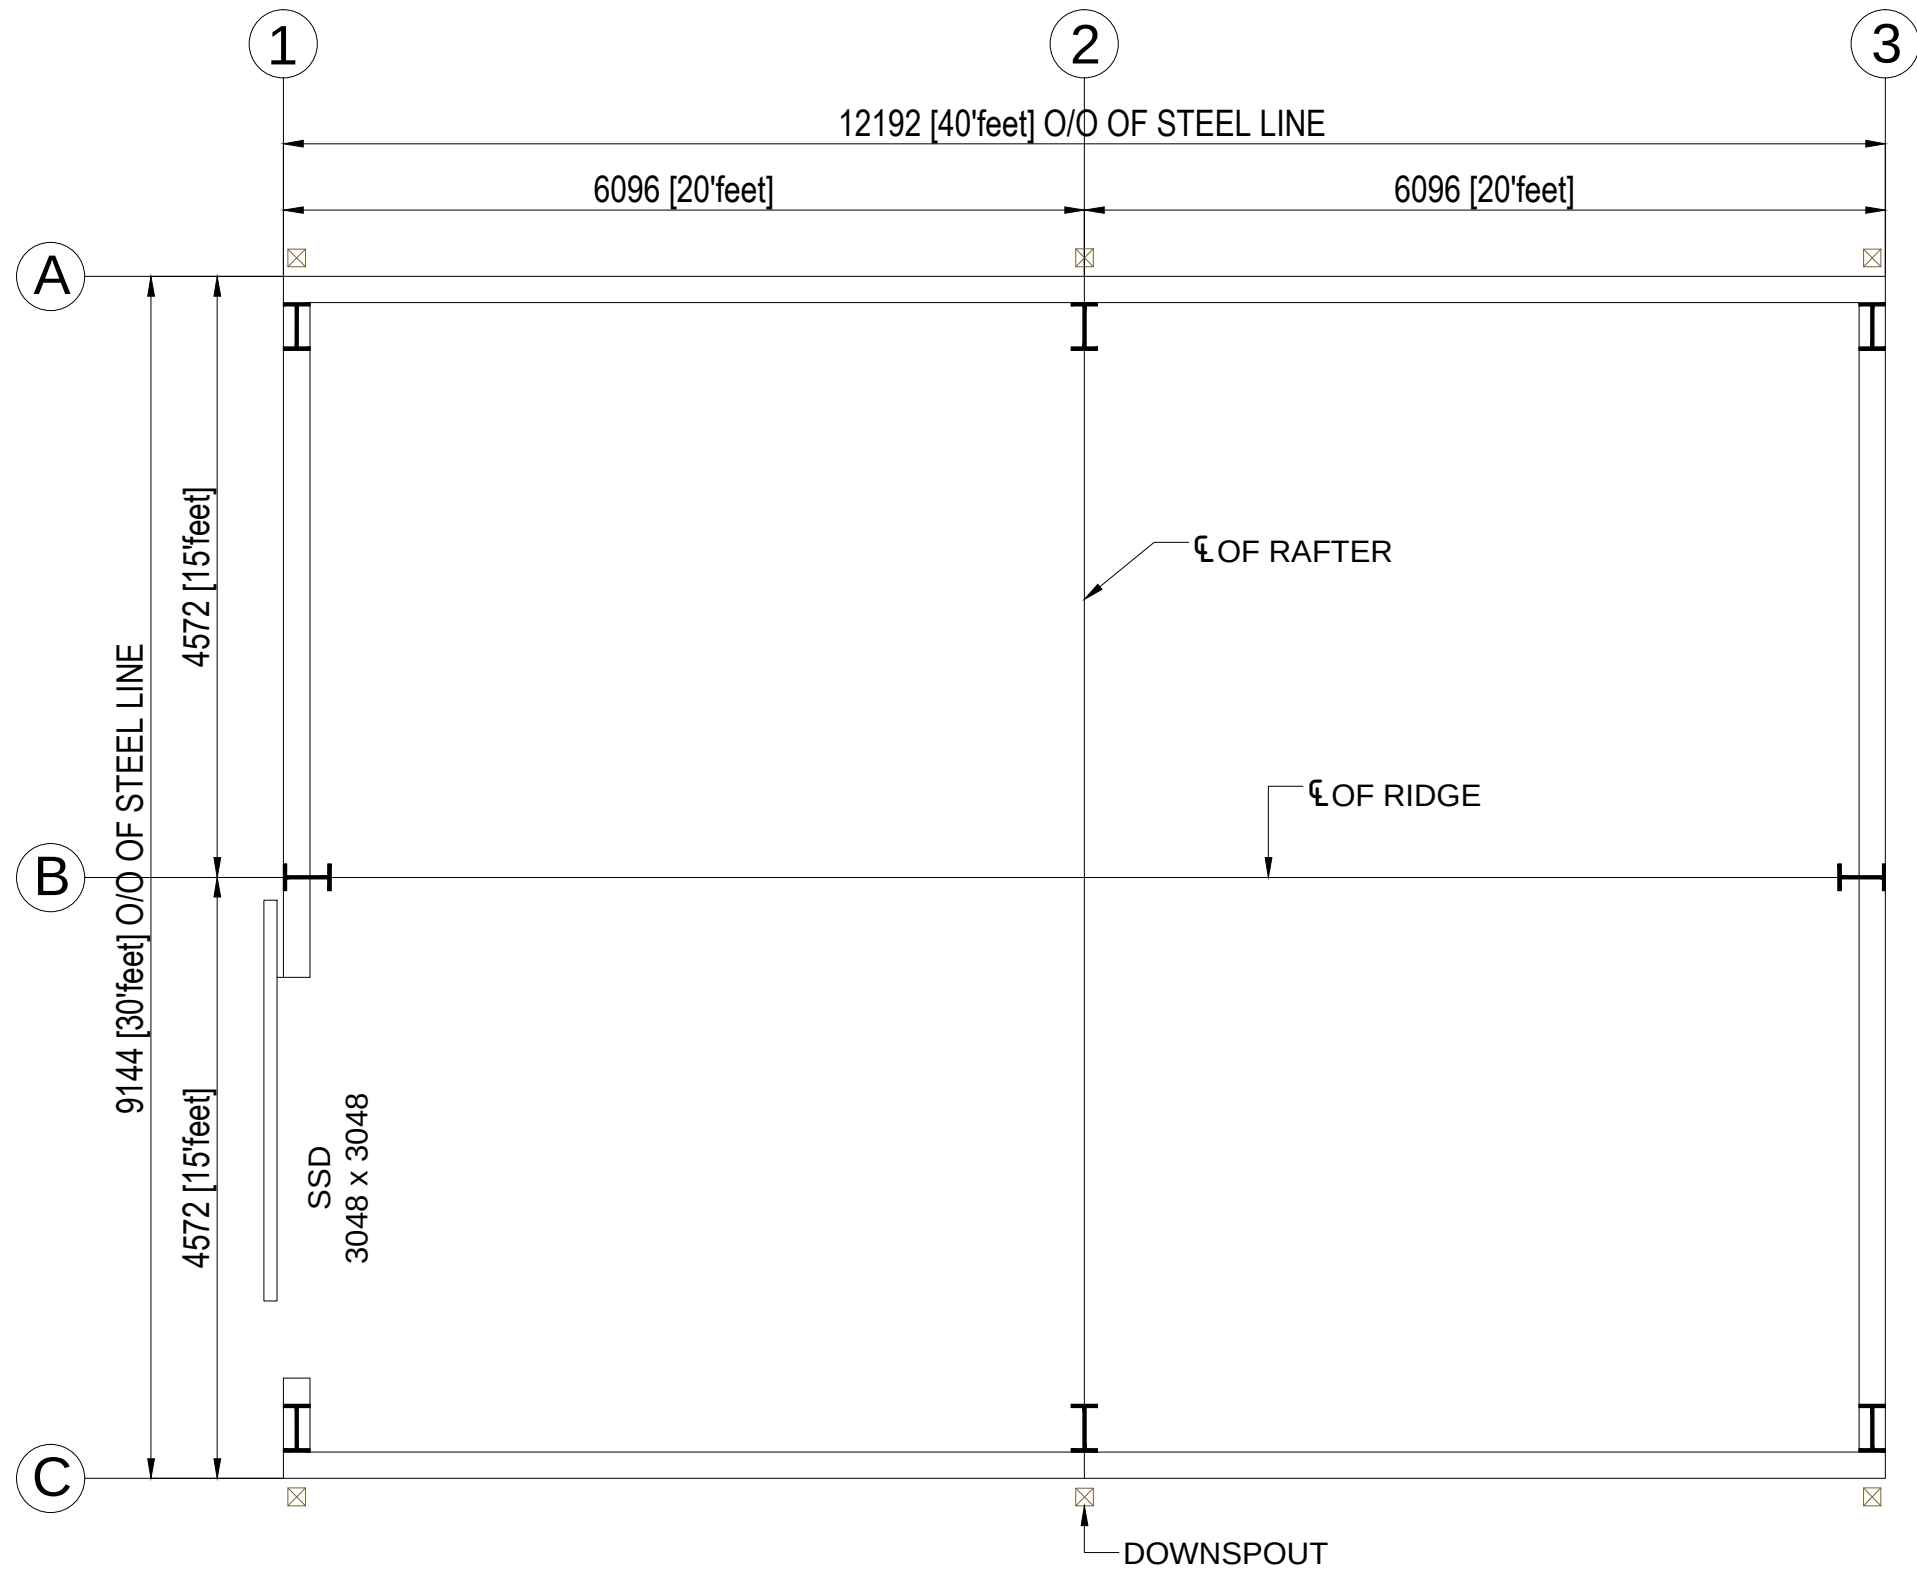

COLUMN LAYOUT PLAN

GENERAL NOTES		BUILDING ACCESSORIES		BUILDING DESIGN LOADS		BUILDING DESIGN CODES		PROJECT INFORMATION				
ALL DIMENSIONS ARE IN 'MM & FEET'. THIS IS PROPOSAL DRAWING ONLY, NOT FOR CONSTRUCTION. THIS DRAWING IS NOT TO SCALE.		01. 0.5mm PPGI		LIVE LOAD = 0.57 KN/SQ.M.		DESIGN CODES AS PER AISC		QUOTE NO. MSPL-022-20		BLDG. NO. : 01		
		02. SINGLE SLIDING DOOR (3048 x 3048mm)		WIND SPEED = 135 KM/HR.		LOADS APPLICATION AS PER MBMA		BLDG. NAME BOILER SHED				
				COLLATERAL LOAD =0.00		COLD FORMED DESIGN CODES AS PER AISI		REV. NO.	DRN. BY	CHK. BY	DATE	SHEET NO.
				EXPOSURE = B				00	NBL	UBD	05-03-2020	PRO-01
								--	--	--	--	--

MAIMAAR



MAIMAAR STEEL Pvt.Ltd

105, Raiwind Road, Thokar Niaz Baig, Lahore, Pakistan

E-mail: nasir.abbas@maimaargroup.com

E-mail: maimaar.steel@gmail.com

Website: www.maimaargroup.com

E-mail: nasir.abbas@maimaargroup.com

Mob-1 : +(92-300) 807 4017 , +(92-333) 807 1115