


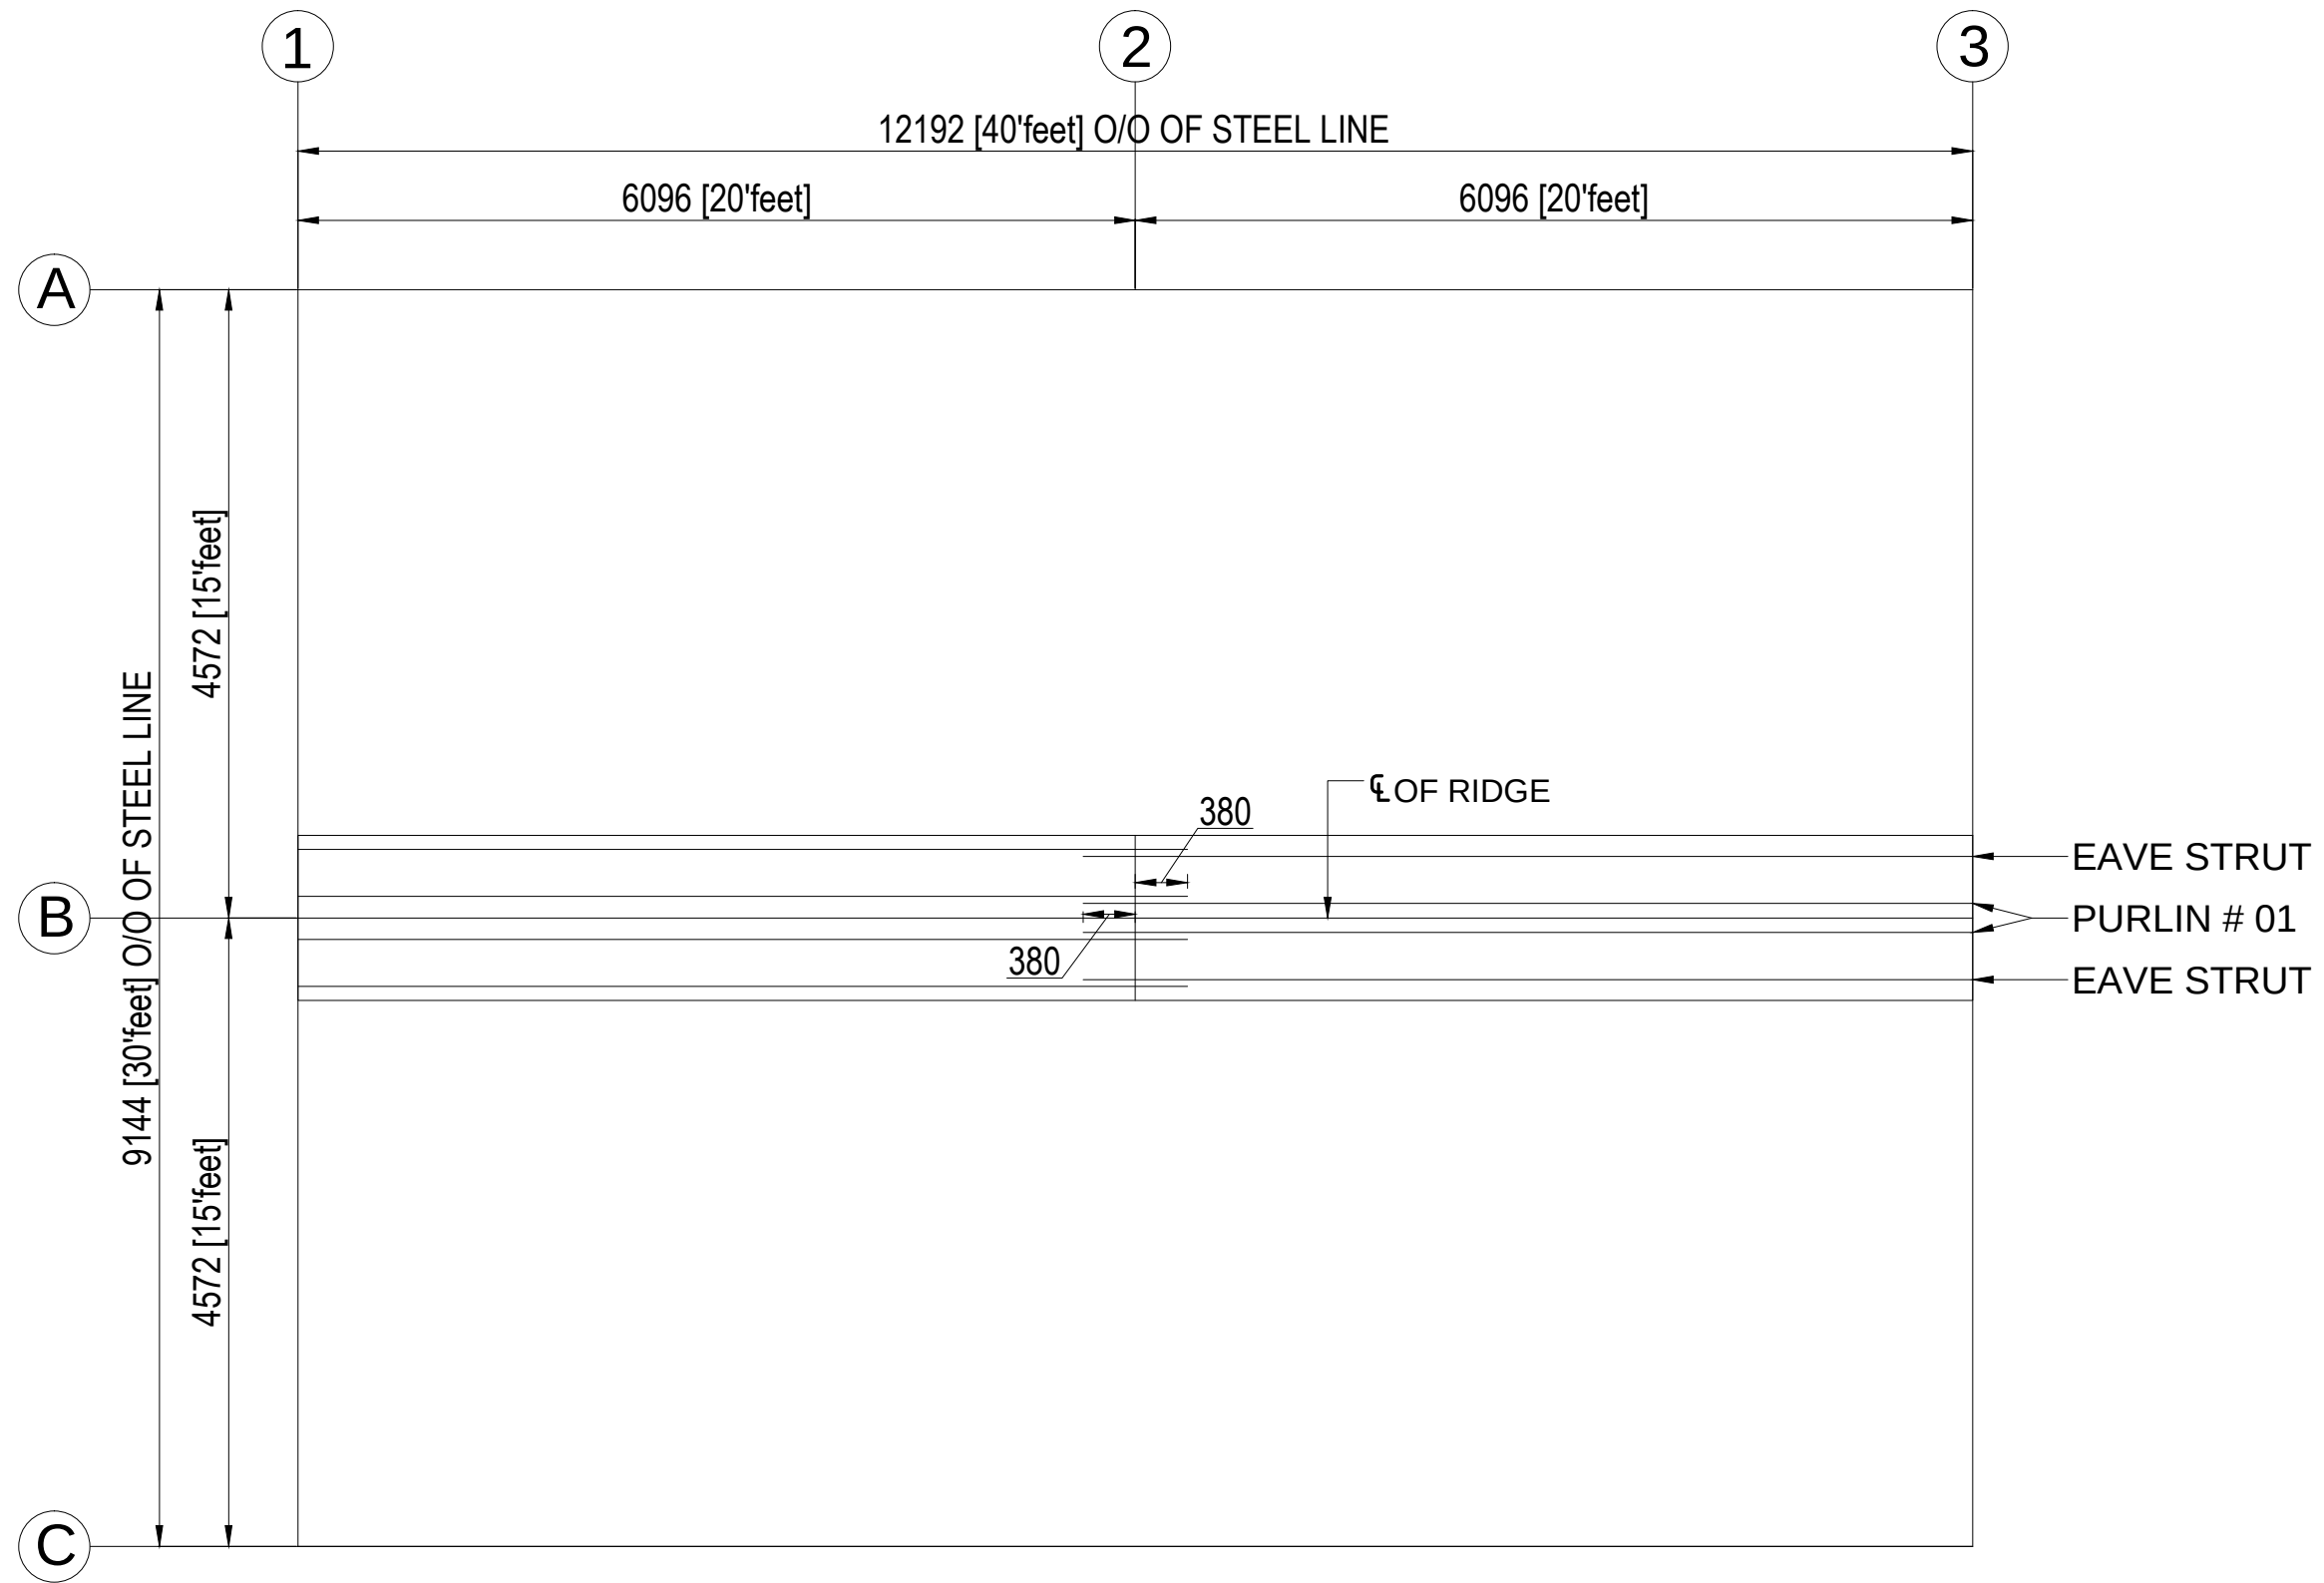

ROOF MONITOR FRAMING PLAN

GENERAL NOTES

ALL DIMENSIONS ARE IN 'MM & FEET'.  
THIS IS PROPOSAL DRAWING ONLY,  
NOT FOR CONSTRUCTION.  
THIS DRAWING IS NOT TO SCALE.

BUILDING ACCESSORIES

01. 0.5mm PPGI  
02. SINGLE SLIDING DOOR  
(3048 x 3048mm)

BUILDING DESIGN LOADS

LIVE LOAD = 0.57 KN/SQ.M.  
WIND SPEED = 135 KM/HR.  
COLLATERAL LOAD = 0.00  
EXPOSURE = B

BUILDING DESIGN CODES

DESIGN CODES AS PER AISC  
LOADS APPLICATION AS PER MBMA  
COLD FORMED DESIGN CODES AS PER AISI

PROJECT INFORMATION

|            |             |         |            |           |      |
|------------|-------------|---------|------------|-----------|------|
| QUOTE NO.  | MSPL-022-20 |         |            | BLDG. NO. | : 01 |
| BLDG. NAME | BOILER SHED |         |            |           |      |
| REV. NO.   | DRN. BY     | CHK. BY | DATE       | SHEET NO. |      |
| 00         | NBL         | UBD     | 05-03-2020 | PRO-04    |      |
| --         | --          | --      | --         | --        |      |



MAIMAAR STEEL Pvt.Ltd  
105, Raiwind Road, Thokar Niaz Balg, Lahore, Pakistan  
E-mail: nasir.abbas@maimaargroup.com  
E-mail: maimaar.steel@gmail.com  
Website: www.maimaargroup.com  
E-mail: nasir.abbas@maimaargroup.com  
Mob-1 : +(92-300) 807 4017 , +(92-333) 807 1115