


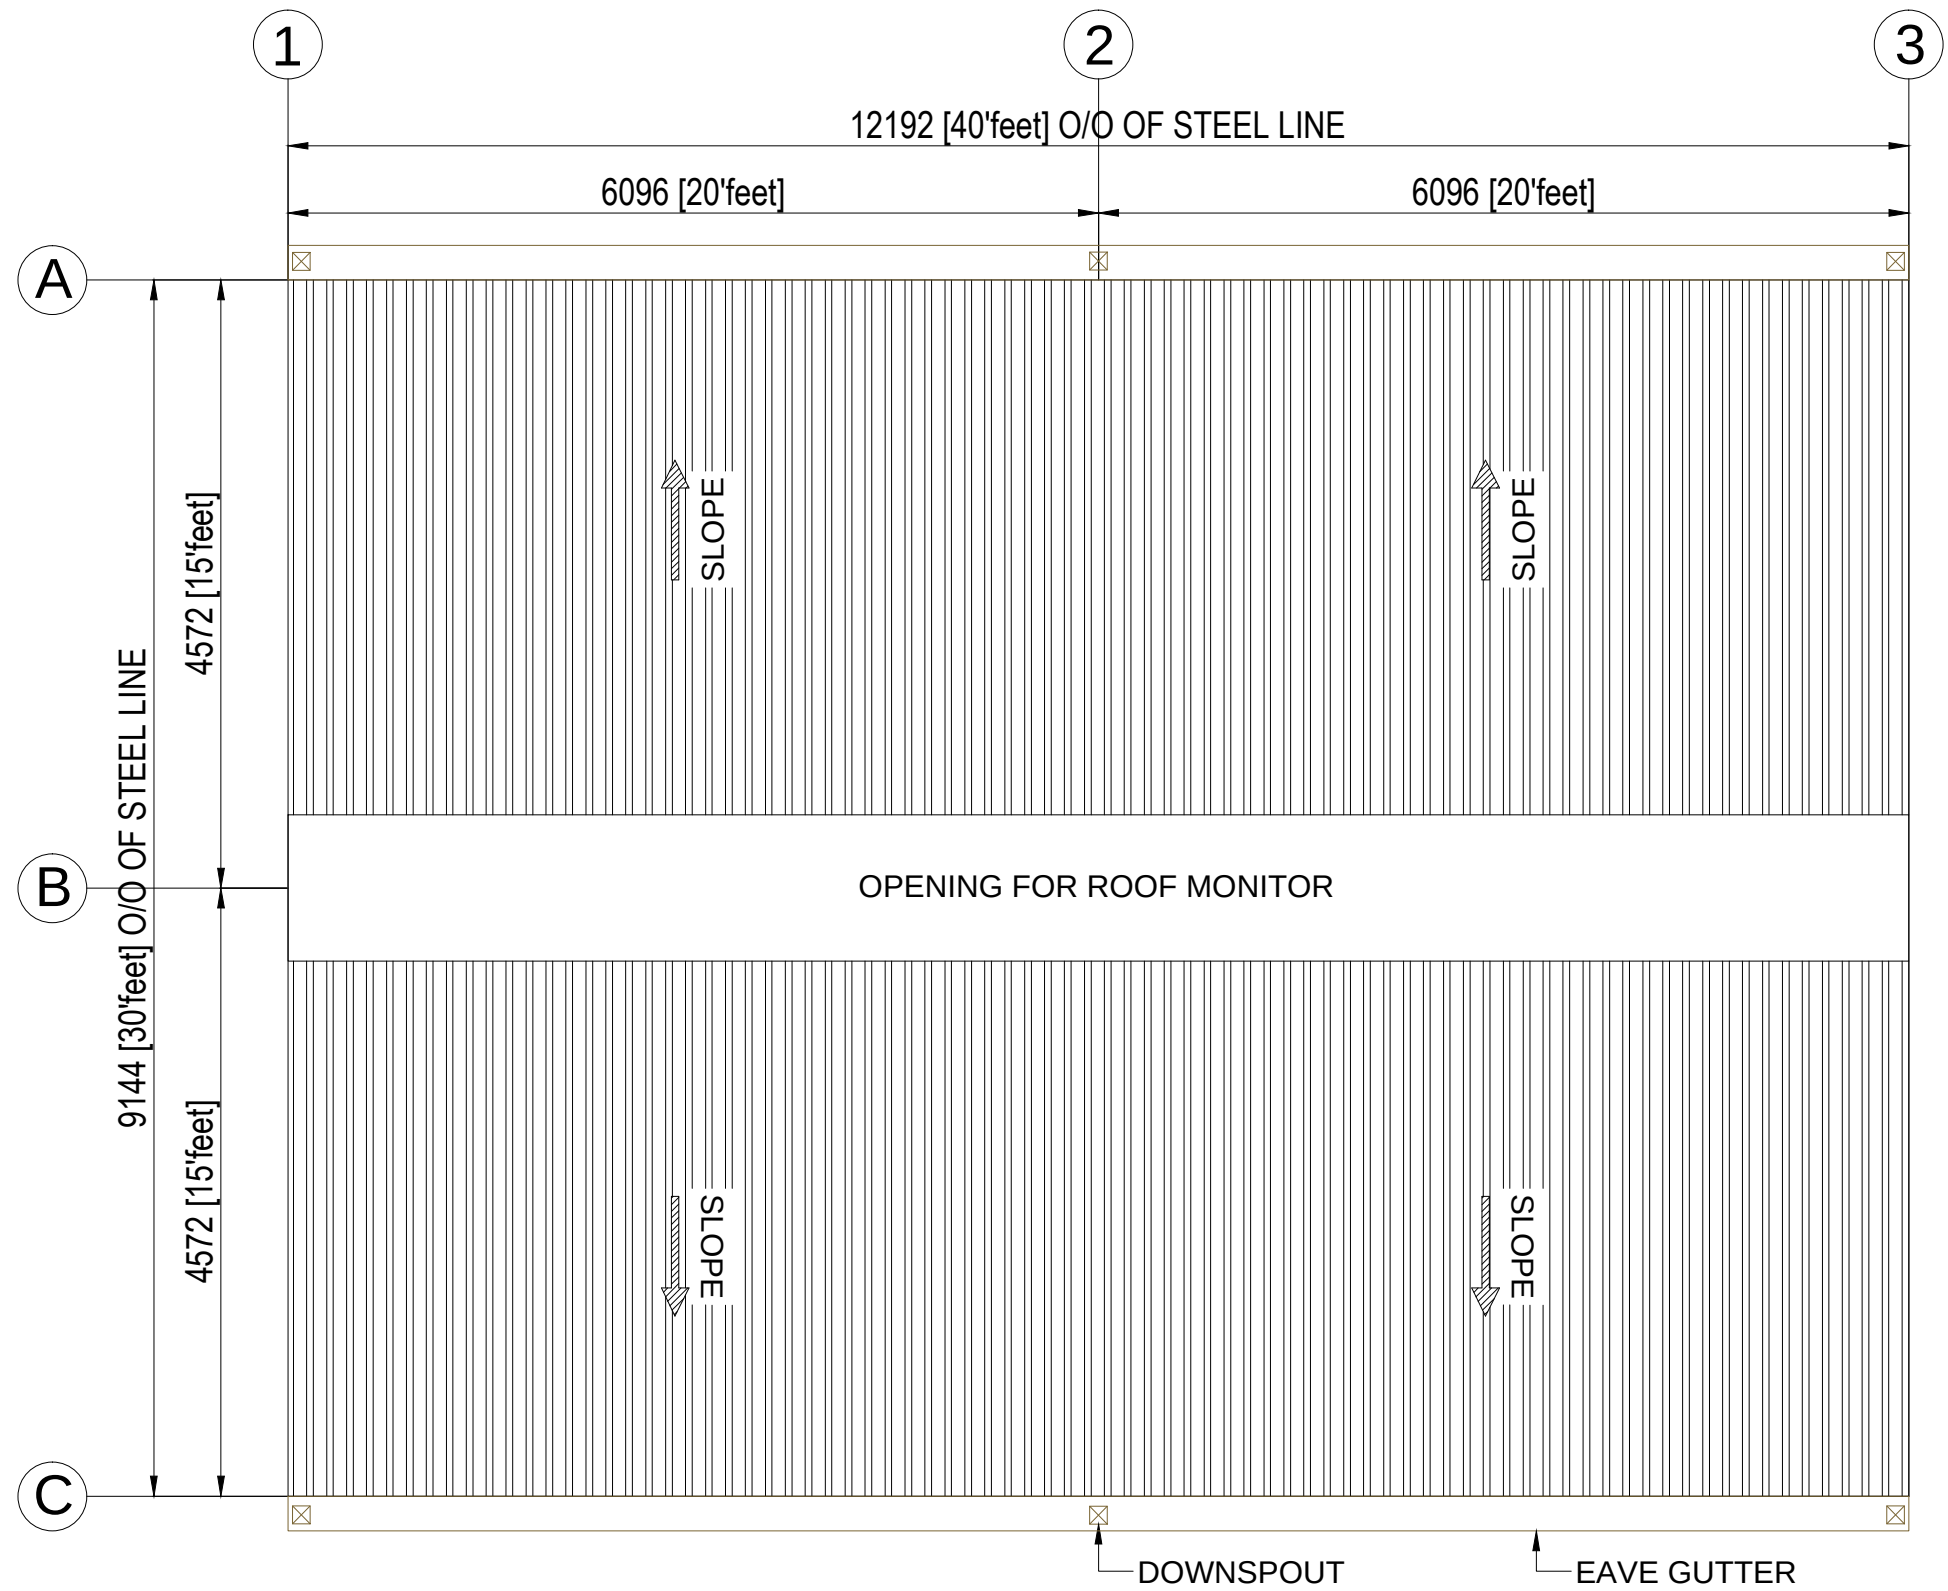

ROOF SHEETING PLAN

GENERAL NOTES		BUILDING ACCESSORIES		BUILDING DESIGN LOADS		BUILDING DESIGN CODES		PROJECT INFORMATION					MAIMAAR  MAIMAAR STEEL Pvt.Ltd 105, Raiwind Road, Thokar Niaz Baig, Lahore, Pakistan E-mail: nasir.abbas@maimaargroup.com E-mail: maimaar.steel@gmail.com Website: www.maimaargroup.com E-mail: nasir.abbas@maimaargroup.com Mob-1 : +(92-300) 807 4017 , +(92-333) 807 1115	
ALL DIMENSIONS ARE IN 'MM & FEET'. THIS IS PROPOSAL DRAWING ONLY, NOT FOR CONSTRUCTION. THIS DRAWING IS NOT TO SCALE.		01. 0.5mm PPGI 02. SINGLE SLIDING DOOR (3048 x 3048mm)		LIVE LOAD = 0.57 KN/SQ.M. WIND SPEED = 135 KM/HR. COLLATERAL LOAD =0.00 EXPOSURE = B		DESIGN CODES AS PER AISC LOADS APPLICATION AS PER MBMA COLD FORMED DESIGN CODES AS PER AISI		QUOTE NO. MSPL-022-20BLDG. NO. : 01 BLDG. NAMEBOILER SHED						