


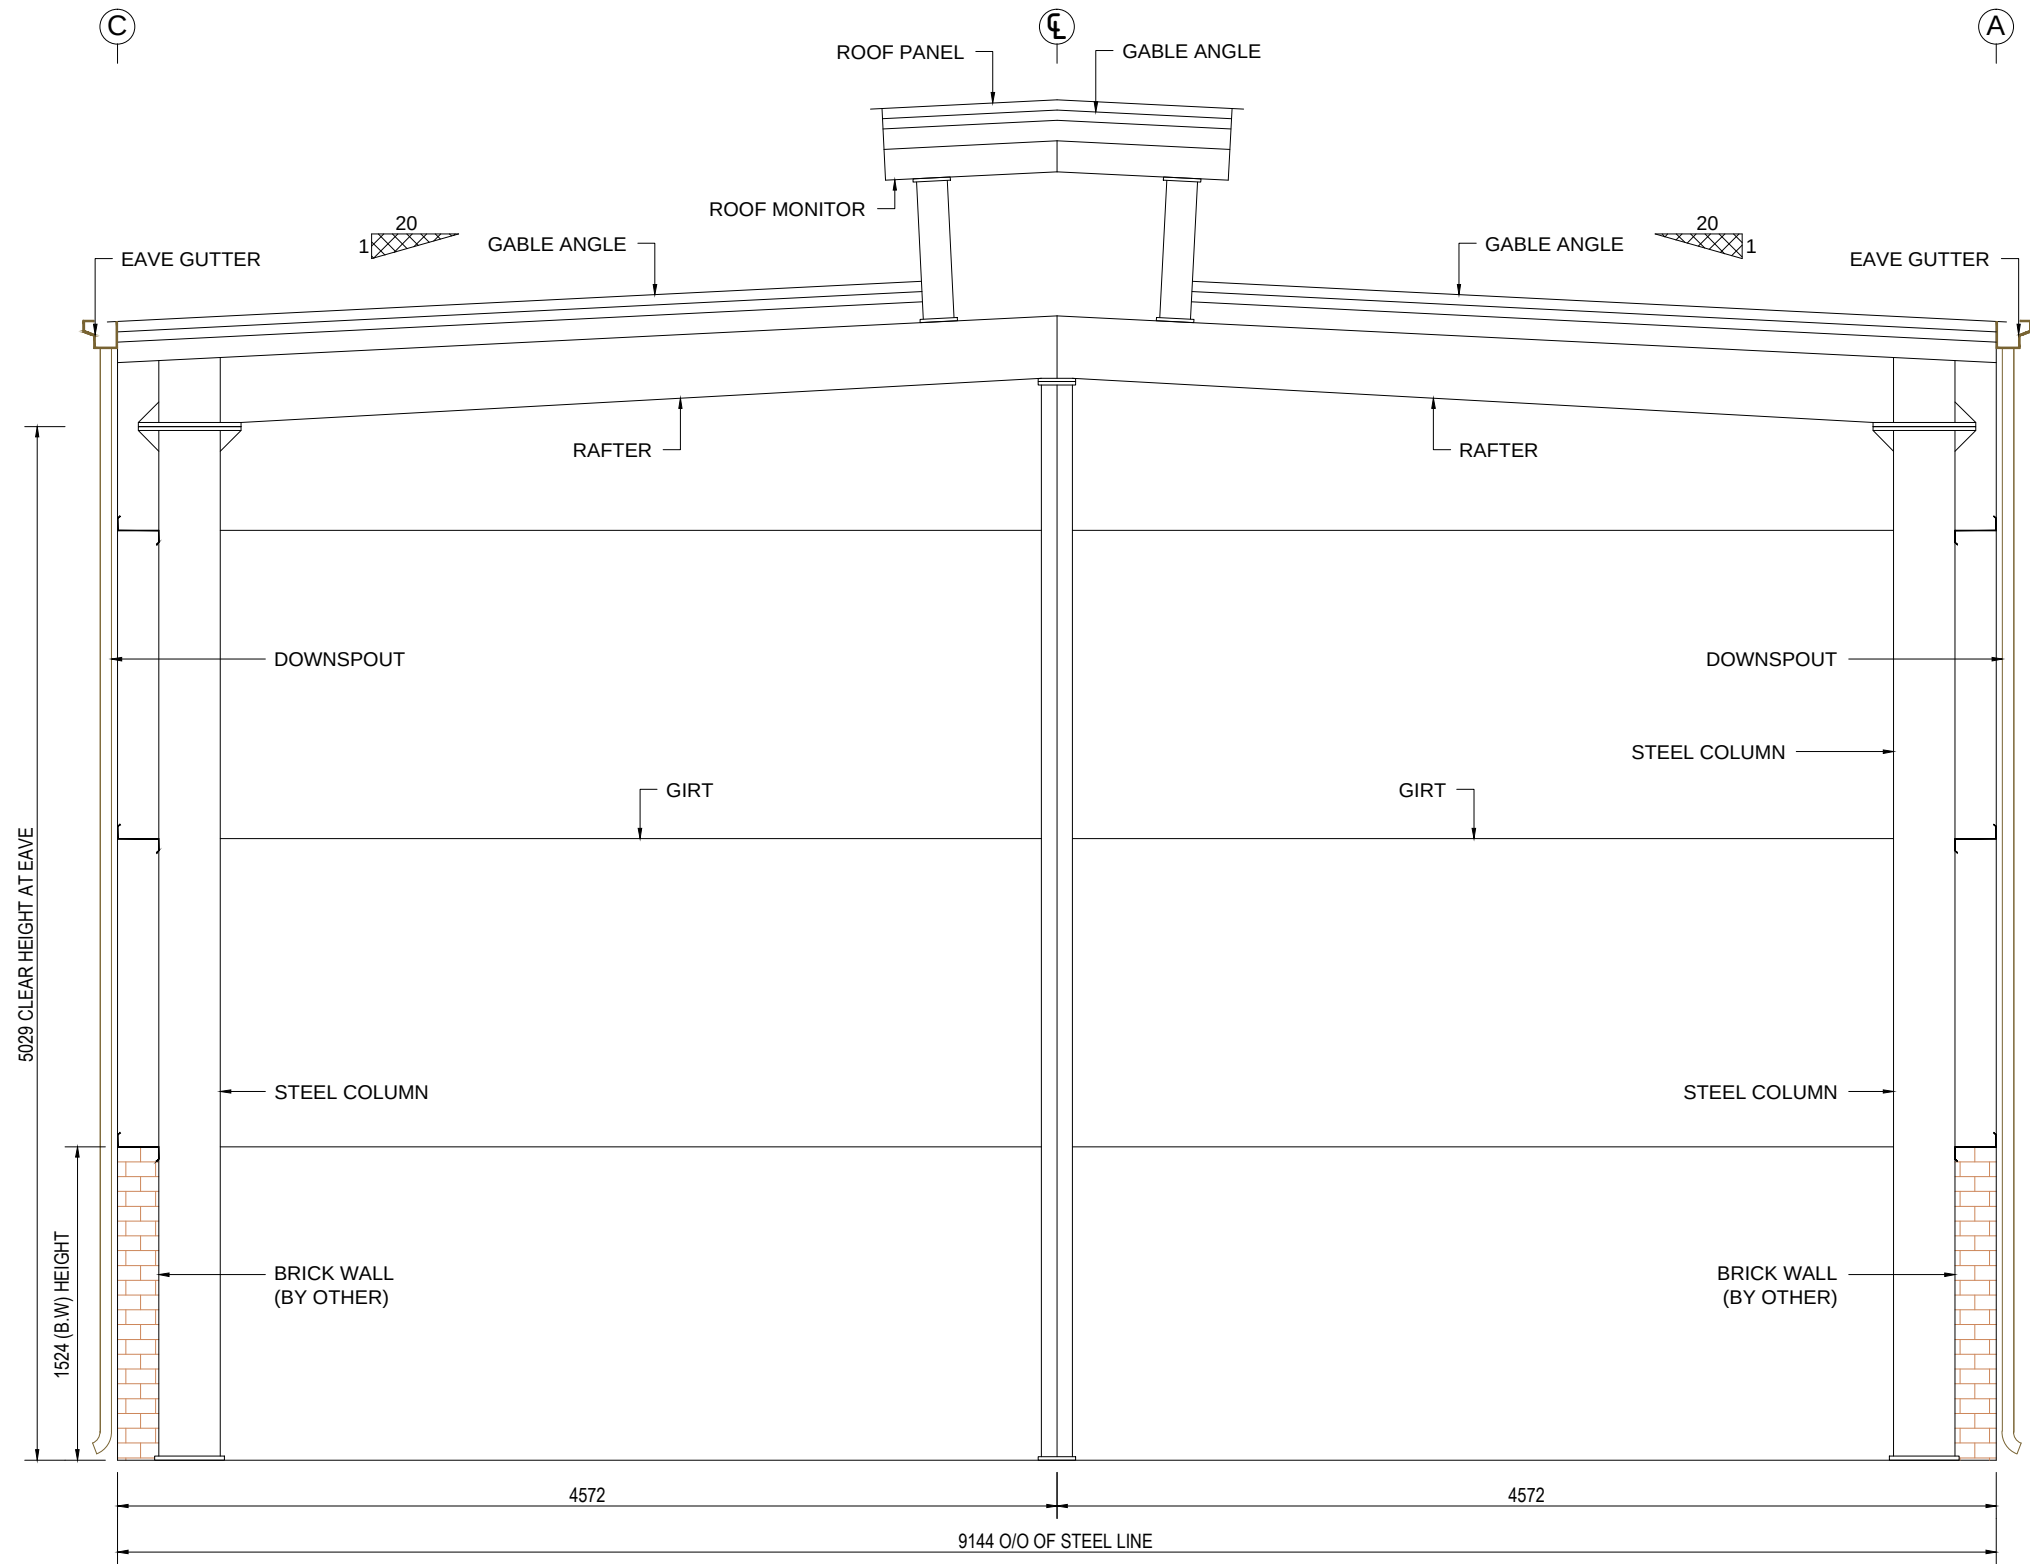

END WALL FRAMING @ GRID-3

GENERAL NOTES

ALL DIMENSIONS ARE IN 'MM & FEET'.
THIS IS PROPOSAL DRAWING ONLY,
NOT FOR CONSTRUCTION.
THIS DRAWING IS NOT TO SCALE.

BUILDING ACCESSORIES

- 01. 0.5mm PPGI
- 02. SINGLE SLIDING DOOR
(3048 x 3048mm)

BUILDING DESIGN LOADS

LIVE LOAD = 0.57 KN/SQ.M.
WIND SPEED = 135 KM/HR.
COLLATERAL LOAD = 0.00
EXPOSURE = B

BUILDING DESIGN CODES

DESIGN CODES AS PER AISC
LOADS APPLICATION AS PER MBMA
COLD FORMED DESIGN CODES AS PER AISI

PROJECT INFORMATION

QUOTE NO.	MSPL-022-20			BLDG. NO.	: 01
BLDG. NAME	BOILER SHED				
REV. NO.	DRN. BY	CHK. BY	DATE	SHEET NO.	
00	NBL	UBD	05-03-2020	PRO-10	
--	--	--	--	--	



MAIMAAR STEEL Pvt.Ltd
105, Raiwind Road, Thokar Niaz Balg, Lahore, Pakistan
E-mail: nasir.abbas@maimaargroup.com
E-mail: maimaar.steel@gmail.com
Website: www.maimaargroup.com
E-mail: nasir.abbas@maimaargroup.com
Mob-1 : +(92-300) 807 4017 , +(92-333) 807 1115