


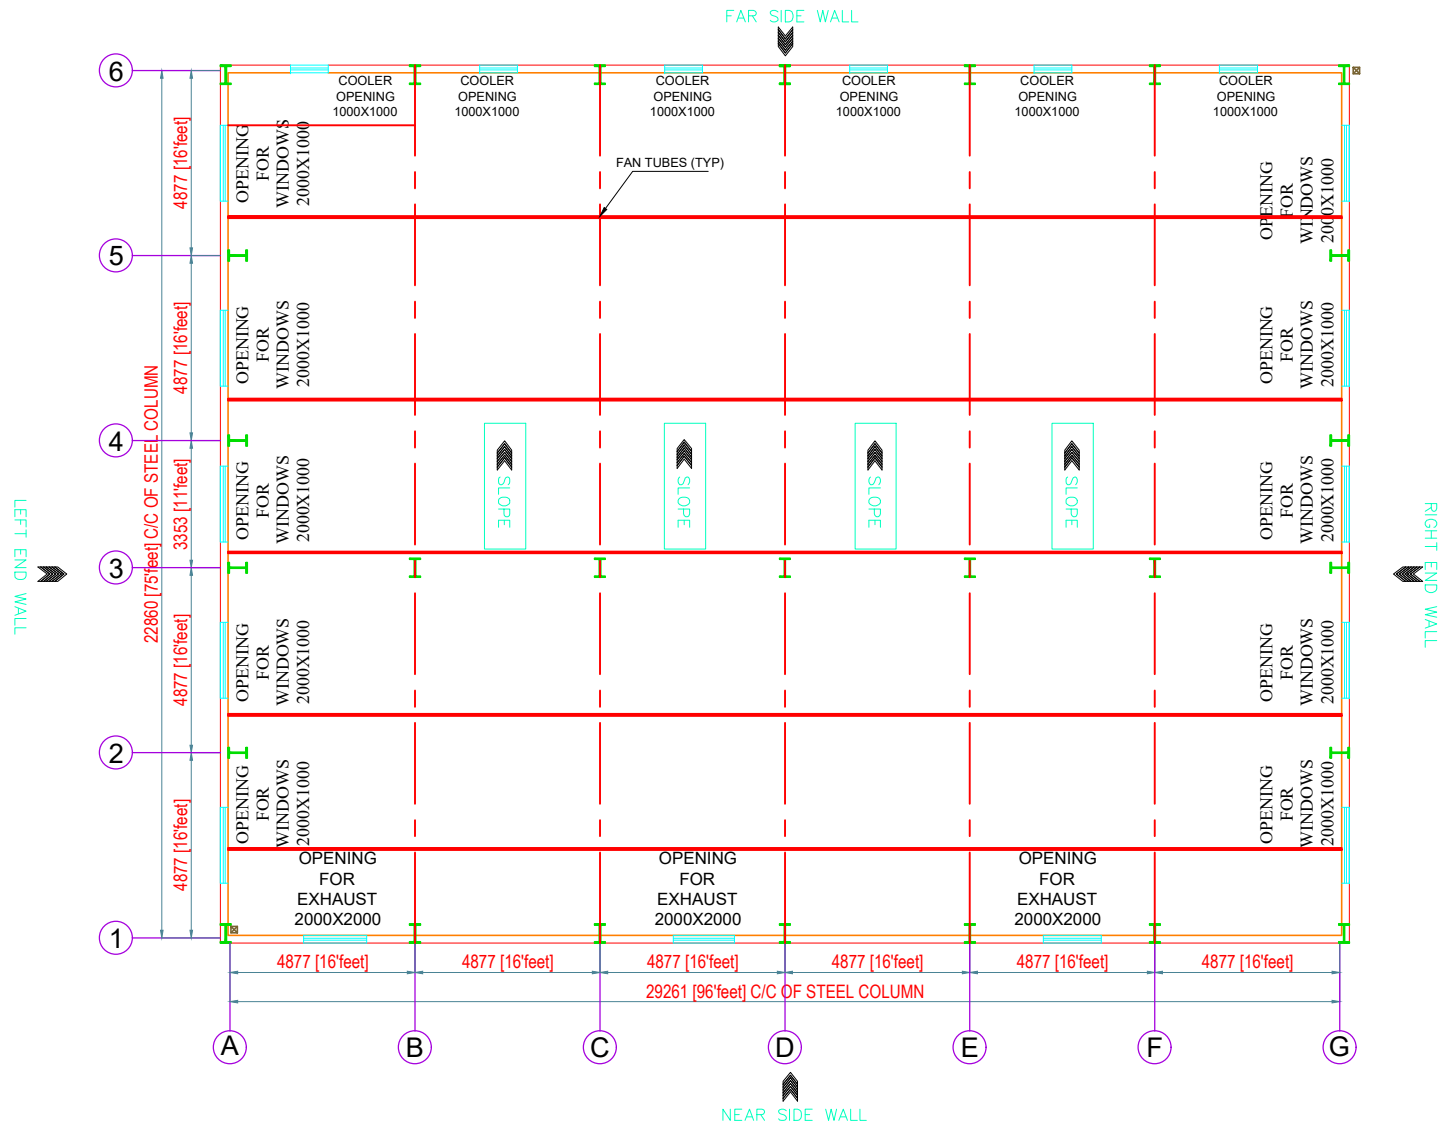

COLUMN LAYOUT PLAN

GENERAL NOTES

ALL DIMENSIONS ARE IN 'MM'.
THIS IS PROPOSAL DRAWING ONLY,
NOT FOR CONSTRUCTION.
THIS DRAWING IS NOT TO SCALE.

BUILDING ACCESSORIES

04 No. ROOF SKY LIGHT (EACH 3250mm)
00 No. GRV (THROAT SIZE=300mm, L=3000mm)
01 No. DOUBLE SLIDING DOOR (4270X4270)
00 No. EMERGENCY DOOR (1220 x 3048)

BUILDING DESIGN LOADS

LIVE LOAD FOR BUILDINGS = 0.57 KN/SQ.M.
LIVE LOAD FOR MEZZANINE = 8.2KN/m²
WIND SPEED = 135 KM/HR.

PROJECT INFORMATION

QUOTE NO.	: MSPL-020-096	REV. NO.	: 00
BLDG. NAME	: N.A ASSOCIATES	BLDG. NO.	: 01
CUSTOMER	: ---		
PROJECT NAME	: N.A ASSOCIATES		
DRN. BY	DATE	CHK. BY	DATE
DA	13-02-2021	YEA	13-02-2021
		SHEET NO.	1 OF 7

PROPOSAL DRAWINGS BY:



MAIMAAR STEEL Pvt.Ltd
105, Raiwind Road, Thokar Niaz Baig, Lahore, Pakistan
E-mail: nasir.abbas@maimaargroup.com
E-mail: maimaar.steel@gmail.com
Website: www.maimaargroup.com
E-mail: nasir.abbas@maimaargroup.com
Mob-1 : +(92-300) 807 4017 , +(92-333) 807 1115