




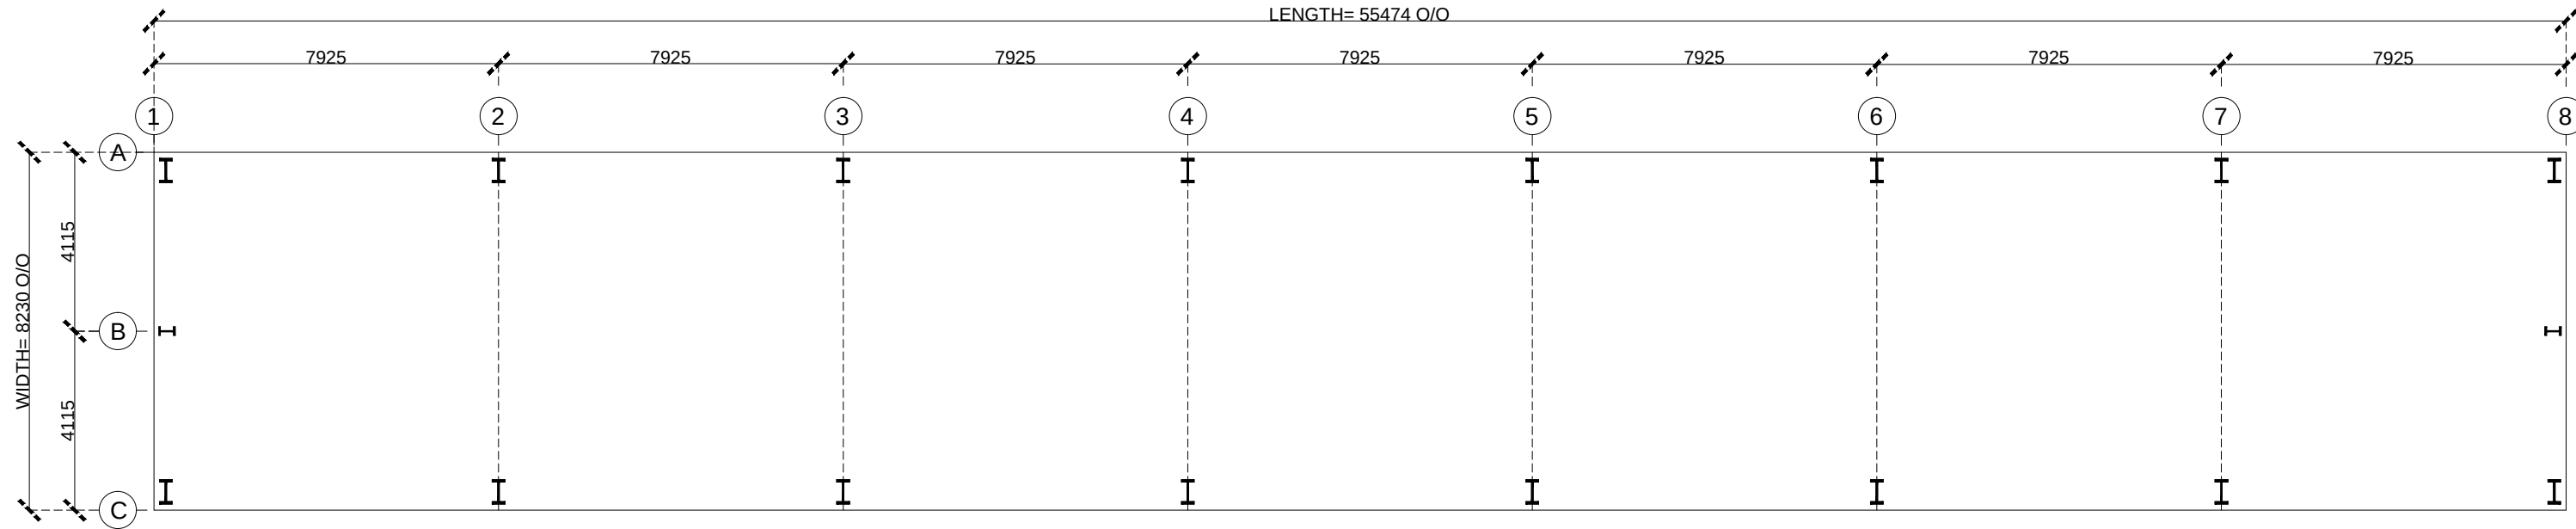


Column Layout

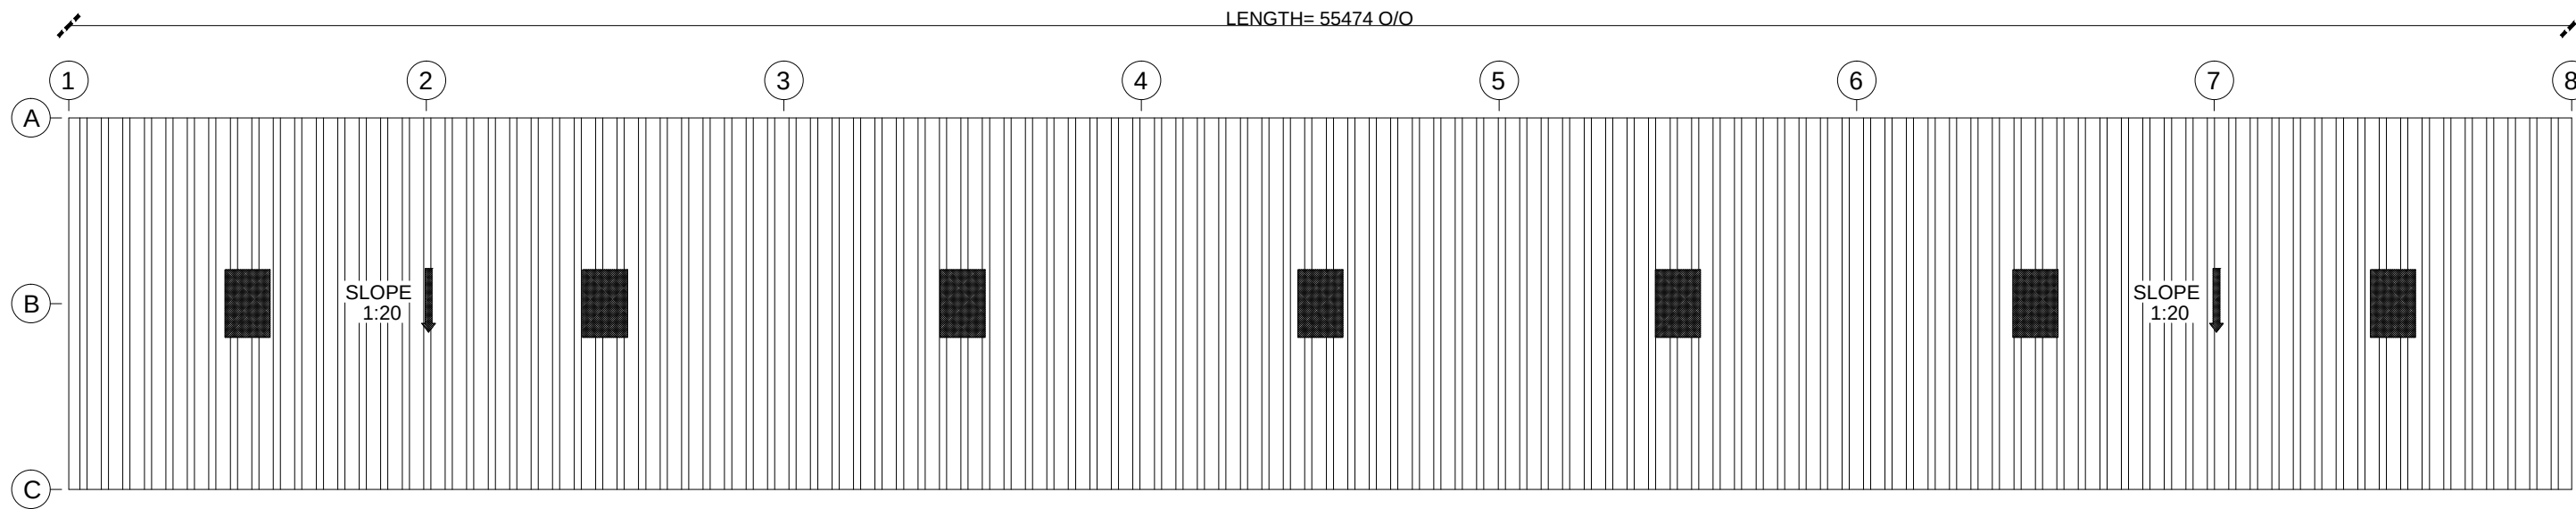


Roof Plan

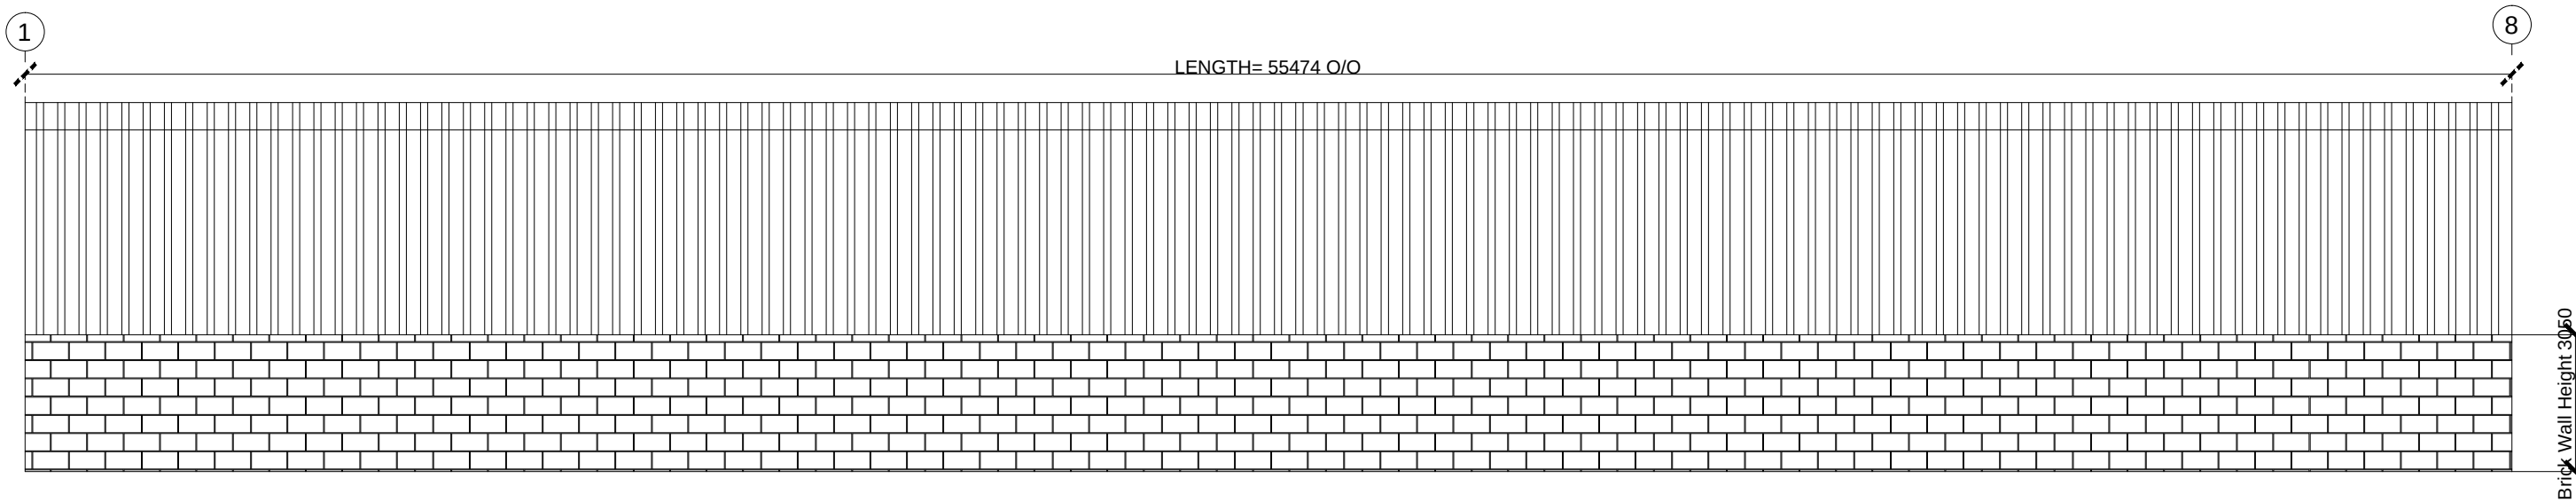

Side Wall Elevation

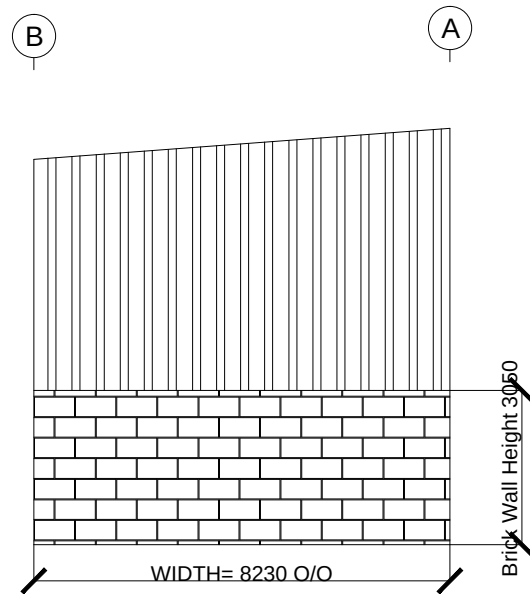

Roof Plan

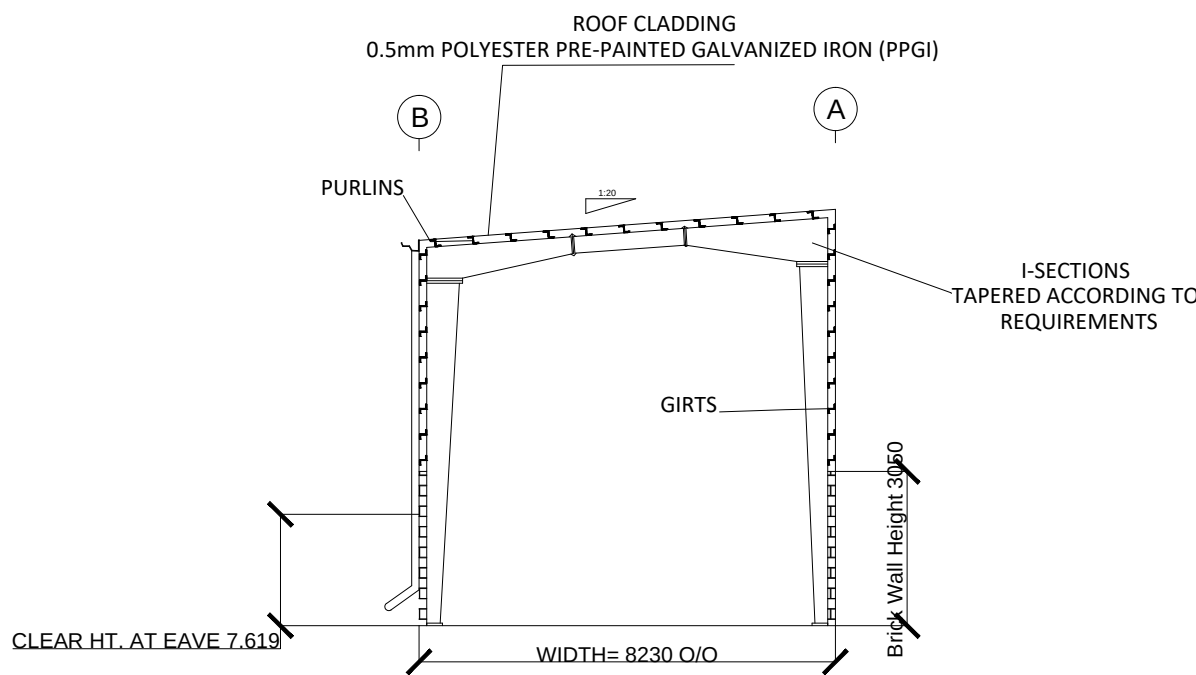

Roof Plan

GENERAL NOTES

ALL DIMENSIONS ARE IN 'MM & FEET'.
THIS IS PROPOSAL DRAWING ONLY,
NOT FOR CONSTRUCTION.
THIS DRAWING IS NOT TO SCALE.

BUILDING ACCESSORIES

7 No. ROOF SKY LIGHT (EACH 1500mm)
0 No. RIDGE VENTILATORS (3000mm)
00 No. F/O FOR WINDOWS (1828x2438)mm
00 No. DOUBLE SLIDING DOOR (3000x3000)

BUILDING DESIGN LOADS

LIVE LOAD = 0.57 KN/SQ.M.
WIND SPEED = 135 KM/HR.
COLLATERAL LOAD = 0.00 KN/SQ.M.
EXPOSURE = B

BUILDING DESIGN CODES

DESIGN CODES AS PER AISC
LOADS APPLICATION AS PER MBMA
COLD FORMED DESIGN CODES AS PER AISI

PROJECT INFORMATION

QUOTE NO.		MSPL-009-19		REV. NO.		: 01			
BLDG. NAME		: WAREHOUSE BUILDING			BLDG. NO.		: 01		
PROJECT NAME								: WAREHOUSE BUILDNG FOR Mr. Israr	
DRN. BY		DATE		CHK. BY		DATE		SHEET NO.	
Yeahyea Gilani		02-02-2019						1 OF 1	

STEEL CONTRACTOR :



105, Basement Floor, Lalazar Commercial
Area ,Raivind Road, Thokar Niaz Baig
Lahore, Pakistan
Website: www.maimaargroup.com
E-mail: nasir.abbas@maimaargroup.com
E-mail: maimaar.steel@gmail.com
Mob-1 : +(92-300) 807 4017
Mob-2 : +(92-333) 807 1115