


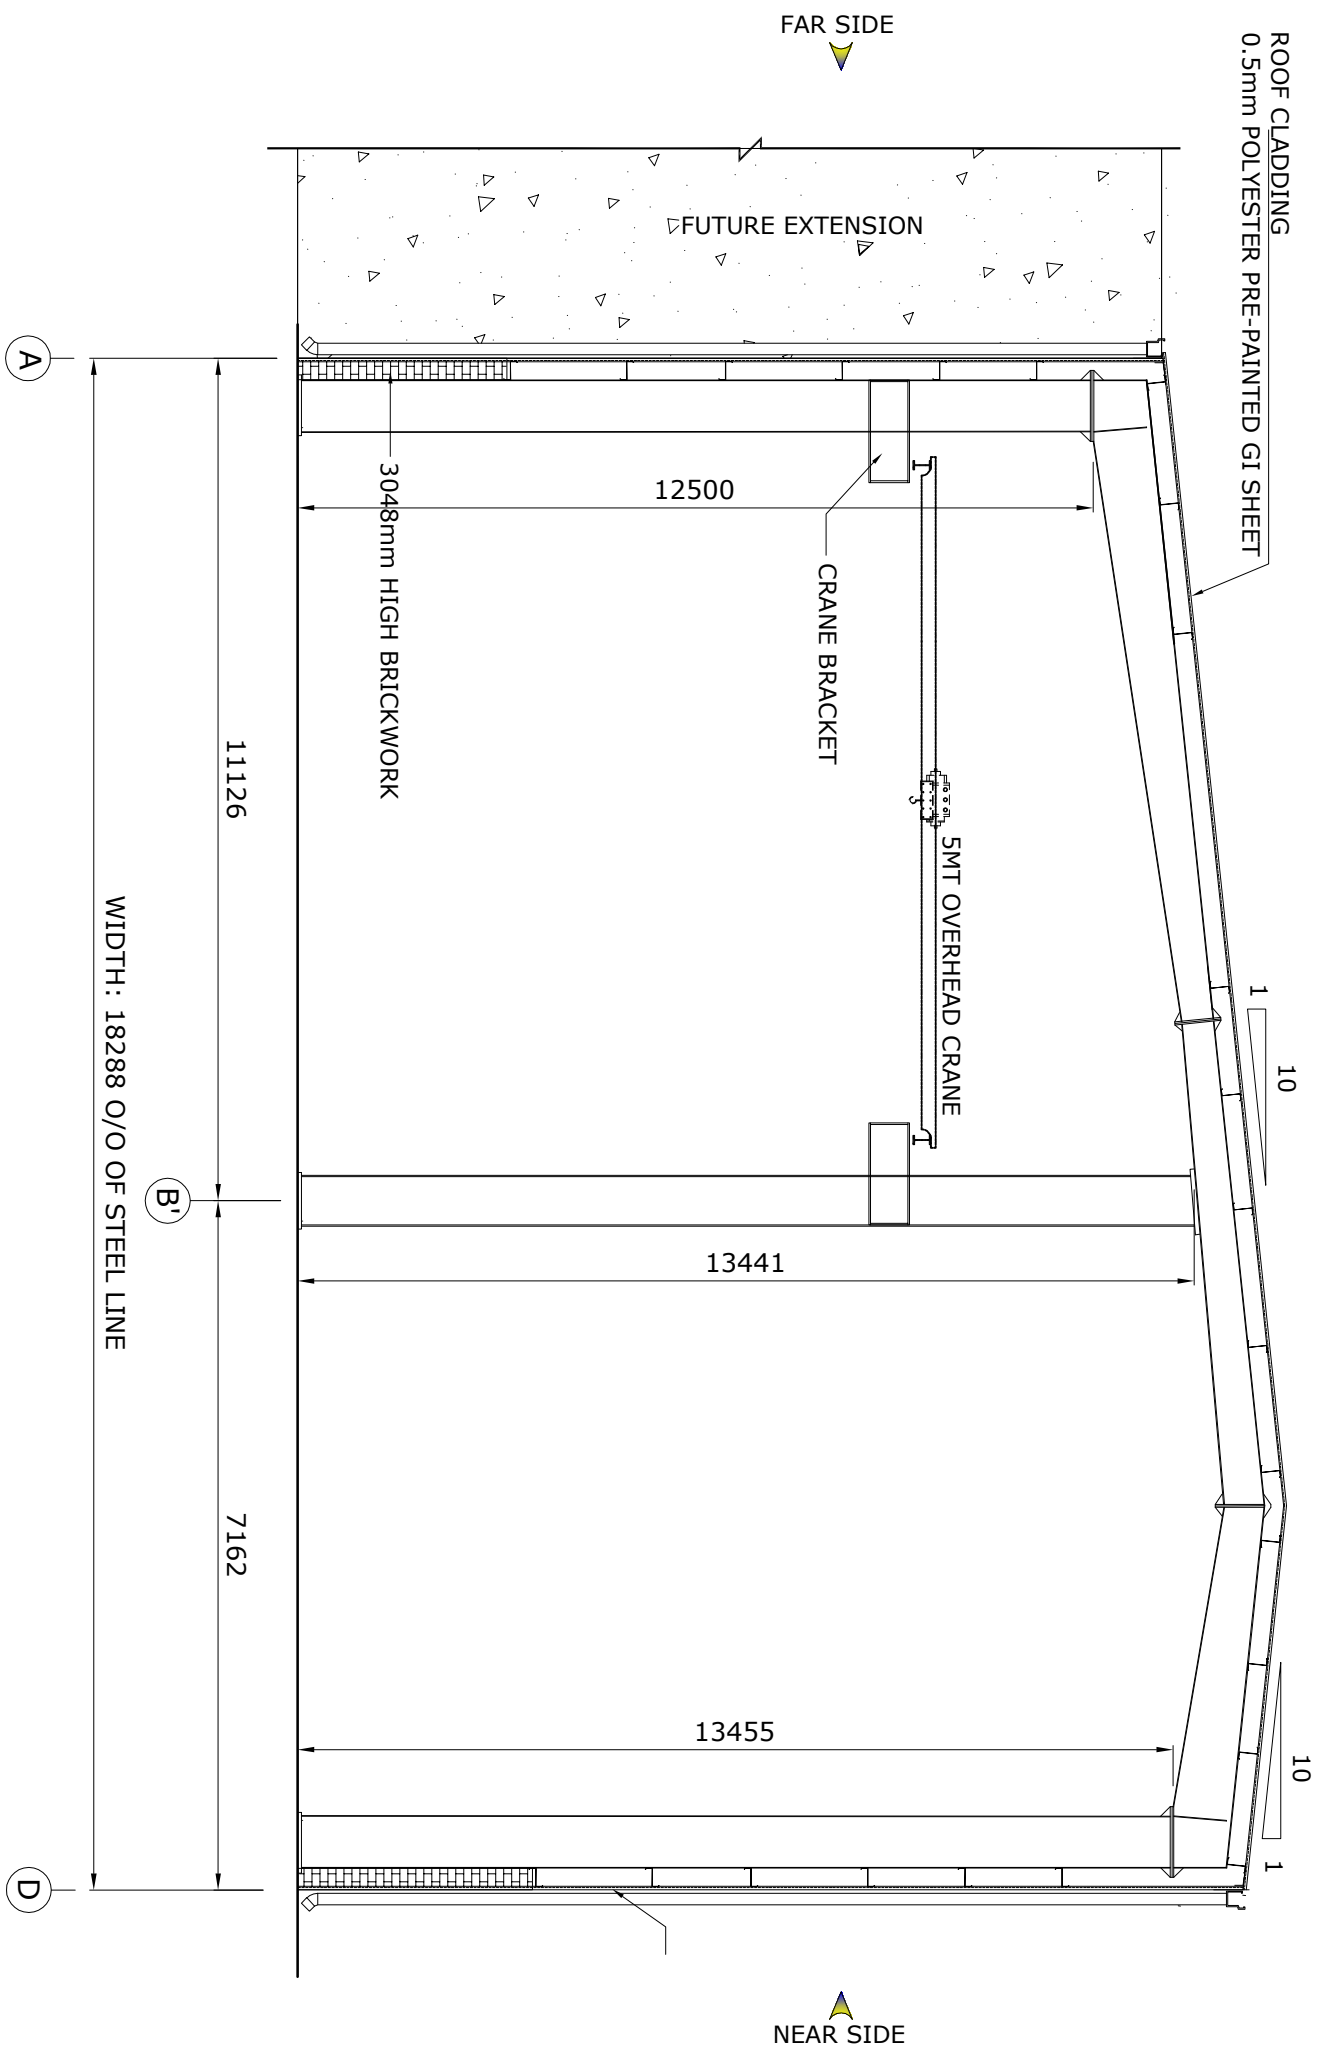

WALL CLADDING
0.5mm ALUMINUM PRE-PAINTED SHEET
50mm THICK GLASSWOOL INSULATION

CROSS SECTION ALONG GL- 09 TO 12

GENERAL NOTES

ALL DIMENSIONS ARE IN "MM".

THIS IS PROPOSAL DRAWING ONLY.

NOT FOR CONSTRUCTION.

THIS DRAWING IS NOT TO SCALE.

BUILDING ACCESSORIES

00 No. ROOF SKY LIGHT (EACH 3250mm)

01 No. ROOF MONITOR

00 No. F/O FOR WINDOWS (1828x2438)mm

03 No. DOUBLE SLIDING DOOR (5000x5000)

BUILDING DESIGN LOADS

LIVE LOAD = 0.57 KN/SQ.M.

WIND SPEED = 135 KM/HR.

COLLATERAL LOAD =0.00 KN/SQ.M.

BUILDING DESIGN CODES

DESIGN CODES AS PER AISC

LOADS APPLICATION AS PER MBMA

COLD FORMED DESIGN CODES AS PER AISI

PROJECT INFORMATION

QUOTE NO.		:	MBS-16-015		REV. NO.	:	00
BLDG. NAME		:	MOLDING & SAND PLANT		BLDG. NO.	:	01
PROJECT NAME : PEB FOR KSB PUMPS							
DRN. BY	DATE	CHK. BY	DATE	SHEET NO.			
	25-06-2016		25-06-2016	4 TO 8			

PROPOSAL DRAWINGS BY

STEEL CONTRACTOR :



MAIMAAR

BUILDING SYSTEMS

220-B, Lahore Gardens

Sharqpur Road, Near Shahdara

Lahore, Pakistan

Website: www.maimaargroup.com

E-mail: nasir.abbas@maimaargroup.com

E-mail: maimair.steel@gmail.com

Mob-1 : +(92-300) 807 4017

Mob-2 : +(92-333) 807 1115