


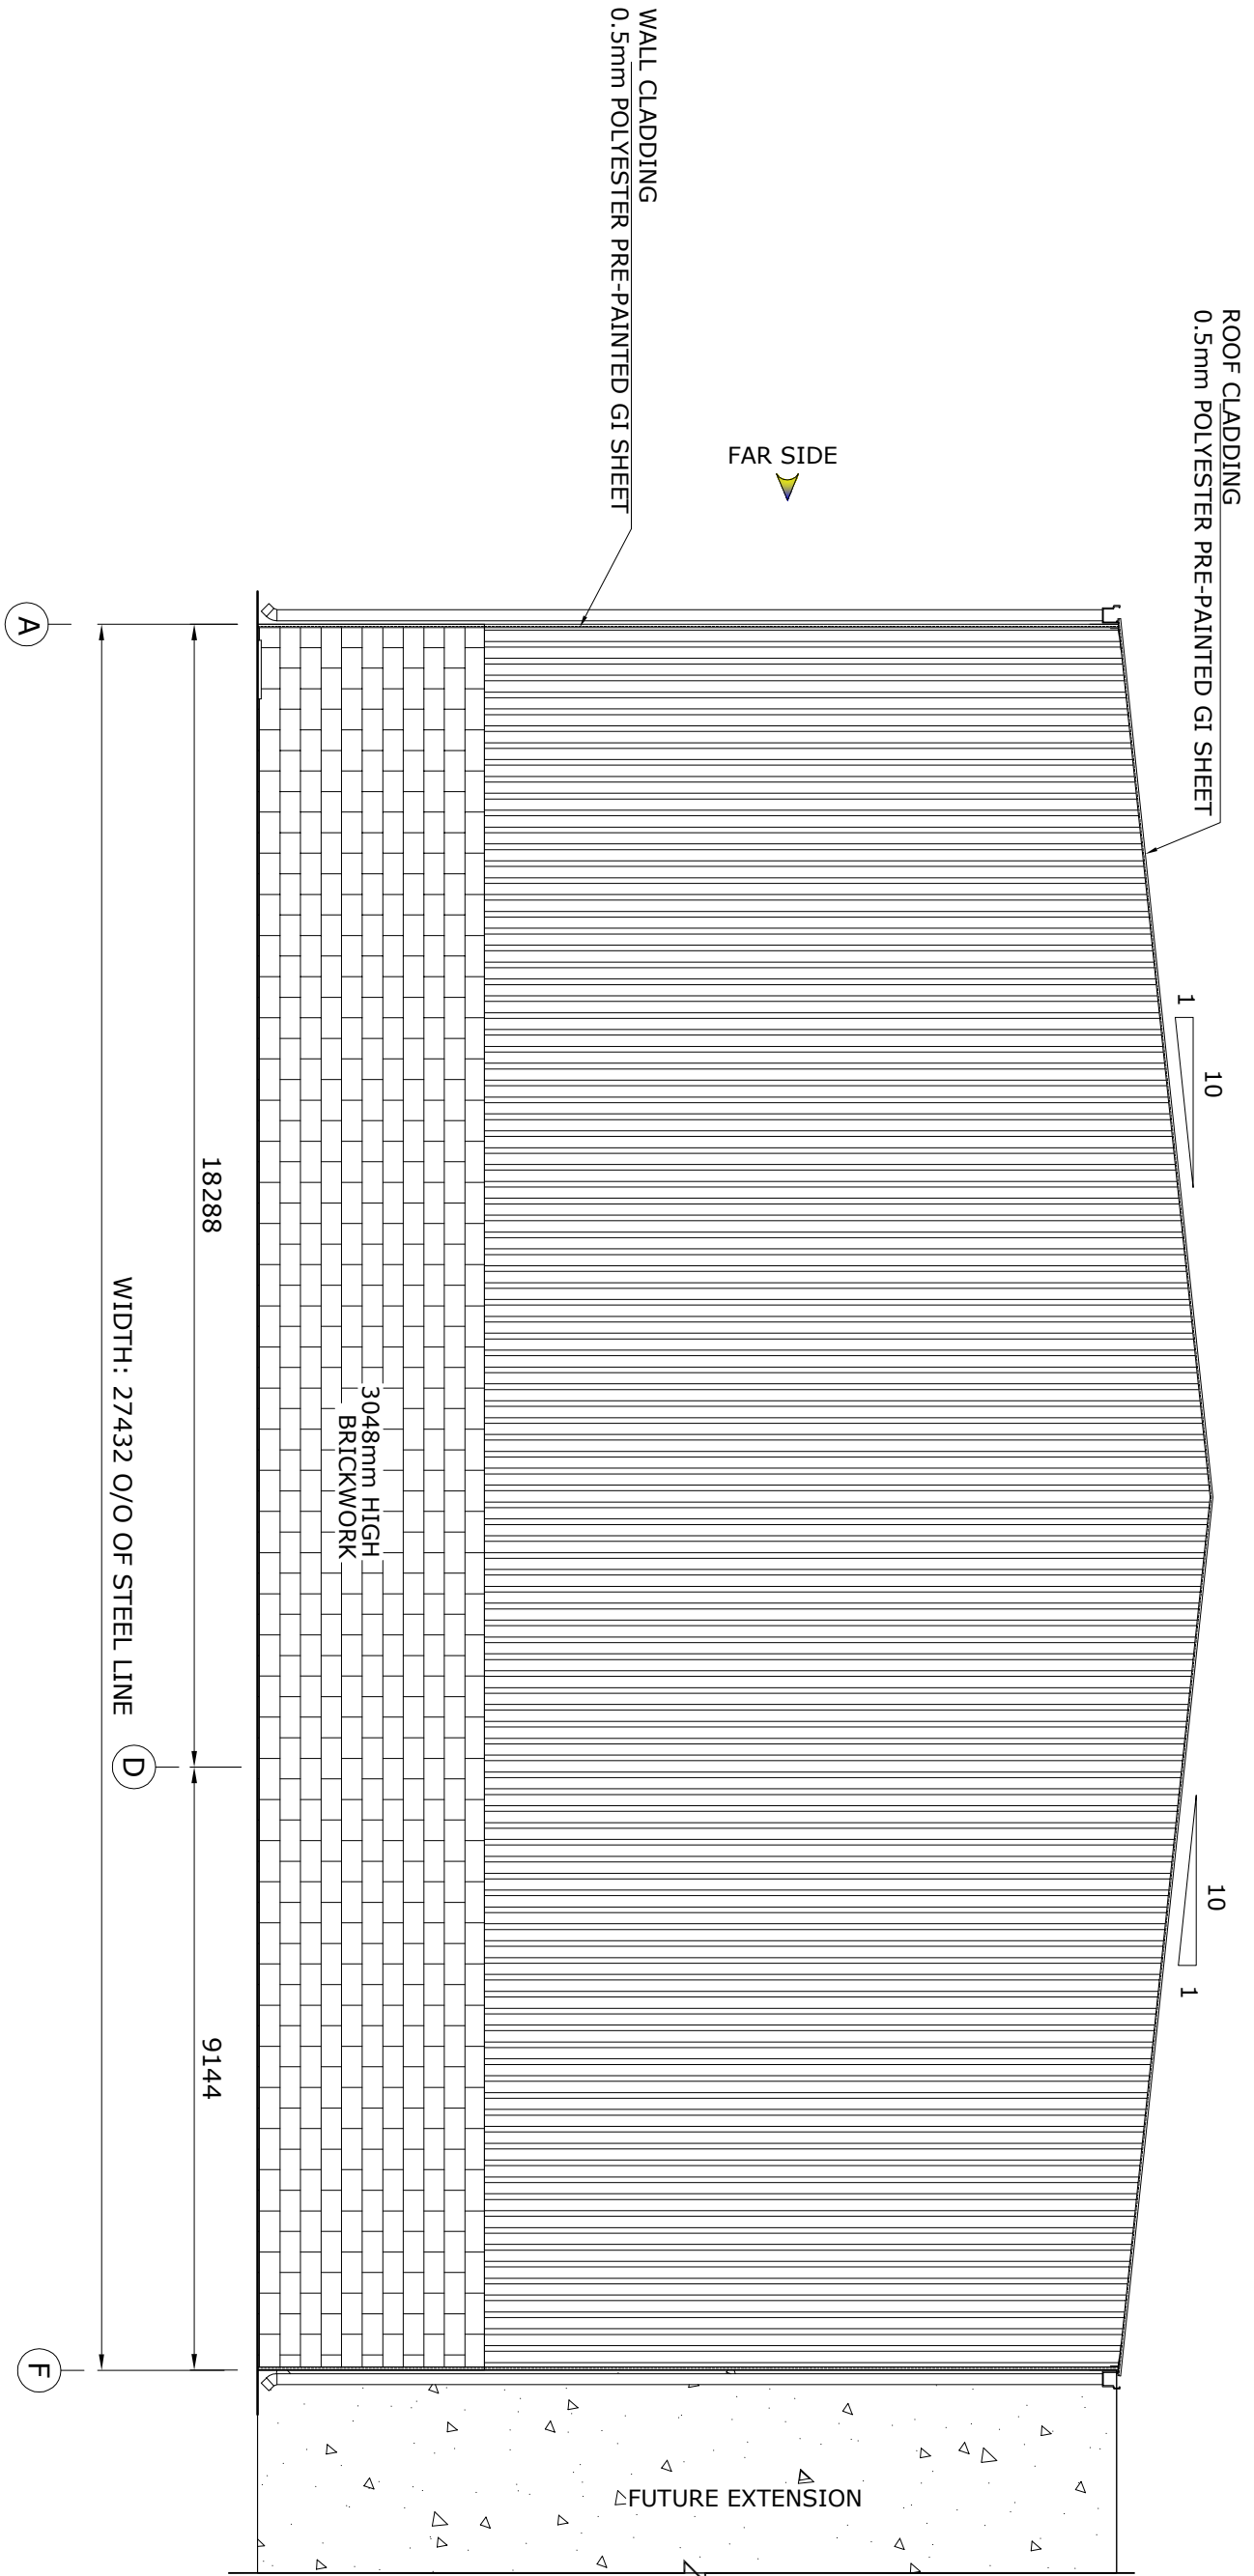

ENDWALL ELEVATION ALONG GL- 01

GENERAL NOTES

ALL DIMENSIONS ARE IN MM.
THIS IS PROPOSAL DRAWING ONLY,
NOT FOR CONSTRUCTION.
THIS DRAWING IS NOT TO SCALE.

BUILDING ACCESSORIES

- 00 No. ROOF SKY LIGHT (EACH 3250mm)
- 01 No. ROOF MONITOR
- 00 No. F/O FOR WINDOWS (1828x2438)mm
- 03 No. DOUBLE SLIDING DOOR (5000x5000)

BUILDING DESIGN LOADS

LIVE LOAD = 0.57 KN/SQ.M.
WIND SPEED = 135 KM/HR.
COLLATERAL LOAD =0.00 KN/SQ.M.

BUILDING DESIGN CODES

DESIGN CODES AS PER AISC
LOADS APPLICATION AS PER MBMA
COLD FORMED DESIGN CODES AS PER AISI

PROJECT INFORMATION

QUOTE NO.	: MBS-16-015	REV. NO.	: 00
BLDG. NAME	: MOLDING & SAND PLANT	BLDG. NO.	: 01
PROJECT NAME	: PEB FOR KSB PUMPS		
DRN. BY	DATE	CHK. BY	DATE
	25-06-2016		25-06-2016
		SHEET NO.	5 TO 8

PROPOSAL DRAWINGS BY
STEEL CONTRACTOR :



220-B, Lahore Gardens
Sharaqpur Road, Near Shandara
Lahore, Pakistan
Website: www.maimaargroup.com
E-mail: nasir.abbas@maimaargroup.com
E-mail: maimaar.steel@gmail.com
Mob-1 : +(92-300) 807 4017
Mob-2 : +(92-333) 807 1115