


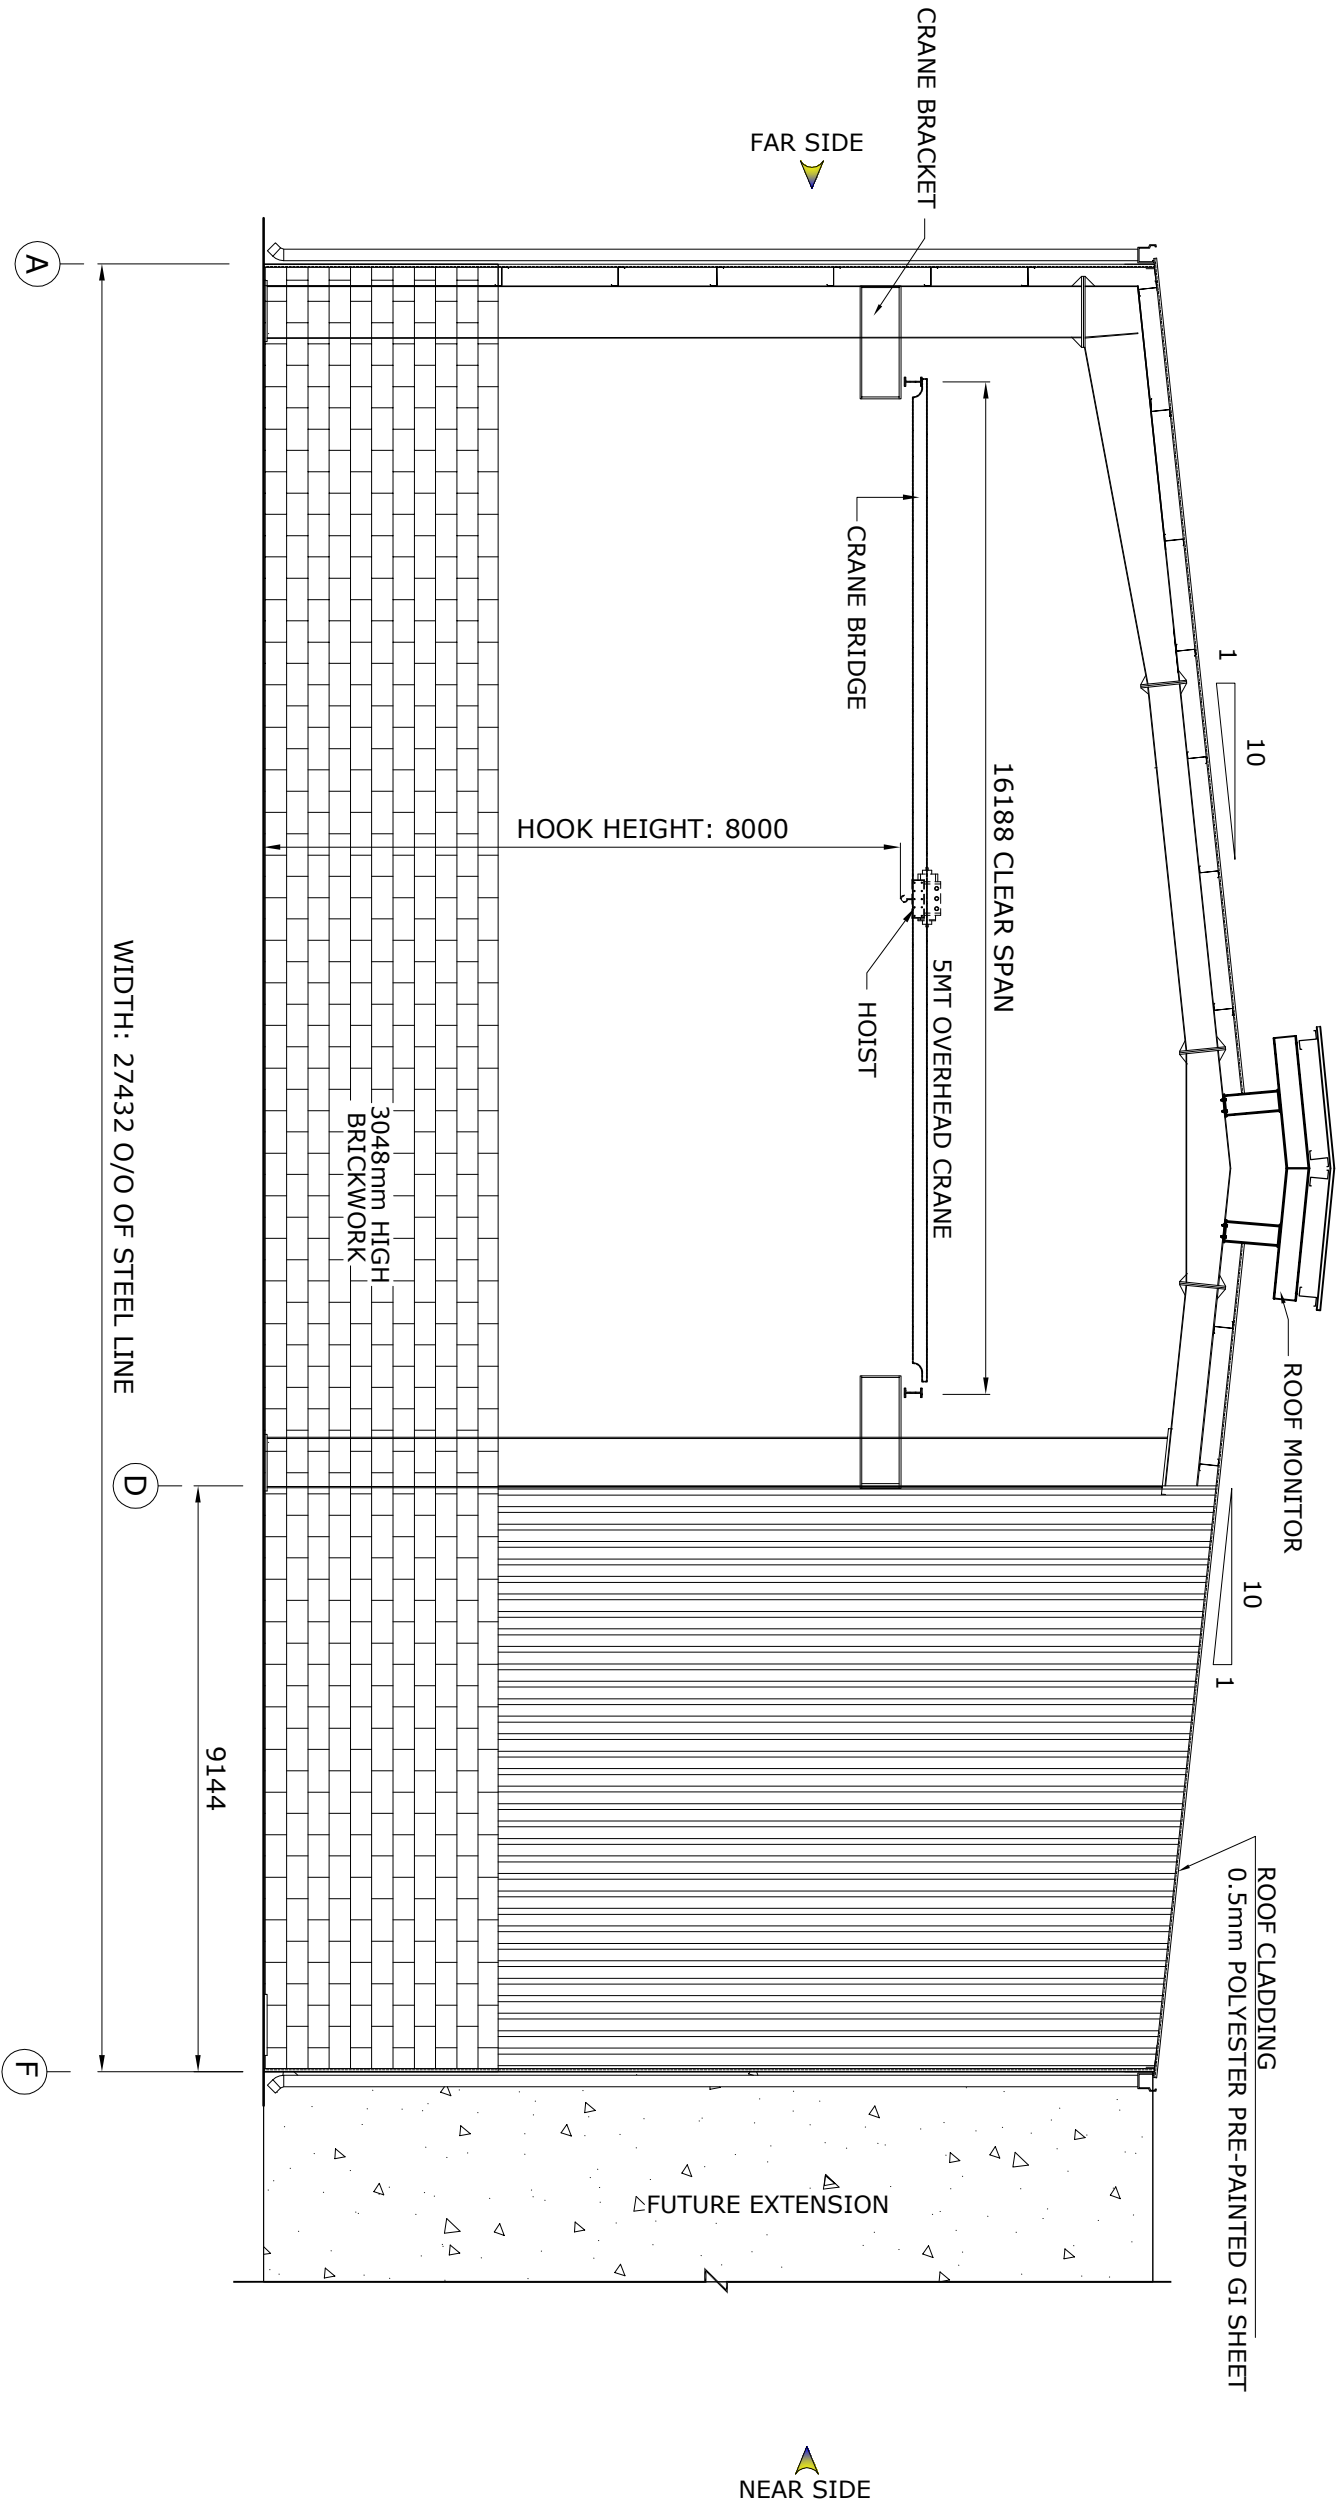

CROSS SECTION ALONG GL- 08

GENERAL NOTES

ALL DIMENSIONS ARE IN MM.
THIS IS PROPOSAL DRAWING ONLY,
NOT FOR CONSTRUCTION.
THIS DRAWING IS NOT TO SCALE.

BUILDING ACCESSORIES

00 No. ROOF SKY LIGHT (EACH 3250mm)
01 No. ROOF MONITOR
00 No. F/O FOR WINDOWS (1828x2438)mm
03 No. DOUBLE SLIDING DOOR (5000x5000)

BUILDING DESIGN LOADS

LIVE LOAD = 0.57 KN/SQ.M.
WIND SPEED = 135 KM/HR.
COLLATERAL LOAD =0.00 KN/SQ.M.

BUILDING DESIGN CODES

DESIGN CODES AS PER AISC
LOADS APPLICATION AS PER MBMA
COLD FORMED DESIGN CODES AS PER AISI

PROJECT INFORMATION

QUOTE NO.	: MBS-16-015	REV. NO.	: 00
BLDG. NAME	: MOLDING & SAND PLANT	BLDG. NO.	: 01
PROJECT NAME	: PEB FOR KSB PUMPS		
DRN. BY	DATE	CHK. BY	DATE
	25-06-2016		25-06-2016
		SHEET NO.	6 TO 8

PROPOSAL DRAWINGS BY:

STEEL CONTRACTOR :



220-B, Lahore Gardens
Sharaqpur Road, Near Shandara
Lahore, Pakistan
Website: www.maimaargroup.com
E-mail: nasir.abbas@maimaargroup.com
E-mail: maimaar_steel@gmail.com
Mob-1 : +(92-300) 807 4017
Mob-2 : +(92-333) 807 1115