


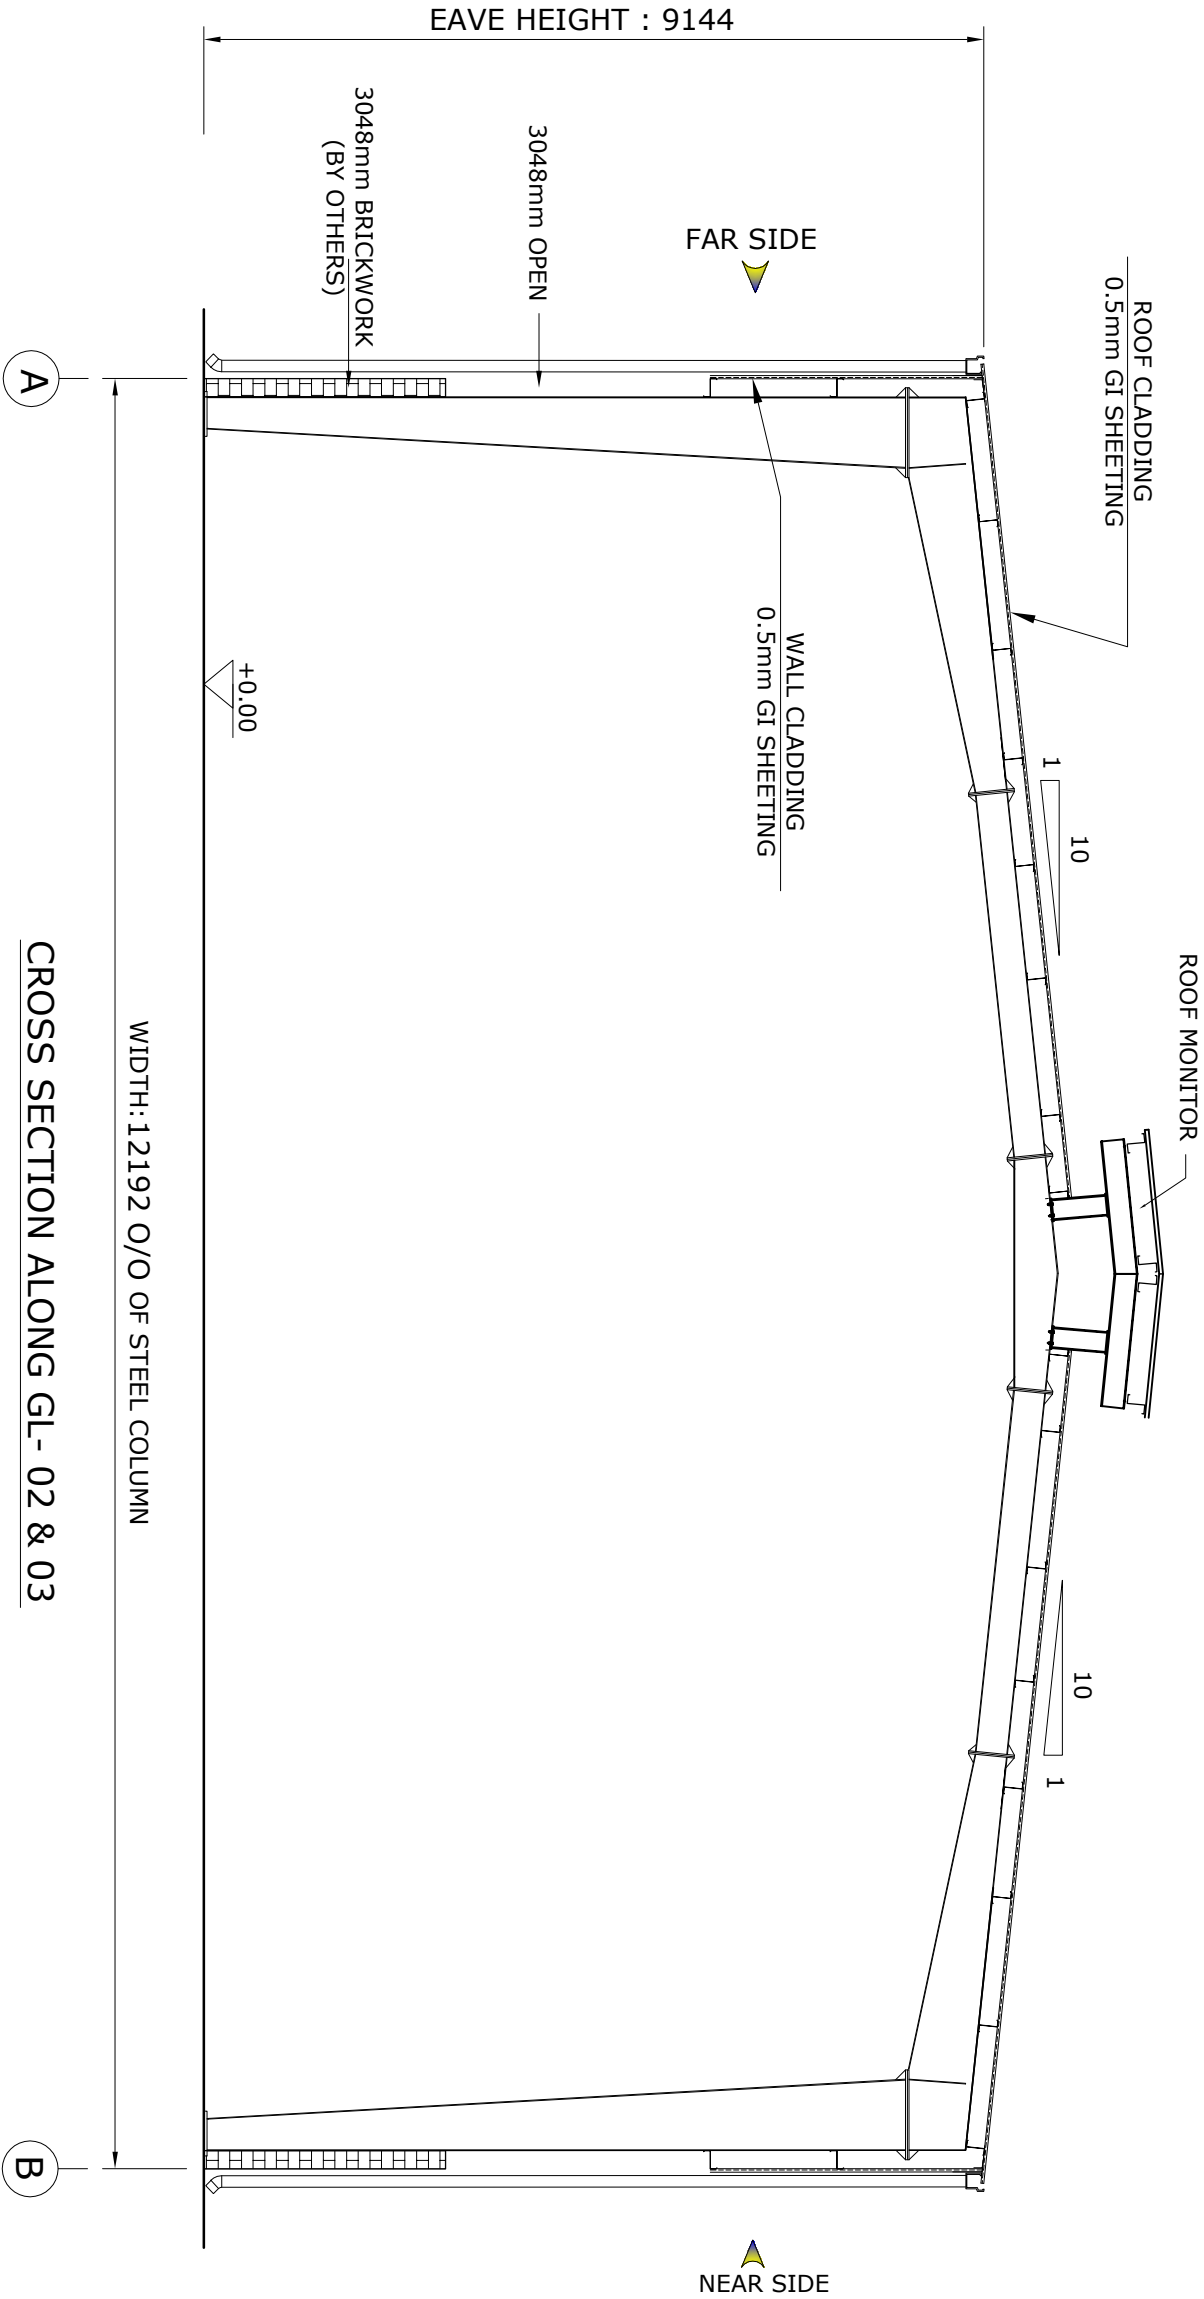

CROSS SECTION

GENERAL NOTES

ALL DIMENSIONS ARE IN MM & FEET.
THIS IS PROPOSAL DRAWING ONLY,
NOT FOR CONSTRUCTION.
THIS DRAWING IS NOT TO SCALE.

BUILDING ACCESSORIES

00 No. ROOF SKY LIGHT (EACH 3250mm)
ROOF MONITOR (THROAT SIZE=700mm)
00 No. F/O FOR WINDOWS (1828x2438)mm
00 No. DOUBLE SLIDING DOOR (3000x3000)

BUILDING DESIGN LOADS

LIVE LOAD = 0.57 KN/SQ.M.
WIND SPEED = 135 KM/HR.
COLLATERAL LOAD =0.00 KN/SQ.M.

BUILDING DESIGN CODES

DESIGN CODES AS PER AISC
LOADS APPLICATION AS PER MBMA
COLD FORMED DESIGN CODES AS PER AISI

PROJECT INFORMATION

QUOTE NO.	: 01	REV. NO.	: 00
BLDG. NAME	:BOILER HOUSE	BLDG. NO.	: 01
PROJECT NAME : BOILER HOUSE			
DRN. BY	DATE	CHK. BY	DATE
	04-05-2016		04-05-2016
			SHEET NO.
			2 TO 5

STEEL CONTRACTOR :



220-B, Lahore Gardens
Sharadpur Road, Near Shandara
Lahore, Pakistan
Website: www.maimaargroup.com
E-mail: nasir.abbas@maimaargroup.com
Mob-1 : +(92-300) 807 4017
Mob-2 : +(92-333) 807 1115