


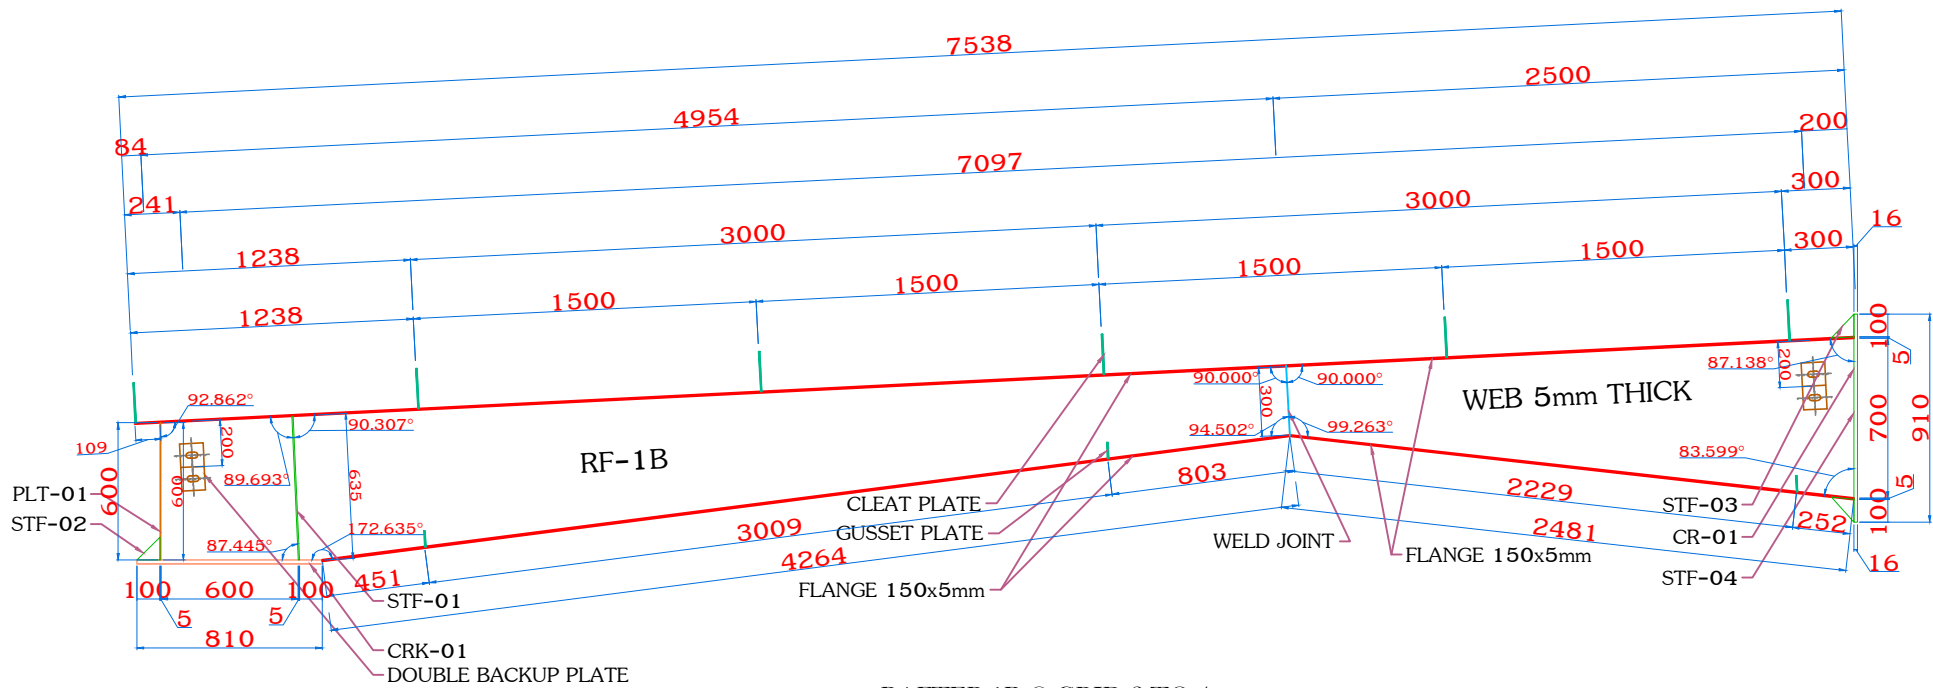

RAFTER-1B @ GRID 2 TO 4
QTY:(03,L)(03,R)

GENERAL NOTES

ALL DIMENSIONS ARE IN 'MM & FEET'.
 THIS IS PROPOSAL DRAWING ONLY,
 NOT FOR CONSTRUCTION.
 THIS DRAWING IS NOT TO SCALE.

BUILDING ACCESSORIES

00 No. ROOF SKY LIGHT (EACH 3250mm)
 00 No. RIDGE VENTILATORS (3000mm)
 00 No. F/O FOR WINDOWS (1828x2438)mm
 00 No. DOUBLE SLIDING DOOR (3000x3000)

BUILDING DESIGN LOADS

LIVE LOAD = 0.57 KN/SQ.M.
 WIND SPEED = 135 KM/HR.
 COLLATERAL LOAD = 0.00 KN/SQ.M.
 EXPOSURE = B

BUILDING DESIGN CODES

DESIGN CODES AS PER AISC
 LOADS APPLICATION AS PER MBMA
 COLD FORMED DESIGN CODES AS PER AISI

PROJECT INFORMATION

QUOTE NO.		MBS-NEW VISION		BLDG. NO. : 01	
BLDG. NAME		STEEL SHED			
REV. NO.	DRN. BY	CHK. BY	DATE	SHEET NO.	
00	FZN	UBD	15-01-2019	FAB-06	
---	---	---	---	---	

STEEL CONTRACTOR

MAIMAAR
 STEEL BUILDING PVT. LTD.

105, Basement Floor, Lalazar Commercial
 Area, Raiwind Road, Thokar Niaz Baig
 Lahore, Pakistan
 Website: www.maimaargroup.com
 E-mail: nasir.abbas@maimaargroup.com
 E-mail: maimaar.steel@gmail.com
 Mob-1 : +(92-300) 807 4017
 Mob-2 : +(92-333) 807 1115