


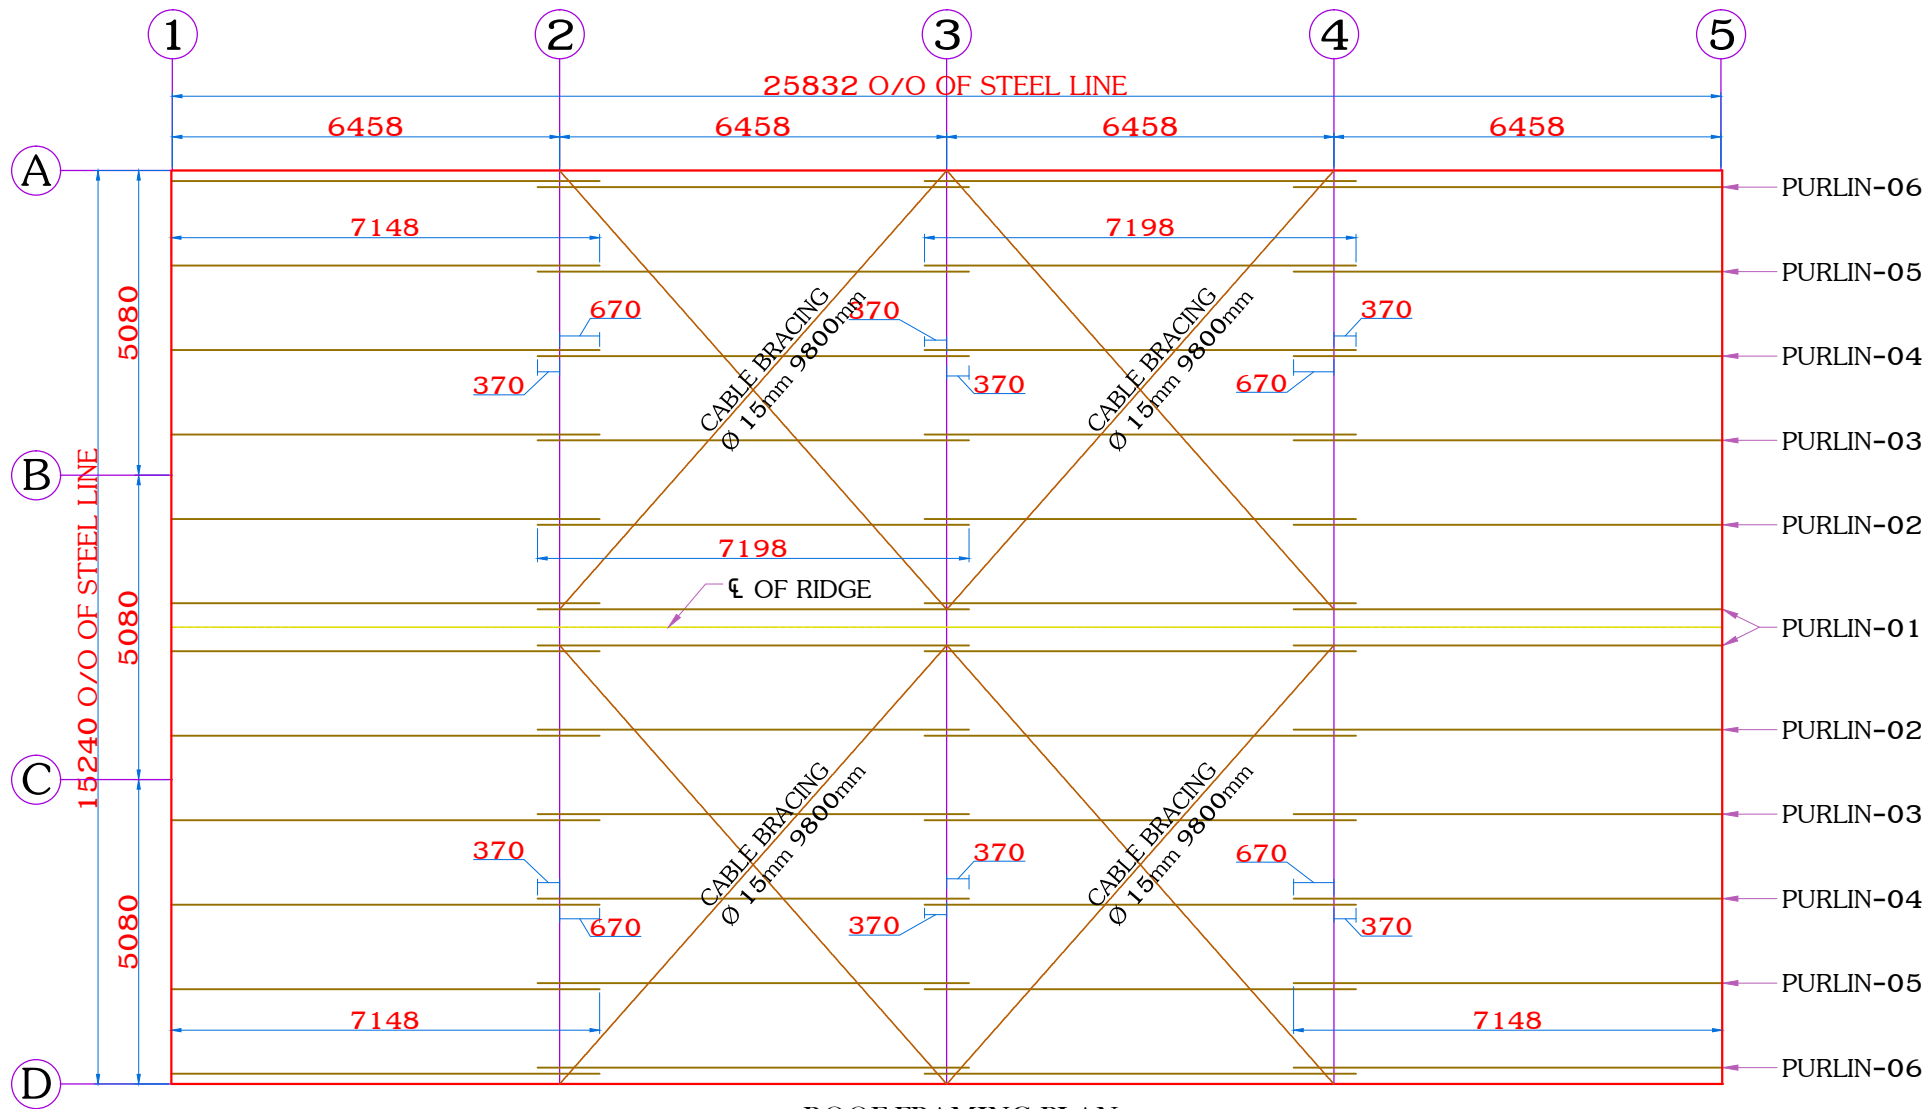

ROOF FRAMING PLAN

GENERAL NOTES

ALL DIMENSIONS ARE IN 'MM & FEET'.
THIS IS PROPOSAL DRAWING ONLY,
NOT FOR CONSTRUCTION.
THIS DRAWING IS NOT TO SCALE.

BUILDING ACCESSORIES

00 No. ROOF SKY LIGHT (EACH 3250mm)
00 No. RIDGE VENTILATORS (3000mm)
00 No. F/O FOR WINDOWS (1828x2438)mm
00 No. DOUBLE SLIDING DOOR (3000x3000)

BUILDING DESIGN LOADS

LIVE LOAD = 0.57 KN/SQ.M.
WIND SPEED = 135 KM/HR.
COLLATERAL LOAD = 0.00 KN/SQ.M.
EXPOSURE = B

BUILDING DESIGN CODES

DESIGN CODES AS PER AISC
LOADS APPLICATION AS PER MBMA
COLD FORMED DESIGN CODES AS PER AISI

PROJECT INFORMATION

QUOTE NO.	MBS-NEW VISION		BLDG. NO. : 01	
BLDG. NAME	STEEL SHED			
REV. NO.	DRN. BY	CHK. BY	DATE	SHEET NO.
00	FZN	UBD	15-01-2019	FAB-12
--	--	--	--	--

STEEL CONSTRUCTOR

MAIMAAR
STEEL BUILDING PVT. LTD.

105, Basement Floor, Lalazar Commercial
Area, Raiwind Road, Thokar Niaz Baig
Lahore, Pakistan
Website: www.maimaargroup.com
E-mail: nasir.abbas@maimaargroup.com
E-mail: maimaar.steel@gmail.com
Mob-1 : +(92-300) 807 4017
Mob-2 : +(92-333) 807 1115