


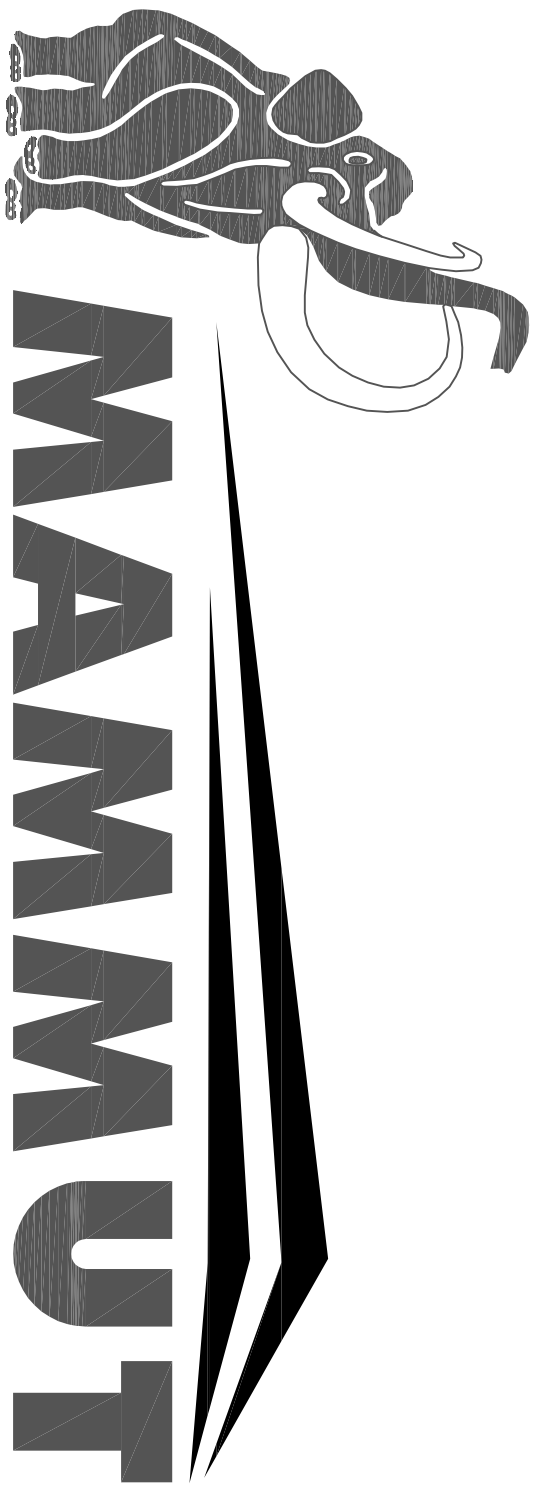


موسوٹ Building Systems F.Z.c

1st Floor, Q-429, Phase-II,
Defense Housing Authority
Lahore Cantt-Pakistan
Website: www.mbs.ae
E-mail: sales@mbs.ae
Phone: +(92-42) 3574 3066-68
Fax. : +(92-42) 3589 8696

PROPOSAL DRAWING

AREA OFFICE / QUOTE NO. SENDERS: PK-14-202

CUSTOMER:			
Rafthan Maize Products Co. Ltd.			
BUILDING NAME:			
Shed Building			
PROJECT TITLE :			
Proposed Shed For Rafthan Maize Products Co. Ltd.			
PREPARED BY : QASIM		CHECKED BY : NASIR	
DATE: 31-10-2014	BLDG. NO. 02 (OPTION-1)	REV.:00	

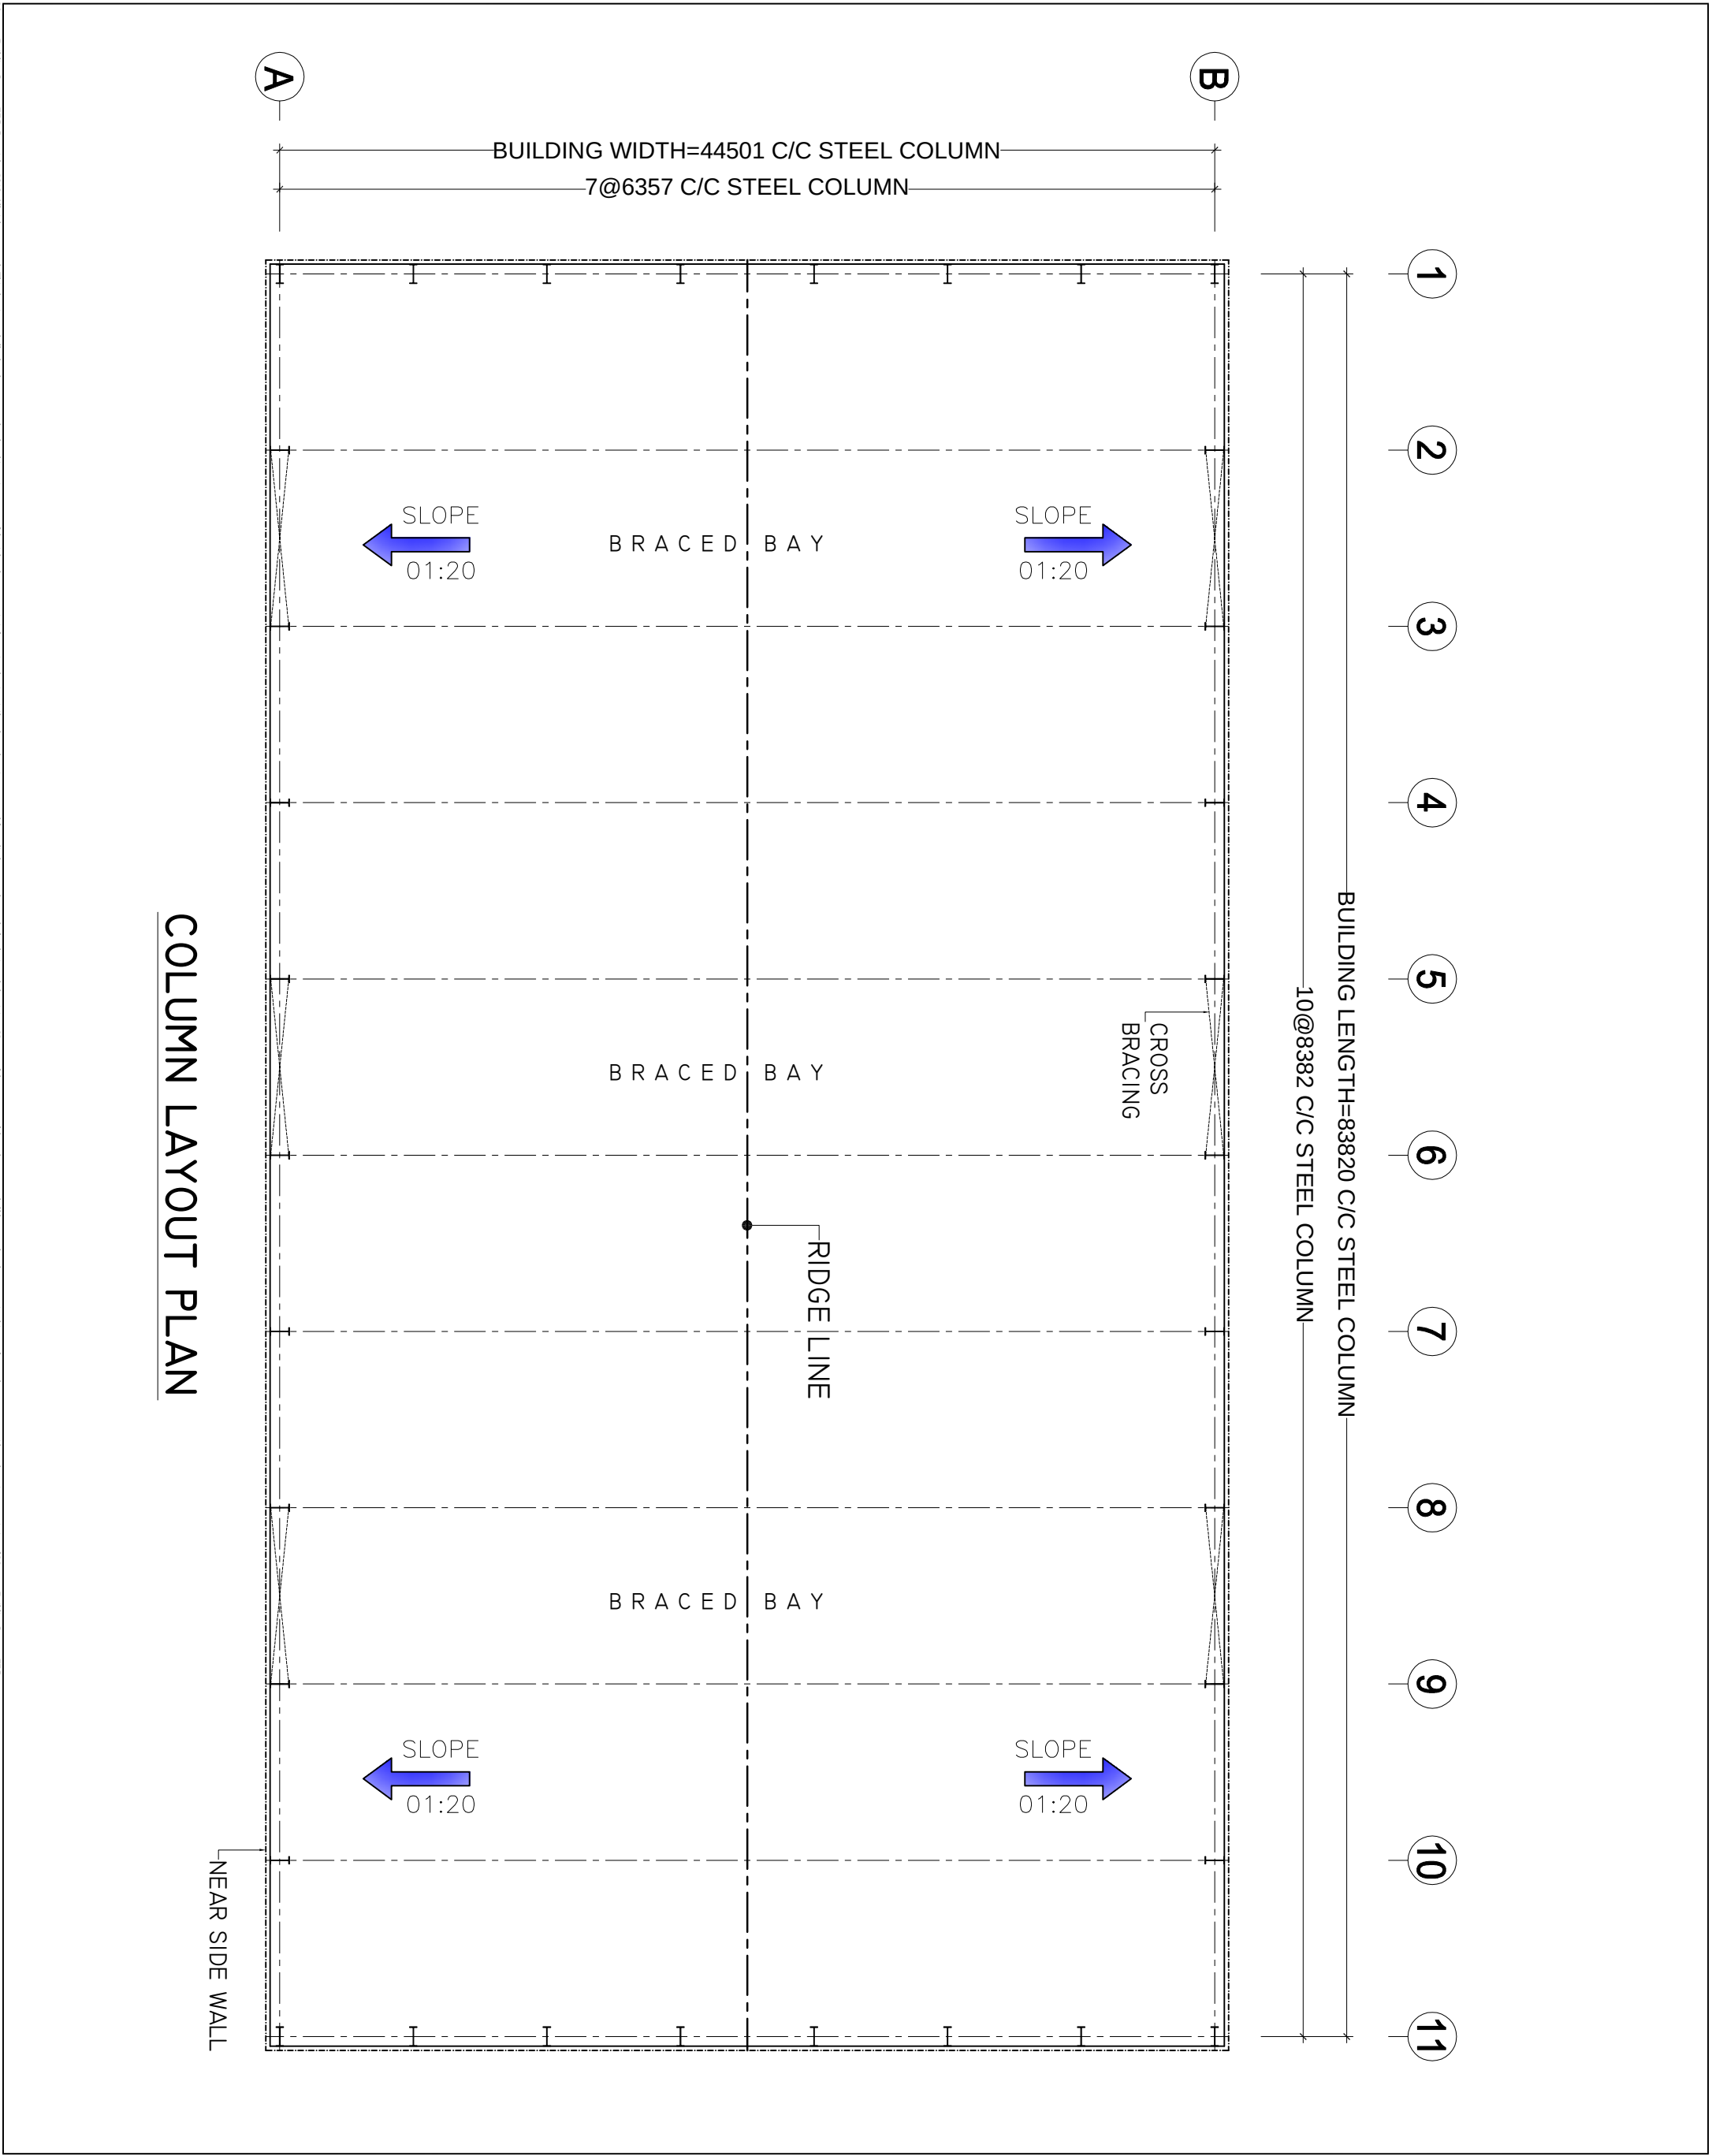

General Notes 1. All dimensions are in millimeters (mm). 2. Panel thickness is the Total Coated Thickness (TCTP). 3. All Dimensions, Levels Shown in the PROPOSAL DRAWING is indicative only, final design Dimensions, Levels will be shown in our APPROVAL DRAWING in design stage. 4. For penal description, Please refer to technical and financial proposal.									
This document is PROPOSAL DRAWING data of MAMMUT BUILDING SYSTEMS FZC. not for construction.									
THE BUILDING HAS BEEN DESIGNED TO SUPPORT IT'S OWN DEAD LOAD PLUS:									
LIVE LOAD ON ROOF 0.57 KN/SQ.M.									
LIVE LOAD ON RAFT 0.57 KN/SQ.M.									
WIND SPEED 130.0 KPH (Exposure-B)									
ADD'L COLLATERAL LOAD 0.00 KN/SQ.M.									
ROOF SNOW LOAD - KN/SQ.M.									
SEISMIC LOAD ZONE-3B									
RAINFALL INTENSITY 150 CM/HR									
AS PER MAKKA, 2006 METAL BUILDING SYSTEMS MANUAL									


00	31-10-2014		QASIM	NASIR
Rev. No.	Date	DSN	DRN	CHK
PROJECT :				
Proposed Shed For Rafhan Maize Products Co. Ltd.				
CUSTOMER :				
Rafhan Maize Products Co. Ltd.				
STEEL CONTRACTOR :				
MAMMUT Building Systems FZC[®] Labore Office 1st Floor Q-429, Phase-II, Defense Housing Authority Lahore Cantt-Pakistan Website : 002-42) 3574 3066-68 Fax. : +02-42) 3589 8896				
QUOTE NO.		: PK-14-202		
Bldg. No.		: 02 (OPTION-1)		
Bldg. Name		: Shed Building		
No. Of Identical Bldg.		: ONE		
Drawing Title :		COLUMN LAYOUT PLAN		
Scale		Sheet Size		Sheet No.
N.T.S.		A3		01

- General Notes**
- All dimensions are in millimeters (mm).
 - Panel thickness is the Total Coated Thickness (TCTP).
 - All Dimensions, Levels Shown in the PROPOSAL DRAWING is indicative only, final design Dimensions, Levels will be shown in our APPROVAL DRAWING in design stage.
 - For panel description, Please refer to technical and financial proposal

This document is PROPOSAL
DRAWING data of MAMMUT
BUILDING SYSTEMS FZC.
not for construction.

1 2 3 4 5 6 7 8 9 10 11

BUILDING LENGTH=83820 C/C STEEL COLUMN
10@8382 C/C STEEL COLUMN

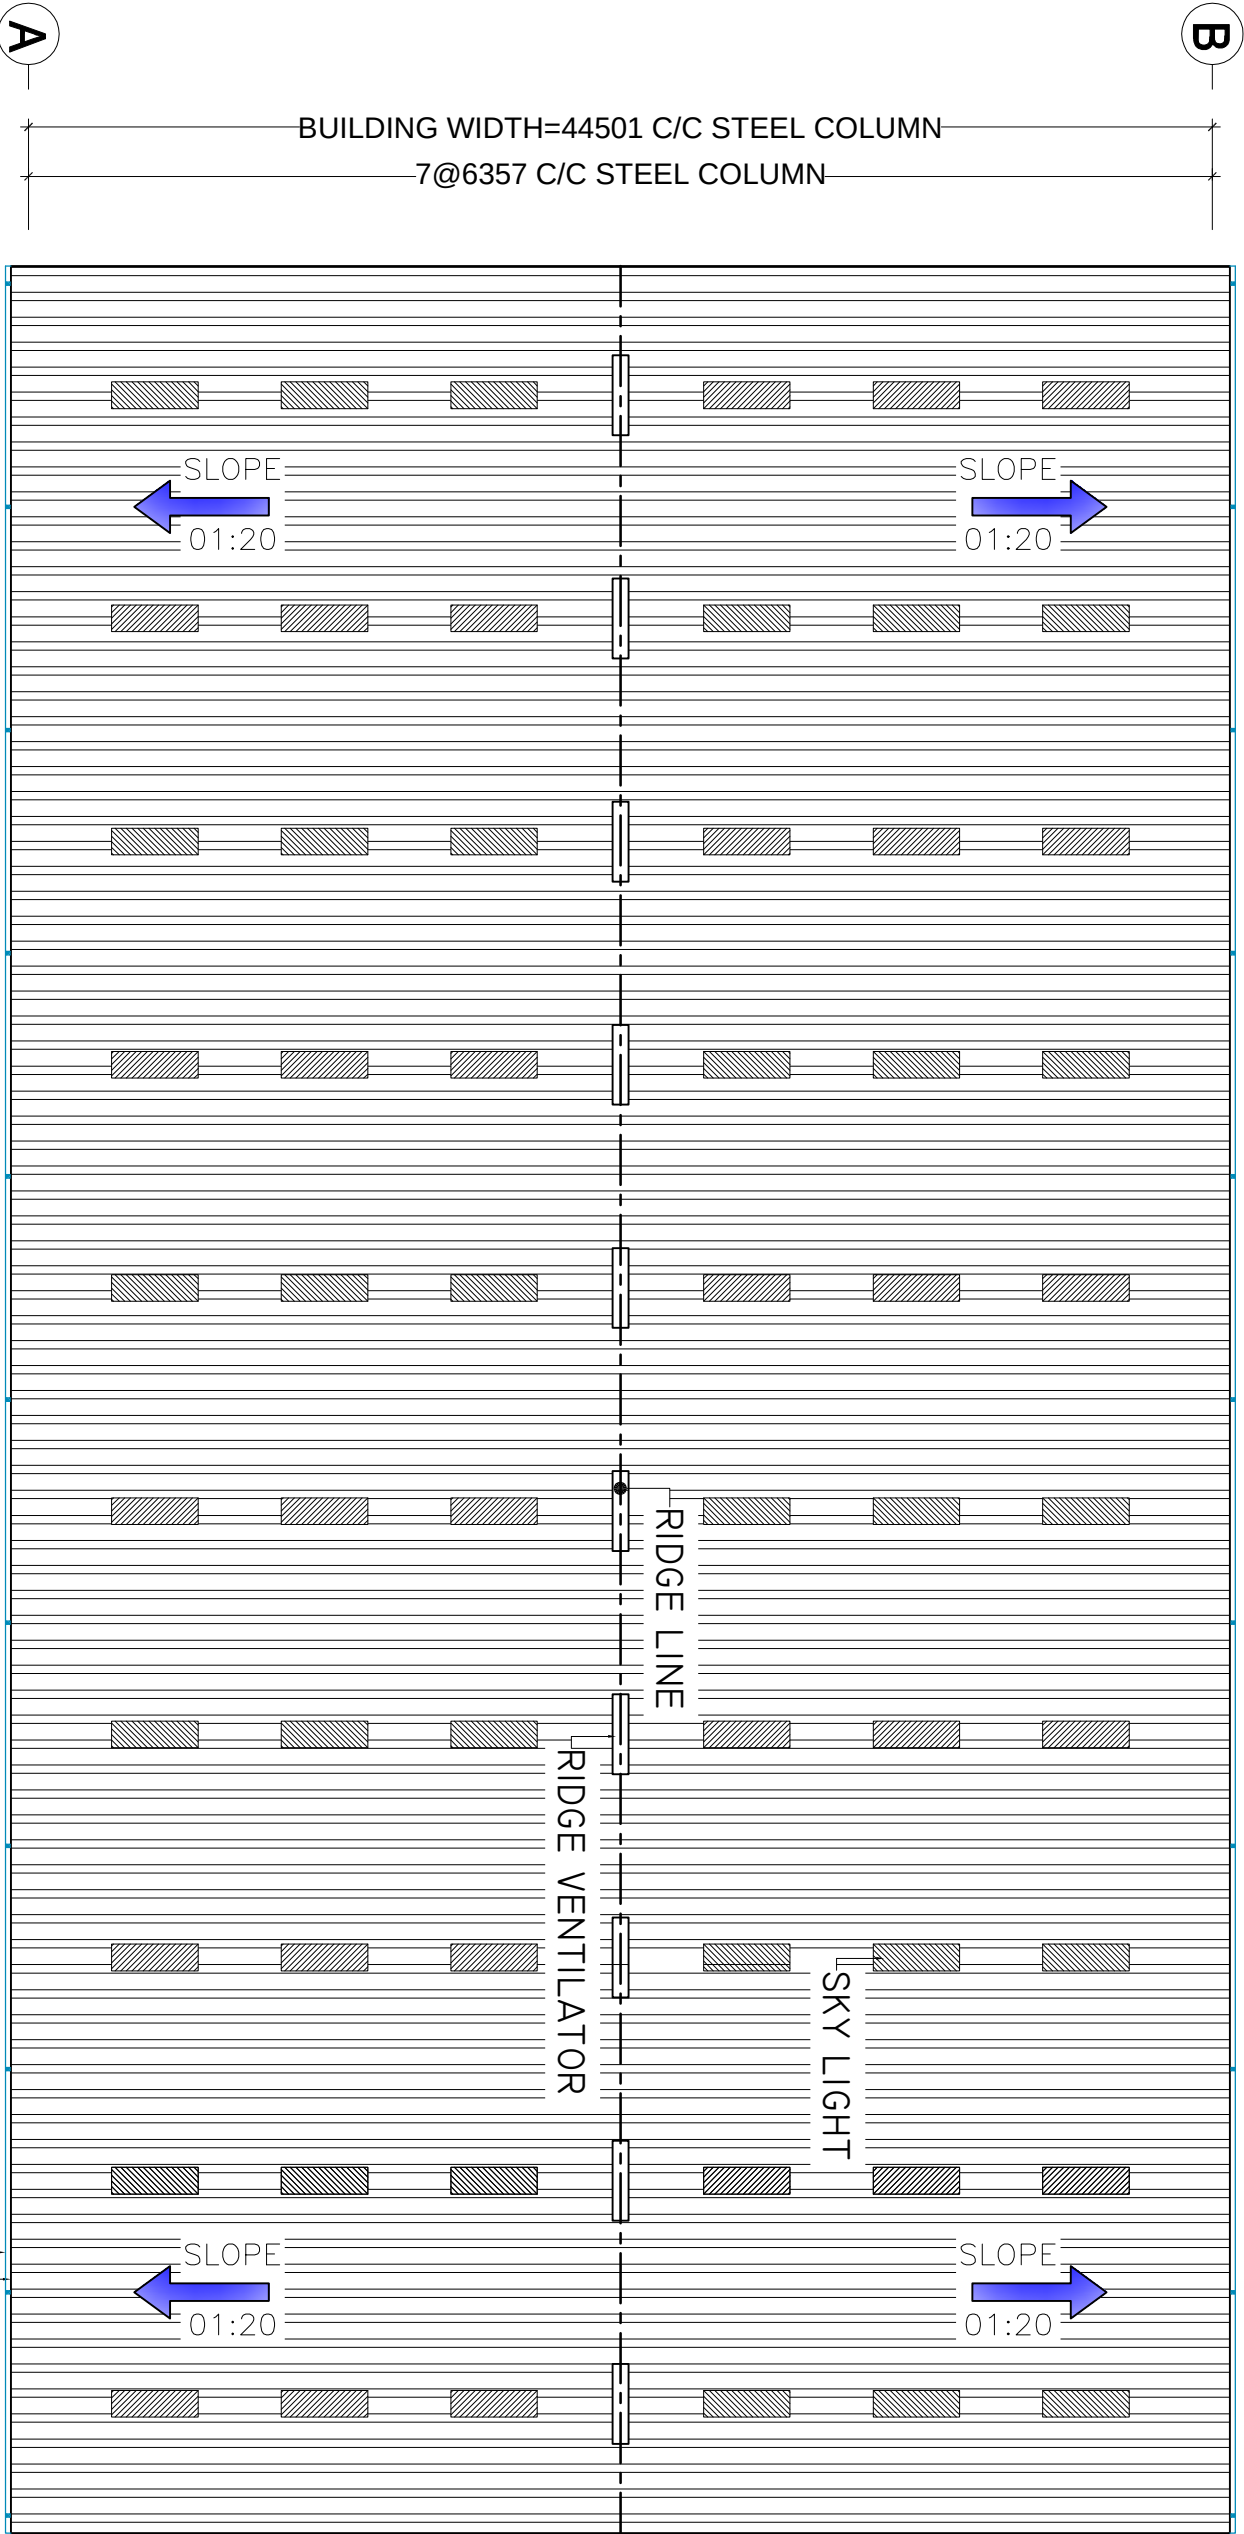

TOP ROOF LAN

NEAR SIDE WALL
EAVE GUTTER &
DOWNSPOUTS



Lahore Office 1st Floor, Q-429,
Phase-II, Defense Housing
Authority, Lahore Cantt-Pakistan
Website: www.mbs.ae
Phone : +92-42) 3574 3066-68
Fax : +92-42) 3589 8896

CUSTOMER :
Rafhan Maize Products Co. Ltd.

Proposed Shed For Rafhan
Maize Products Co. Ltd.

00	31-10-2014		QASIM	NASIR
Rev. No.	Date	DSN	DRN	CHK
PROJECT :				


STEEL CONTRACTOR :

QUOTE NO. : PK-14-202


Blg. No. : 02 (OPTION-1)
Blg. Name : Shed Building

No. Of identical Blg. : ONE
Drawing Title : TOP ROOF PLAN

Scale : N.T.S. Sheet Size : A3 Sheet No. : 02

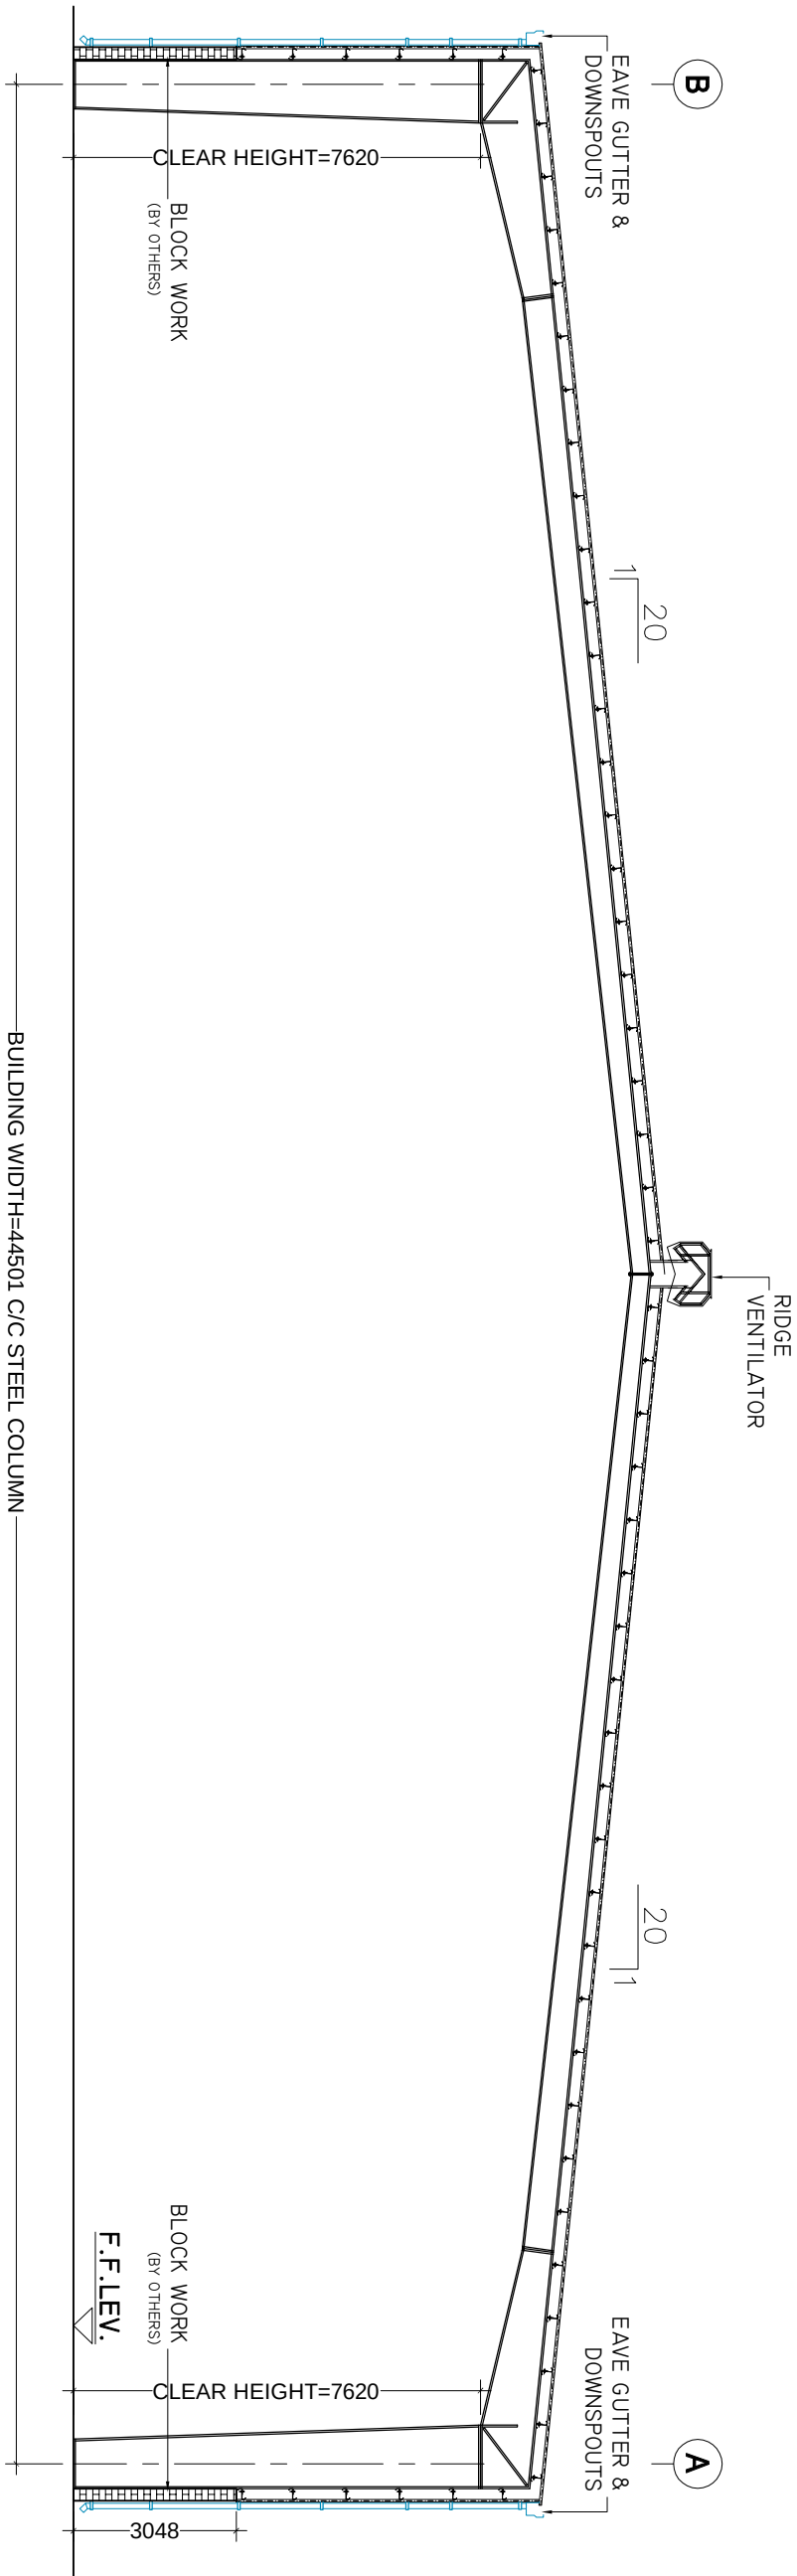

TYPICAL RIDGE FRAME CROSS SECTION
AT GL. 2 THRU 10

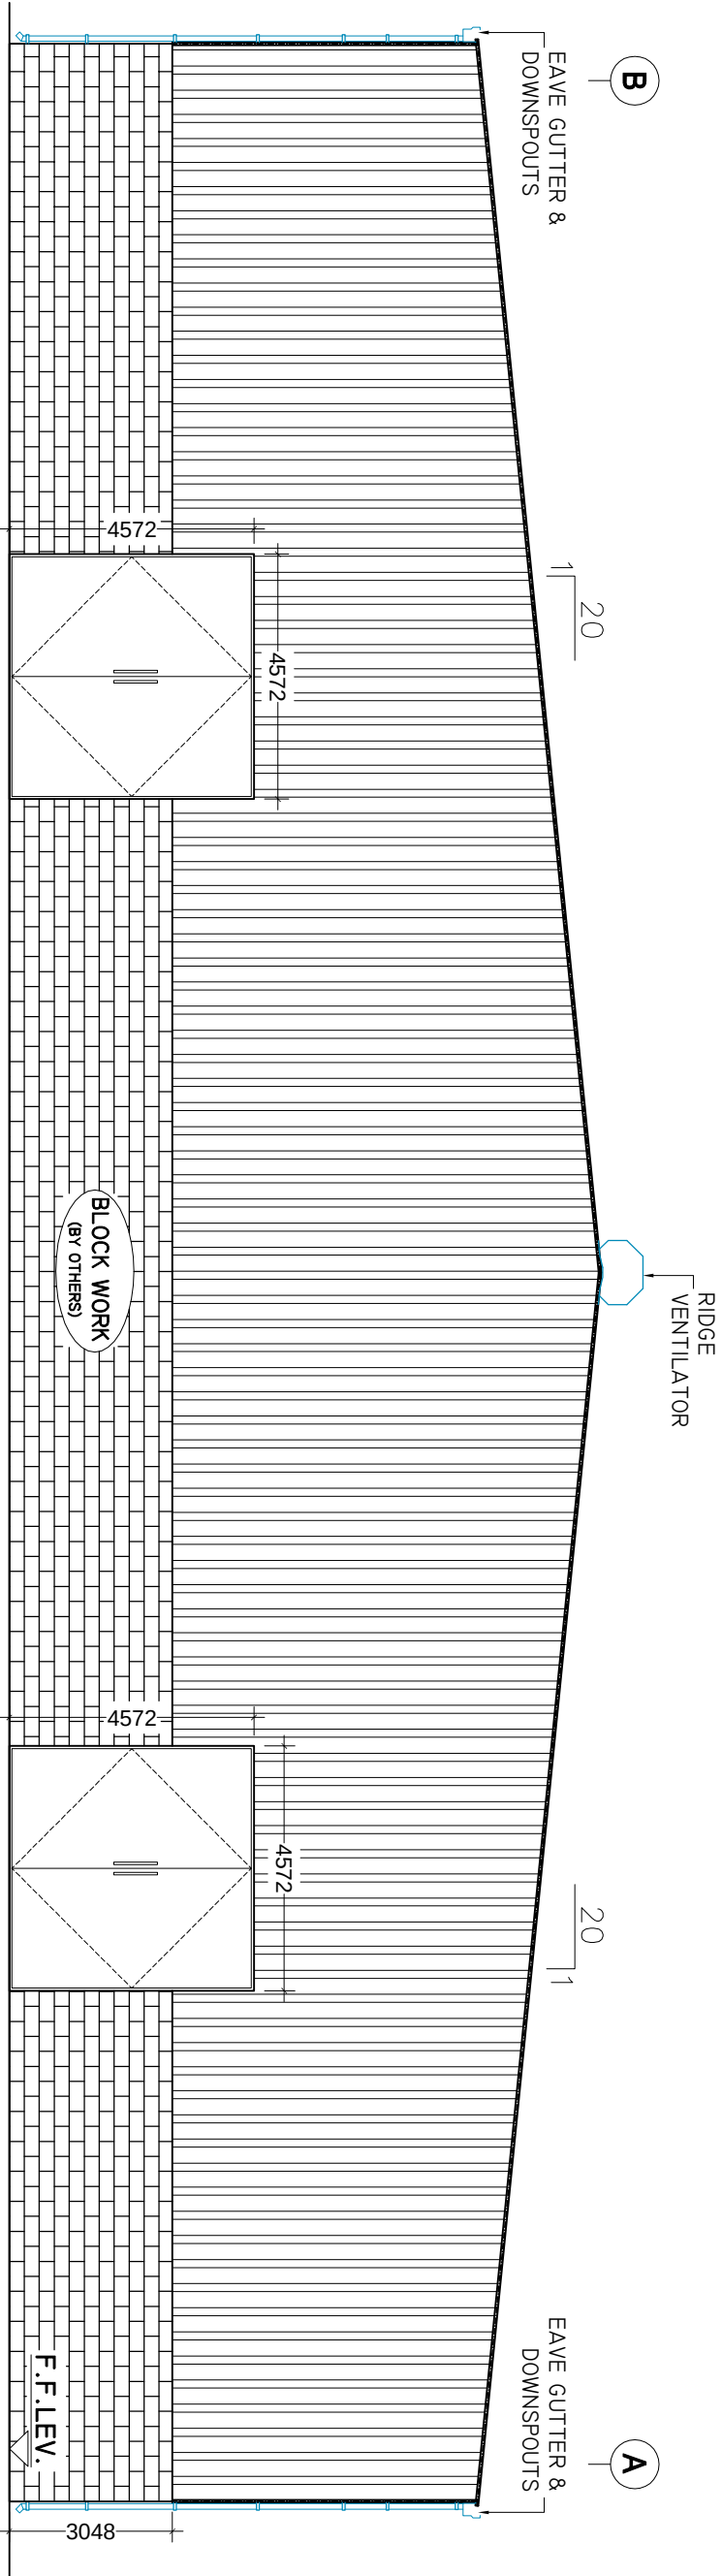

RIGHT & LEFT END WALL ELEVATION

- General Notes**
- All dimensions are in millimeters (mm).
 - Panel thickness is the Total Coated Thickness (TCTP).
 - All Dimensions, Levels Shown in the PROPOSAL DRAWING is indicative only, final design Dimensions, Levels will be shown in our APPROVAL DRAWING in design stage.
 - For penal description, Please refer to technical and financial proposal

This document is PROPOSAL
DRAWING data of MAMMUT
BUILDING SYSTEMS PZC.
not for construction.

00	31-10-2014		QASIM	NASIR
Rev. No.	Date	DSN	DRN	CHK

PROJECT :

Proposed Shed For Rafhan
Maize Products Co. Ltd.

CUSTOMER :

Rafhan Maize Products Co. Ltd.

STEEL CONTRACTOR :



Lahore Office 1st Floor, Q-429,
Phase-II, Defense Housing
Authority, Lahore Cantt-Pakistan
Website: www.mbsae
Phone : +92-42) 3574 3066-68
Fax : +92-42) 3589 8896

QUOTE NO.	: PK-14-202
Blg. No.	: 02 (OPTION-1)
Blg. Name	: Shed Building
No. Of identical Blg.	: ONE
Drawing Title	: CROSS SECTION END WALL ELEVATION
Scale	: N.T.S.
Sheet No.	: A3
Sheet No.	: 03

1

2

3

4

5


6

7

8

BUILDING LENGTH=83820 C/C STEEL COLUMN

RIDGE VENTILATOR

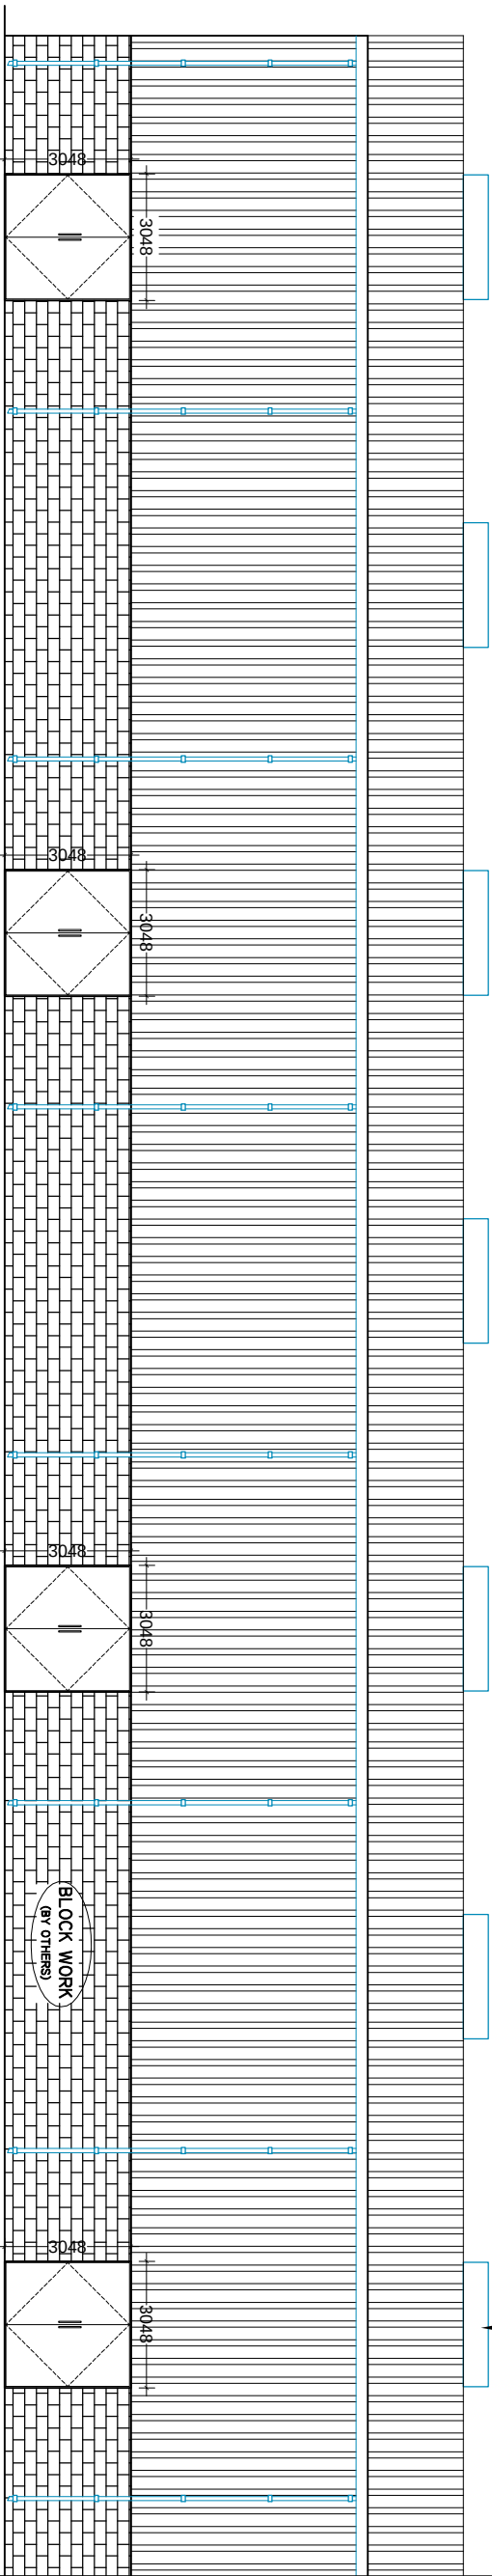

NEAR & FAR SIDE WALL ELEVATION

4

5

6

7

8


9

10

11

BUILDING LENGTH=83820 C/C STEEL COLUMN

RIDGE VENTILATOR

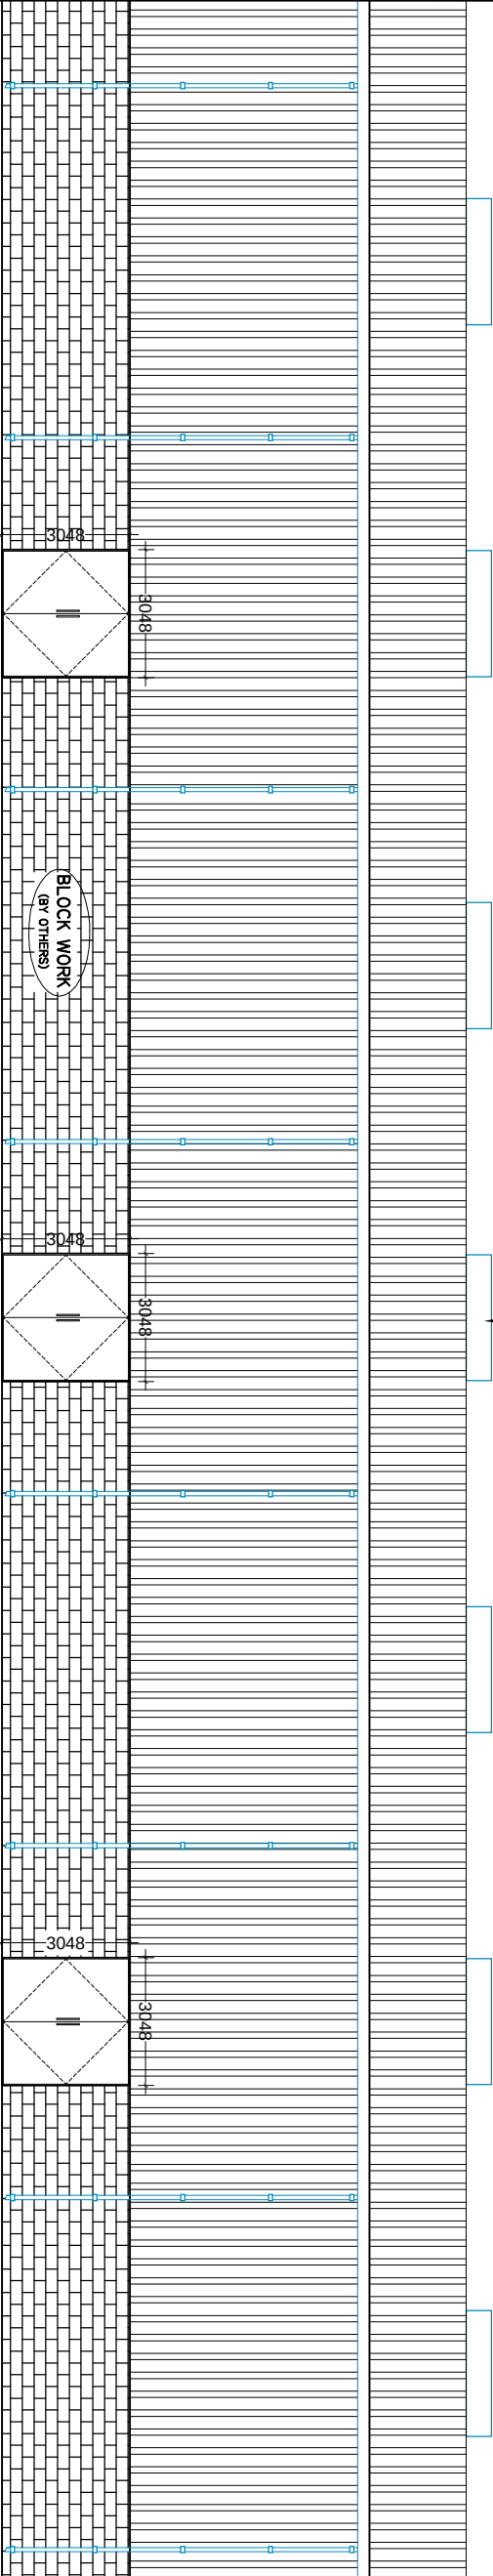

- General Notes**
- All dimensions are in millimeters (mm).
 - Panel thickness is the Total Coated Thickness (TCTP).
 - All Dimensions, Levels Shown in the PROPOSAL DRAWING is indicative only, final design Dimensions, Levels will be shown in our APPROVAL DRAWING in design stage.
 - For penal description, Please refer to technical and financial proposal

This document is PROPOSAL DRAWING data of MAMMUT BUILDING SYSTEMS PZC. not for construction.



MAMMUT
Building Systems PZC

Lahore Office 1st Floor, Q-429,
Phase-II, Defense Housing
Authority, Lahore Cantt-Pakistan
Website: www.mps.ac
Phone : +92-42) 3574 3066-68
Fax : +92-42) 3559 8896

STEEL CONTRACTOR :

CUSTOMER :

Rafhan Maize Products Co. Ltd.

Proposed Shed For Rafhan
Maize Products Co. Ltd.

00	31-10-2014		QASIM	NASIR
Rev. No.	Date	DSN	DRN	CHK
PROJECT :				

QUOTE NO.	: PK-14-202
Blgd. No.	: 02 (OPTION-1)
Blgd. Name	: Shed Building
No. Of identical Bldg.	: ONE
Drawing Title	: SIDE WALL ELEVATION

Scale	Sheet Size	Sheet No.
N.T.S.	A3	04