




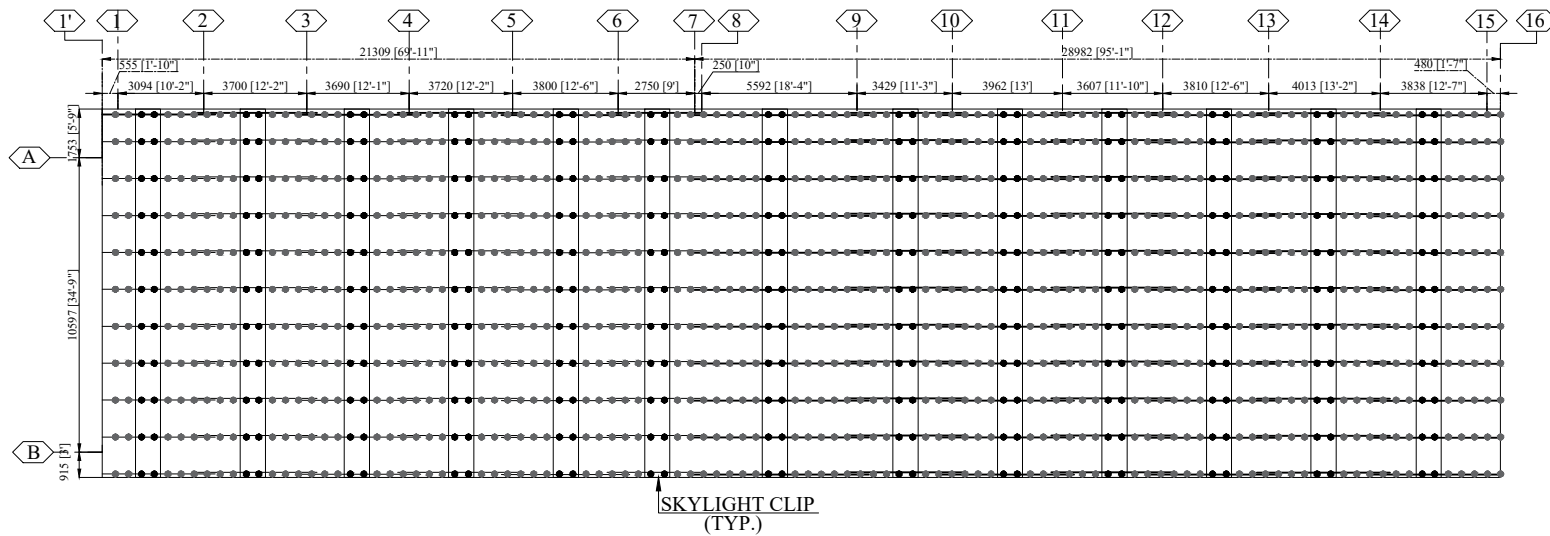

- LOCK SEAM SHEET CLIP DISTANCE 470mm C/C
- SKYLIGHT CLIP DISTANCE 491mm C/C

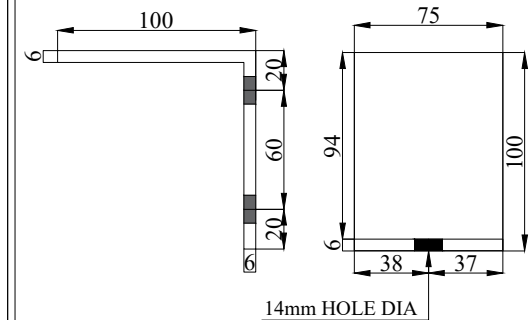

DETAIL OF [L-CLIP-100*100*75*6]

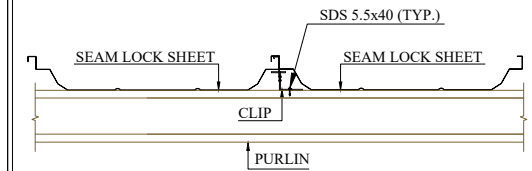

PURLIN WITH SEAM LOCK CLIP DETAIL

FOR APPROVAL :

IN ORDER TO SCHEDULE THIS PROJECT IN AN EFFICIENT MANNER , KINDLY RETURN THESE DRAWINGS WITH YOUR COMMENTS MARKED IN RED
APPROVAL OF THESE DRAWINGS MAY DELAY THE FABRICATION SCHEDULE AND SUBSEQUENTLY THE DELIVERY OF THE BUILDING.
PLEASE TICK MARK ONLY ONE OF THE FOLLOWING

☐ " APPROVED AS IS "


☐ " APPROVED AS NOTED "

☐ " RESUBMIT AS NOTED "


APPROVE : _____

SIGNATURE: _____


DATE : _____

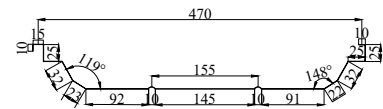


LOCKSEAM SHEET : THK. 0.6mm

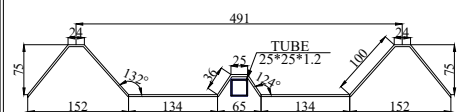

SKYLIGHT PROFILE : THK. 2mm

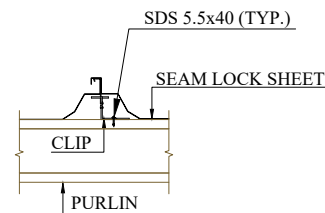

CLIP DETAIL

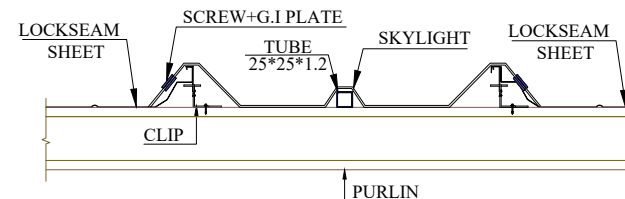

SKYLIGHT & LOCKSEAM SHEET DETAIL TYPICAL

REV	DATE	DESCRIPTION	DRAWN BY	CHK BY	APR BY
00	26-02-26	ISSUED FOR APPROVAL	M.A	S.S	S.S



MAIMAAR STEEL Pvt.Ltd
238, Raiwind Road, Thokar Niaz Baig, Lahore, Pakistan
E-mail: nasir.abbas@maimaargroup.com
E-mail: maimaar.steel@gmail.com
Website: www.maimaargroup.com
E-mail: info@maimaargroup.com
Mob-I : +(92-300) 807 4017 , +(92-333) 807 1115

JOB NO./QUOTE NO.	MSPL-224	BUILDING #	01
PROJECT NAME	SUPPLY & INSTALLATION OF ROOF SHEETING		
CUSTOMER	PAECO		
JOB SITE LOCATION	KASUR		

CLIP'S DETAILS TYPICAL PLAN

DWG NO.

02