



CRANE BRIDGE — TOP VIEW

CRANE BRIDGE, HOIST AND MOTORS — NOT IN MAIMAAR SCOPE (BY OTHERS)

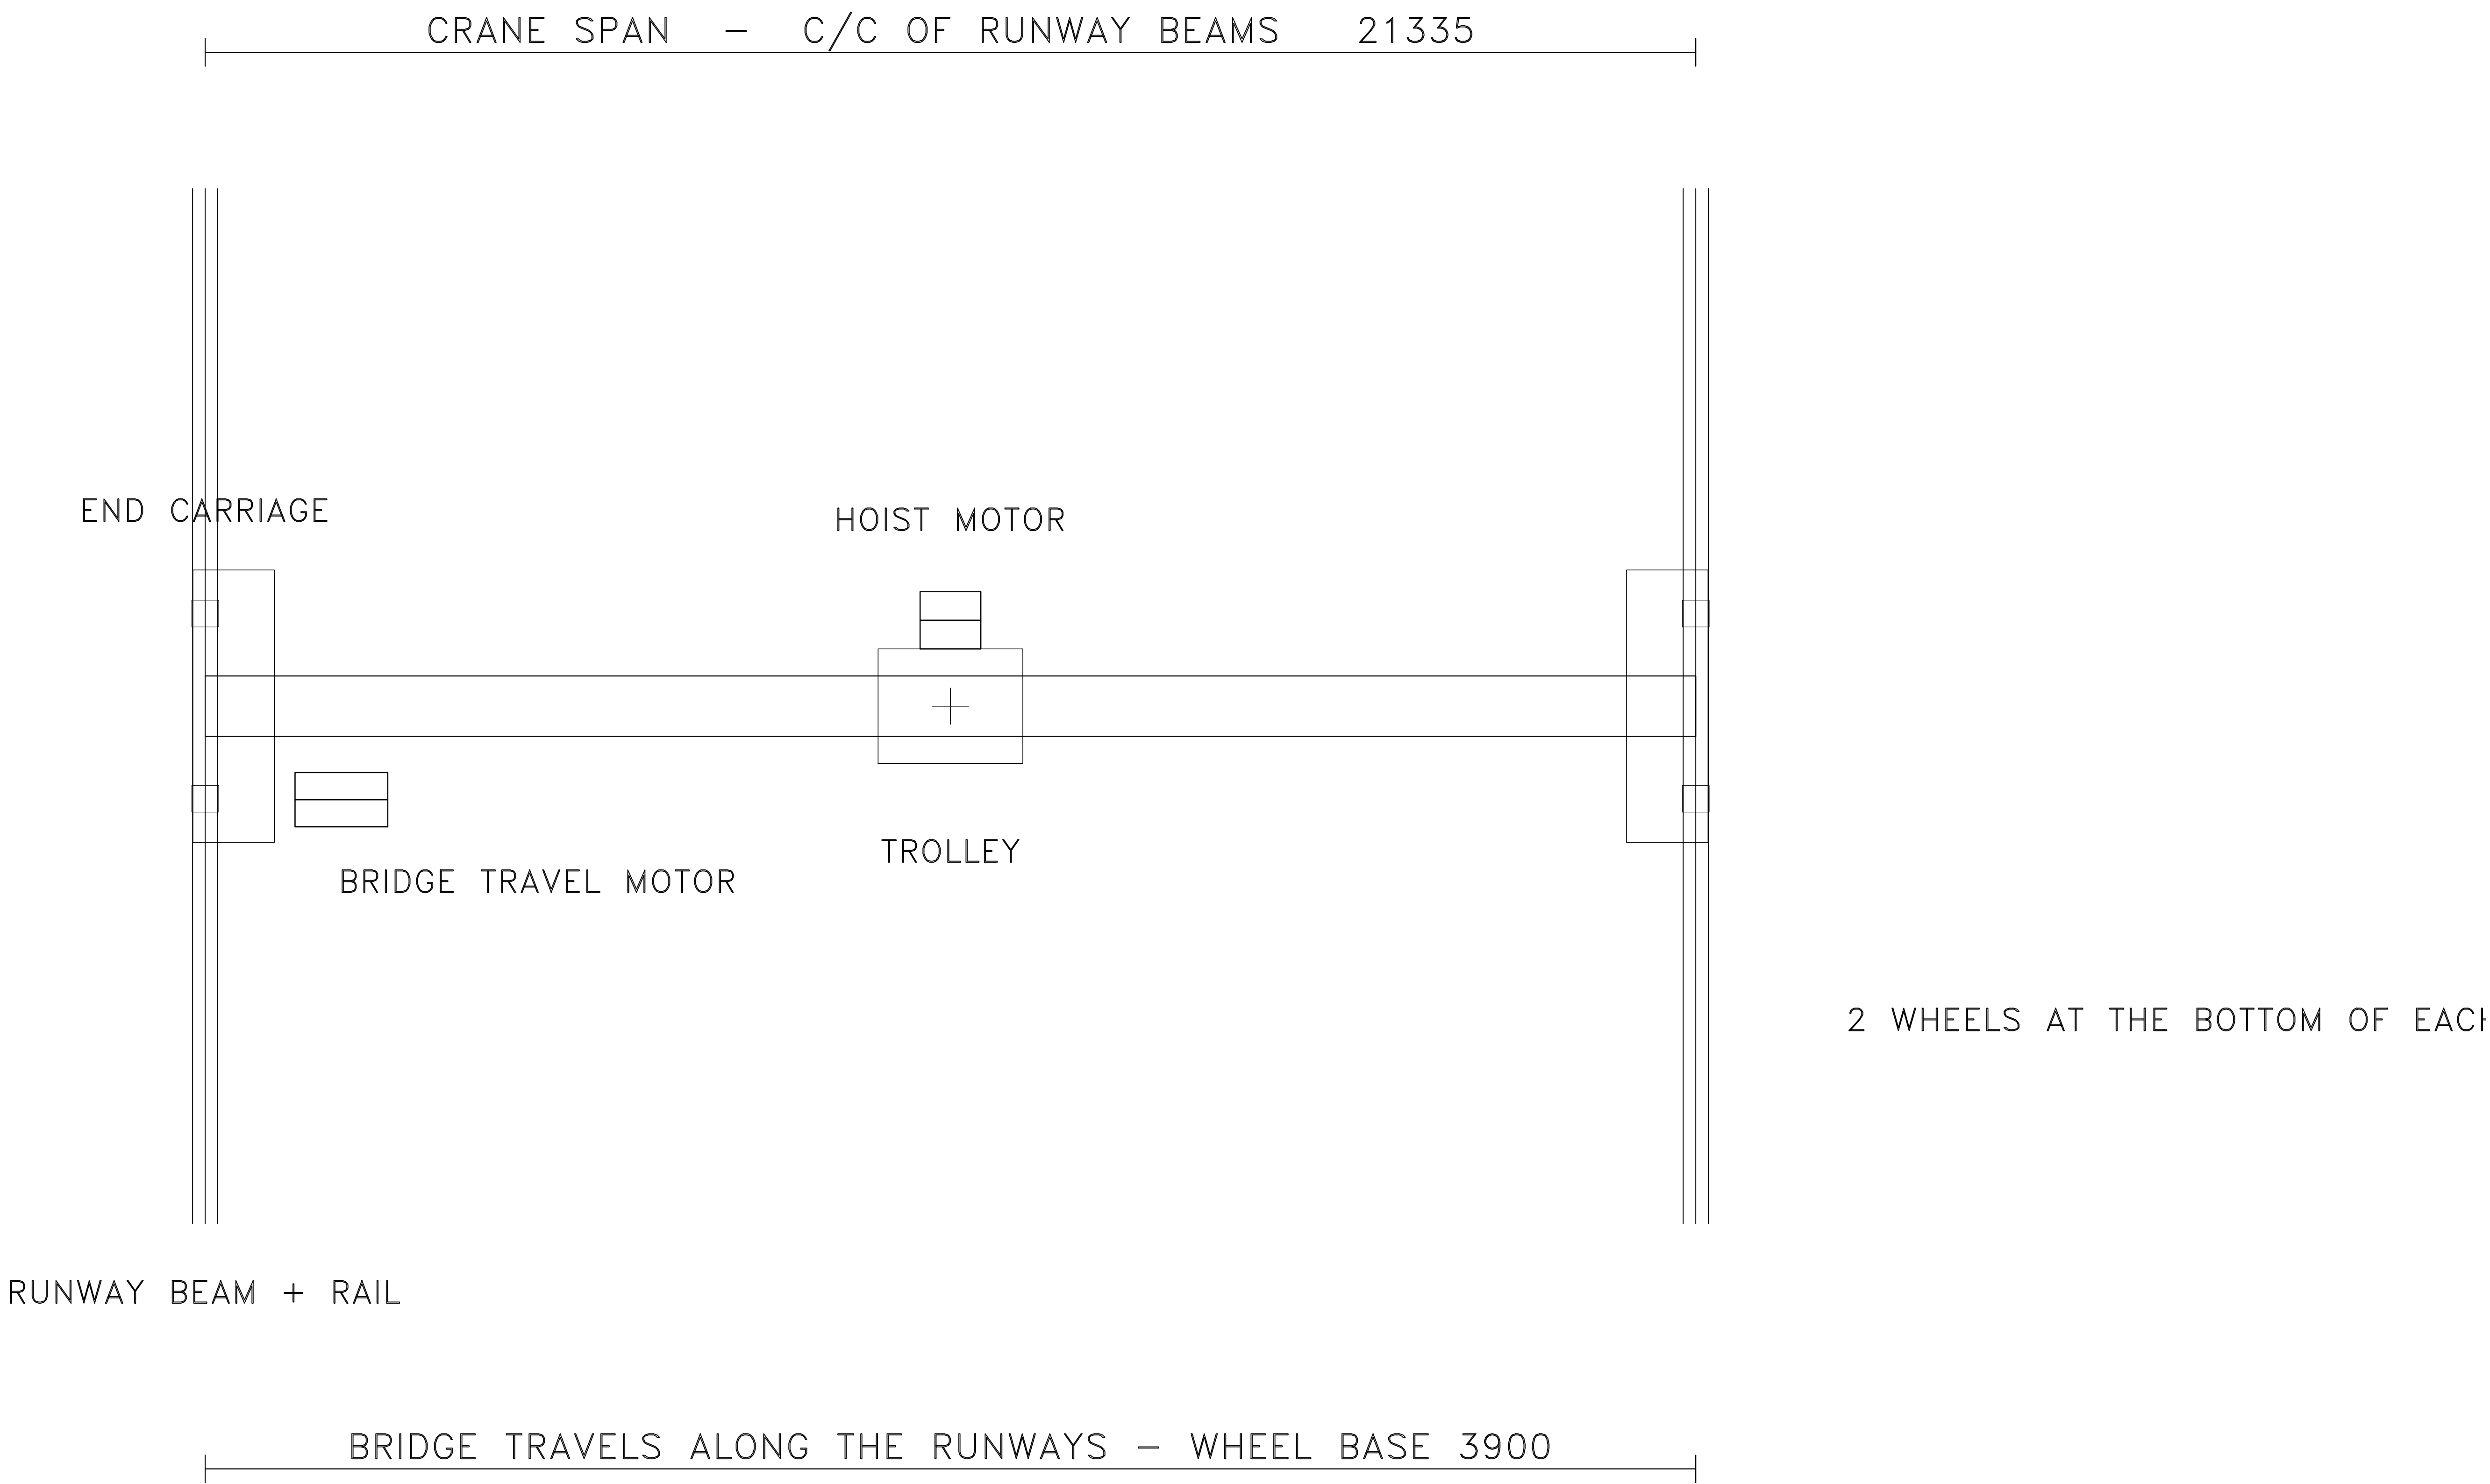

IT BOX, ONLY 345 DEEP
E BOTTOM, ON THE RAIL

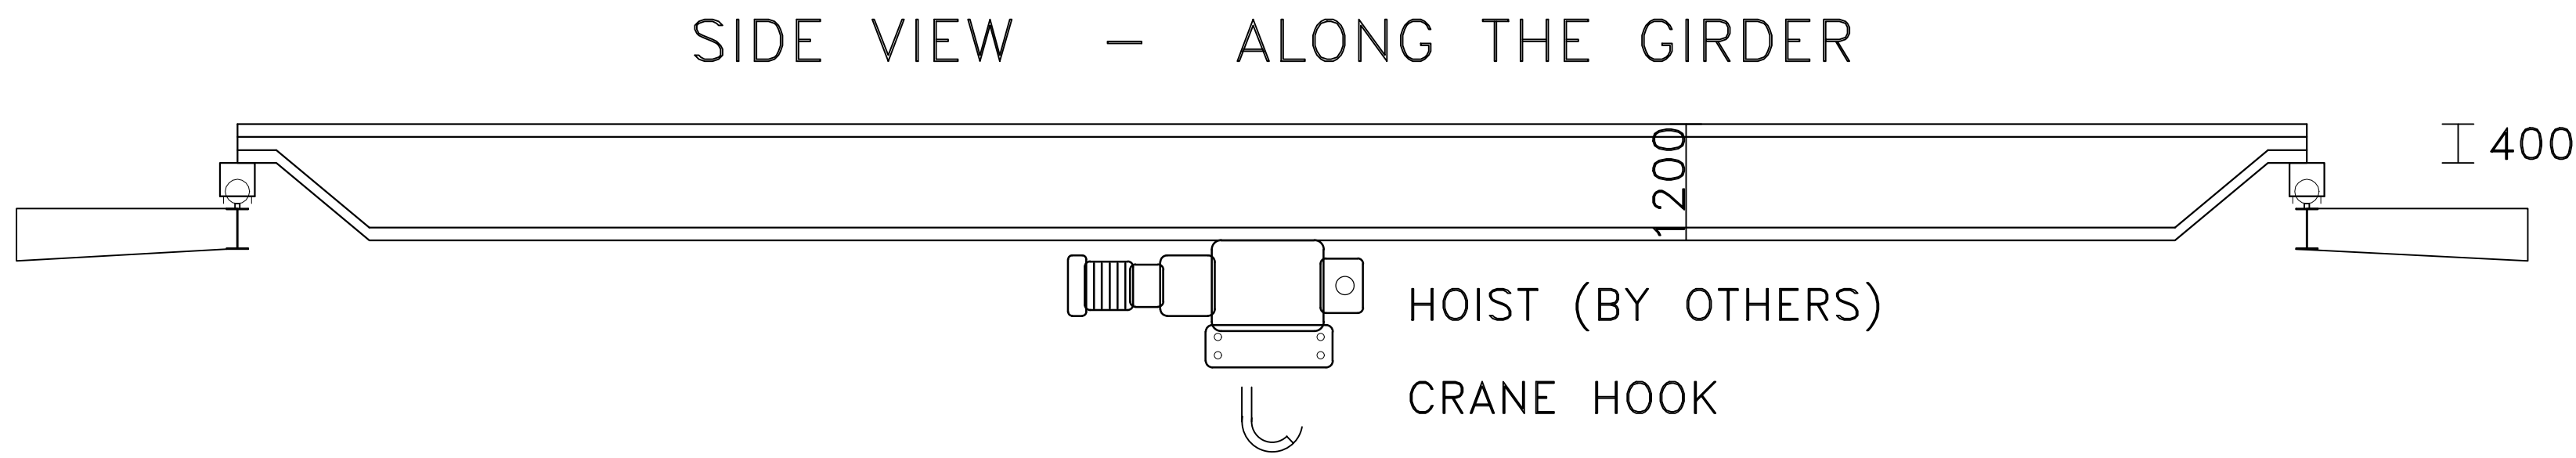


CRANE BRIDGE – GIRDER DEPTH 1200 (RULE: 500 + SPAN/30.5)

CRANE BEAM + RAIL (MAIMAAR SCOPE – SOLID)

CRANE BEAM BRACKET (MAIMAAR SCOPE)

HOOK HEIGHT IS MEASURED FFL TO THE HOOK – IT SETS THE EAVE HEIGHT

HOIST DETAIL – ENLARGED

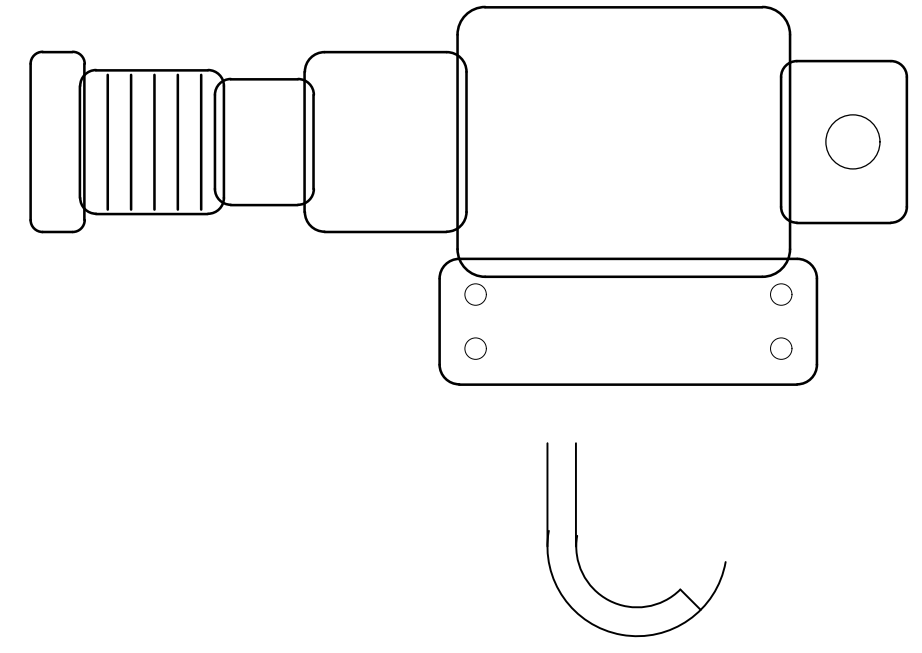

TRACED FROM REFERENCE/CRANE-IN-PEB-SECTION_REFERENCE.WEBP

END CAP / FINNED MOTOR / SHOULDER / MID BOX / DRUM HOUSING / SHEAVE / PLATE / HOOK

CRANE BEAM – SECTION, ELEVATION AND RAIL

PLATE SIZES READ OFF THE MSPL-032 SINGLE-PART SHEET (MAIMAAR FACTORY, 10 MT)

ING ON THE RAIL (CRANE – BY OTHERS)

D X 50 I-SECTION, LIKE A RAILWAY TRACK

FLANGE PL 10 X 225 (OF34 / OF35)

BUILDING COLUMN

AM BRACKET / HAUNCH OFF THE COLUMN

FLANGE 225

SECTION

WEB 400

OVERALL 420

WEB PLATE PL 8 X 400 (CRB-1 / CRB-2)

BOTTOM FLANGE PL 10 X 225 (OF33 / OF37)

STIFFENER SPACING 742 (8 PAIRS PER BEAM)


STIFFENER FL 8 X 108 BOTH SIDES (ST4, 128 OFF)


ELEVATION – ALONG THE BEAM

RAIL FOOT 50

RAIL HEAD WIDTH 36

HEIGHT 50

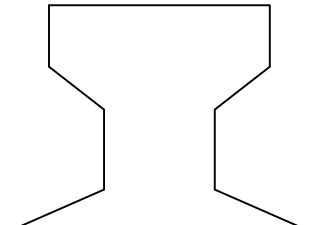

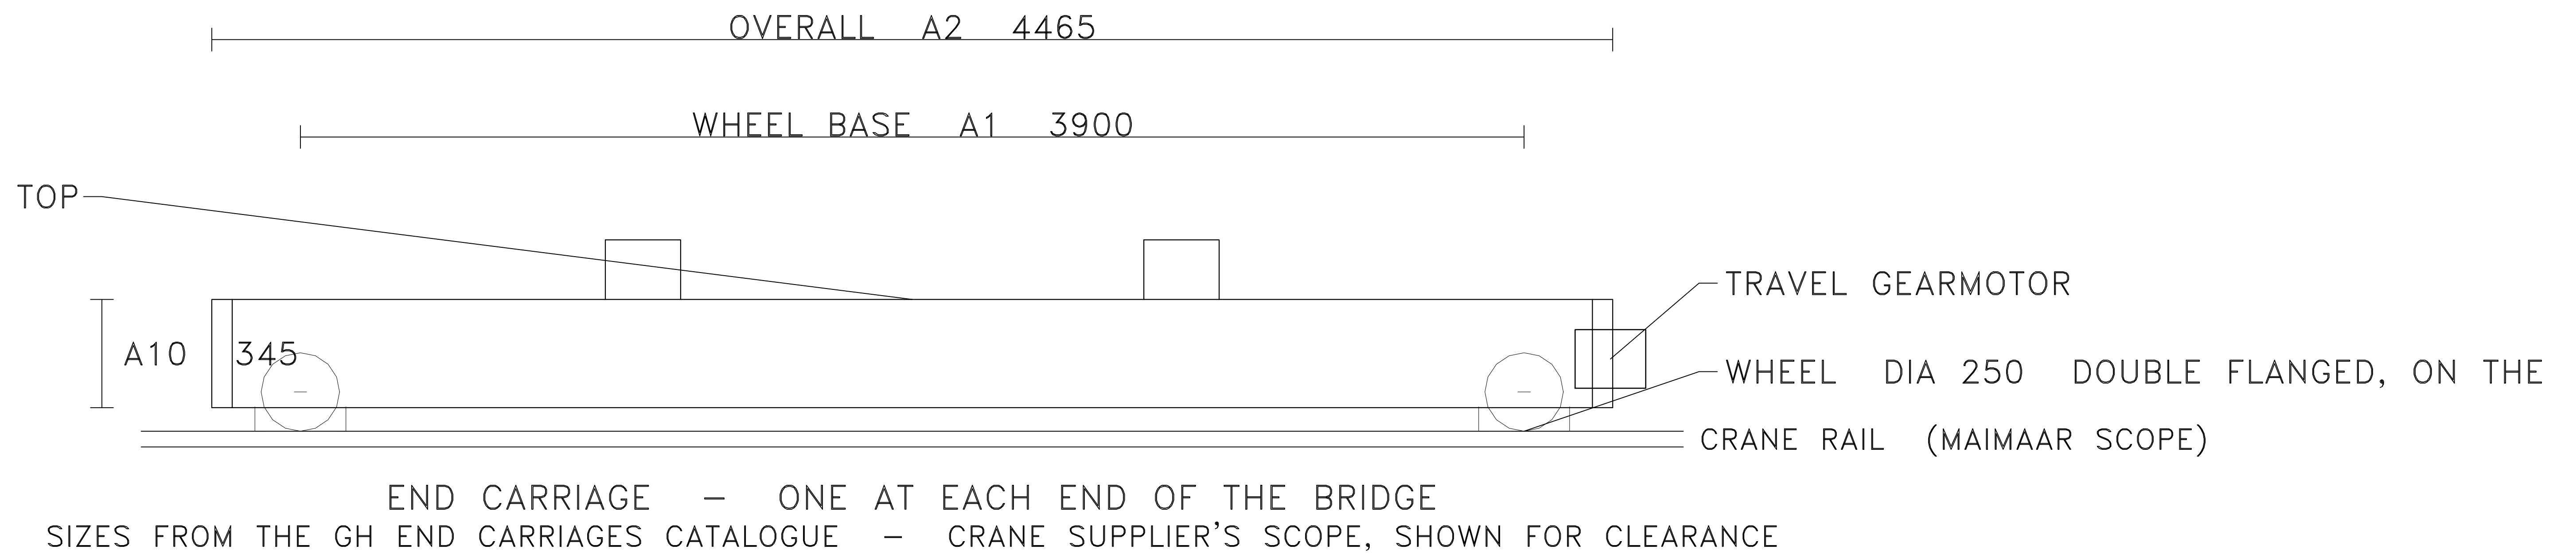

CAPACITY 10 MT

TYPE TOP RUNNING (TR) – MANUAL CH.8 LISTS TR / MONORAIL / UNDERHUNG / JIB / SEMI-GANTRY

END CARRIAGE WHEELS 2 PER END, 4 TOTAL – MANUAL CH.8 NWB = 2 (WORKED 10 MT EXAMPLE)

END CARRIAGE WELDED BOX, WHEELS ON THE BOTTOM RUNNING ON THE RAIL – GH CATALOGUE

STRAIGHT BOX 300–350 DEEP (GH A10 = 345) UNDER A 1000–1400 GIRDER – OWNER, 5-SEP-2026

VERTICAL IMPACT 10% PENDANT OPERATED – MANUAL TABLE 8.3

CMAA SERVICE CLASS C – MANUAL TABLE 8.1

LONGITUDINAL 10% OF MAX WHEEL LOAD, AT TOP OF RAILS – MANUAL CH.8 SEC 2.4.4

RUNWAY BEAM BUILT-UP, DOUBLE SIDE FILLET WELD (≤ 15 MT) – THAL 125-23 SPEC

SCOPE IS SAID BY THE LABEL, NOT BY THE LINETYPE – REF: CRANE-IN-PEB-SECTION

HOOK HEIGHT FFL-TO-HOOK SETS THE EAVE HEIGHT – MANUAL, EAVE HEIGHT GUIDELINE

GIRDER DEPTH $(500 + \text{SPAN}/30.5) \times (\text{CAP}/10)^{0.20}$ – 1000 AT 15,240 SPAN, 1200 AT 21,335

GIRDER END ONE TAPERED CUT TO A 400 DEEP STUB ~ 400 LONG, RESTING ON THE END CARRIAGE

CRANE BEAM $\text{BAY}/15 \times (\text{CAP}/10)^{0.25}$, SNAPPED TO 25 ; 400 WEB AT A 6,096 BAY, 10 MT

CRANE BEAM PLATES WEB PL 8 X 400 / FLANGE PL 10 X 225 / STIFFENER FL 8 X 108

MSPL-032 SINGLE PARTS: CRB-1,2 X4 EACH ; OF33,34,35,37 X4 EACH ; ST4 X128