

MAIMAAR STEEL Pvt.Ltd

105, Raiwind Road, Thokar Niaz Baig ,Lahore, Pakistan



E-mail: nasir.abbas@maimaargroup.com



E-mail: maimaar.steel@gmail.com

Website: www.maimaargroup.com


E-mail: nasir.abbas@maimaargroup.com

Mob-1 : +(92-300) 807 4017 ,+(92-333) 807 1115

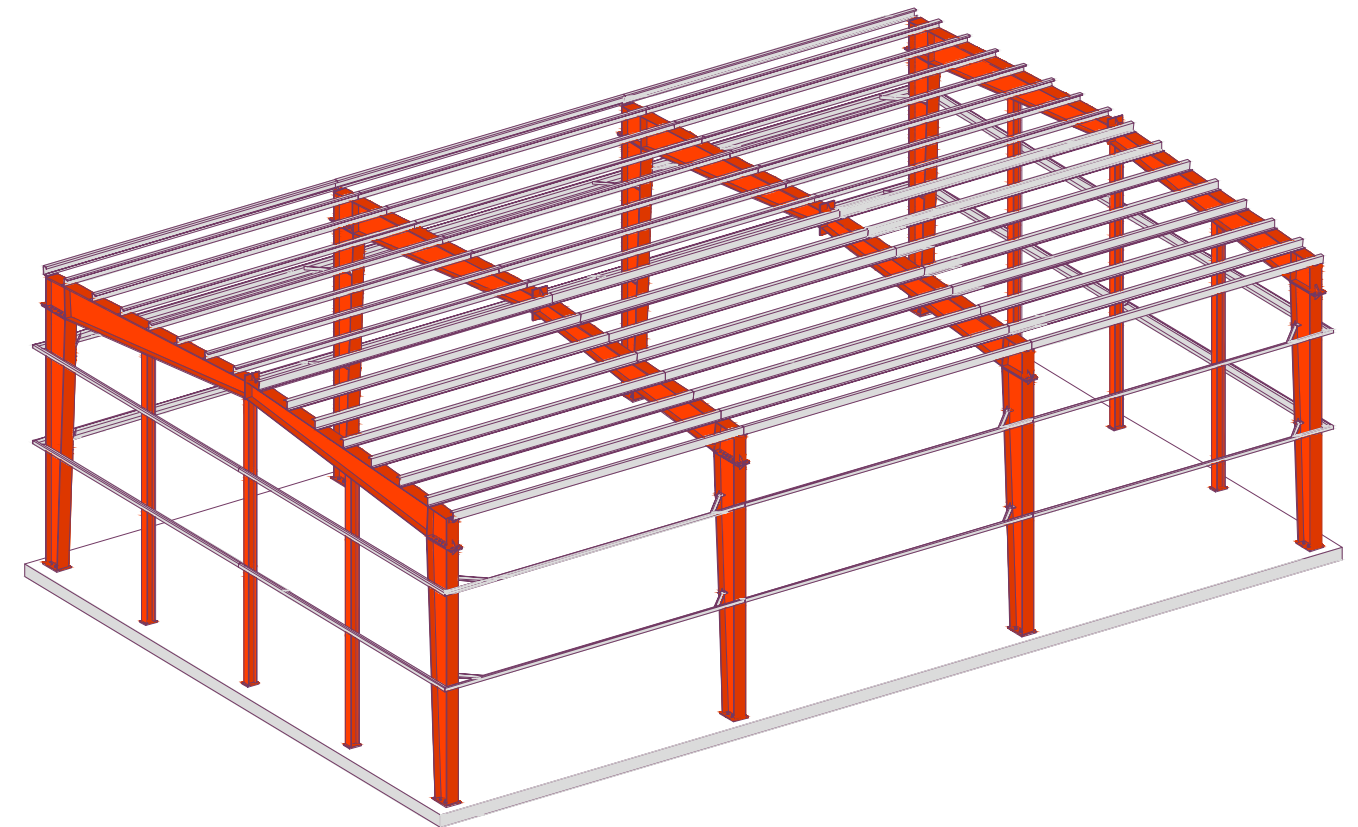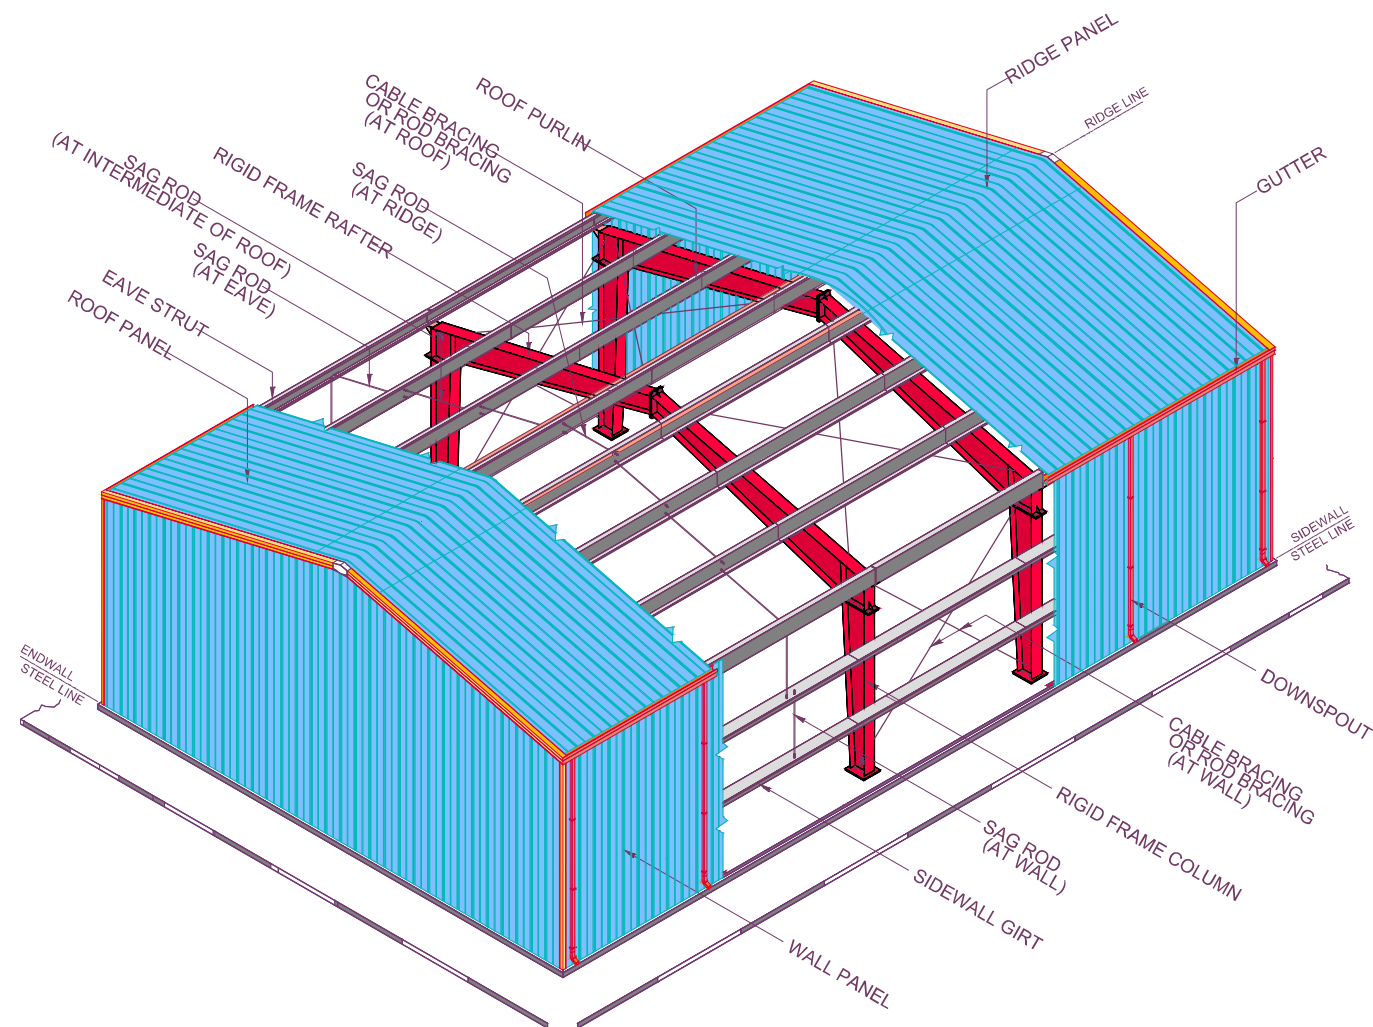


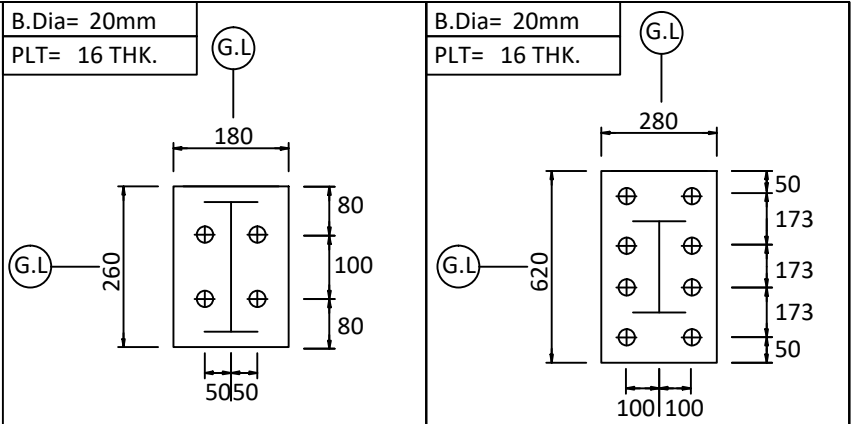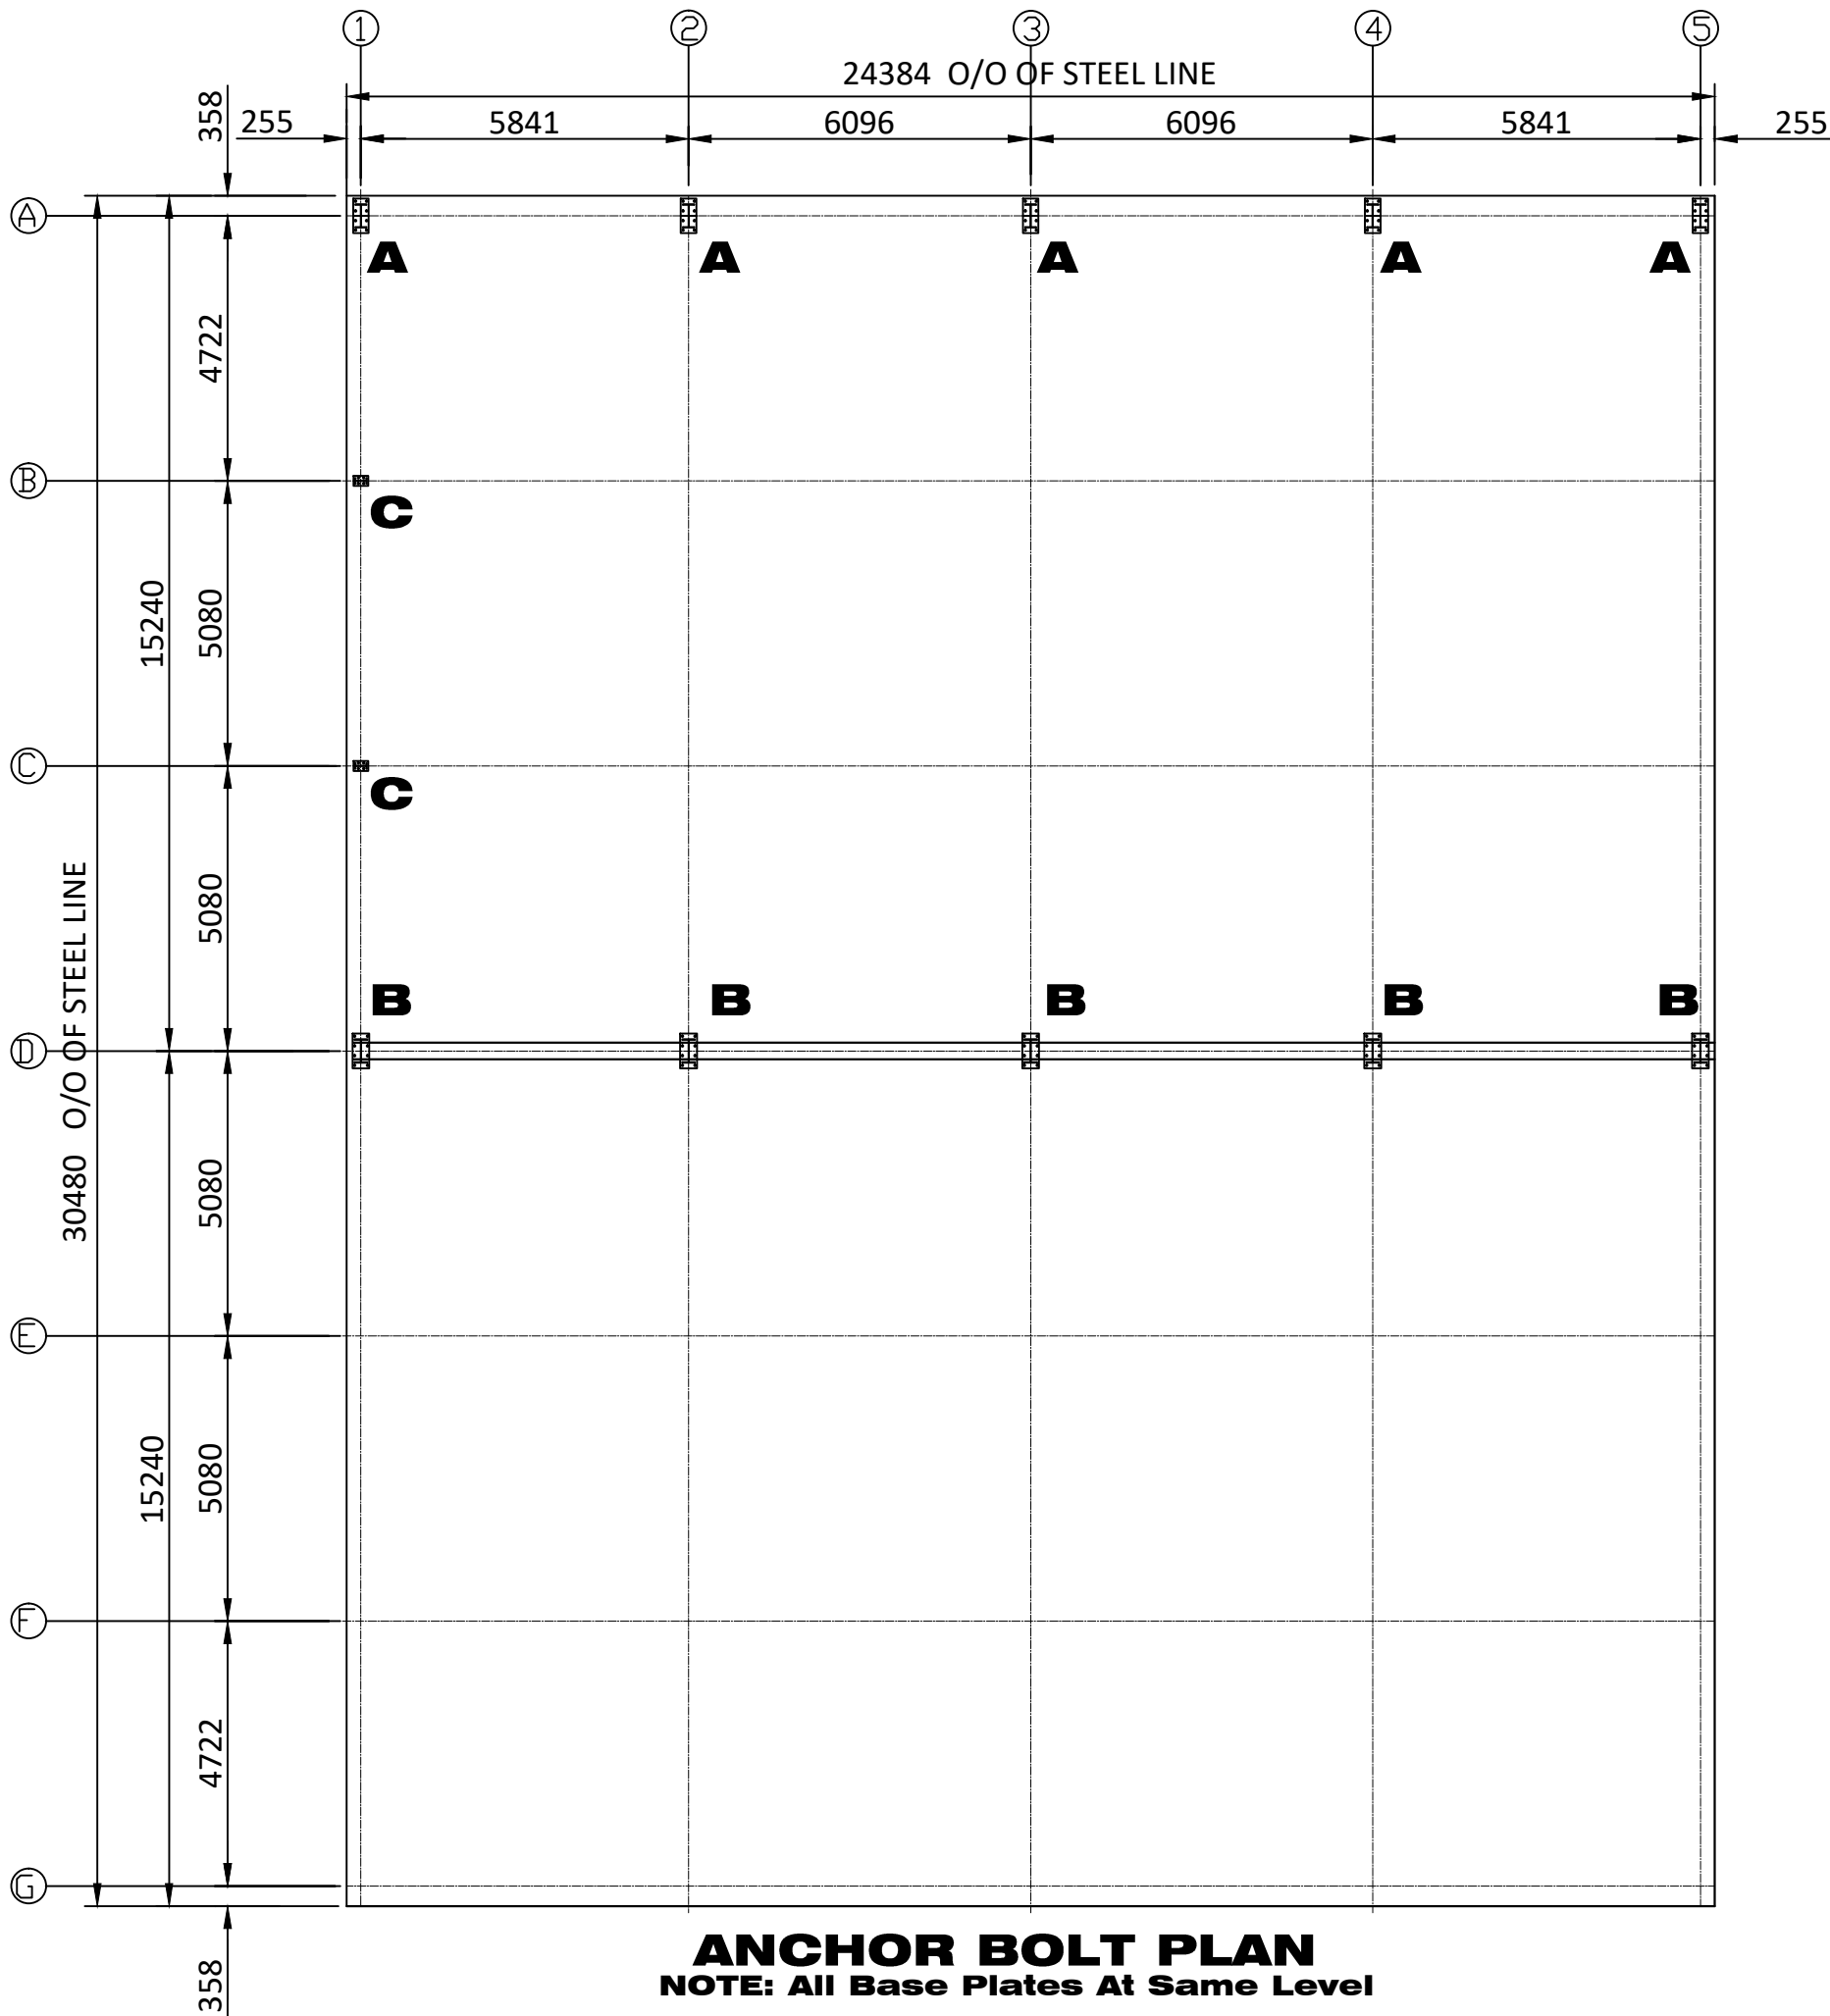


BASE PLATE DET: C

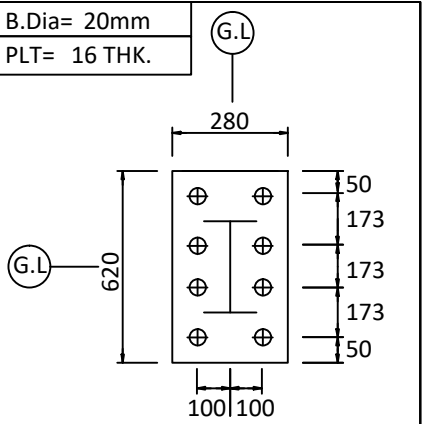

BASE PLATE DET: A

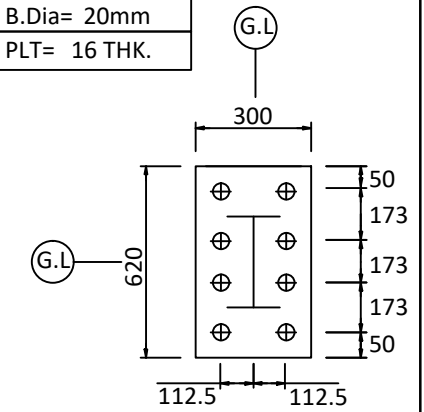


BASE PLATE DET: B

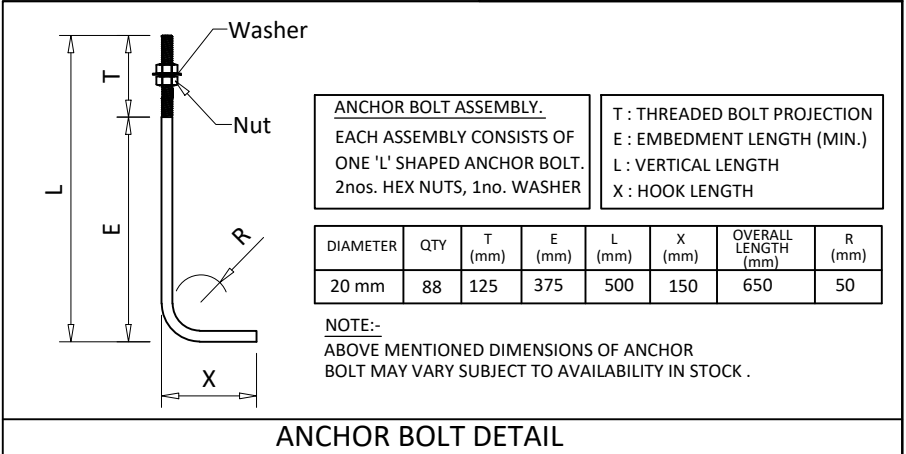

ANCHOR BOLT DETAIL

A	02-11-22	ISSUED FOR IFC	D.A	UBD	UBD
REV.	DATE	DESCRIPTION	DRWN BY	CHK BY	APR BY
MAIMAAR					
MAIMAAR STEEL Pvt.Ltd 105, Raiwind Road, Thokar Niaz Baig ,Lahore, Pakistan E-mail: nasir.abbas@maimaargroup.com E-mail: maimaar.steel@gmail.com Website: www.maimaargroup.com E-mail: nasir.abbas@maimaargroup.com Mob-1 : +(92-300) 807 4017 ,+(92-333) 807 1115					
JOB NO./QUOTE NO.		-		BLDG #.	01
PROJECT NAME		MAIMAAR FACTORY			
CUSTOMER					
JOBSITE LOCATION					
ANCHOR BOLT PLAN				DWG. NO.	
				01	

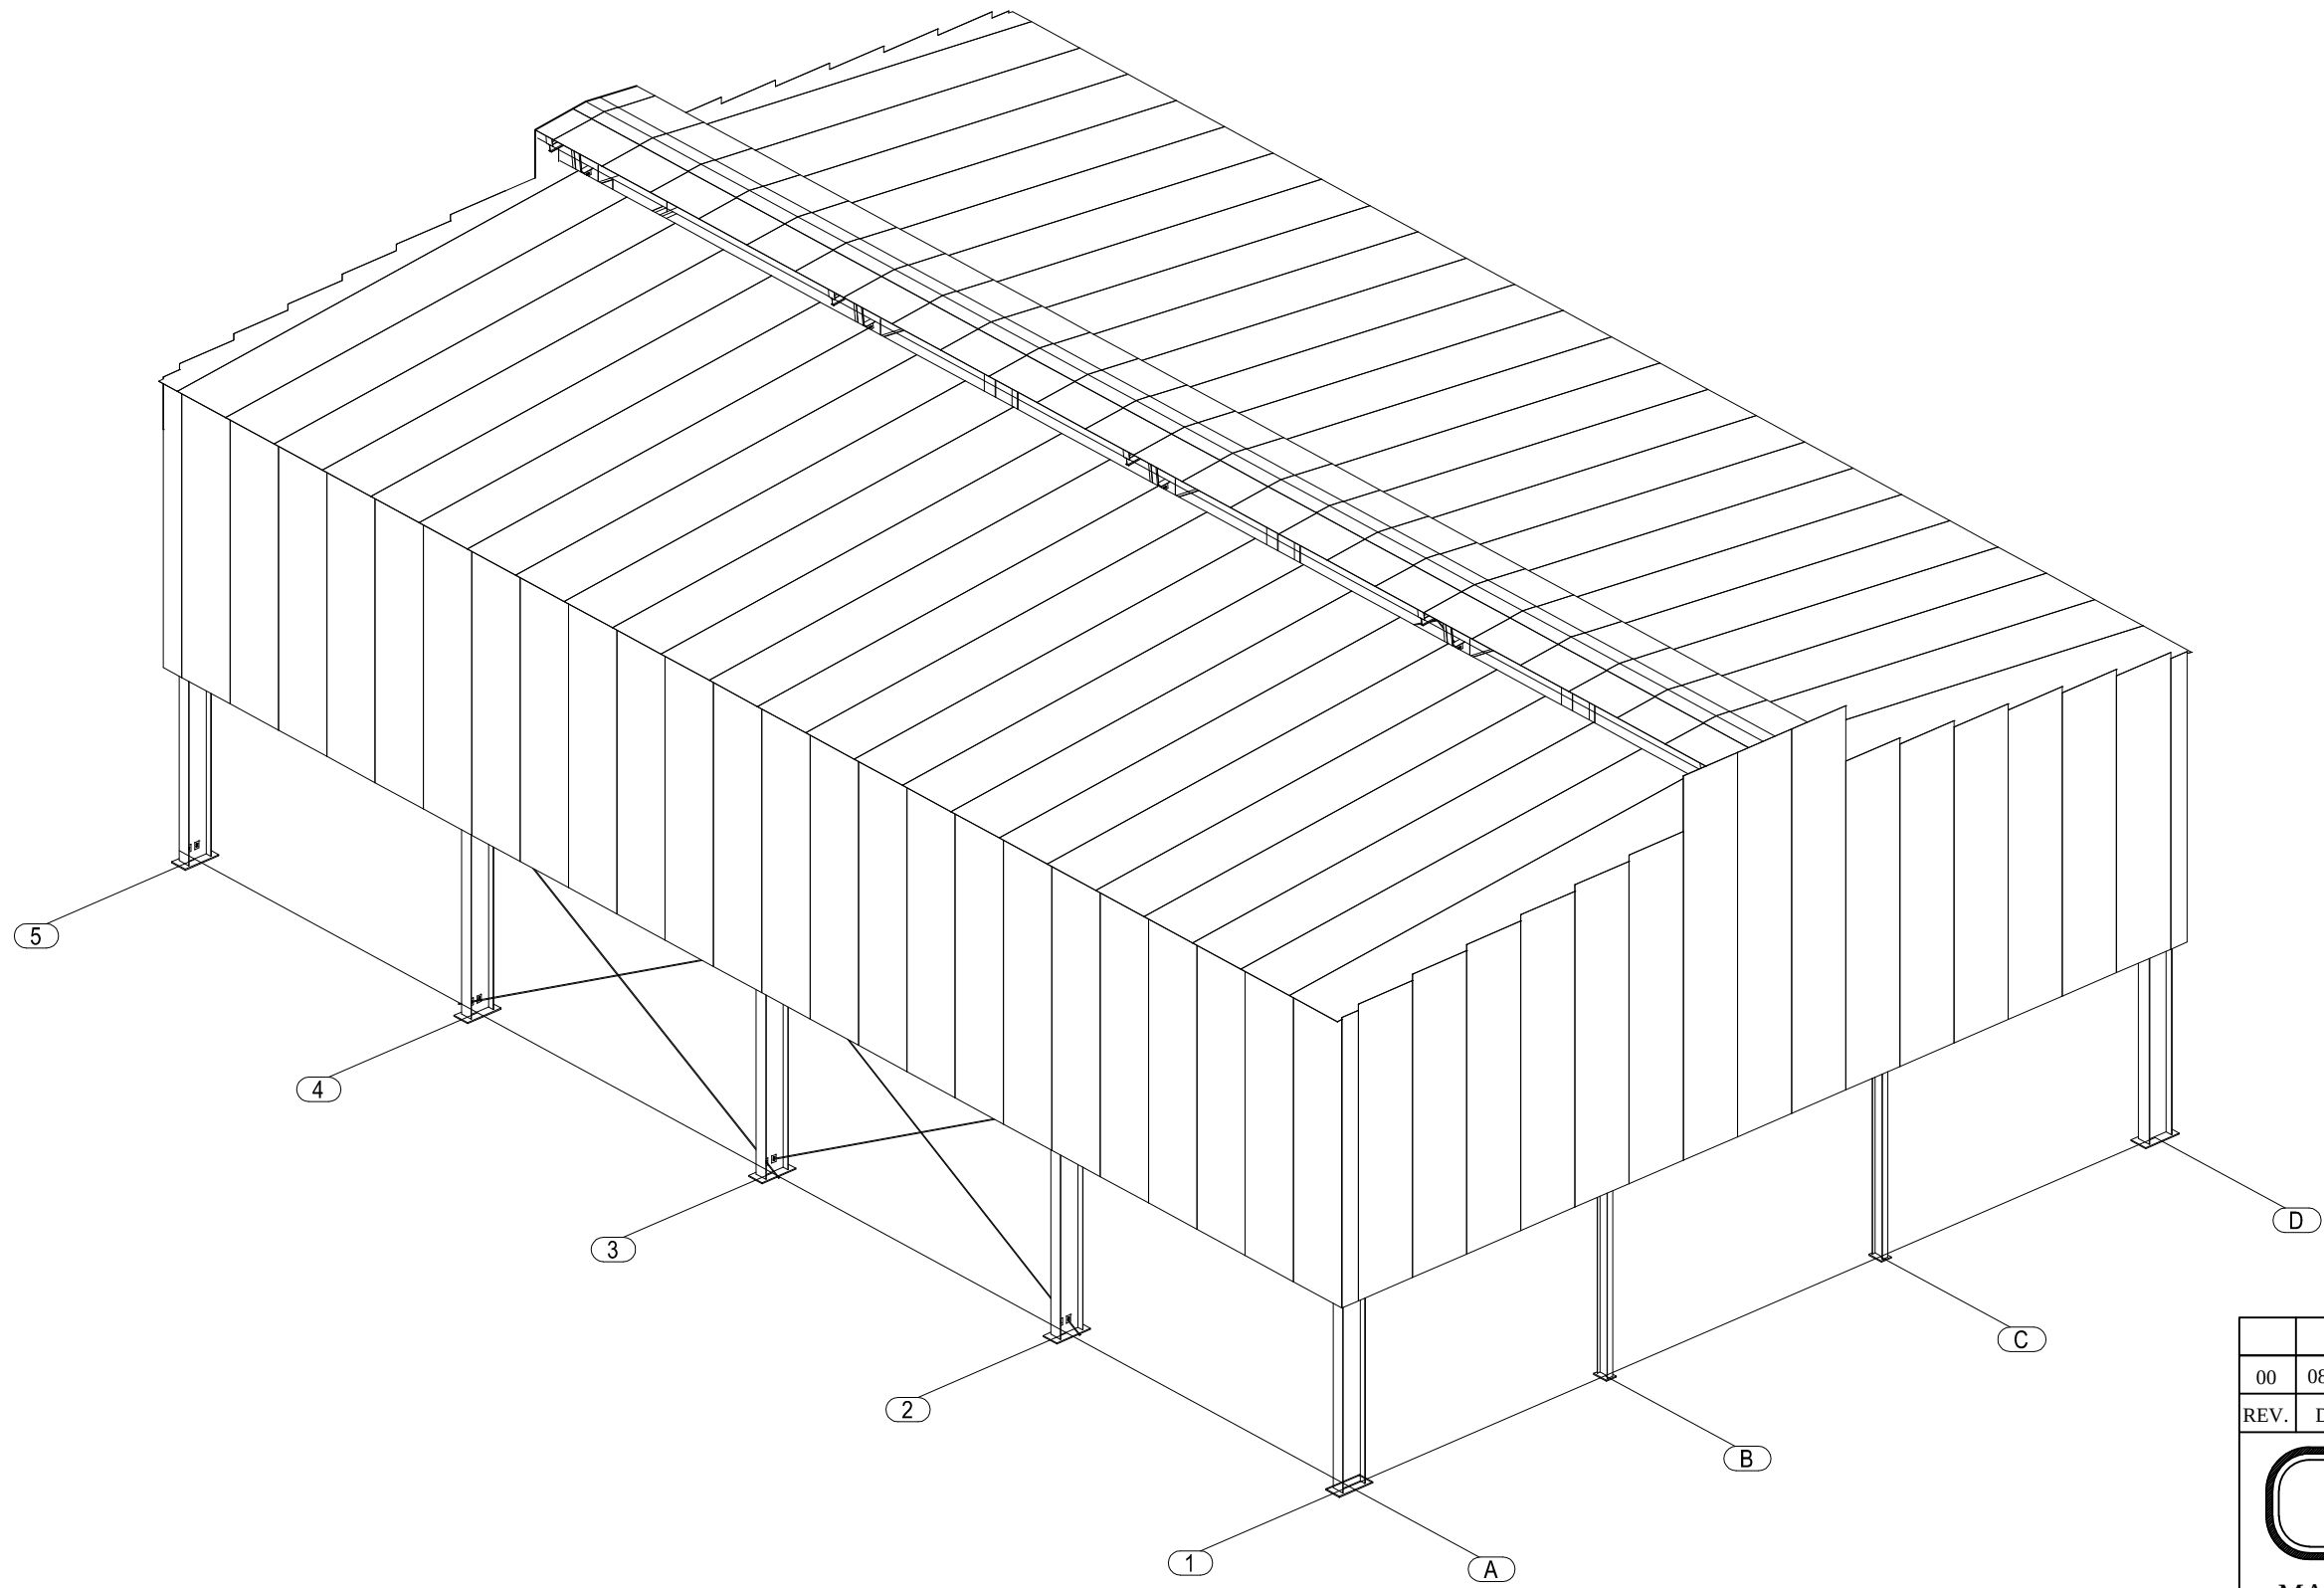


3D SHEETING

00	08-11-22	ISSUED FOR IFC	D.A	UBD	UBD
REV.	DATE	DESCRIPTION	DRWN BY	CHK BY	APR BY

MAIMAAR


MAIMAAR STEEL Pvt.Ltd
105, Raiwind Road, Thokar Niaz Baig ,Lahore, Pakistan
E-mail: nasir.abbas@maimaargroup.com
E-mail: maimaar.steel@gmail.com
Website: www.maimaargroup.com
E-mail: nasir.abbas@maimaargroup.com
Mob-1 : +(92-300) 807 4017 ,+(92-333) 807 1115

JOB NO./QUOTE NO.	-	BLDG #.	01
PROJECT NAME	MAIMAAR FACTORY		
CUSTOMER			
JOB SITE LOCATION			
3D SHEETING		DWG. NO.	01

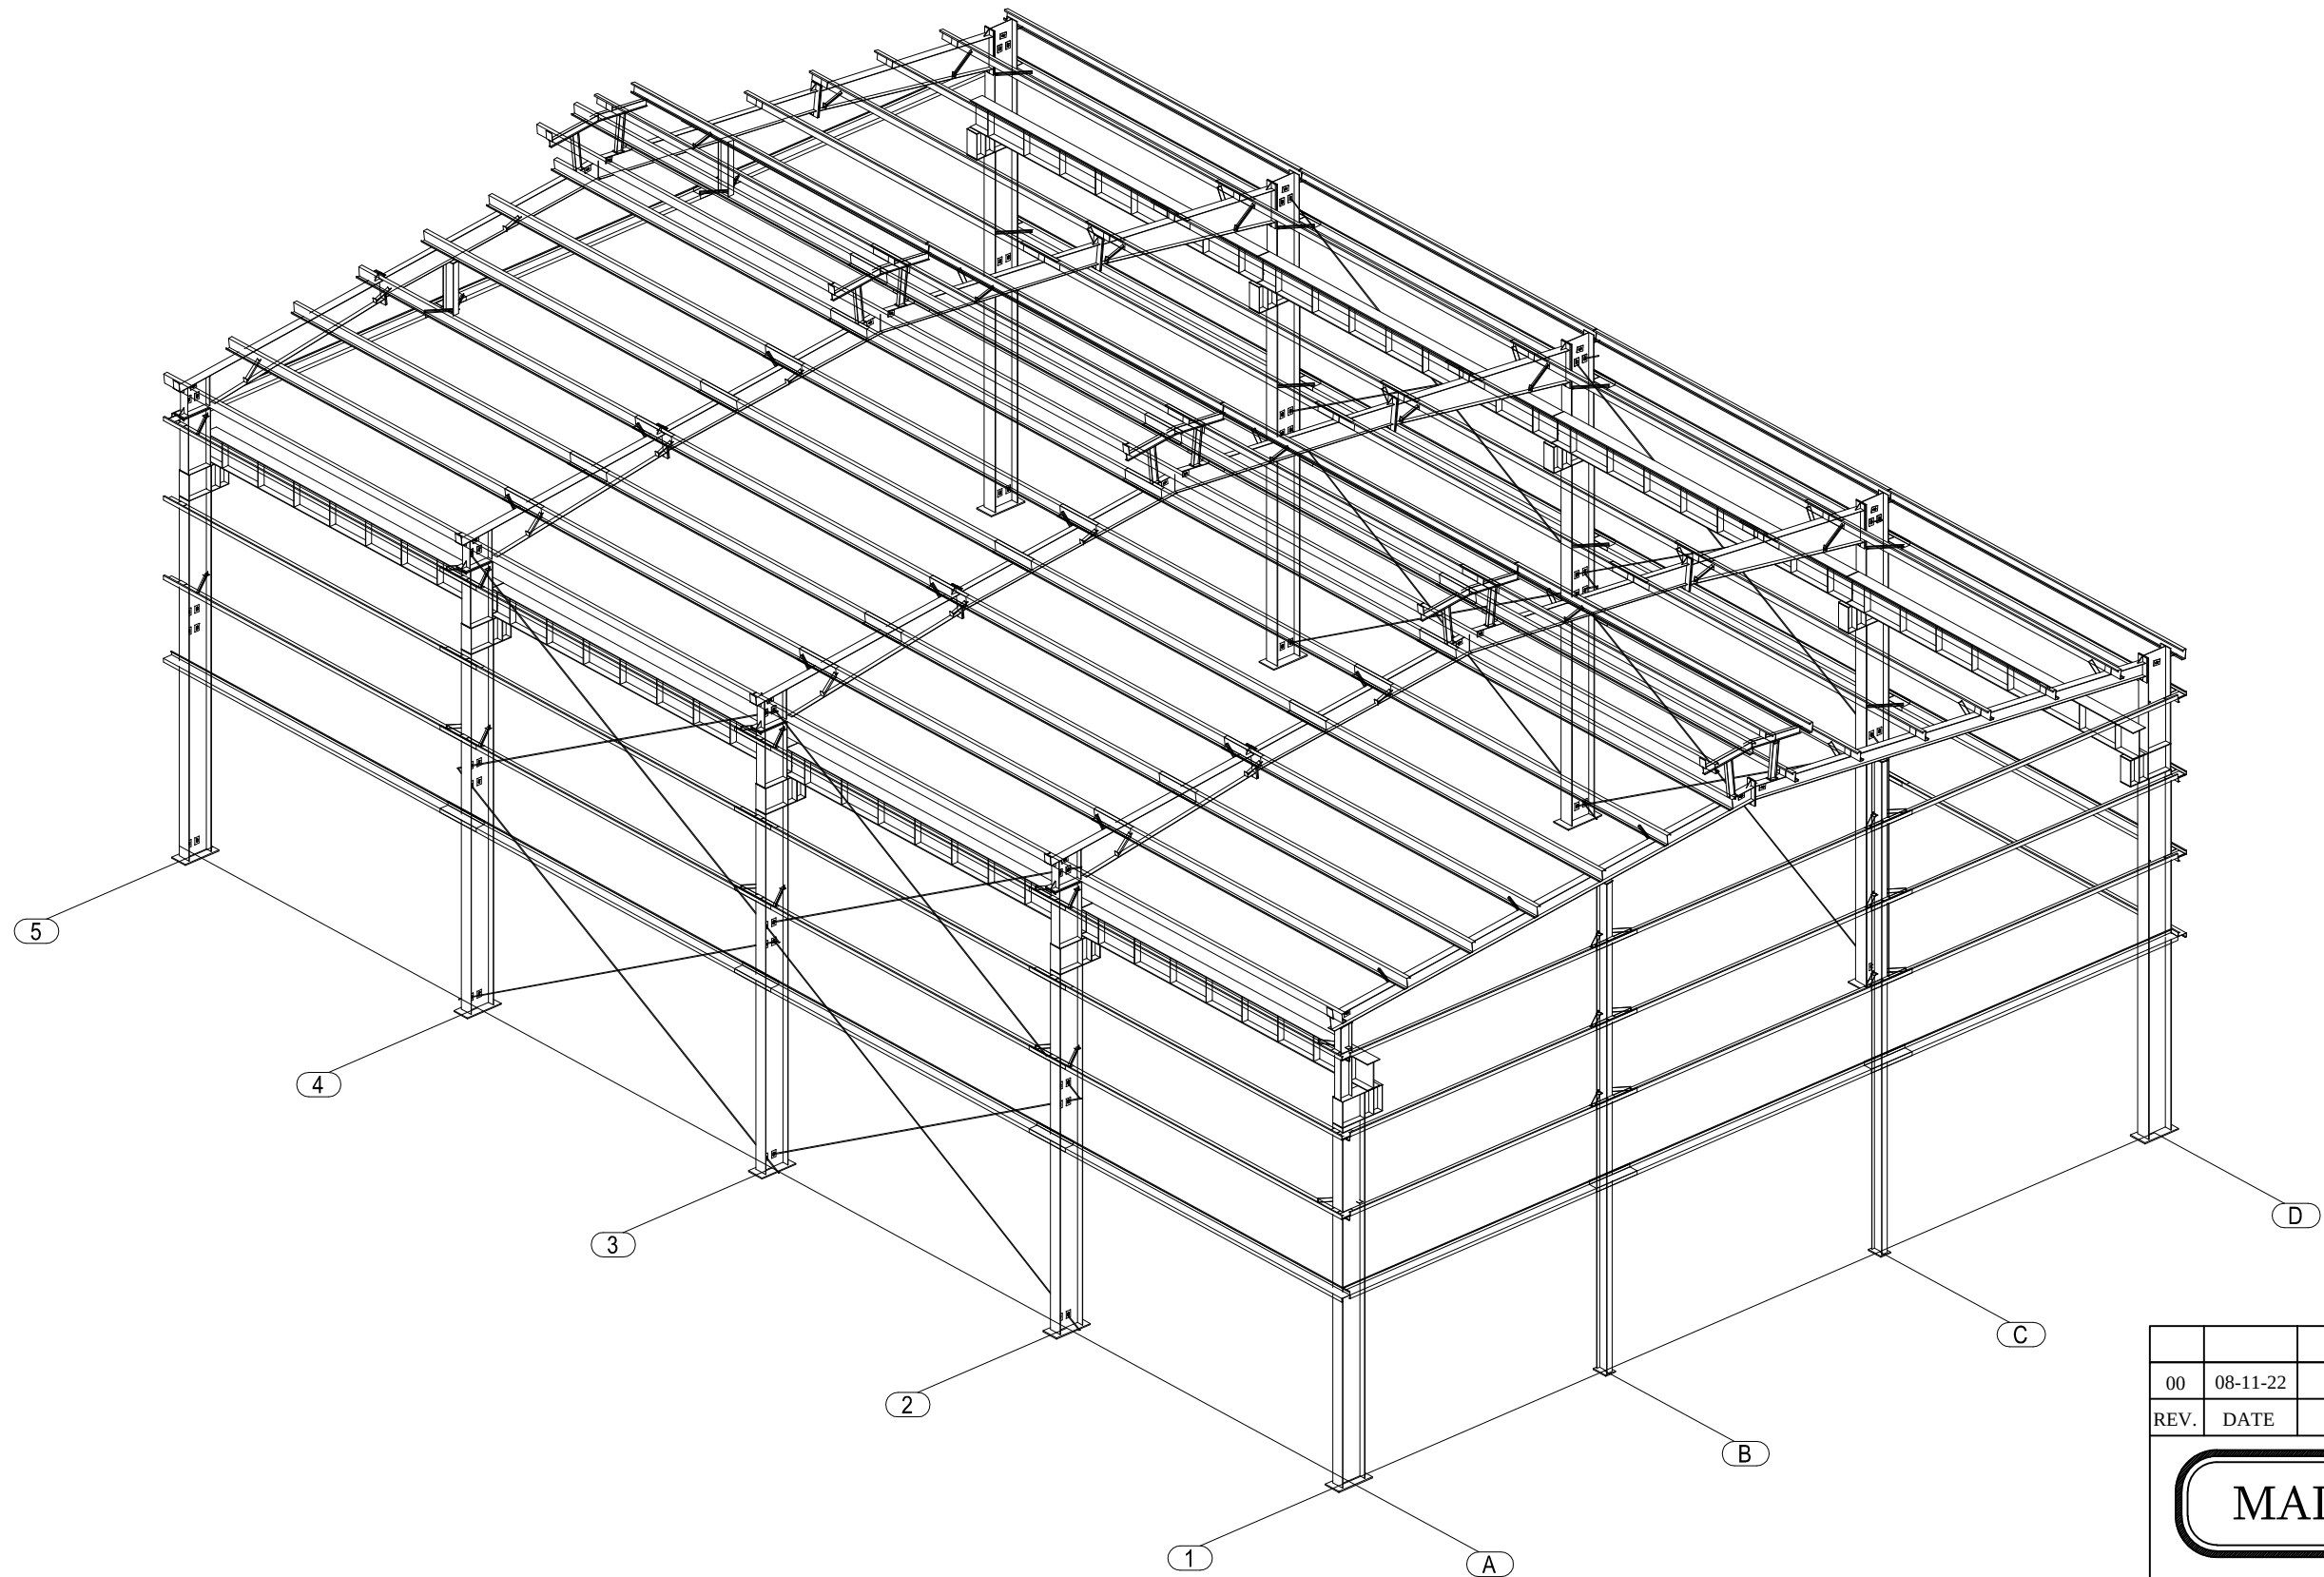


3D PLAN

00	08-11-22	ISSUED FOR IFC	D.A	UBD	UBD
REV.	DATE	DESCRIPTION	DRWN BY	CHK BY	APR BY
MAIMAAR					
MAIMAAR STEEL Pvt.Ltd 105, Raiwind Road, Thokar Niaz Baig ,Lahore, Pakistan E-mail: nasir.abbas@maimaargroup.com E-mail: maimaar.steel@gmail.com Website: www.maimaargroup.com E-mail: nasir.abbas@maimaargroup.com Mob-1 : +(92-300) 807 4017 ,+(92-333) 807 1115					
JOB NO./QUOTE NO.			-	BLDG #.	01
PROJECT NAME			MAIMAAR FACTORY		
CUSTOMER					
JOBSITE LOCATION					
3D PLAN				DWG. NO.	
				01	

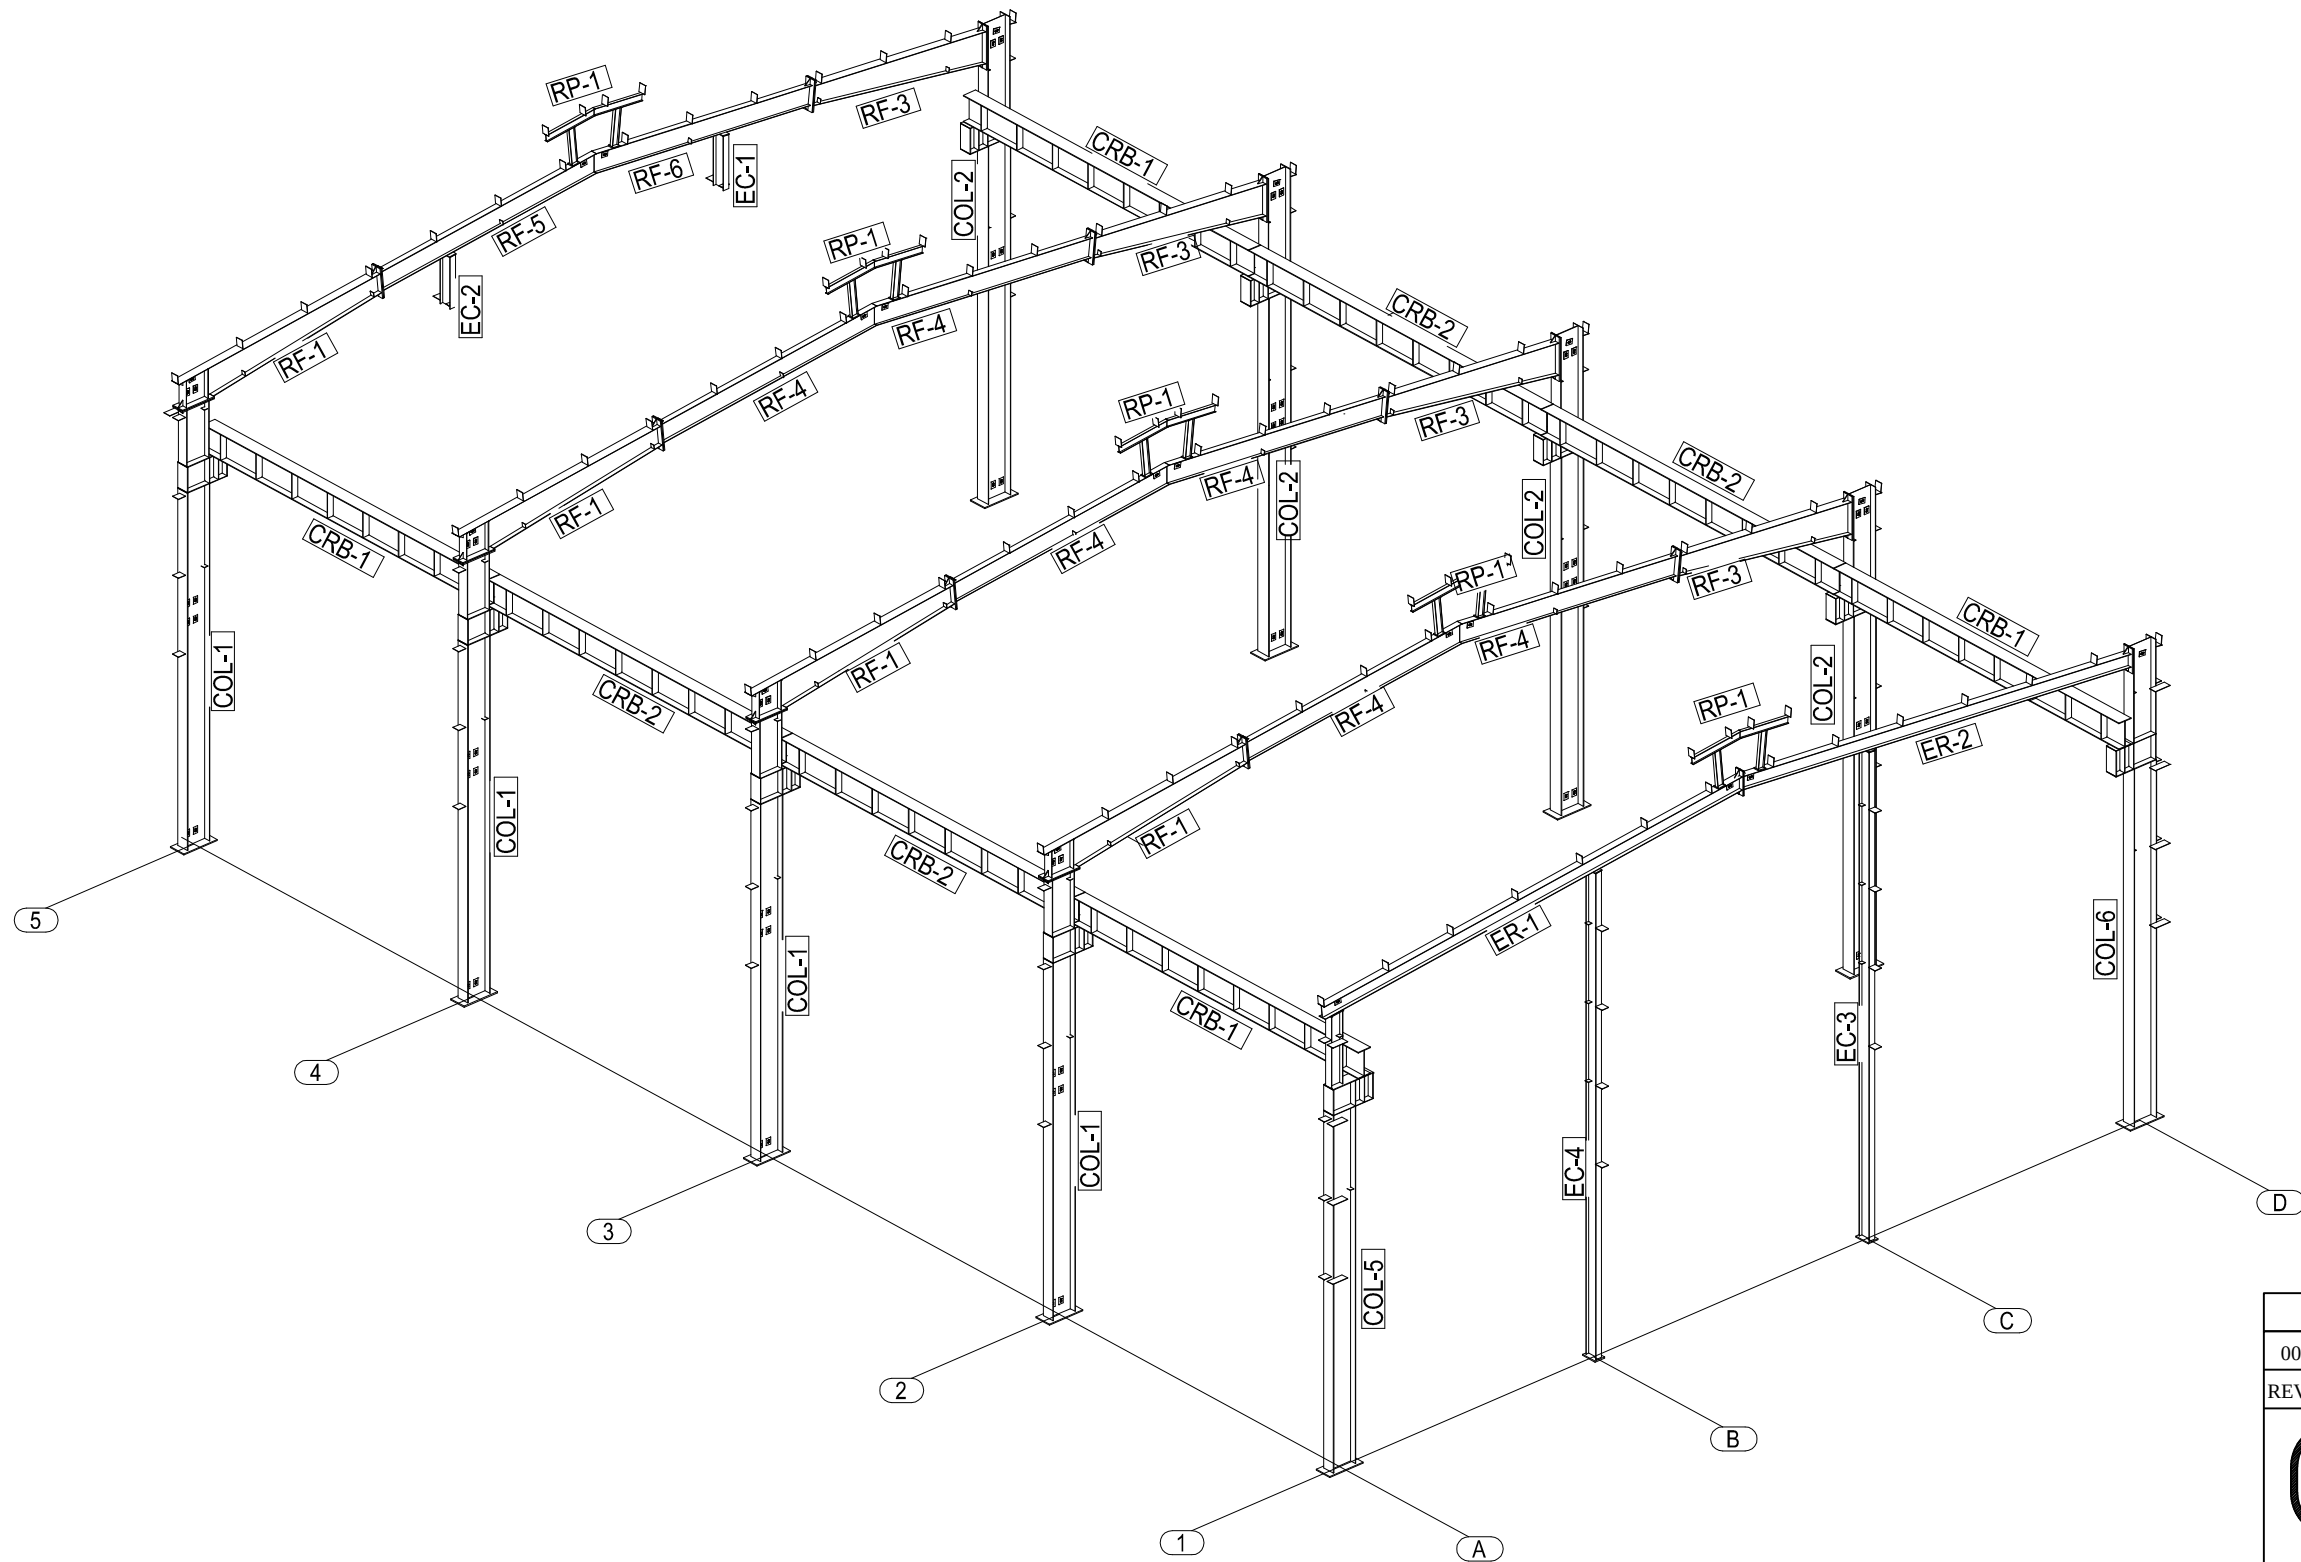

3D COLUMN AND RAFTER

00	08-11-22	ISSUED FOR IFC	D.A	UBD	UBD
REV.	DATE	DESCRIPTION	DRWN BY	CHK BY	APR BY
MAIMAAR MAIMAAR STEEL Pvt.Ltd 105, Raiwind Road, Thokar Niaz Baig ,Lahore, Pakistan E-mail: nasir.abbas@maimaargroup.com E-mail: maimaar.steel@gmail.com Website: www.maimaargroup.com E-mail: nasir.abbas@maimaargroup.com Mob-1 : +(92-300) 807 4017 ,+(92-333) 807 1115					
JOB NO./QUOTE NO.			BLDG #. 01		
PROJECT NAME			MAIMAAR FACTORY		
CUSTOMER					
JOBSITE LOCATION					
3D COLUMN AND RAFTER					DWG. NO.
					01

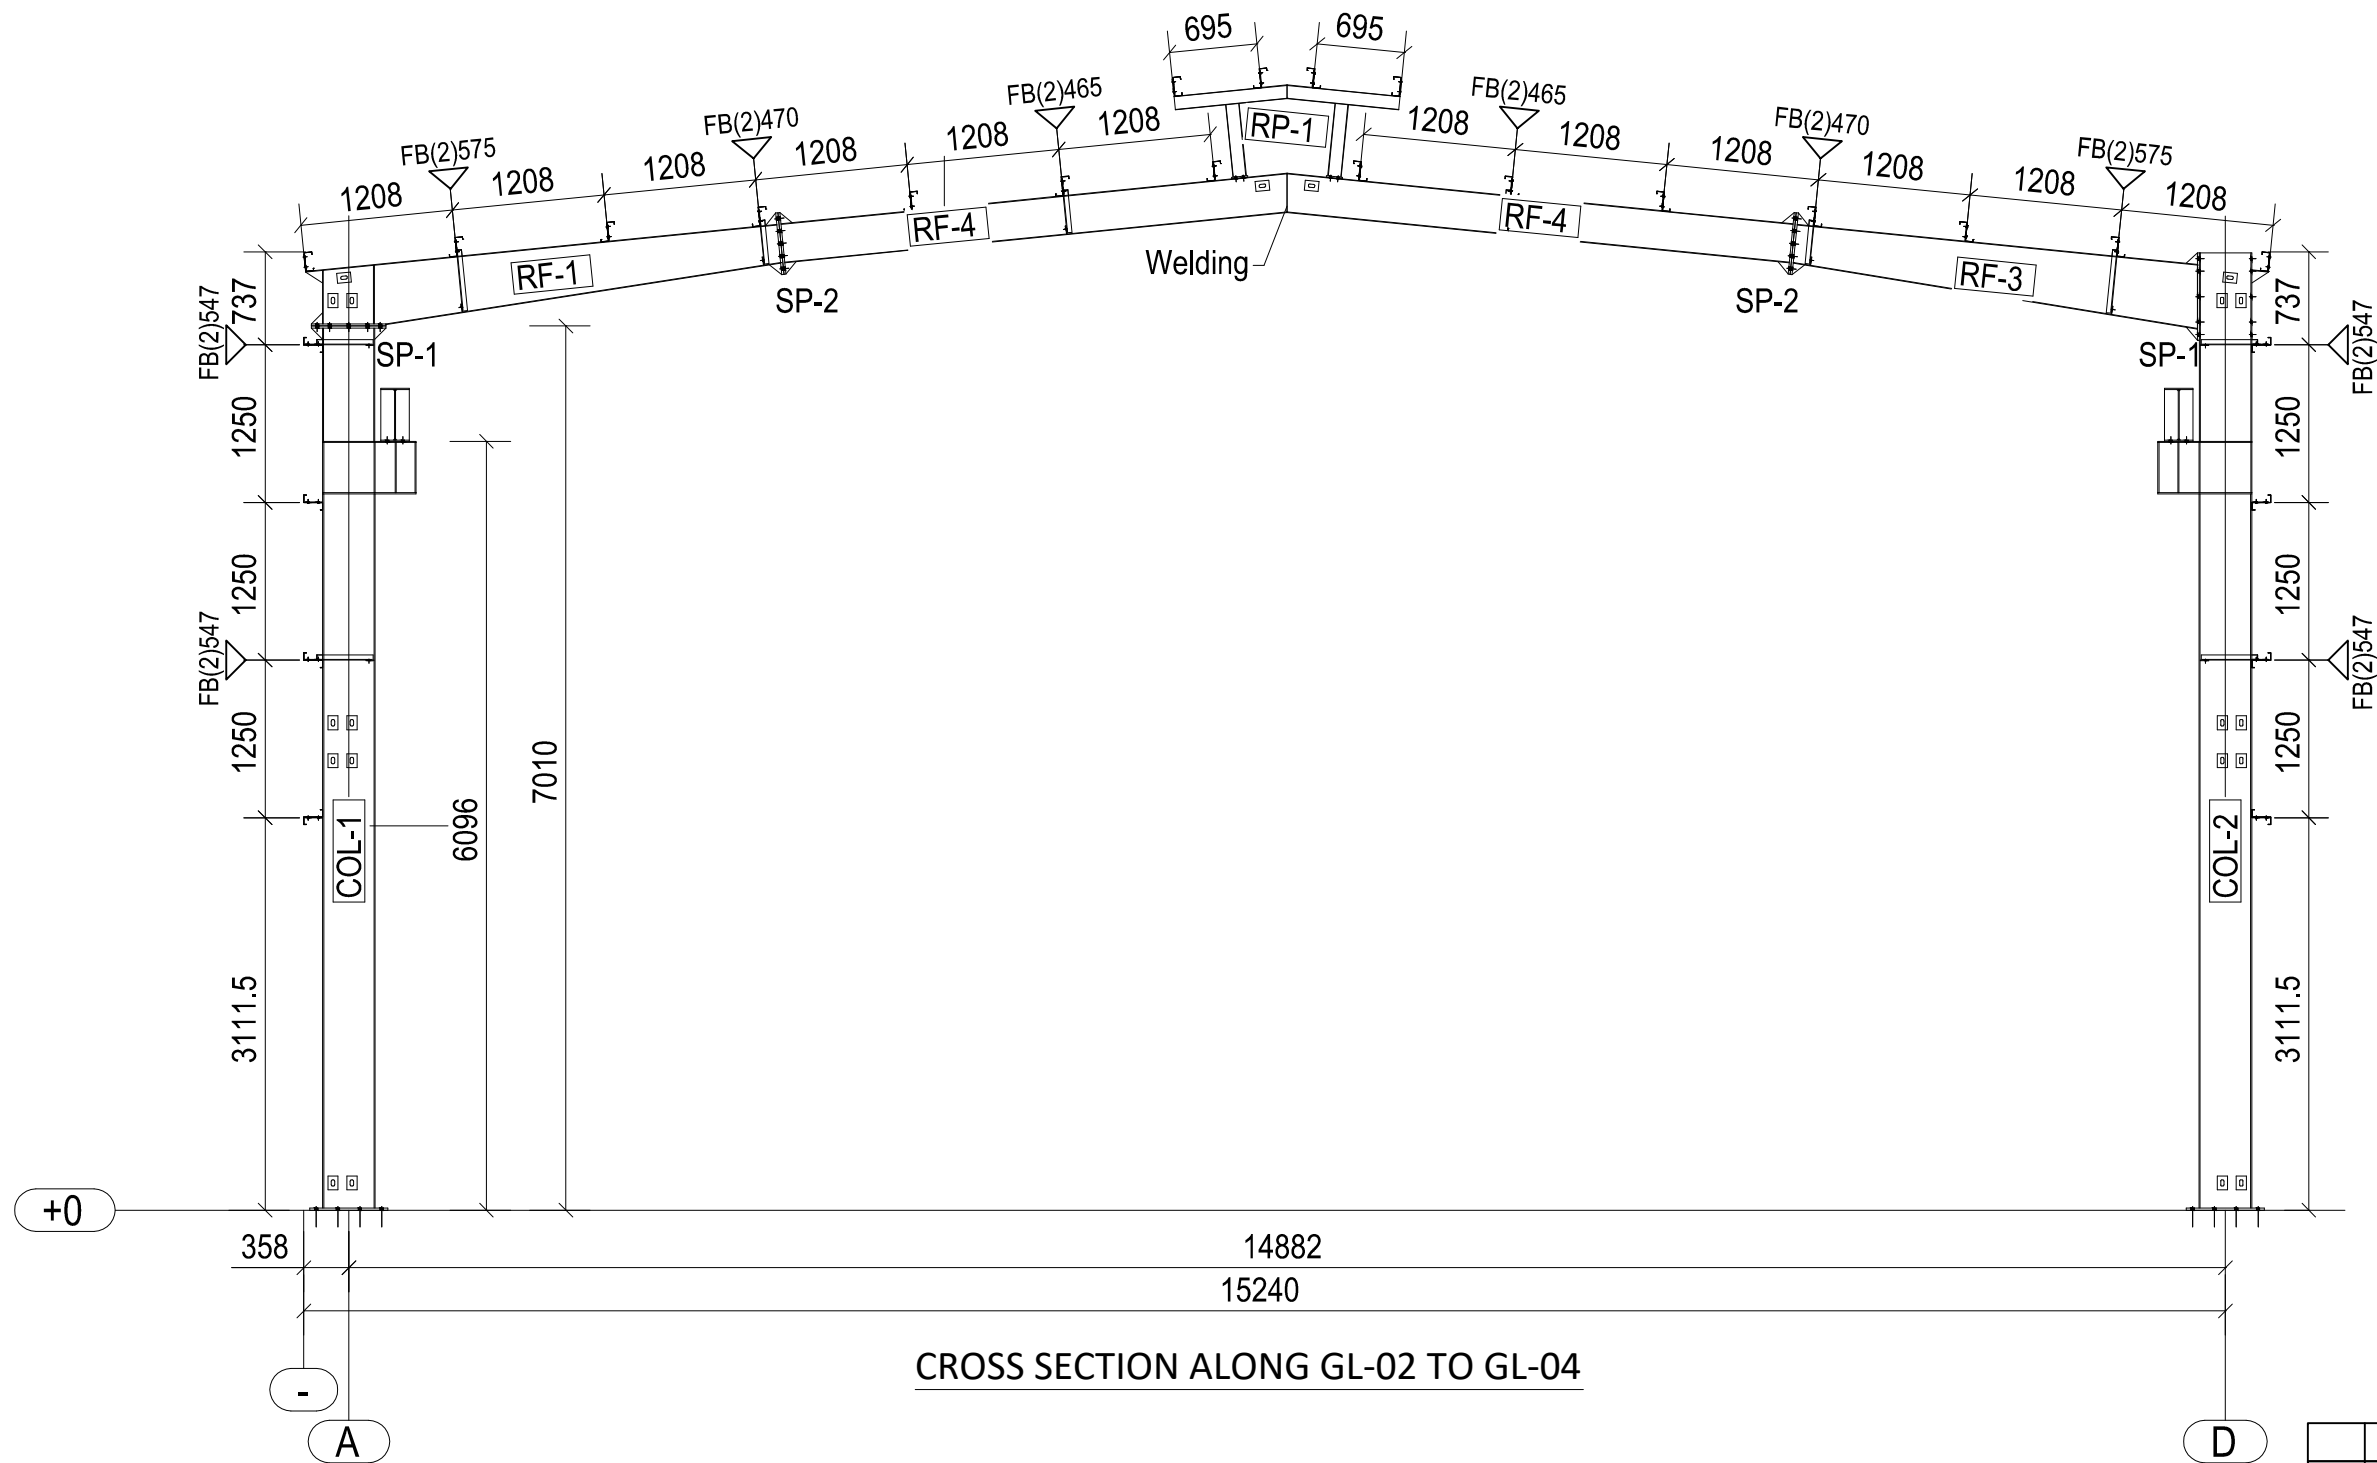

CROSS SECTION ALONG GL-02 TO GL-04


00	08-11-22	ISSUED FOR IFC	D.A	UBD	UBD
REV.	DATE	DESCRIPTION	DRWN BY	CHK BY	APR BY


MAIMAAR




MAIMAAR STEEL Pvt.Ltd
105, Raiwind Road, Thokar Niaz Baig ,Lahore, Pakistan
E-mail: nasir.abbas@maimaargroup.com
E-mail: maimaar.steel@gmail.com
Website: www.maimaargroup.com
E-mail: nasir.abbas@maimaargroup.com
Mob-1 : +(92-300) 807 4017 ,+(92-333) 807 1115

JOB NO./QUOTE NO.	-	BLDG #.	01
PROJECT NAME	MAIMAAR FACTORY		
CUSTOMER			
JOB SITE LOCATION			
CROSS SECTION ALONG GL-02 TO GL-04			DWG. NO. 01

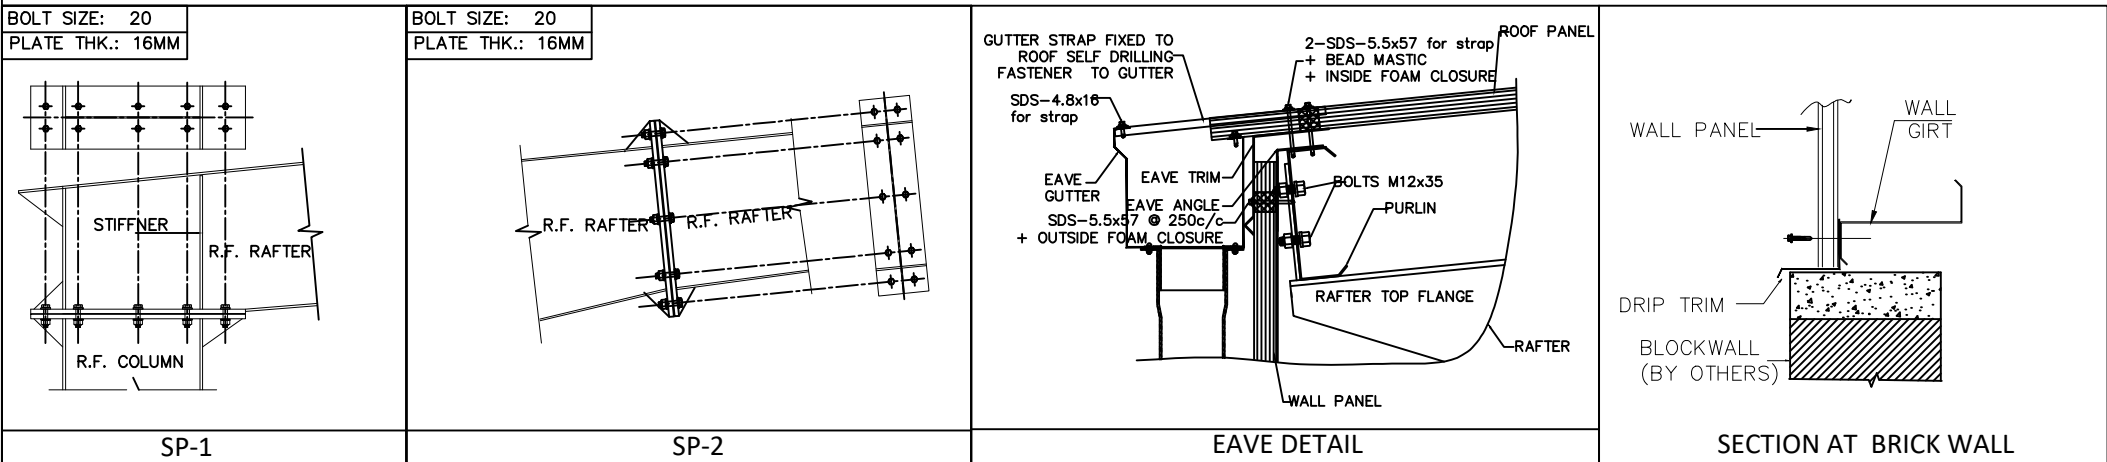

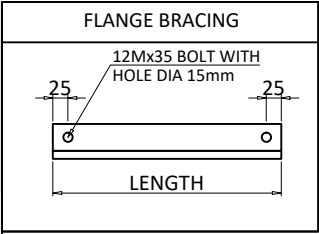


▽ FLANGE BRACES: Both Sides(U.N.)
FBxxE(1): xx=length(mm)
E - L40x4

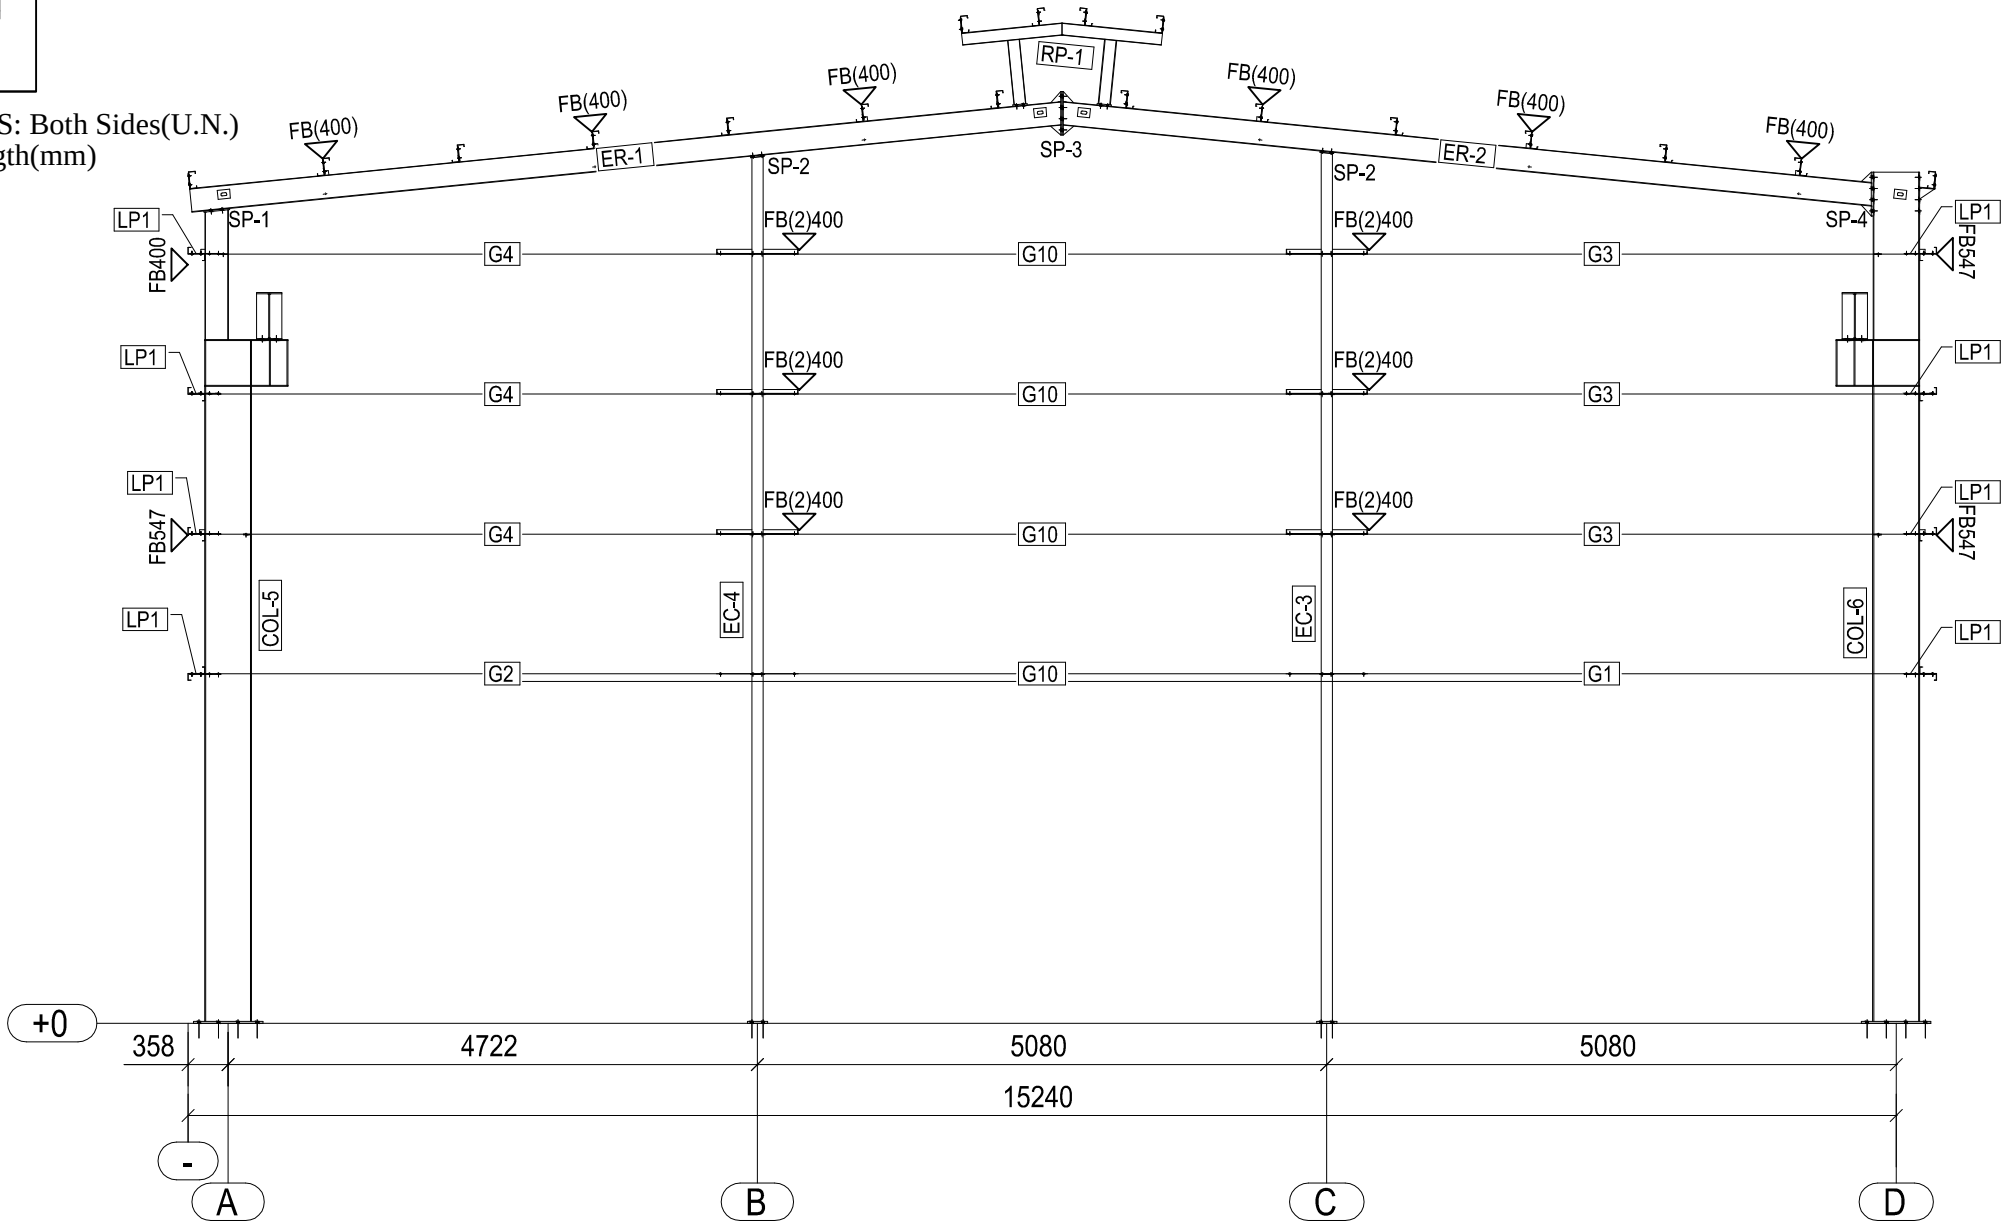


ENDWALL ELEVATION ALONG GL-1


BOLT SIZE: 20
PLATE THK.: 16MM

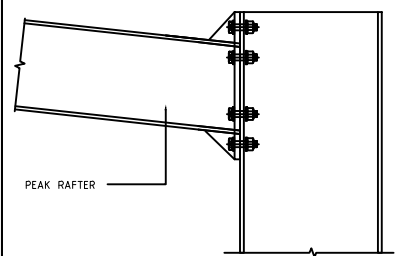


SP-4

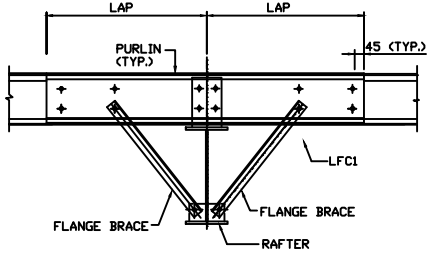

FLANGE BRACE DETAIL

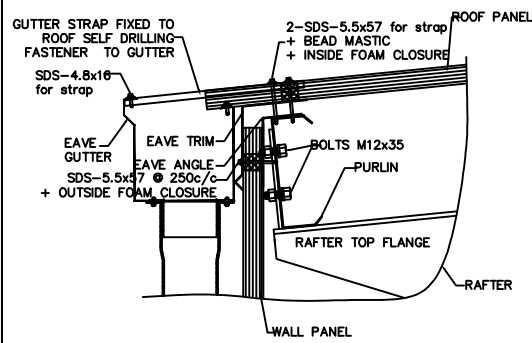


EAVE DETAIL

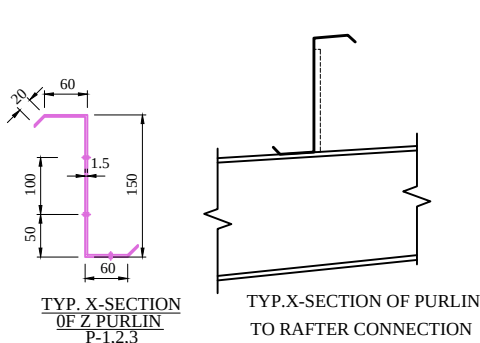


PURLIN DETAILS

BOLT SIZE: 16
PLATE THK.: 12MM

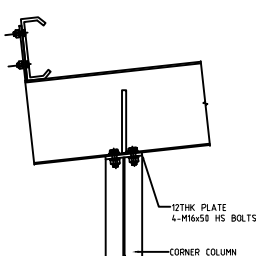


SP-1

BOLT SIZE: 16
PLATE THK.: 12MM

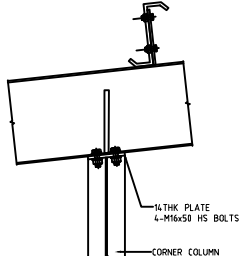

SP-2

BOLT SIZE: 20
PLATE THK.: 12MM

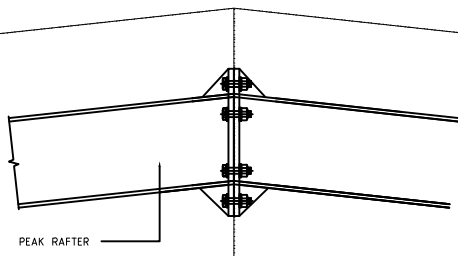


SP-3

00	08-11-22	ISSUED FOR IFC	D.A	UBD	UBD
REV.	DATE	DESCRIPTION	DRWN BY	CHK BY	APR BY



MAIMAAR STEEL Pvt.Ltd
105, Raiwind Road, Thokar Niaz Baig ,Lahore, Pakistan
E-mail: nasir.abbas@maimaargroup.com
E-mail: maimaar.steel@gmail.com
Website: www.maimaargroup.com
E-mail: nasir.abbas@maimaargroup.com
Mob-1 : +(92-300) 807 4017 ,+(92-333) 807 1115

JOB NO./QUOTE NO.	-	BLDG #.	01
PROJECT NAME	MAIMAAR FACTORY		
CUSTOMER			
JOB SITE LOCATION			
ENDWALL ELEVATION ALONG GL-1			DWG. NO. 01

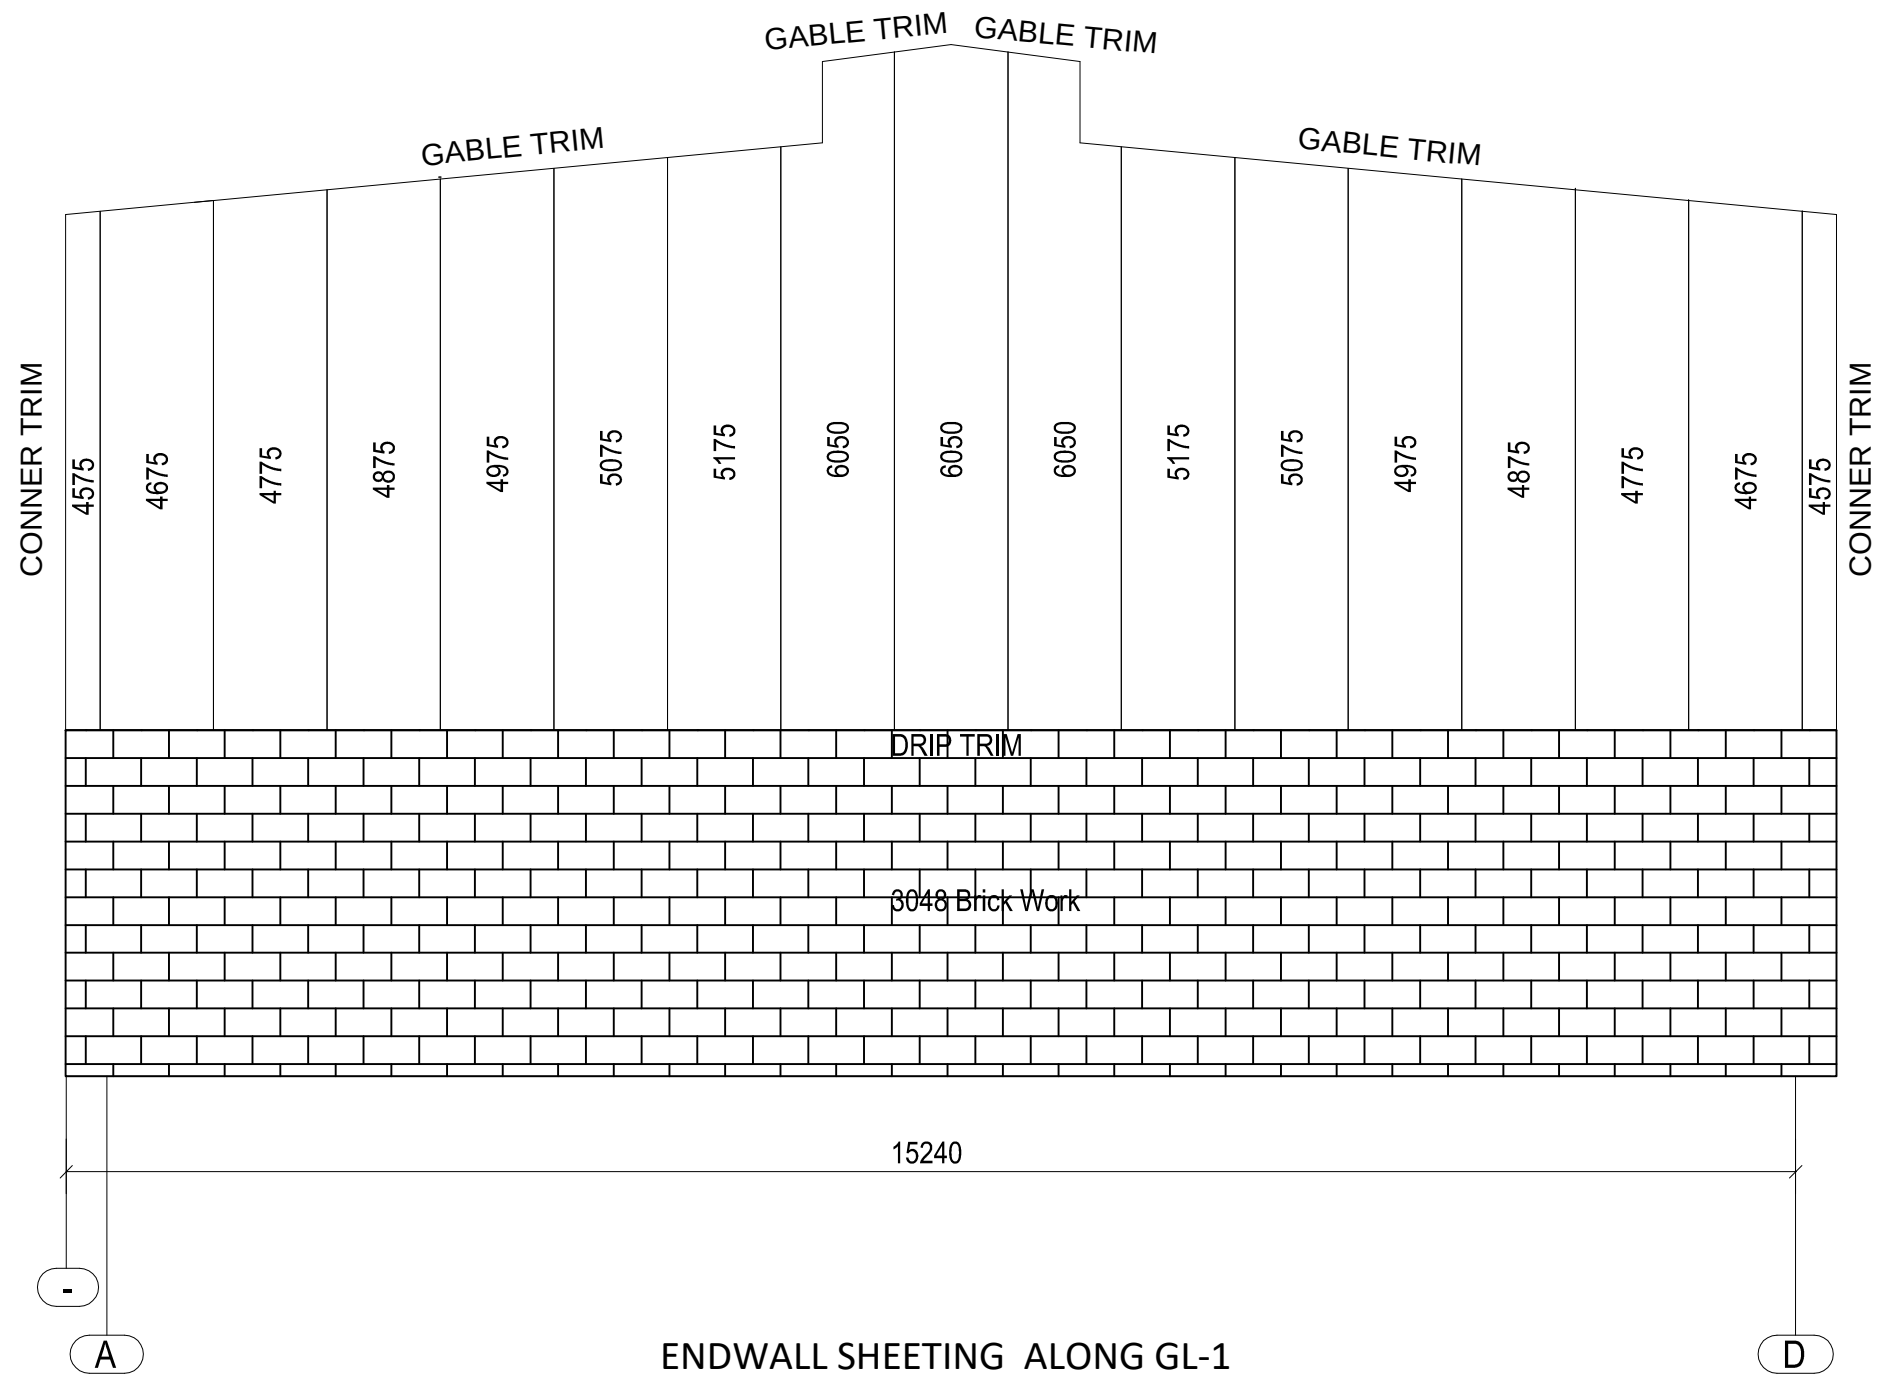

ENDWALL SHEETING ALONG GL-1


00	08-11-22	ISSUED FOR IFC	D.A	UBD	UBD
REV.	DATE	DESCRIPTION	DRWN BY	CHK BY	APR BY

MAIMAAR




MAIMAAR STEEL Pvt.Ltd
105, Raiwind Road, Thokar Niaz Baig ,Lahore, Pakistan
E-mail: nasir.abbas@maimaargroup.com
E-mail: maimaar.steel@gmail.com
Website: www.maimaargroup.com
E-mail: nasir.abbas@maimaargroup.com
Mob-1 : +(92-300) 807 4017 ,+(92-333) 807 1115


JOB NO./QUOTE NO.	-	BLDG #.	01
PROJECT NAME	MAIMAAR FACTORY		
CUSTOMER			
JOB SITE LOCATION			
ENDWALL SHEETING ALONG GL-1			DWG. NO. 01

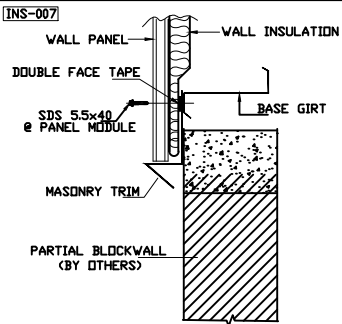


SECTION AT PARTIAL BLOCKWALL

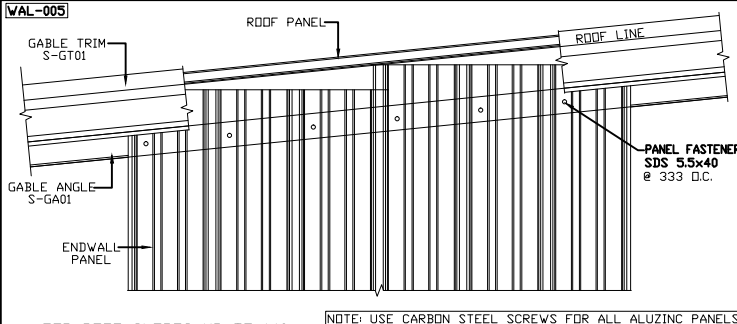


TYPICAL ENDWALL PANEL FIXING DETAIL

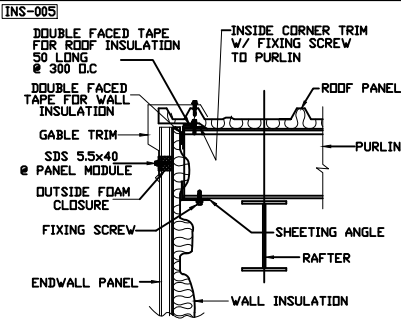


GABLE DETAIL WITH INSULATION

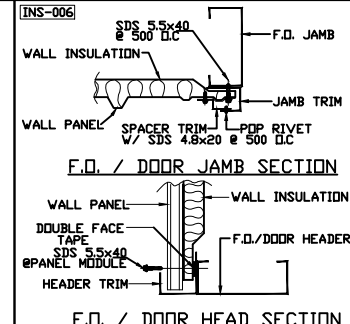


SECTION AT F.O./DOOR HEAD & JAMB

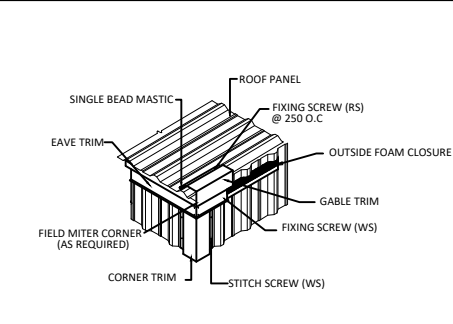

GABLE TRIM WITH EAVE TRIM DETAIL

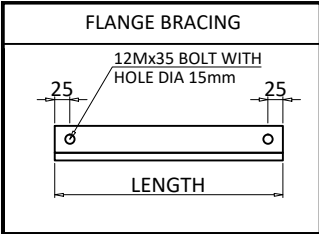


▽ FLANGE BRACES: Both Sides(U.N.)
FBxxE(1): xx=length(mm)
E - L40x4

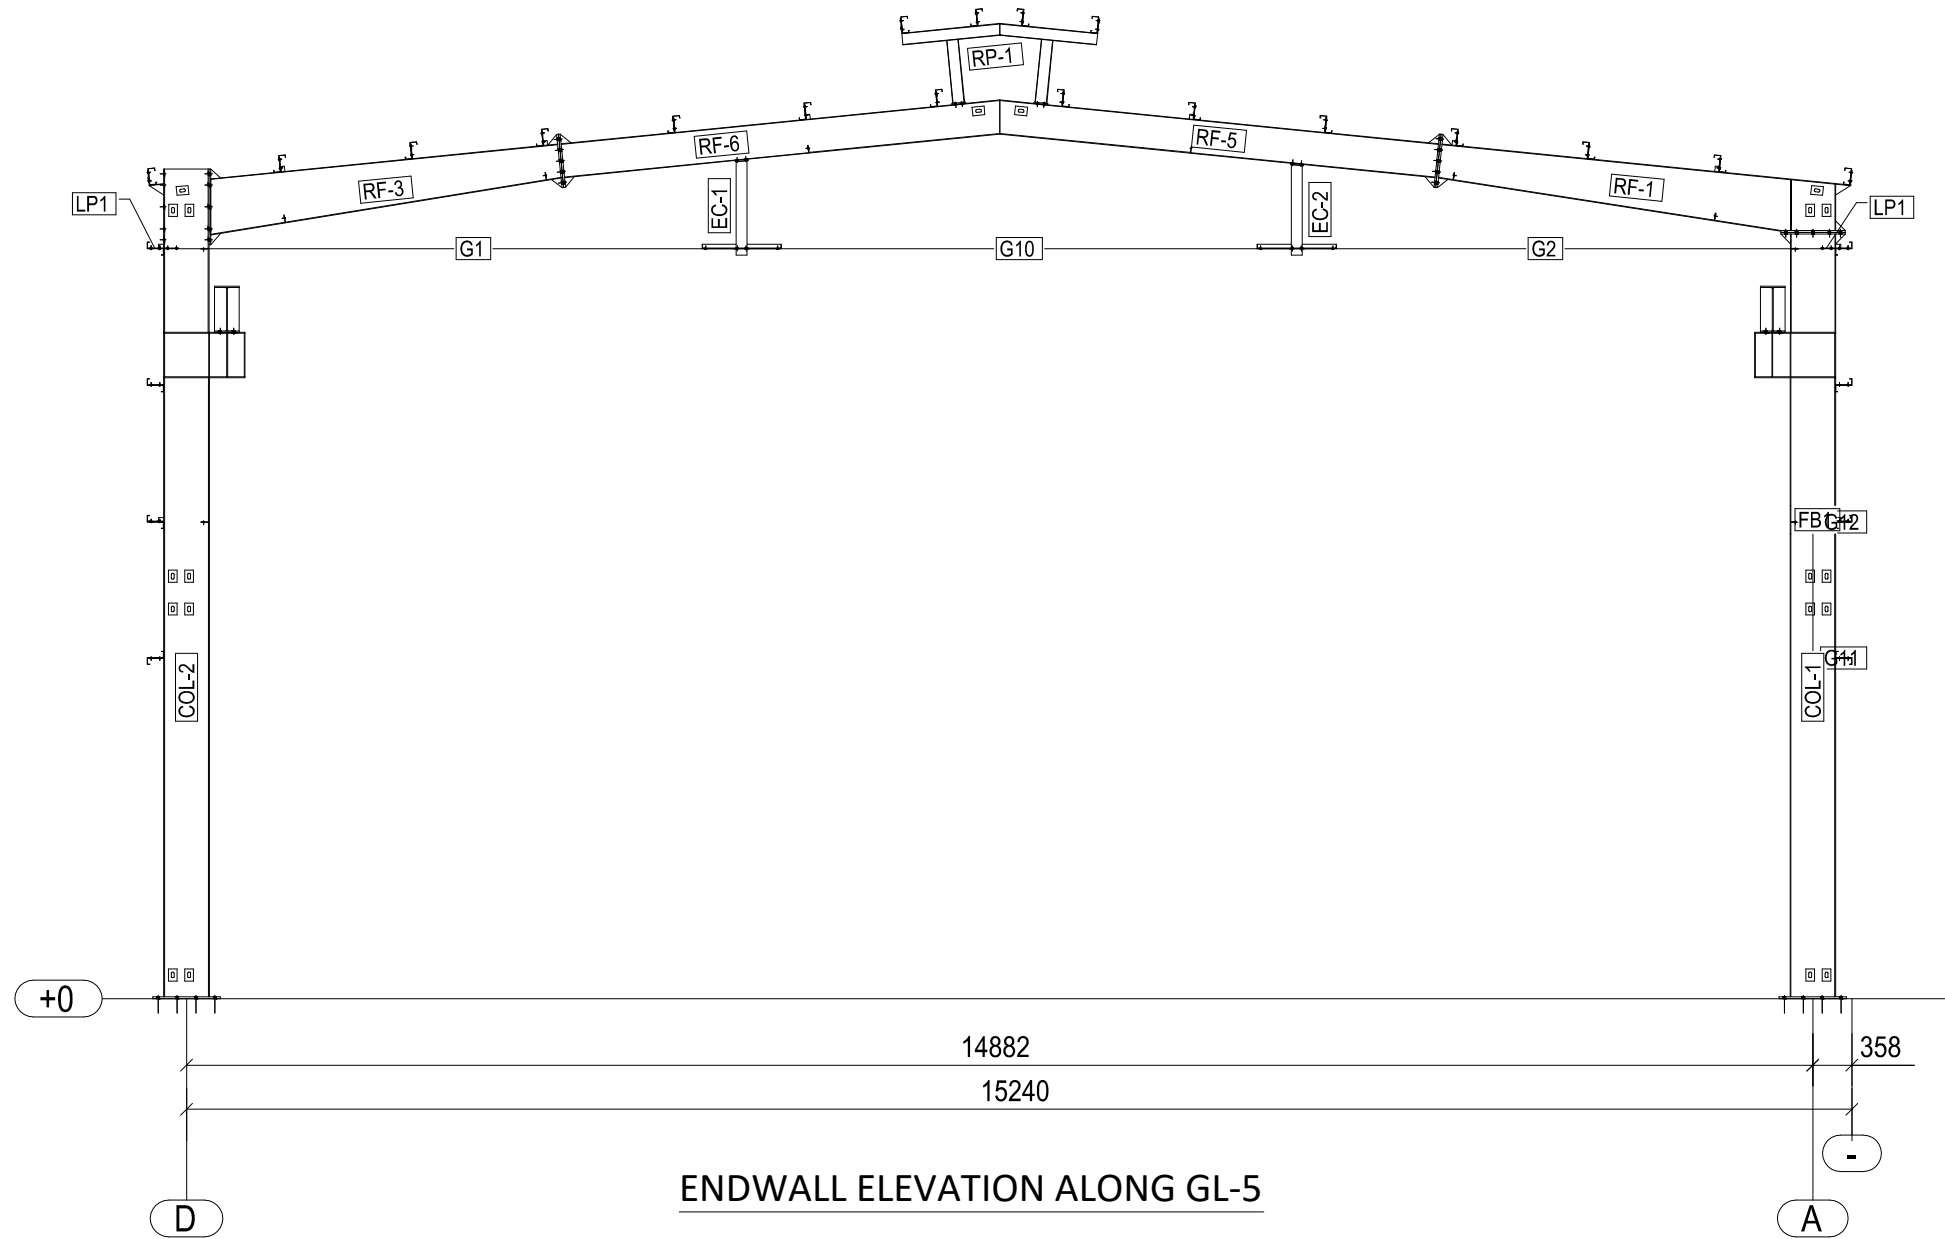


ENDWALL ELEVATION ALONG GL-5


BOLT SIZE: 20
PLATE THK.: 16MM

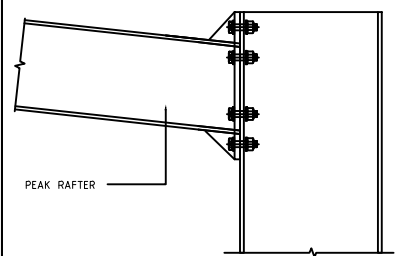


SP-4

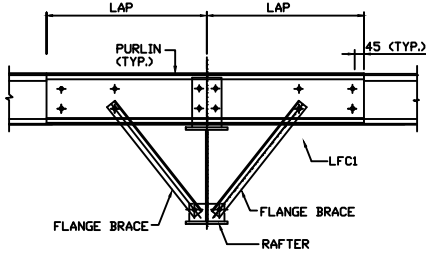


FLANGE BRACE DETAIL

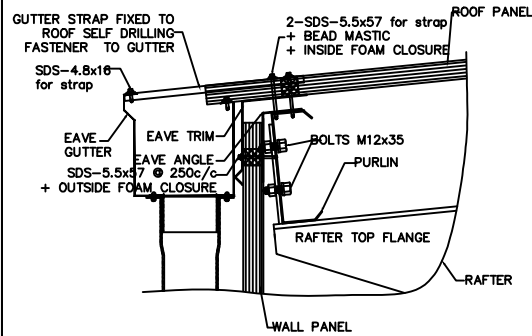

EAVE DETAIL

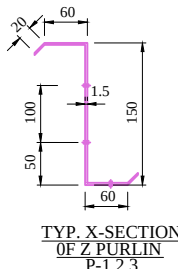


TYP. X-SECTION
OF Z PURLIN
P-1,2,3

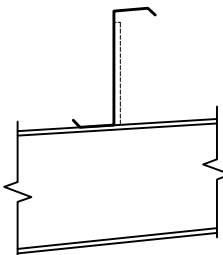


TYP.X-SECTION OF PURLIN
TO RAFTER CONNECTION

BOLT SIZE: 16
PLATE THK.: 12MM

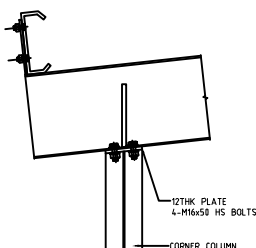


SP-1

BOLT SIZE: 16
PLATE THK.: 12MM

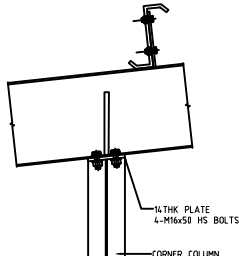

SP-2

BOLT SIZE: 20
PLATE THK.: 12MM

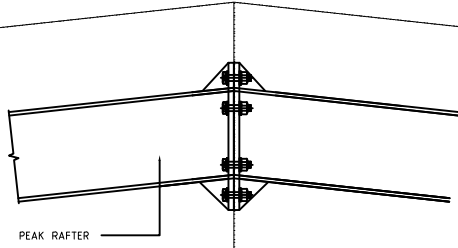


SP-3

00	08-11-22	ISSUED FOR IFC	D.A	UBD	UBD
REV.	DATE	DESCRIPTION	DRWN BY	CHK BY	APR BY



MAIMAAR STEEL Pvt.Ltd
105, Raiwind Road, Thokar Niaz Baig ,Lahore, Pakistan
E-mail: nasir.abbas@maimaargroup.com
E-mail: maimaar.steel@gmail.com
Website: www.maimaargroup.com
E-mail: nasir.abbas@maimaargroup.com
Mob-1 : +(92-300) 807 4017 ,+(92-333) 807 1115

JOB NO./QUOTE NO.	-	BLDG #.	01
PROJECT NAME	MAIMAAR FACTORY		
CUSTOMER			
JOB SITE LOCATION			
ENDWALL ELEVATION ALONG GL-5			DWG. NO. 01

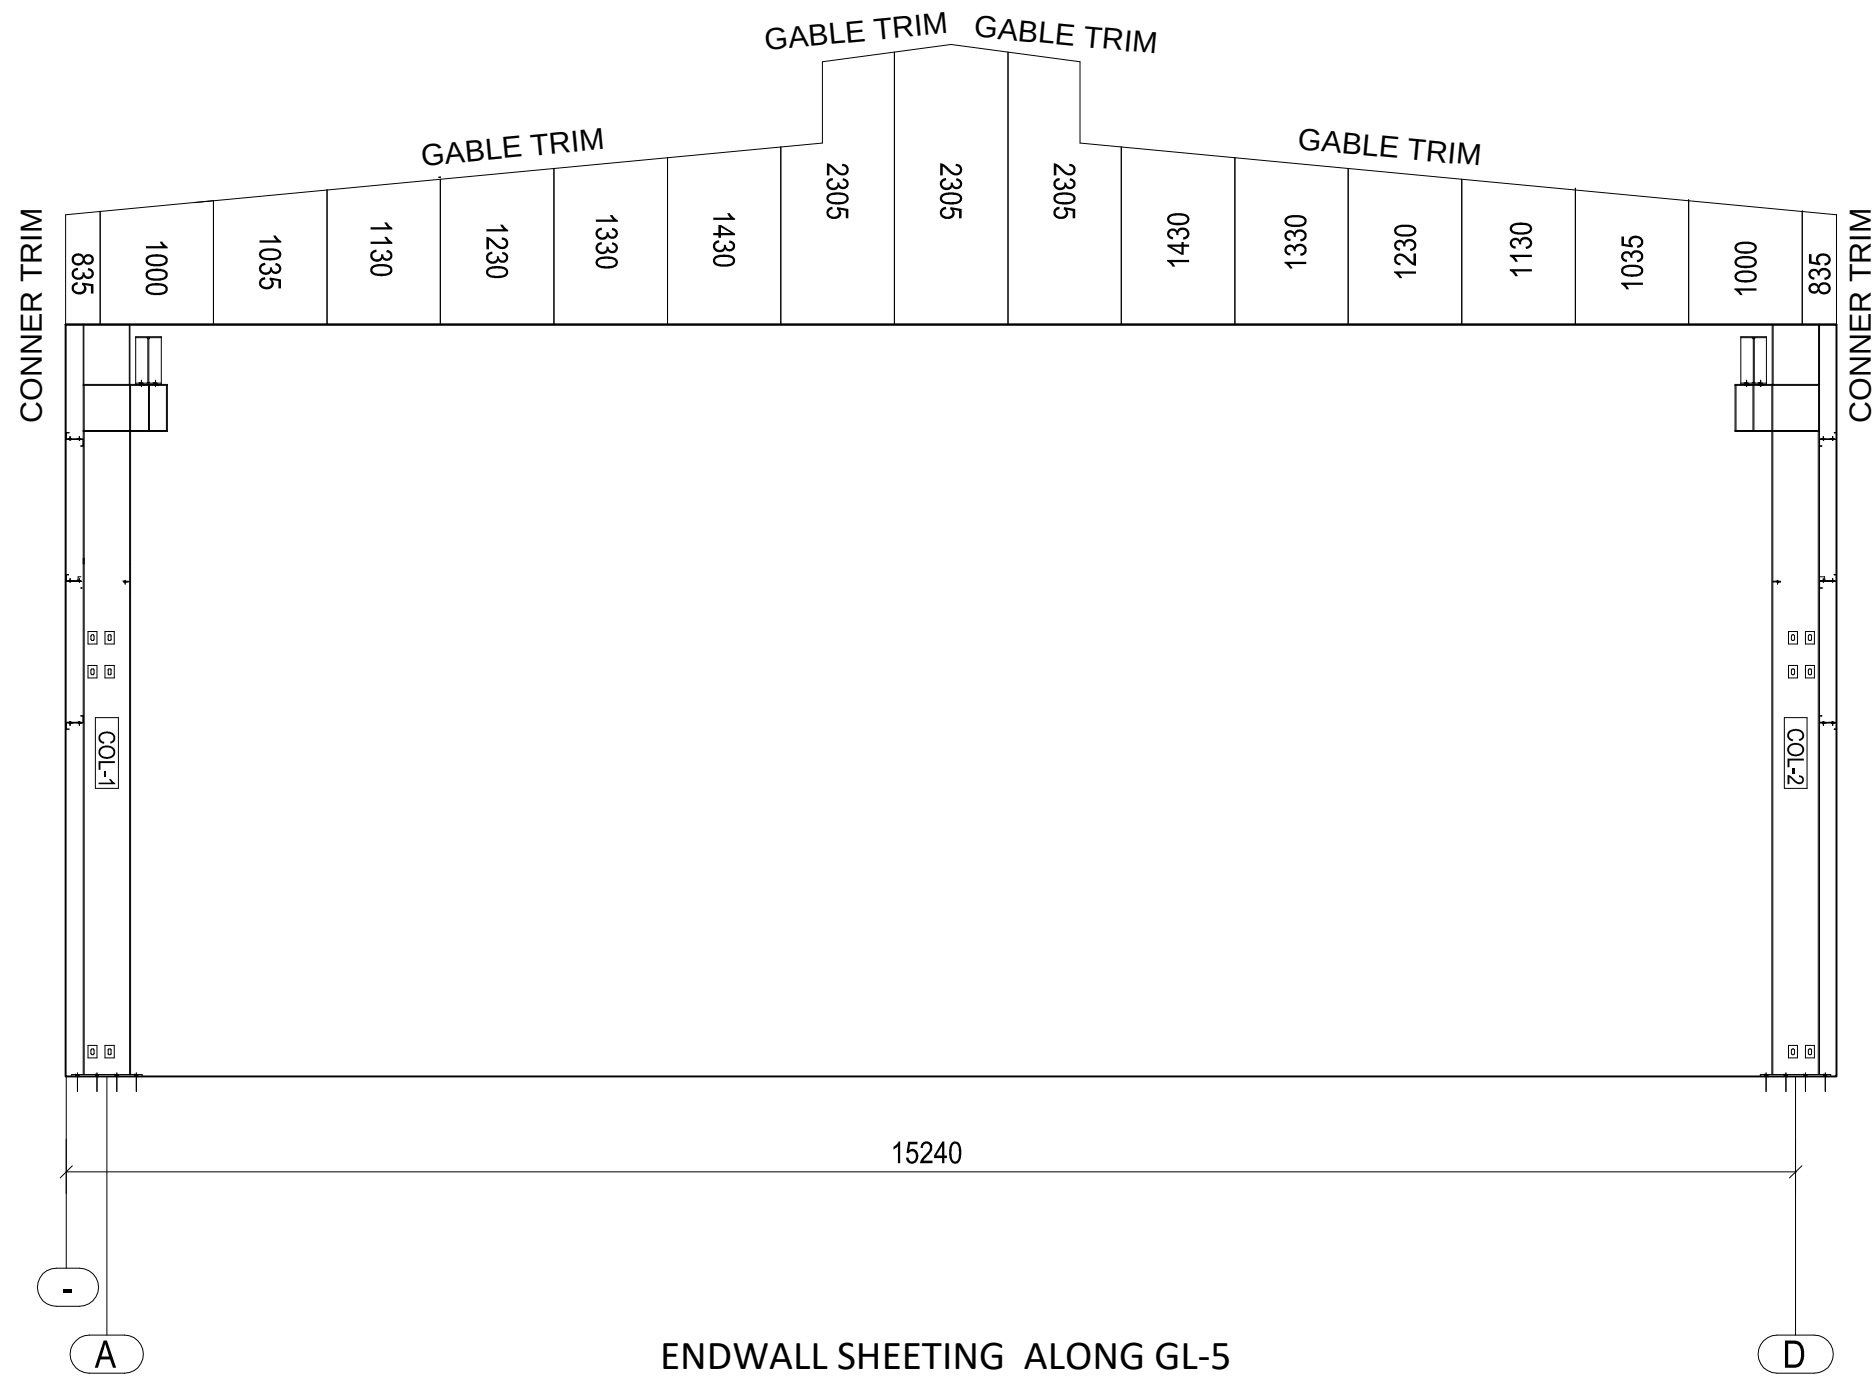

ENDWALL SHEETING ALONG GL-5


00	08-11-22	ISSUED FOR IFC	D.A	UBD	UBD
REV.	DATE	DESCRIPTION	DRWN BY	CHK BY	APR BY

MAIMAAR




MAIMAAR STEEL Pvt.Ltd
105, Raiwind Road, Thokar Niaz Baig ,Lahore, Pakistan
E-mail: nasir.abbas@maimaargroup.com
E-mail: maimaar.steel@gmail.com
Website: www.maimaargroup.com
E-mail: nasir.abbas@maimaargroup.com
Mob-1 : +(92-300) 807 4017 ,+(92-333) 807 1115


JOB NO./QUOTE NO.	-	BLDG #.	01
PROJECT NAME	MAIMAAR FACTORY		
CUSTOMER			
JOB SITE LOCATION			
ENDWALL SHEETING ALONG GL-5			DWG. NO. 01

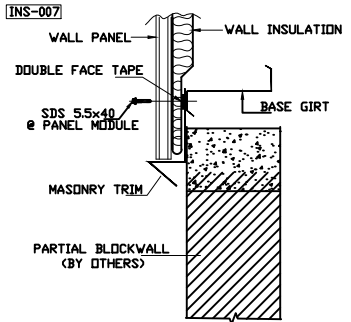


SECTION AT PARTIAL BLOCKWALL

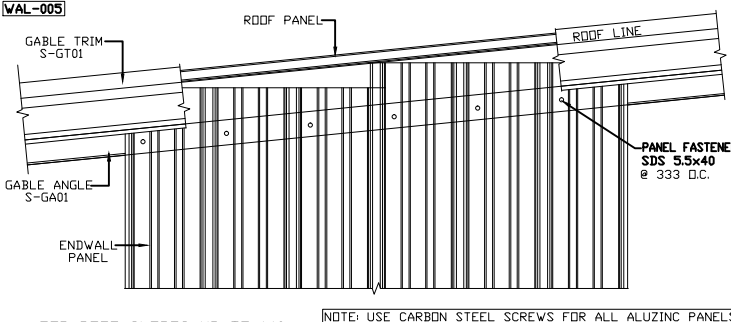


TYPICAL ENDWALL PANEL FIXING DETAIL

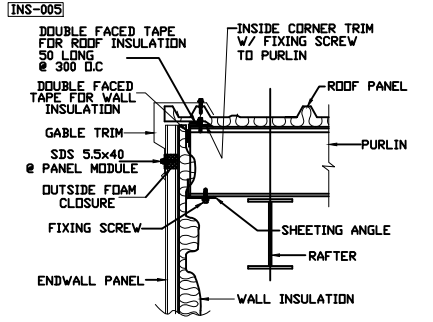


GABLE DETAIL WITH INSULATION

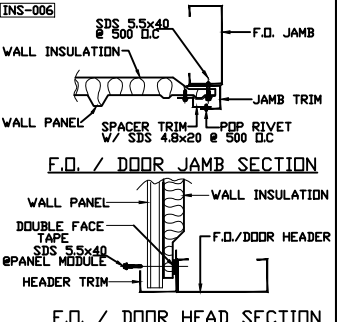

SECTION AT F.O./DOOR HEAD & JAMB

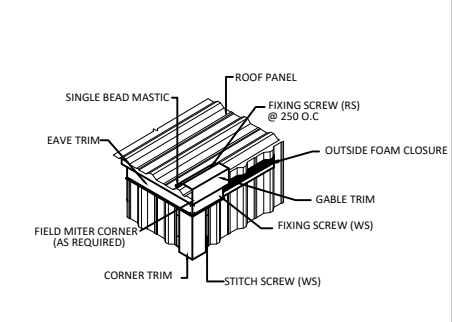

GABLE TRIM WITH EAVE TRIM DETAIL

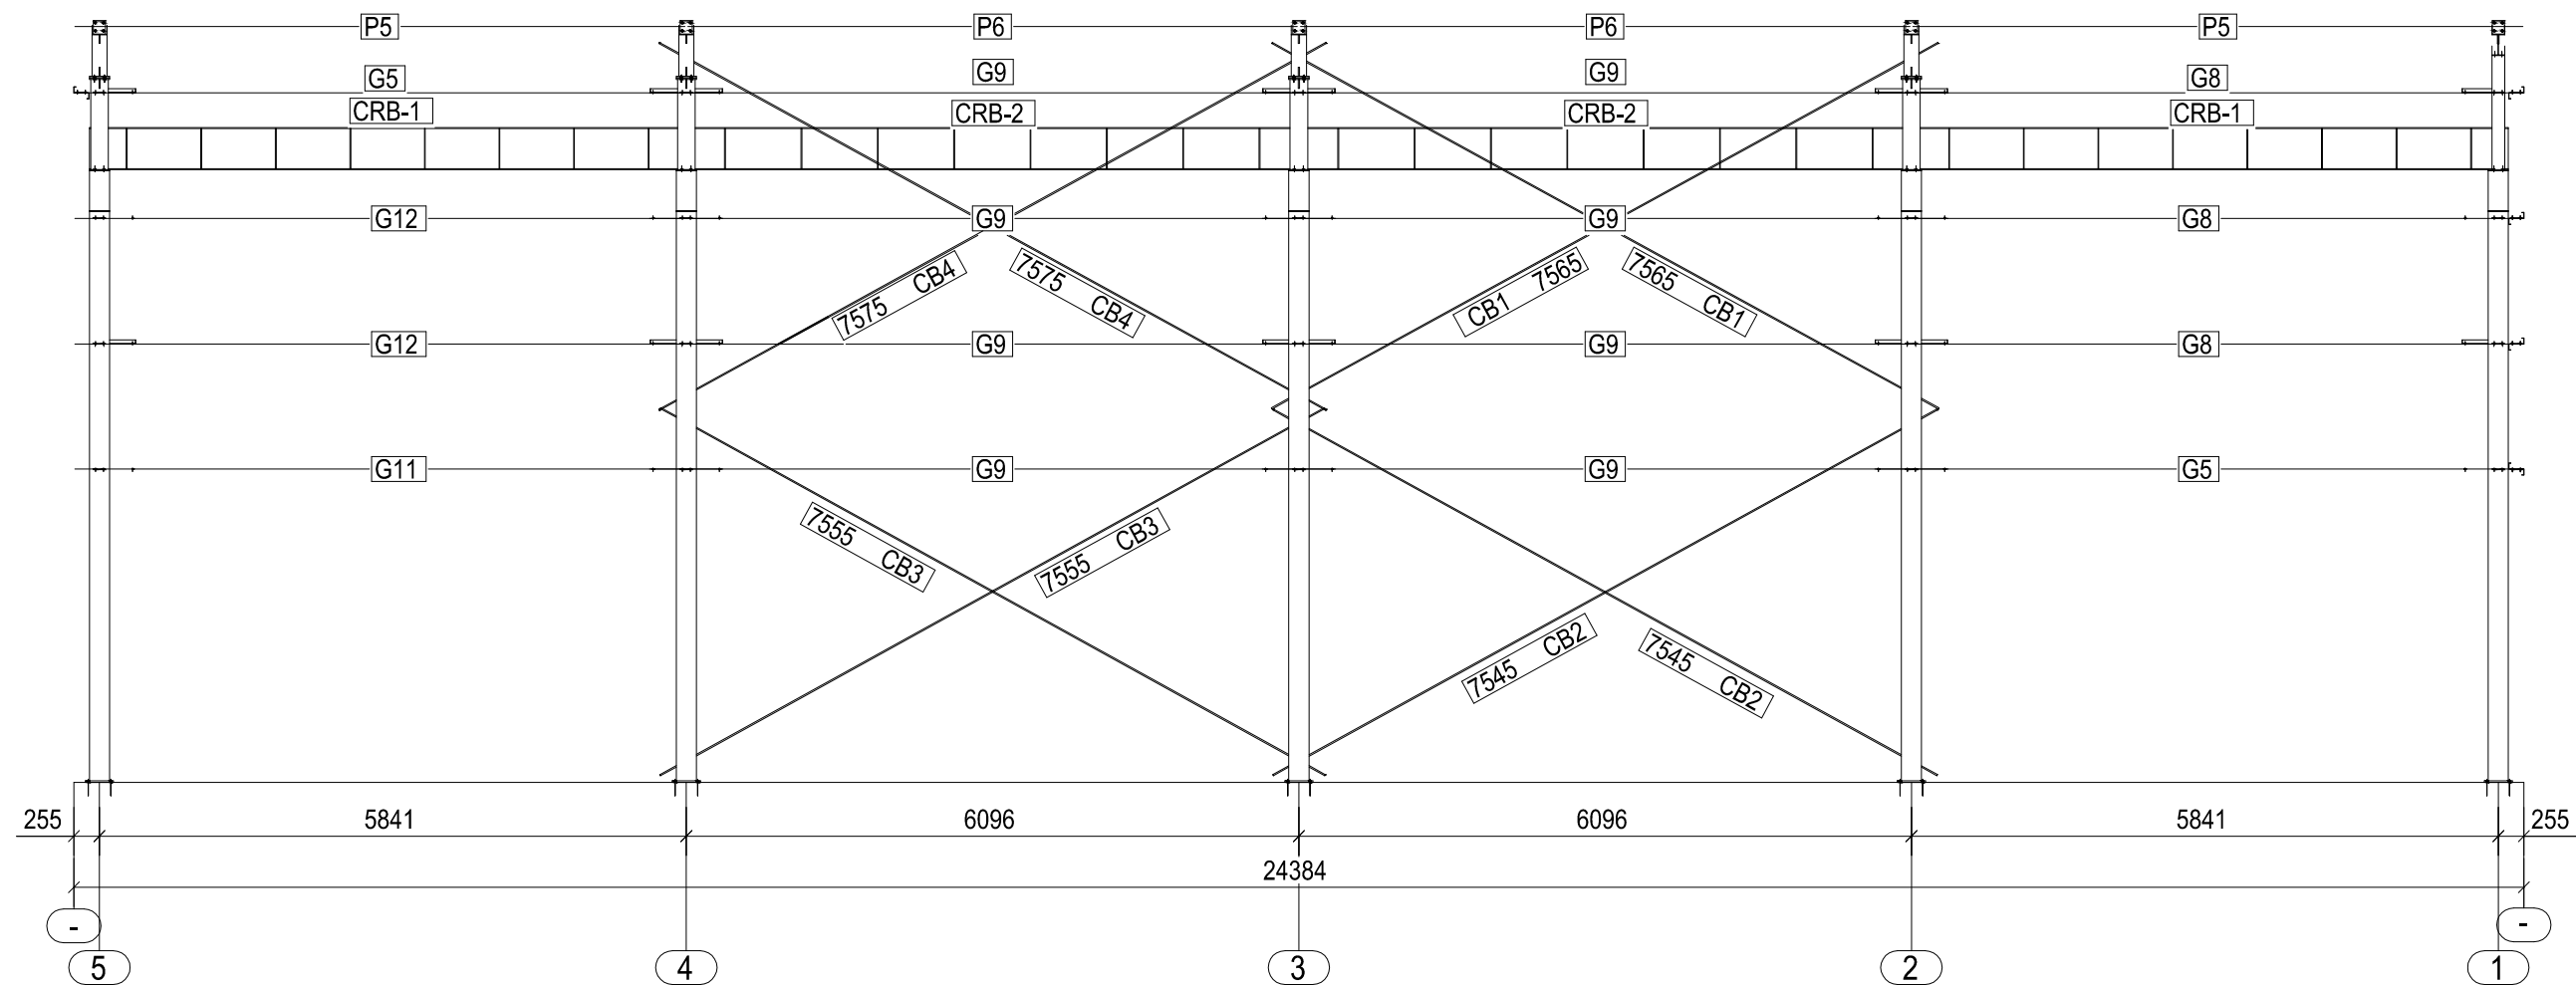

SIDEWALL ELEVATION ALONG GL-A

00	08-11-22	ISSUED FOR IFC	D.A	UBD	UBD
REV.	DATE	DESCRIPTION	DRWN BY	CHK BY	APR BY



MAIMAAR STEEL Pvt.Ltd
 105, Raiwind Road, Thokar Niaz Baig ,Lahore, Pakistan
 E-mail: nasir.abbas@maimaargroup.com
 E-mail: maimaar.steel@gmail.com
 Website: www.maimaargroup.com
 E-mail: nasir.abbas@maimaargroup.com
 Mob-1 : +(92-300) 807 4017 ,+(92-333) 807 1115

JOB NO./QUOTE NO.	-	BLDG #.	01
PROJECT NAME	MAIMAAR FACTORY		
CUSTOMER			
JOB SITE LOCATION			
SIDEWALL ELEVATION ALONG GL-A			DWG. NO. 01


SECTION AT BRICK WALL

FLANGE BRACE DETAIL

TYP. X-SECTION OF Z PURLIN P-1,2,3

TYP.X-SECTION OF PURLIN TO RAFTER CONNECTION

CABLE BRACE DETAIL





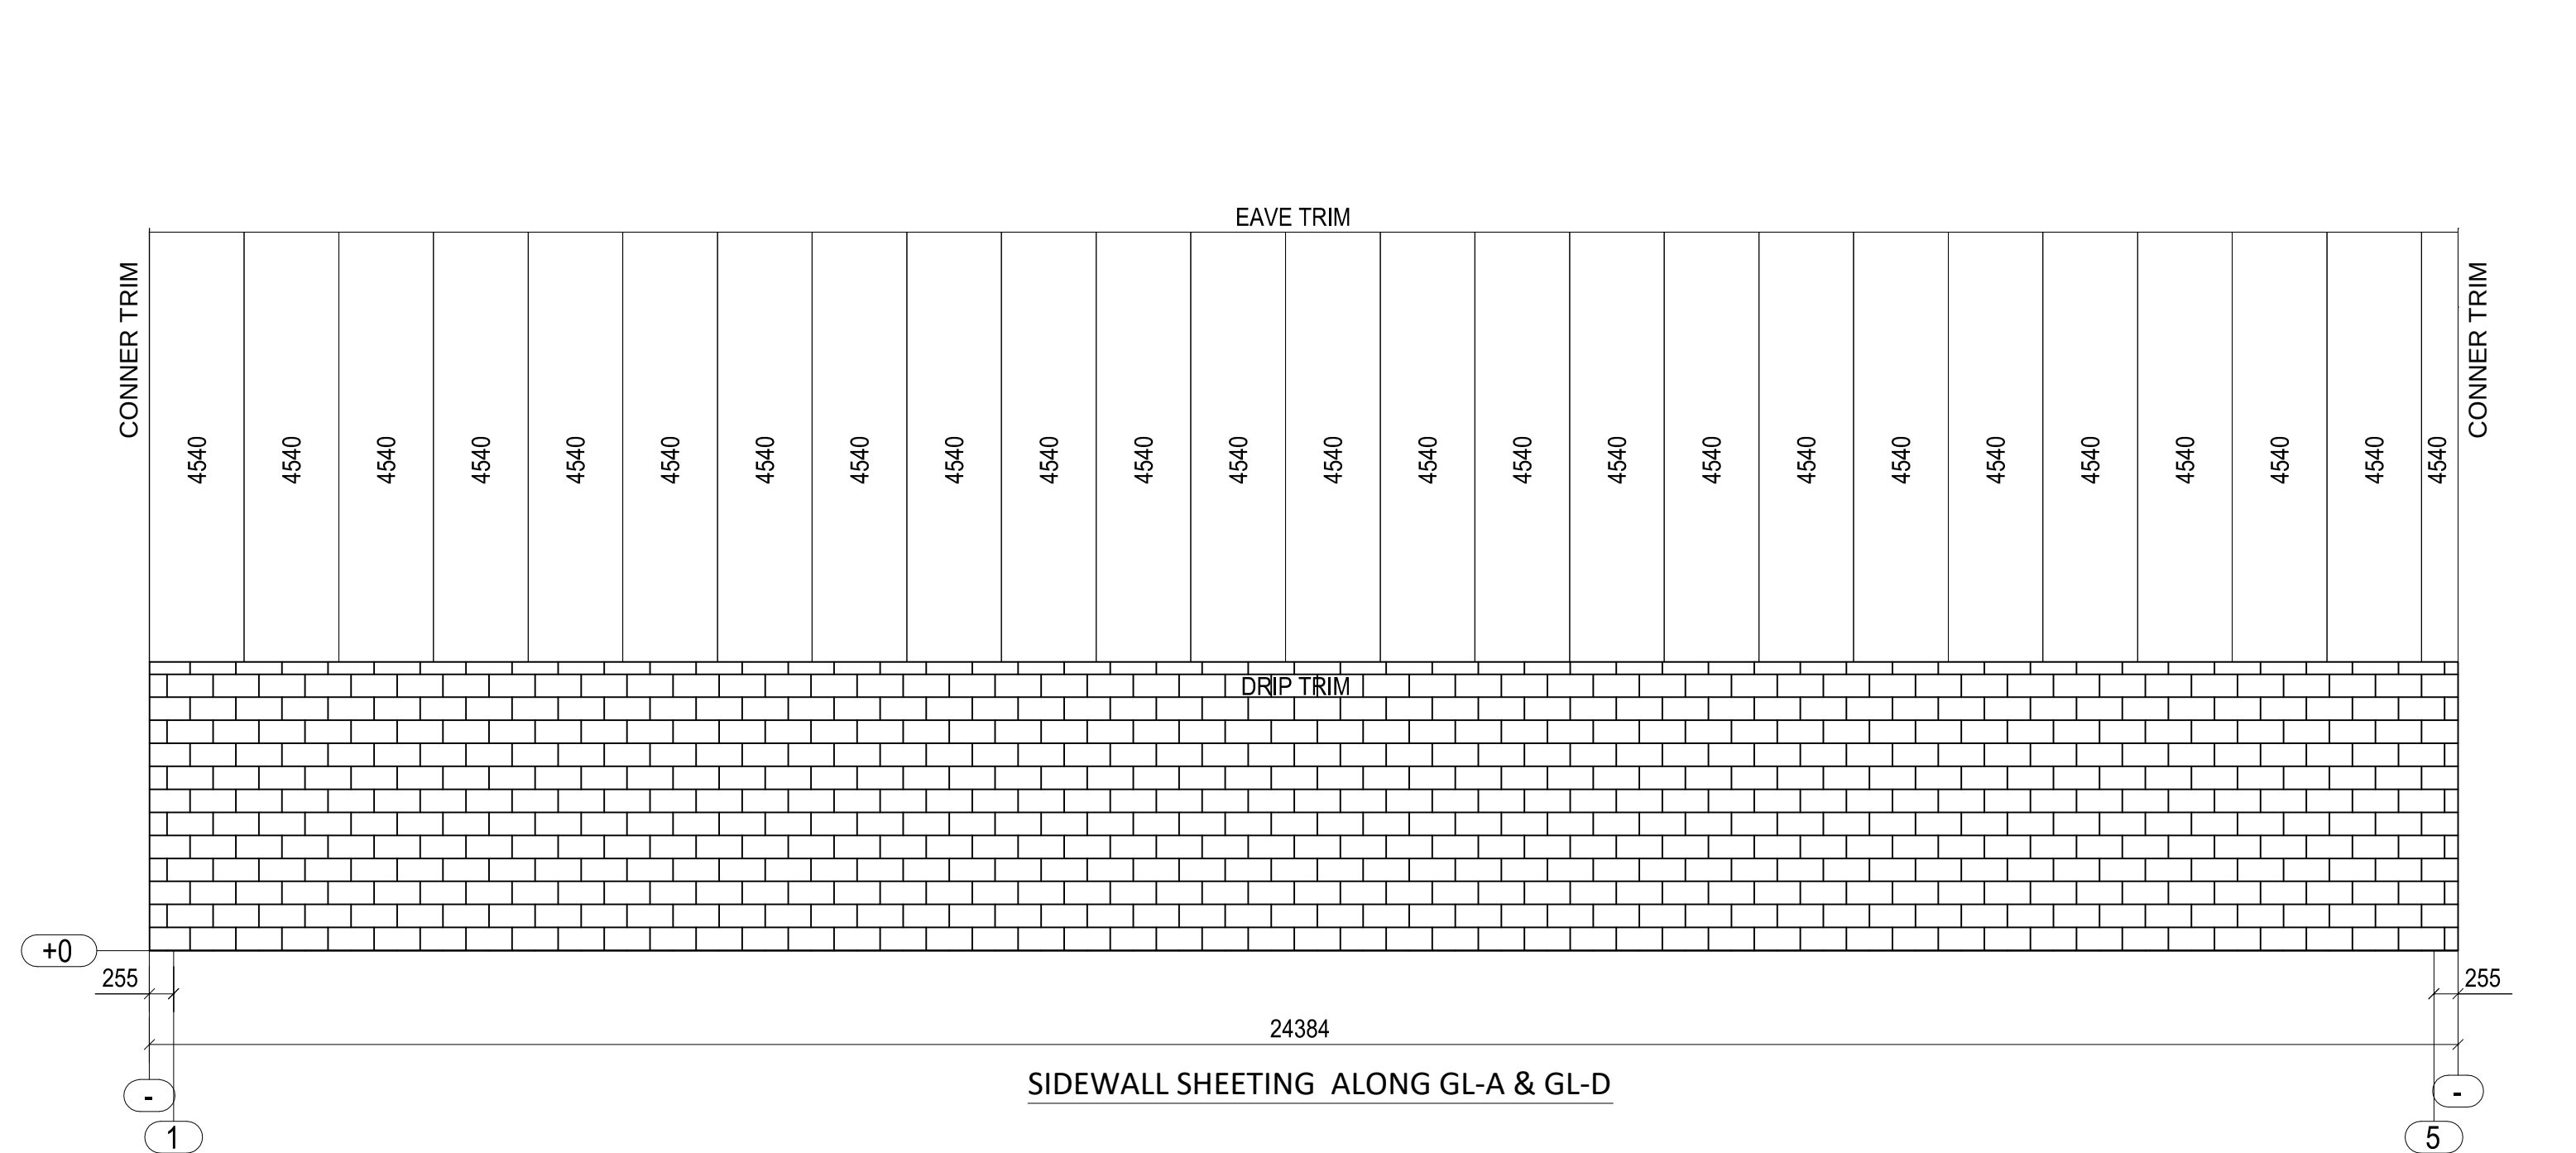



00	08-11-22	ISSUED FOR IFC	D.A	UBD	UBD
REV.	DATE	DESCRIPTION	DRWN BY	CHK BY	APR BY



MAIMAAR STEEL Pvt.Ltd
105, Raiwind Road, Thokar Niaz Baig ,Lahore, Pakistan
E-mail: nasir.abbas@maimaargroup.com
E-mail: maimaar.steel@gmail.com
Website: www.maimaargroup.com
E-mail: nasir.abbas@maimaargroup.com
Mob-1 : +(92-300) 807 4017 ,+(92-333) 807 1115

JOB NO./QUOTE NO.	-	BLDG #.	01
PROJECT NAME	MAIMAAR FACTORY		
CUSTOMER			
JOB SITE LOCATION			
SIDEWALL SHEETING ALONG GL-A & GL-D			DWG. NO. 01

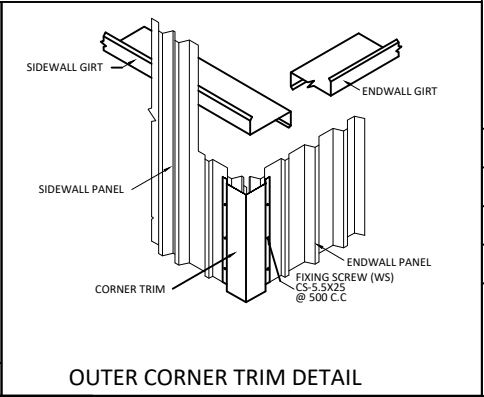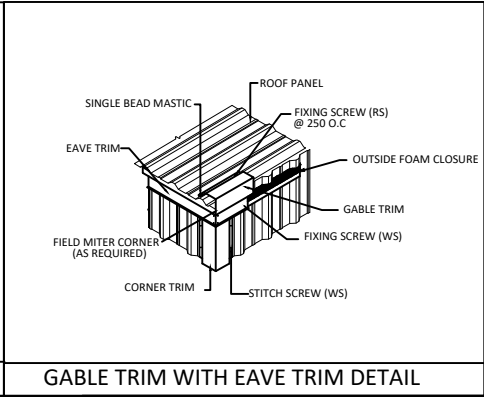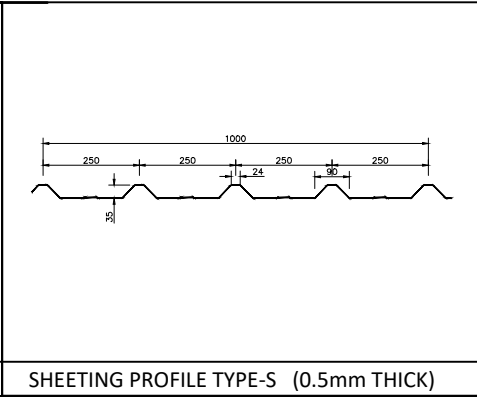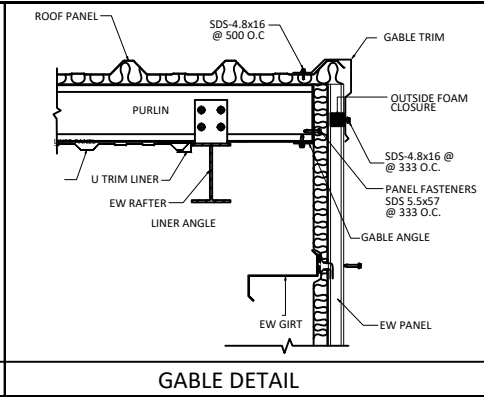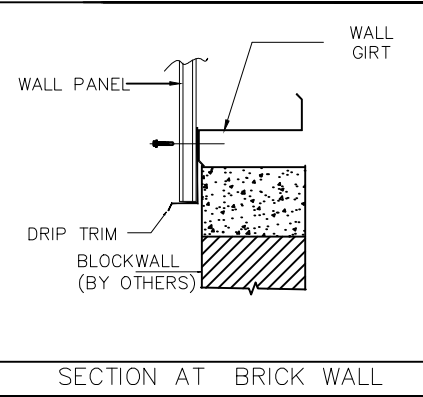

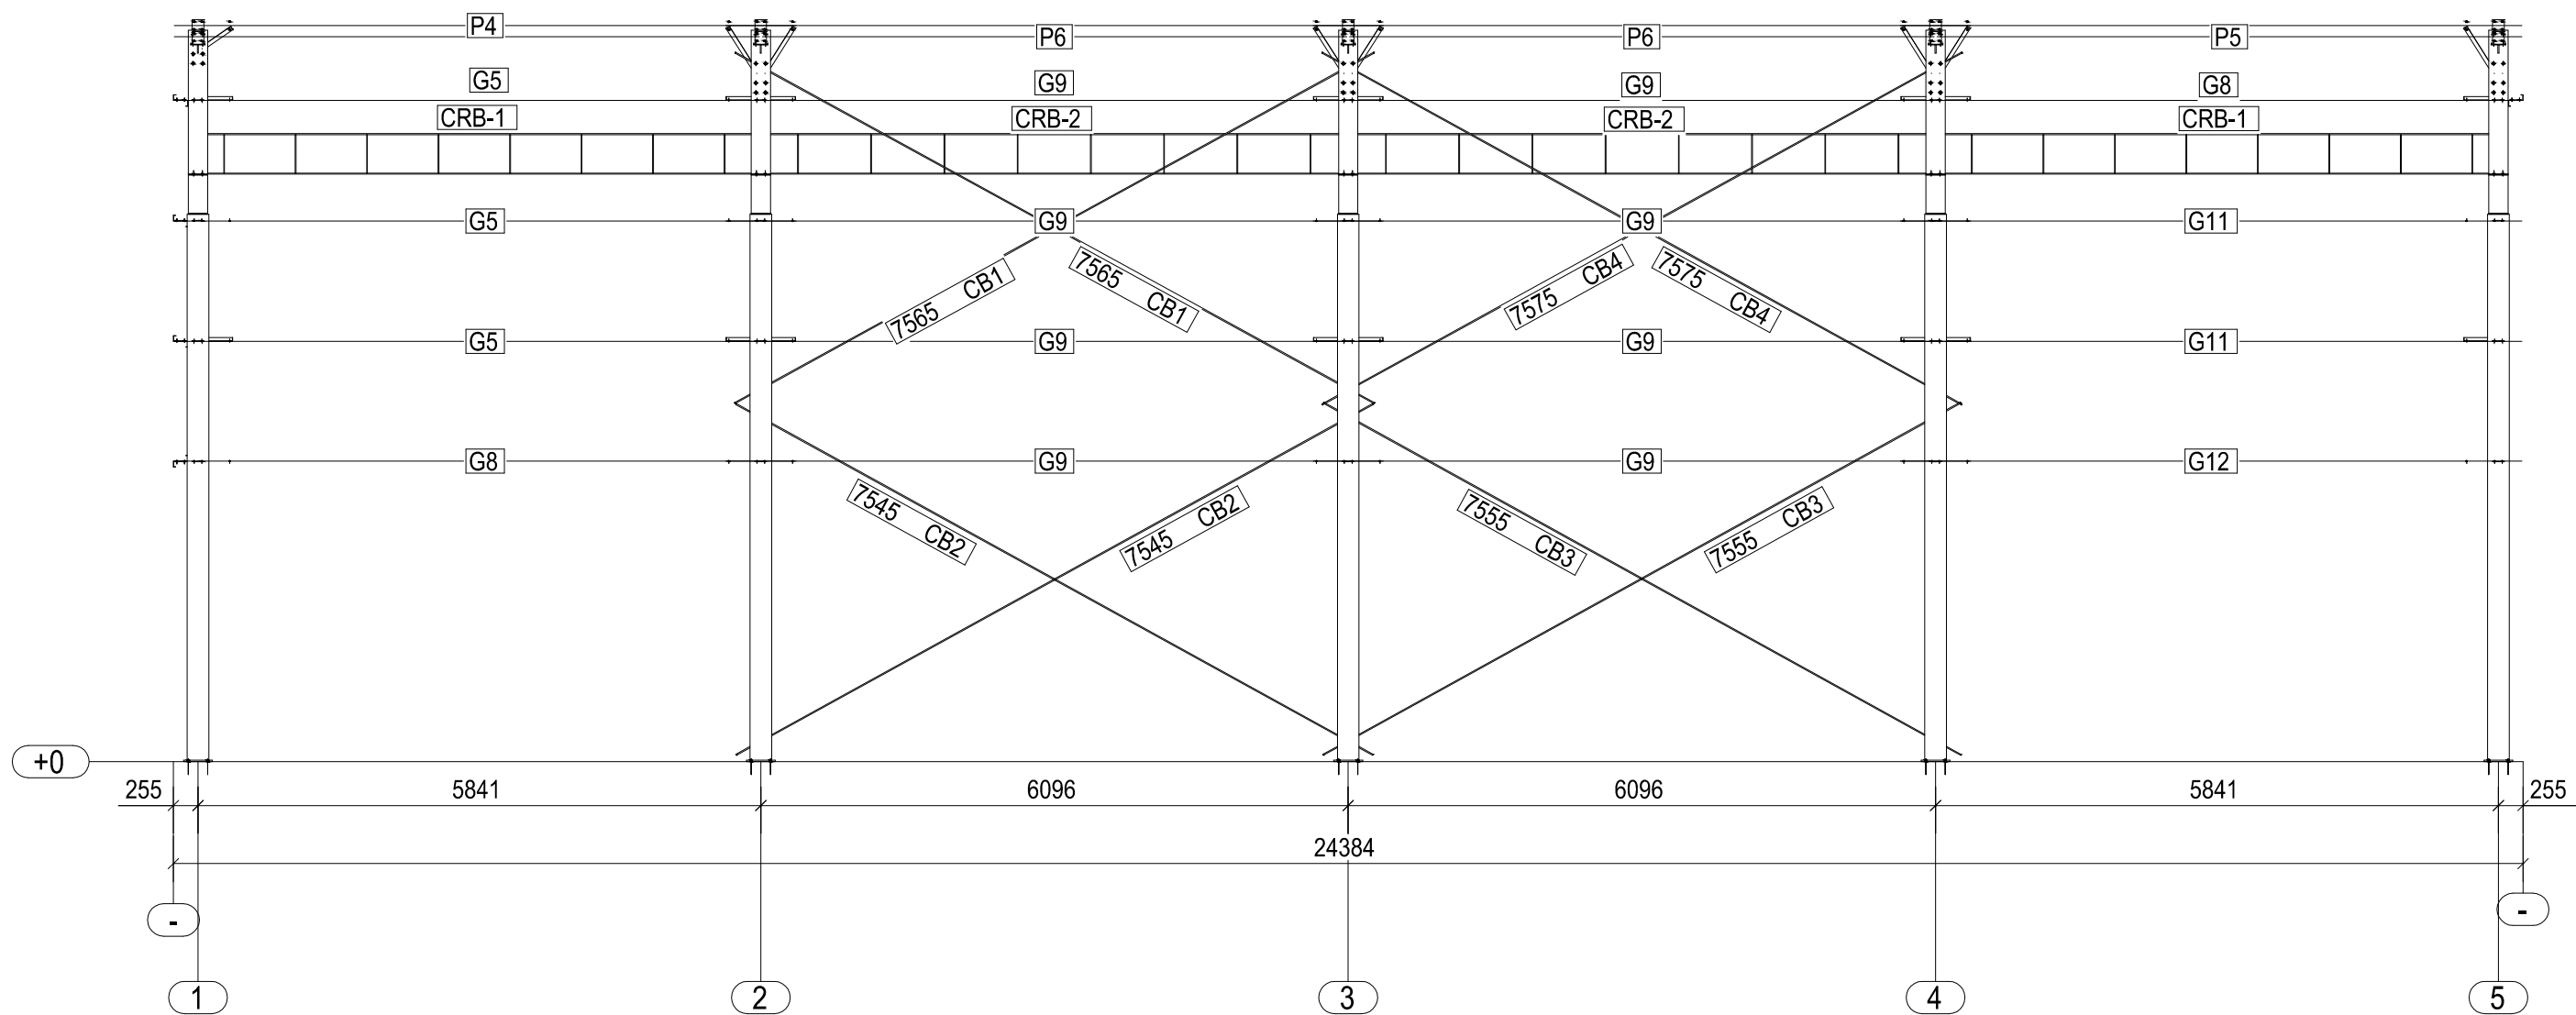

SIDEWALL ELEVATION ALONG GL-D

00	08-11-22	ISSUED FOR IFC	D.A	UBD	UBD
REV.	DATE	DESCRIPTION	DRWN BY	CHK BY	APR BY

MAIMAAR

MAIMAAR STEEL Pvt.Ltd
105, Raiwind Road, Thokar Niaz Baig ,Lahore, Pakistan
E-mail: nasir.abbas@maimaargroup.com
E-mail: maimaar.steel@gmail.com
Website: www.maimaargroup.com
E-mail: nasir.abbas@maimaargroup.com
Mob-1 : +(92-300) 807 4017 ,+(92-333) 807 1115

JOB NO./QUOTE NO.	-	BLDG #.	01
PROJECT NAME	MAIMAAR FACTORY		
CUSTOMER			
JOB SITE LOCATION			

SIDEWALL ELEVATION ALONG GL-D		DWG. NO.	01
-------------------------------	--	----------	----


SECTION AT BRICK WALL

FLANGE BRACE DETAIL


TYP. X-SECTION OF Z PURLIN P-1,2,3

TYP. X-SECTION OF PURLIN TO RAFTER CONNECTION

CABLE BRACE DETAIL

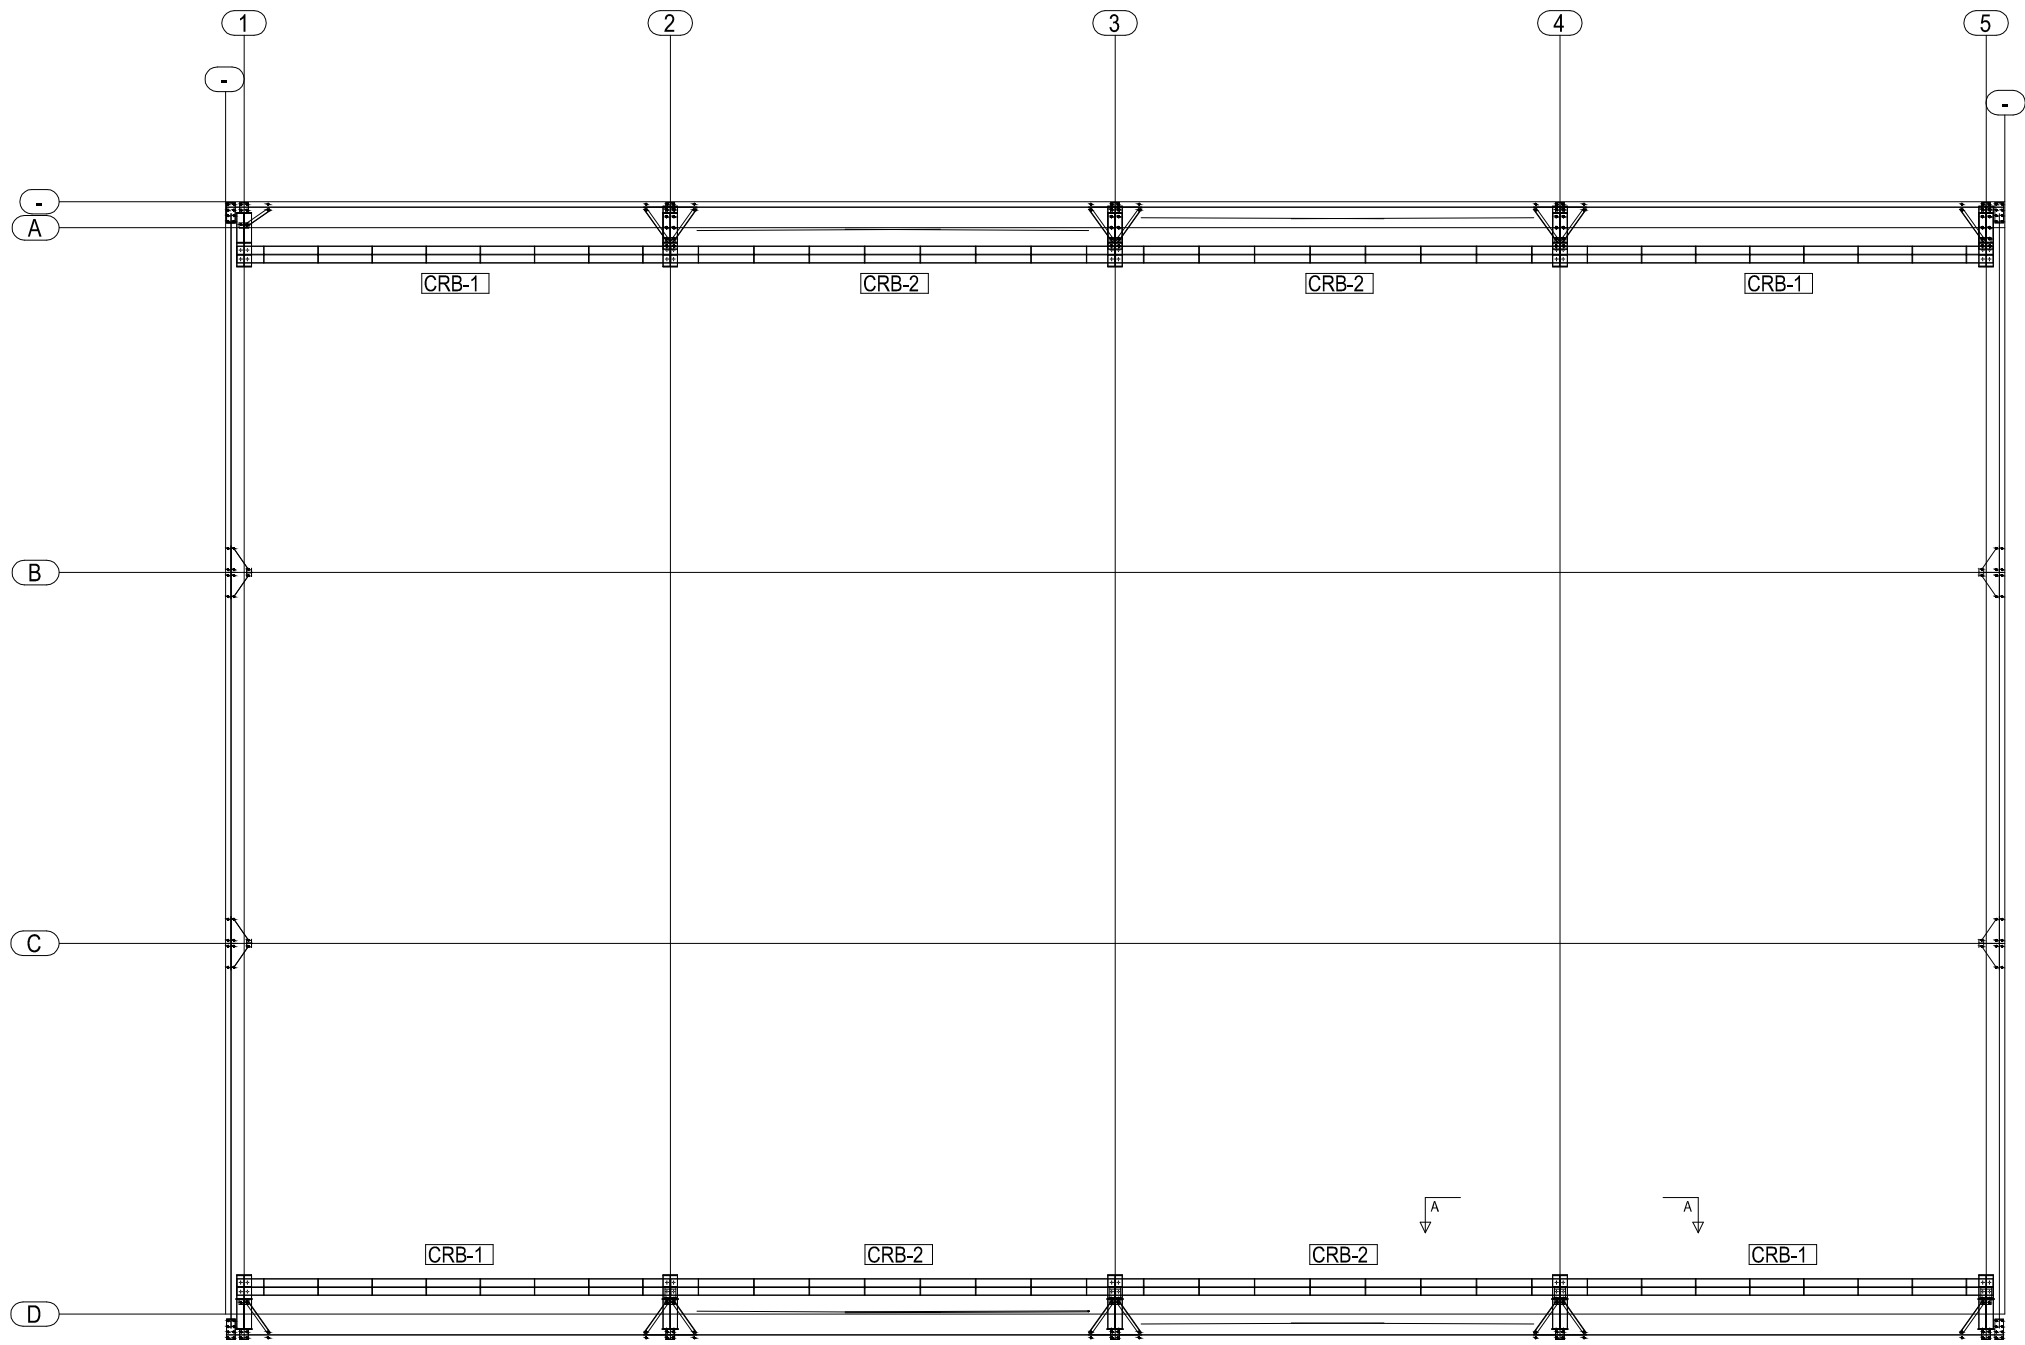

CRANE BEAM PLAN

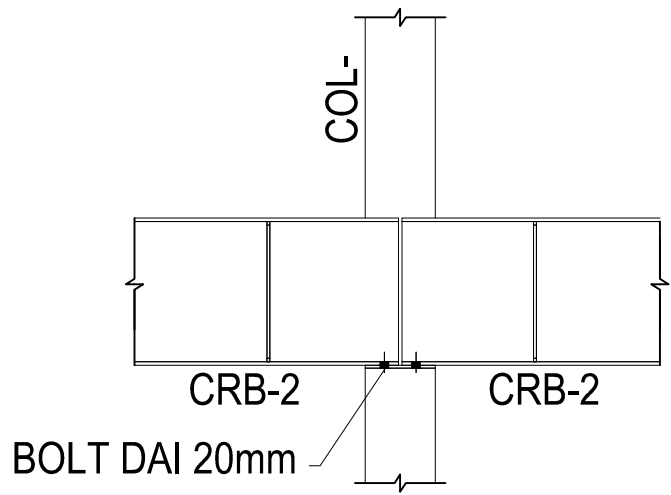


DETAIL=A-A

00	08-11-22	ISSUED FOR IFC	D.A	UBD	UBD
REV.	DATE	DESCRIPTION	DRWN BY	CHK BY	APR BY


MAIMAAR

MAIMAAR STEEL Pvt.Ltd
 105, Raiwind Road, Thokar Niaz Baig ,Lahore, Pakistan
 E-mail: nasir.abbas@maimaargroup.com
 E-mail: maimaar.steel@gmail.com
 Website: www.maimaargroup.com
 E-mail: nasir.abbas@maimaargroup.com
 Mob-1 : +(92-300) 807 4017 ,+(92-333) 807 1115


JOB NO./QUOTE NO.	-	BLDG #.	01
PROJECT NAME	MAIMAAR FACTORY		
CUSTOMER			
JOB SITE LOCATION			
CRANE BEAM PLAN			DWG. NO. 01

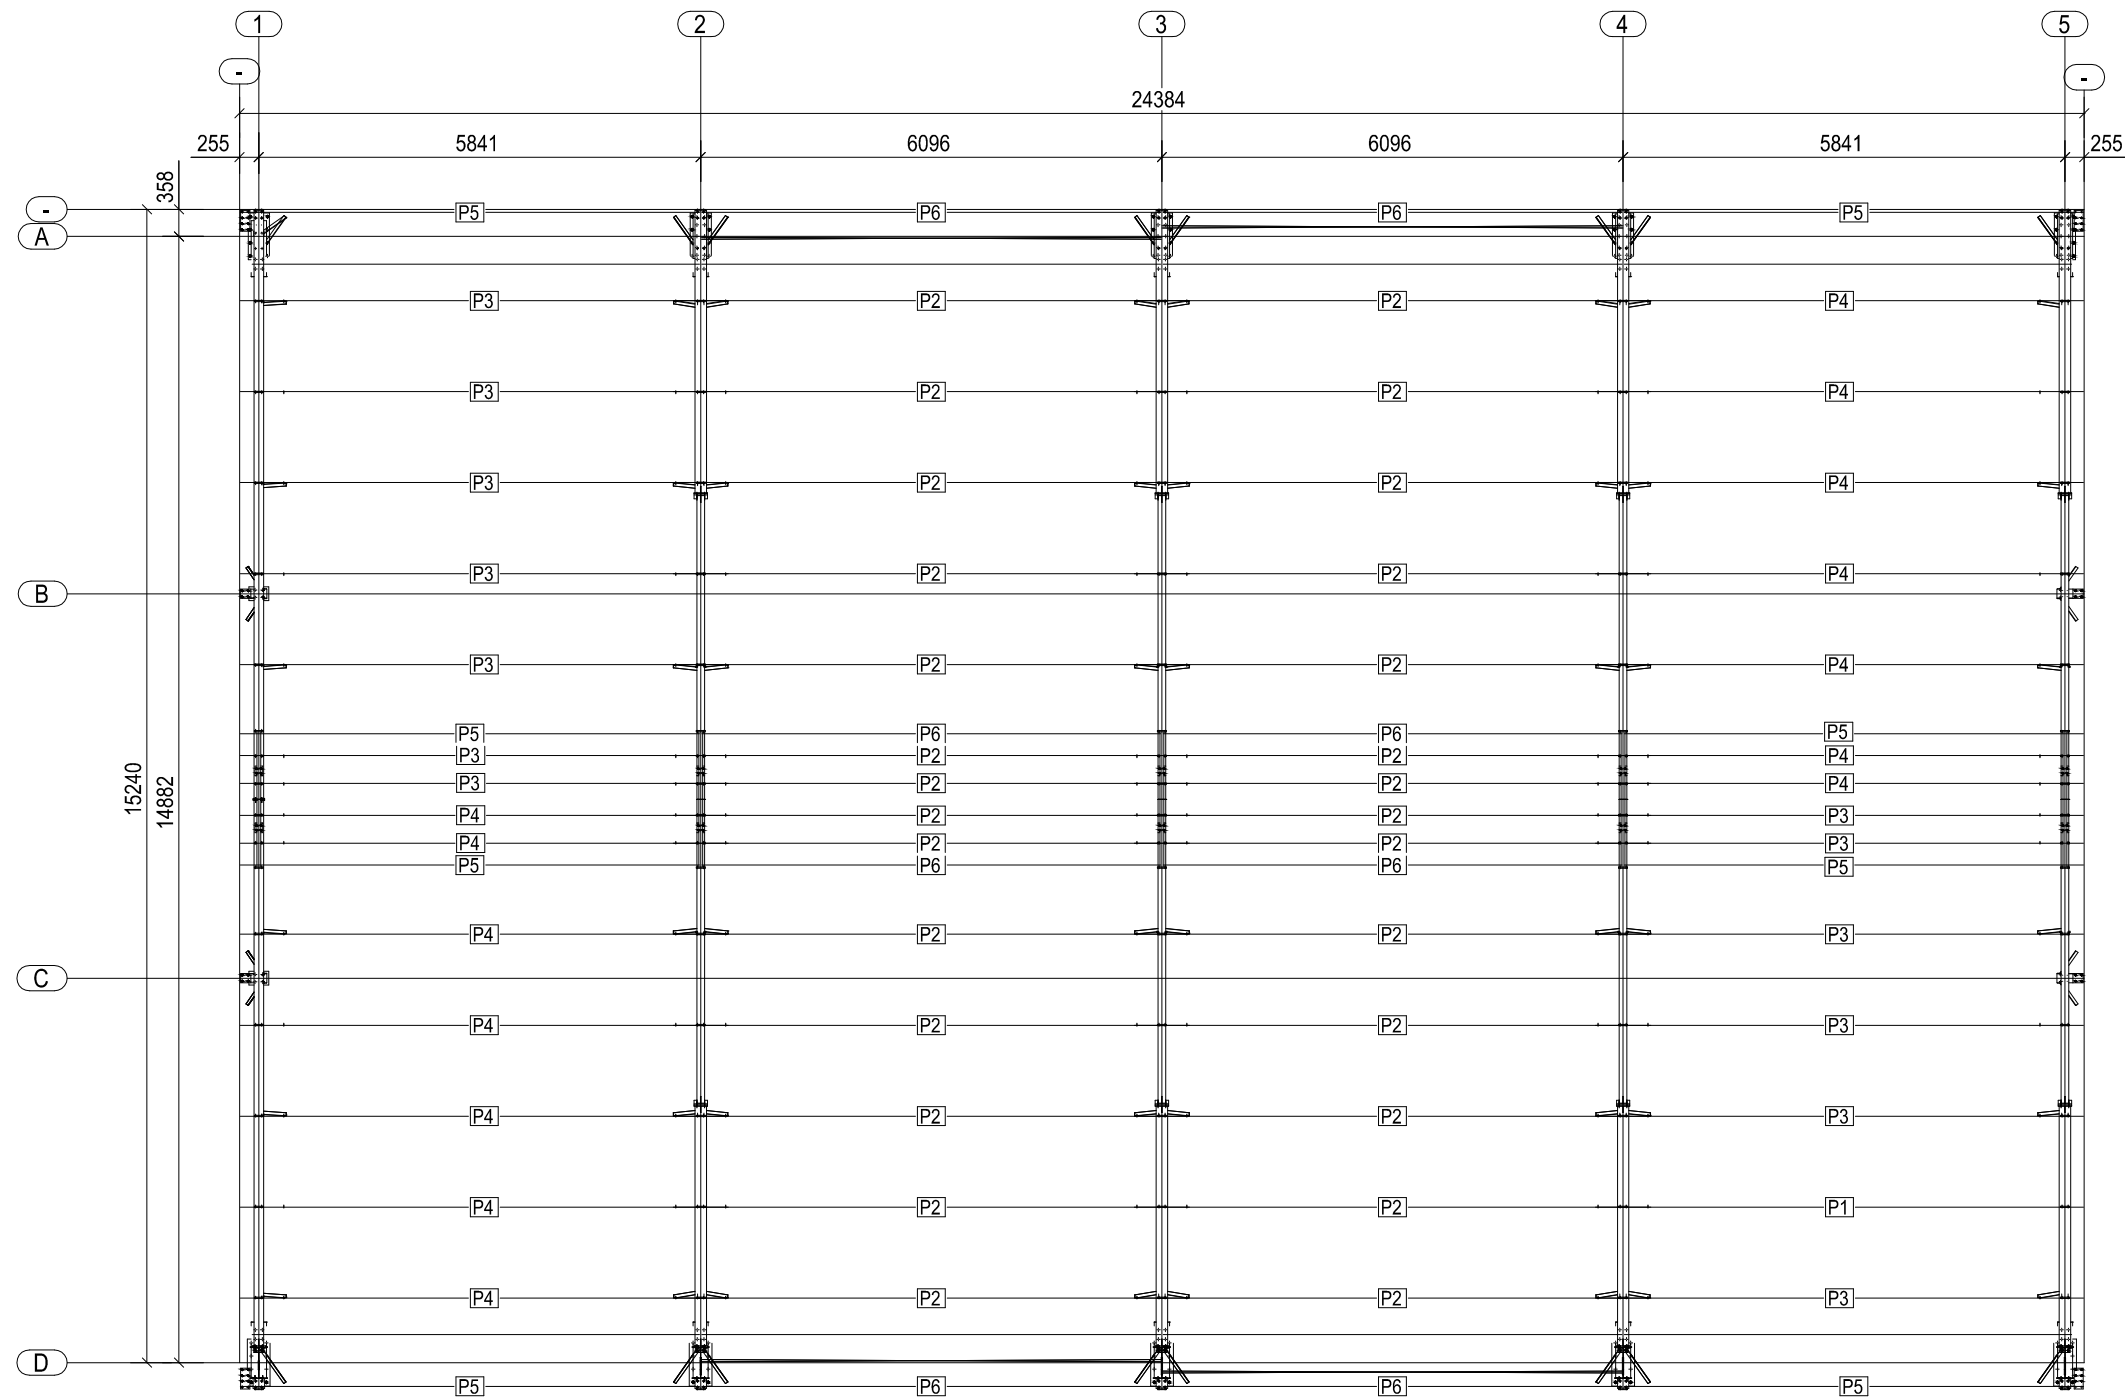


ROOF FRAMING PLAN

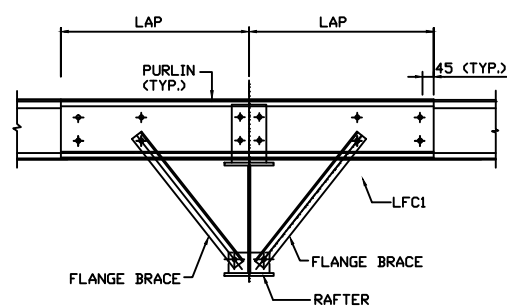


FLANGE BRACE DETAIL

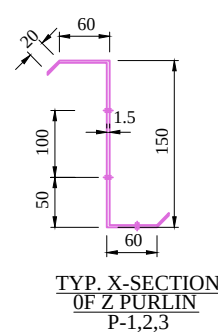

TYP. X-SECTION OF Z PURLIN P-1,2,3

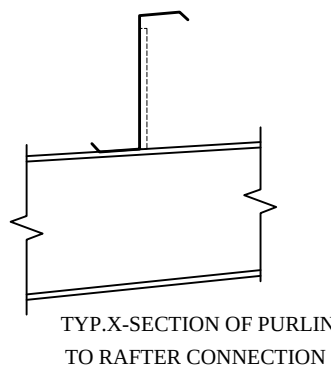


TYP. X-SECTION OF PURLIN TO RAFTER CONNECTION

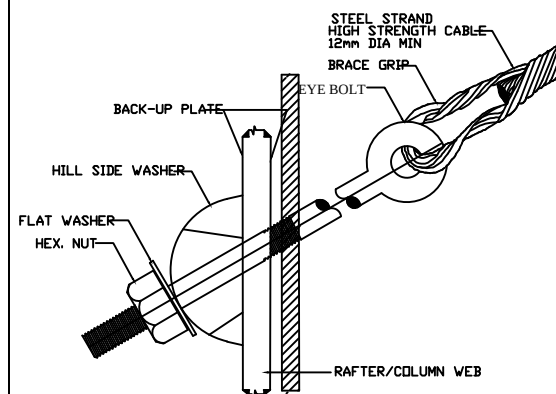

CABLE BRACE DETAIL

00	08-11-22	ISSUED FOR IFC	D.A	UBD	UBD
REV.	DATE	DESCRIPTION	DRWN BY	CHK BY	APR BY
MAIMAAR MAIMAAR STEEL Pvt.Ltd 105, Raiwind Road, Thokar Niaz Baig ,Lahore, Pakistan E-mail: nasir.abbas@maimaargroup.com E-mail: maimaar.steel@gmail.com Website: www.maimaargroup.com E-mail: nasir.abbas@maimaargroup.com Mob-1 : +(92-300) 807 4017 ,+(92-333) 807 1115					
JOB NO./QUOTE NO.			BLDG #. 01		
PROJECT NAME			MAIMAAR FACTORY		
CUSTOMER					
JOBSITE LOCATION					
ROOF FRAMING PLAN					DWG. NO.
					01

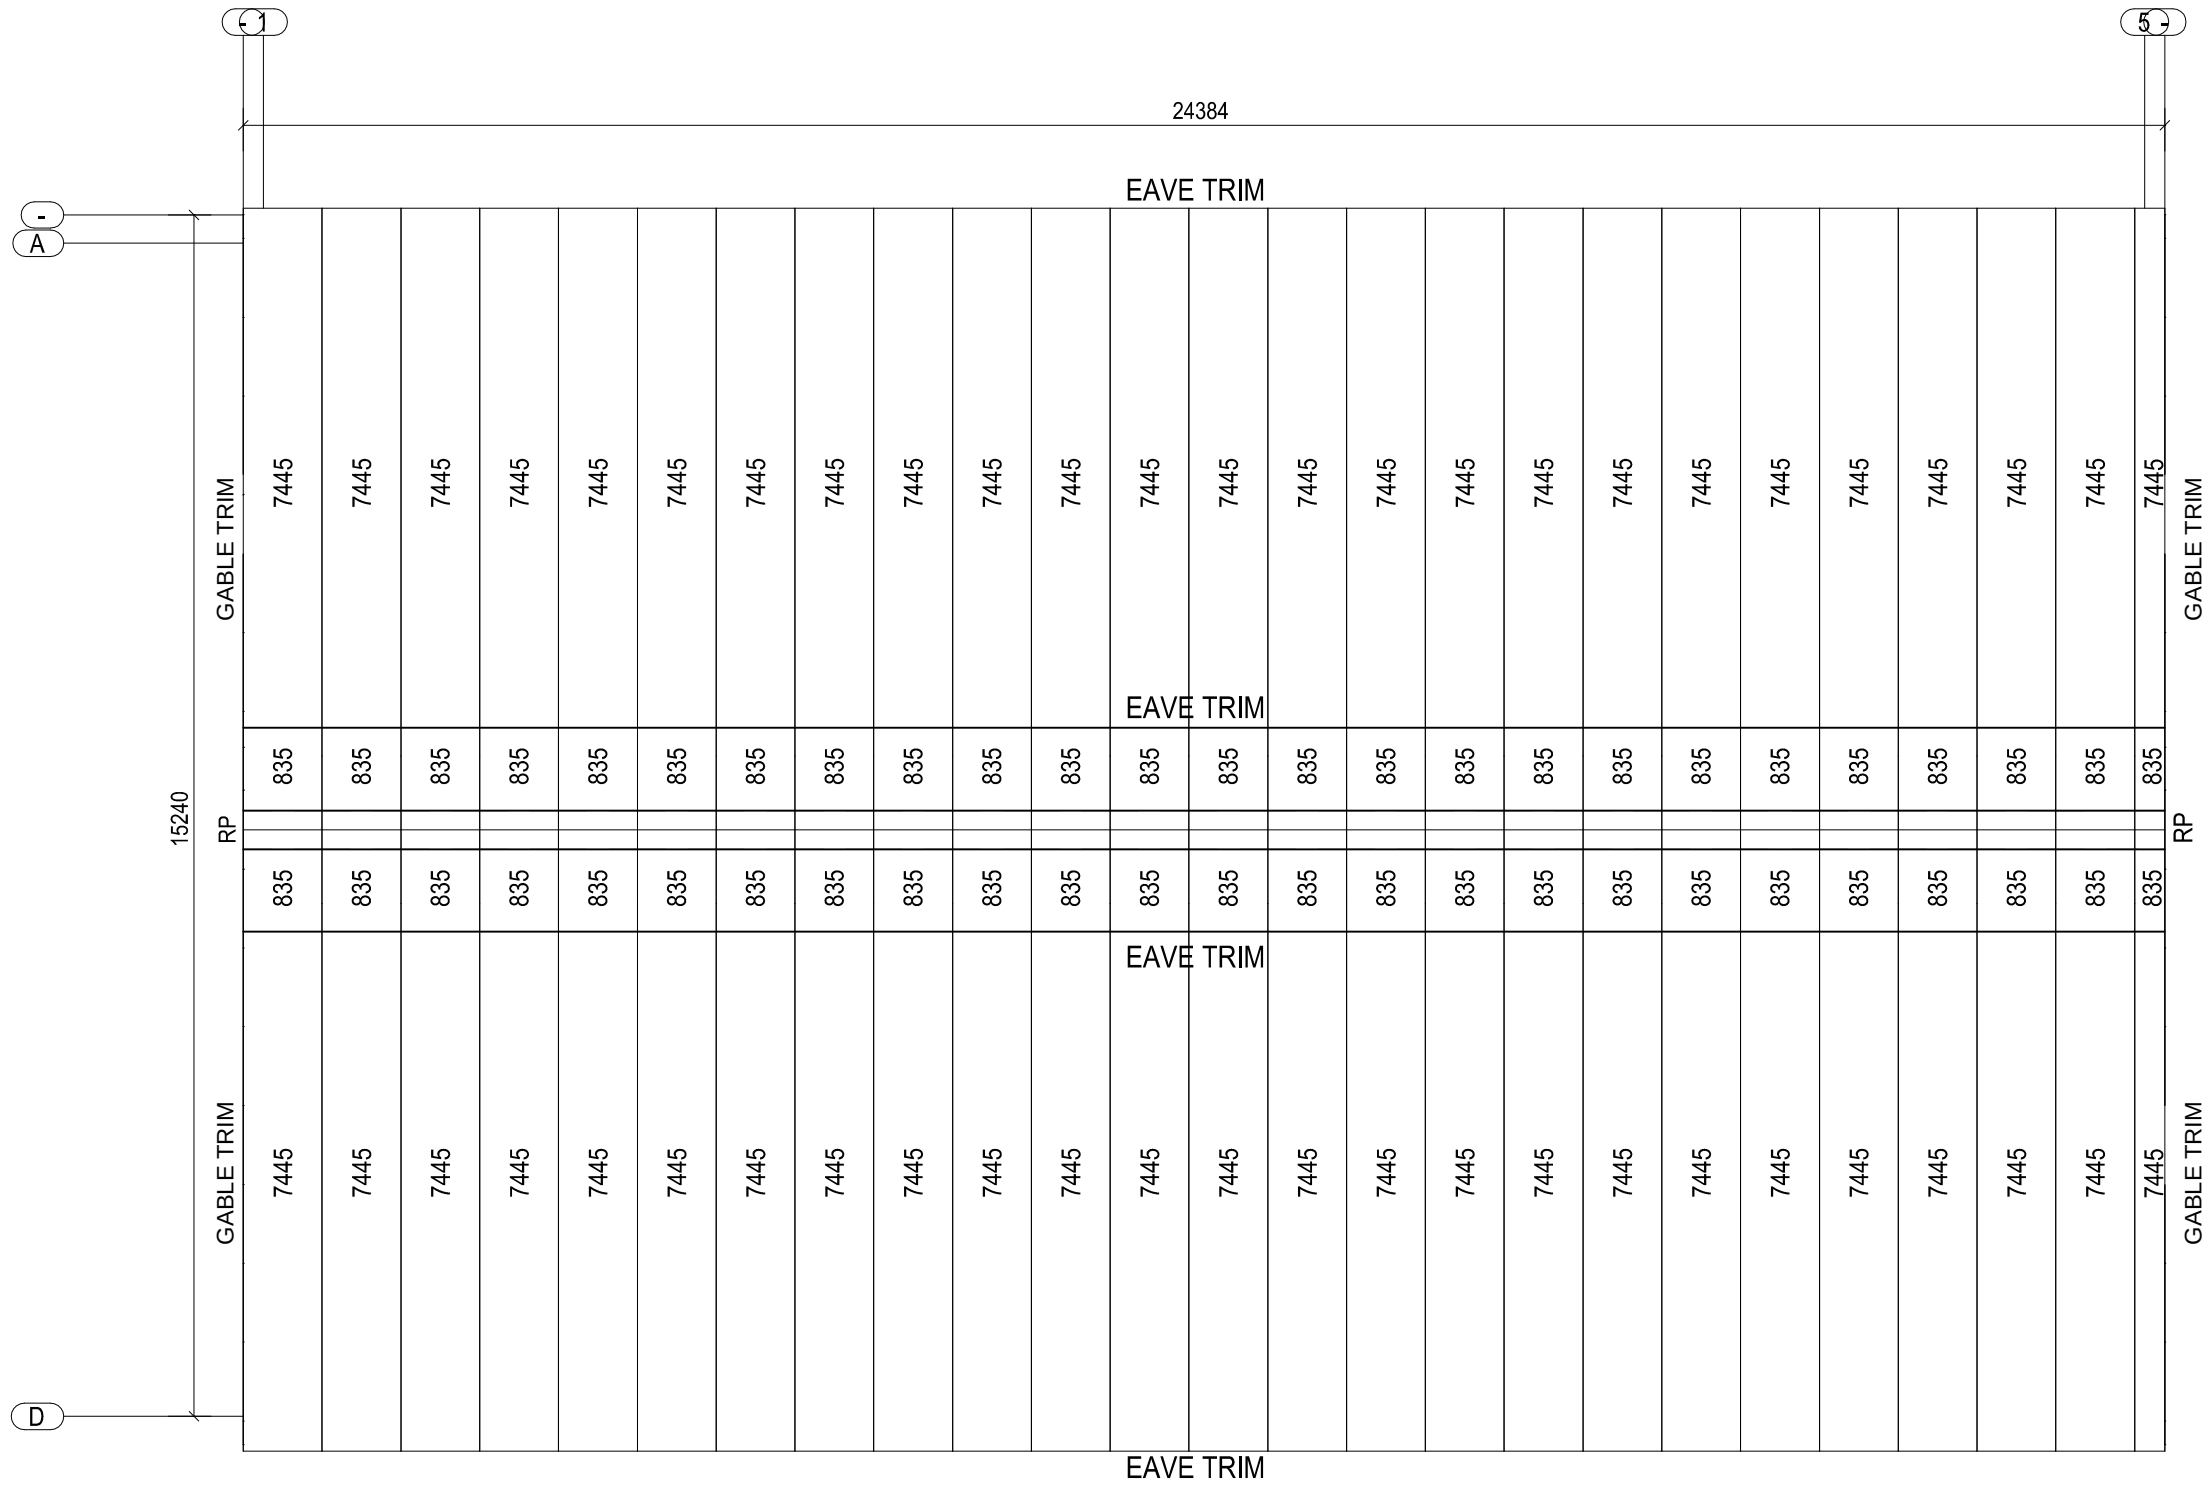

ROOF SHEETING PLAN




00	08-11-22	ISSUED FOR IFC	D.A	UBD	UBD
REV.	DATE	DESCRIPTION	DRWN BY	CHK BY	APR BY




MAIMAAR STEEL Pvt.Ltd
105, Raiwind Road, Thokar Niaz Baig ,Lahore, Pakistan
E-mail: nasir.abbas@maimaargroup.com
E-mail: maimaar.steel@gmail.com
Website: www.maimaargroup.com
E-mail: nasir.abbas@maimaargroup.com
Mob-1 : +(92-300) 807 4017 ,+(92-333) 807 1115


JOB NO./QUOTE NO.	-	BLDG #.	01
PROJECT NAME	MAIMAAR FACTORY		
CUSTOMER			
JOB SITE LOCATION			

ROOF SHEETING PLAN

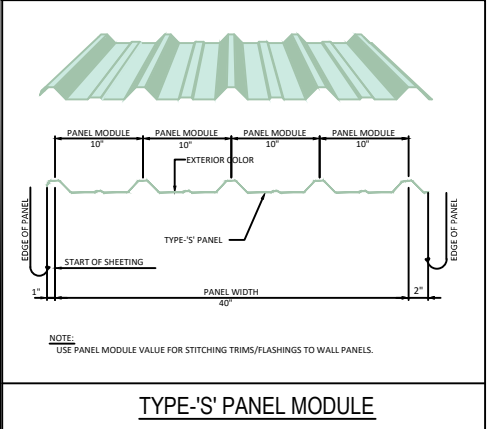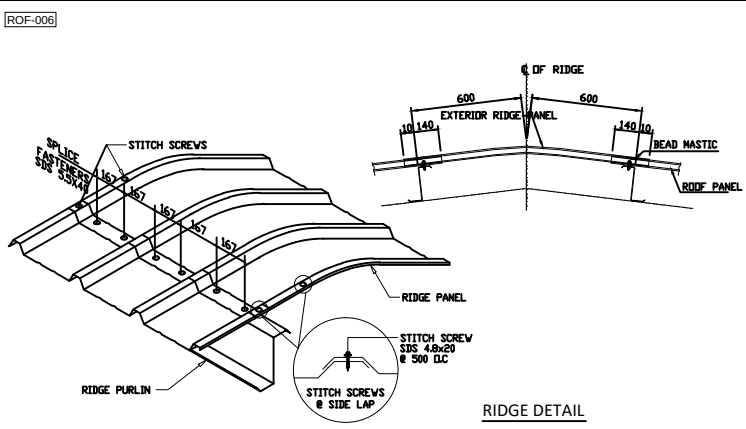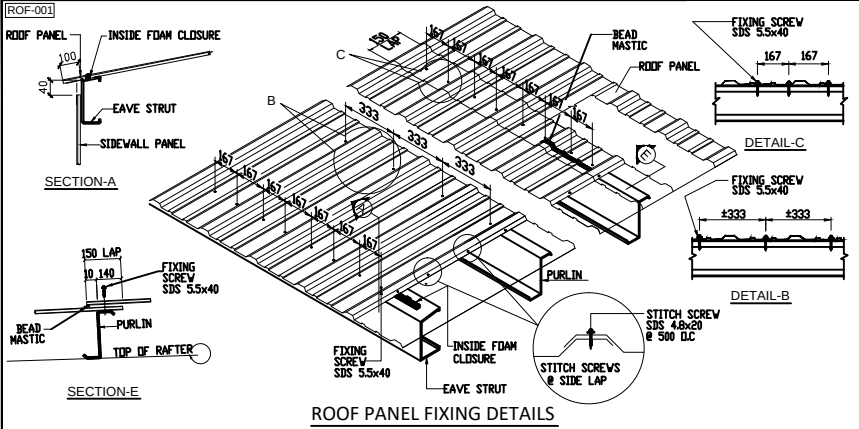


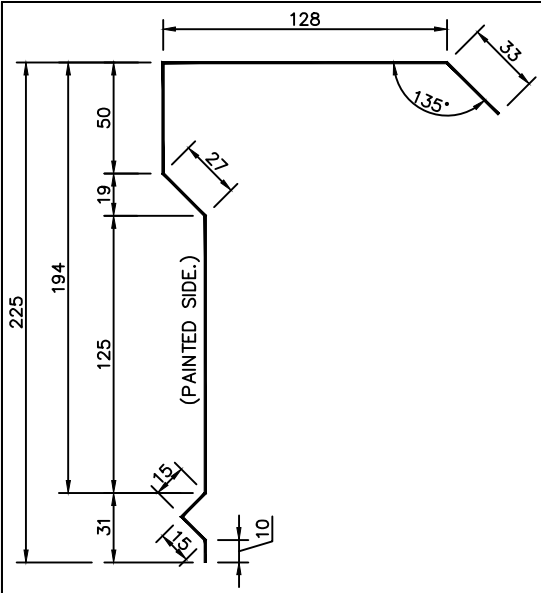


GABLE TRIM (GT)

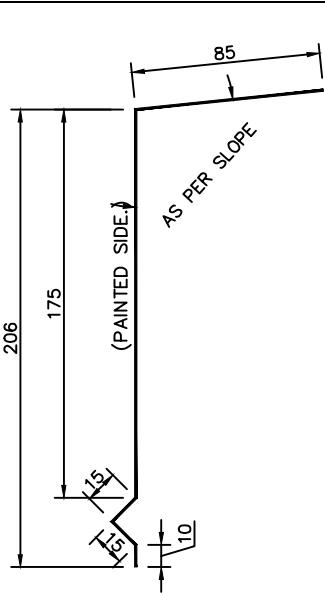


EAVE TRIM (ET)

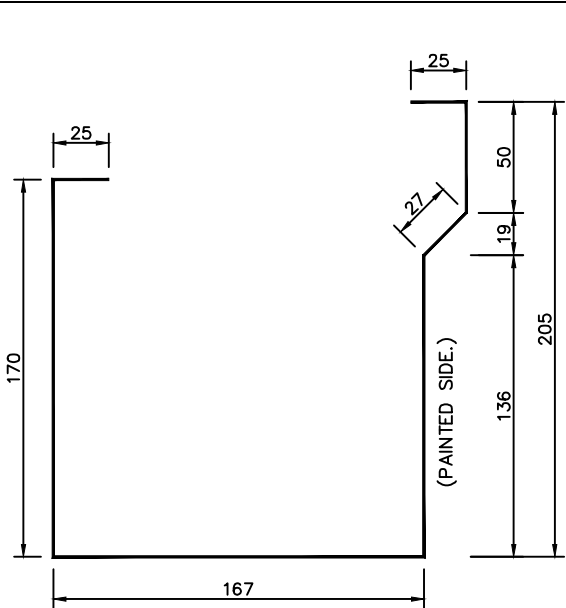


EAVE GUTTER (EG)

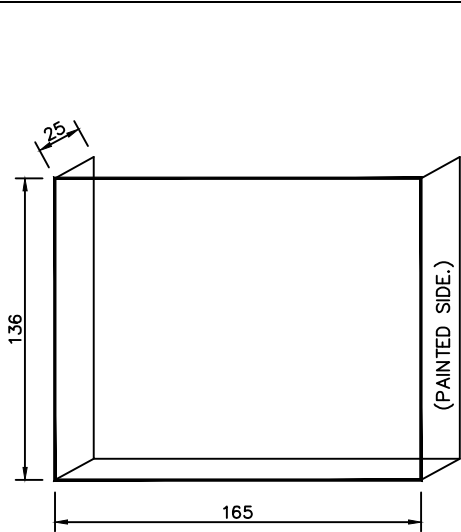


EAVE GUTTER END CLOUSURE (EC) L AND R

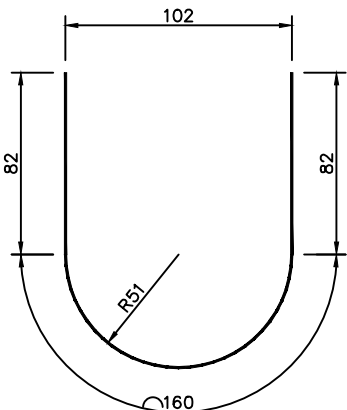


STRAP
1.5 mm G.I

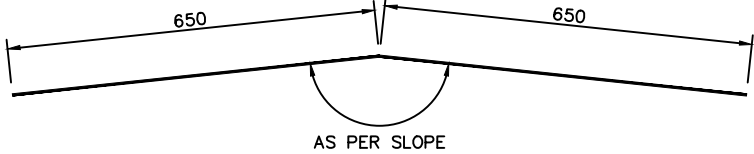


RIDGE PANLE (RP)

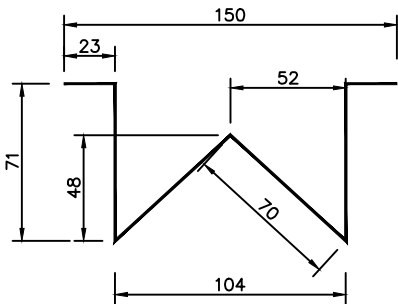

SADDLE CLIP
1.5 mm G.I

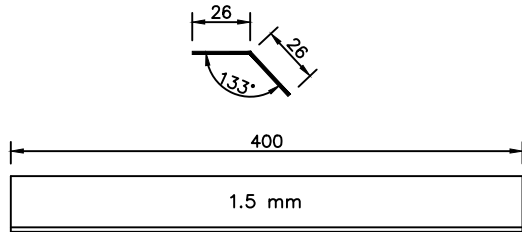


EAVE GUTTER STRAP (EGS)

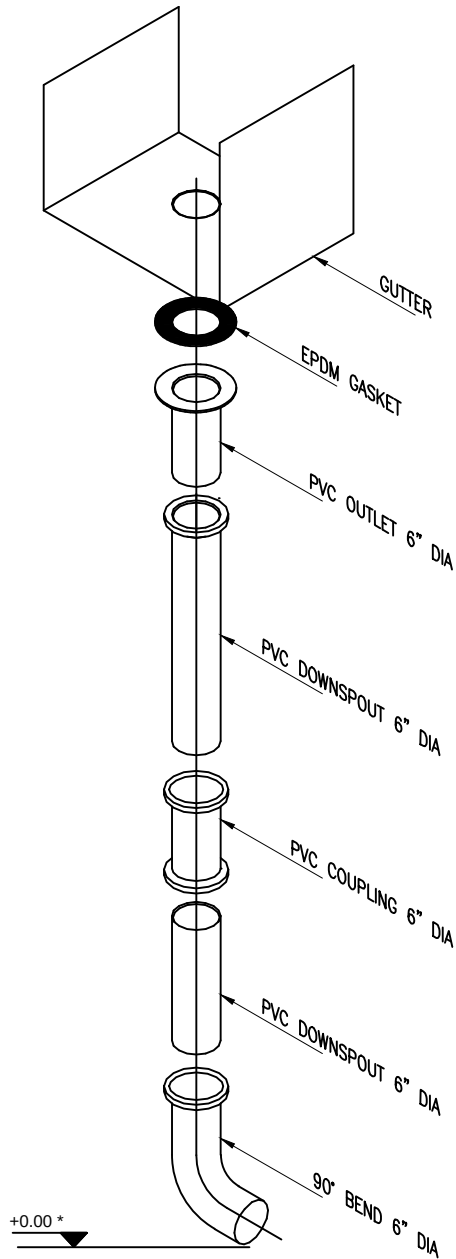


PVC DOWN SPOUT FIXING DETAIL

00	08-11-22	ISSUED FOR IFC	D.A	UBD	UBD
REV.	DATE	DESCRIPTION	DRWN BY	CHK BY	APR BY
MAIMAAR  MAIMAAR STEEL Pvt.Ltd 105, Raiwind Road, Thokar Niaz Baig ,Lahore, Pakistan E-mail: nasir.abbas@maimaargroup.com E-mail: maimaar.steel@gmail.com Website: www.maimaargroup.com E-mail: nasir.abbas@maimaargroup.com Mob-1 : +(92-300) 807 4017 ,+(92-333) 807 1115					
JOB NO./QUOTE NO.		-		BLDG #.	01
PROJECT NAME		MAIMAAR FACTORY			
CUSTOMER					
JOBSITE LOCATION					
TRIME					DWG. NO.
					01

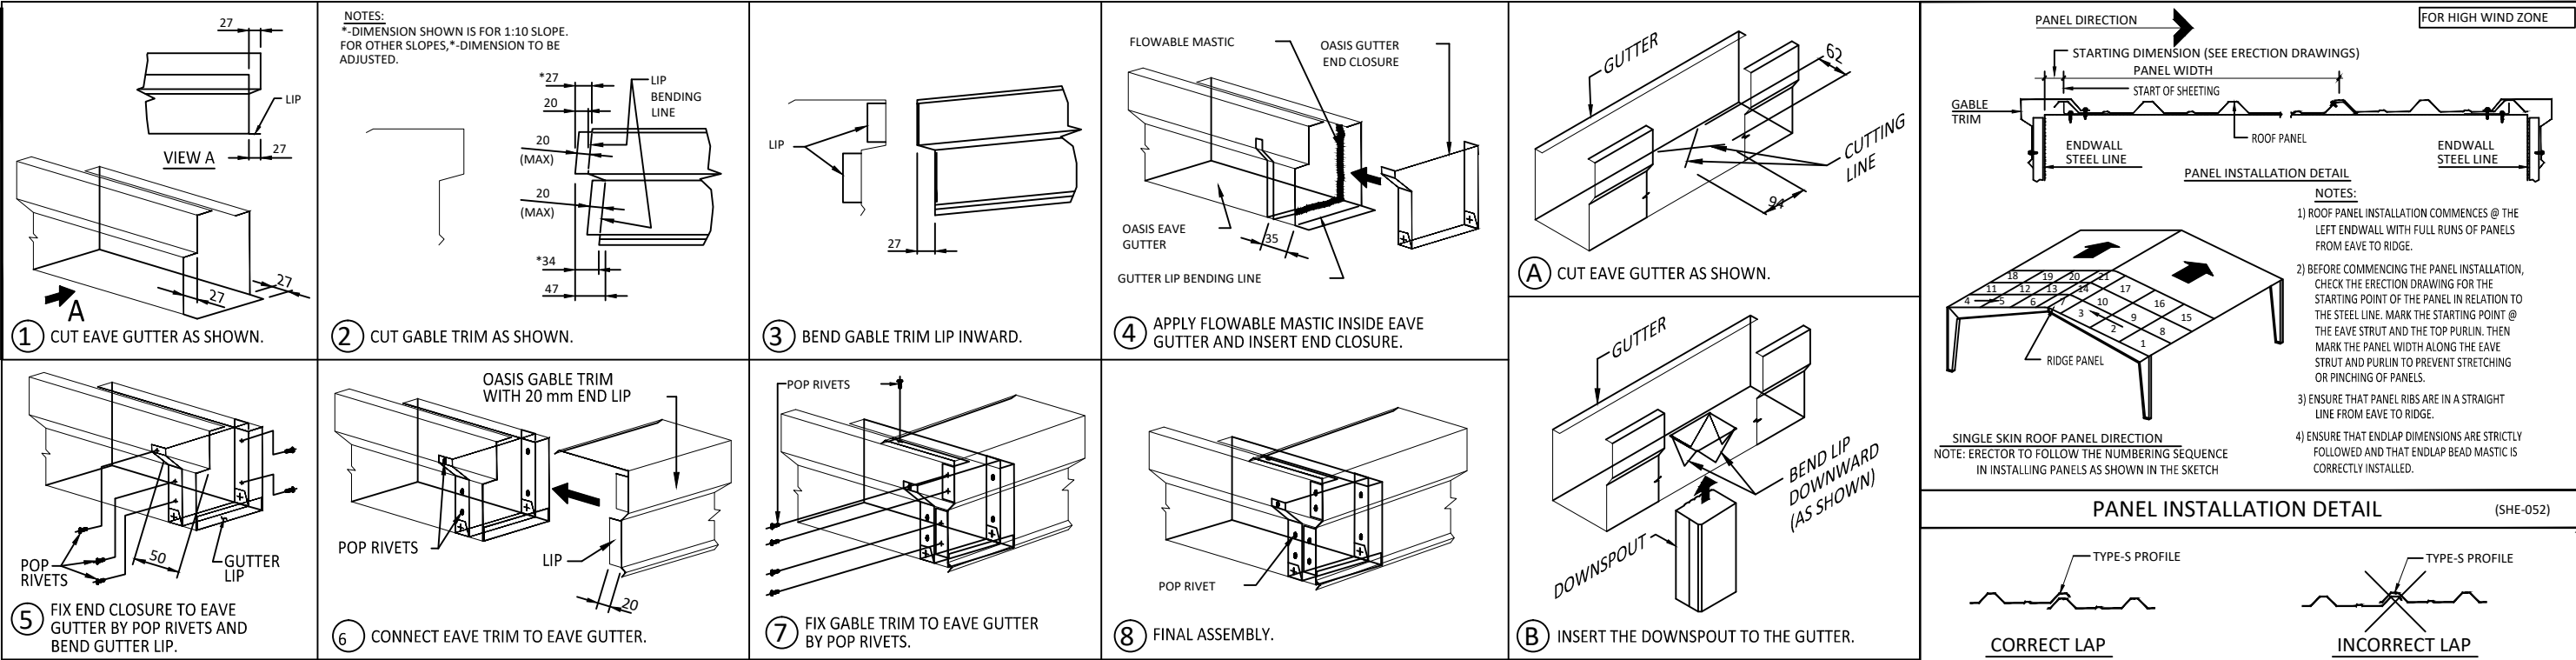

EAVE GUTTER & GABLE TRIM CONNECTION DETAIL **GUTTER & DOWNSPOUT CONNECTION DETAIL**

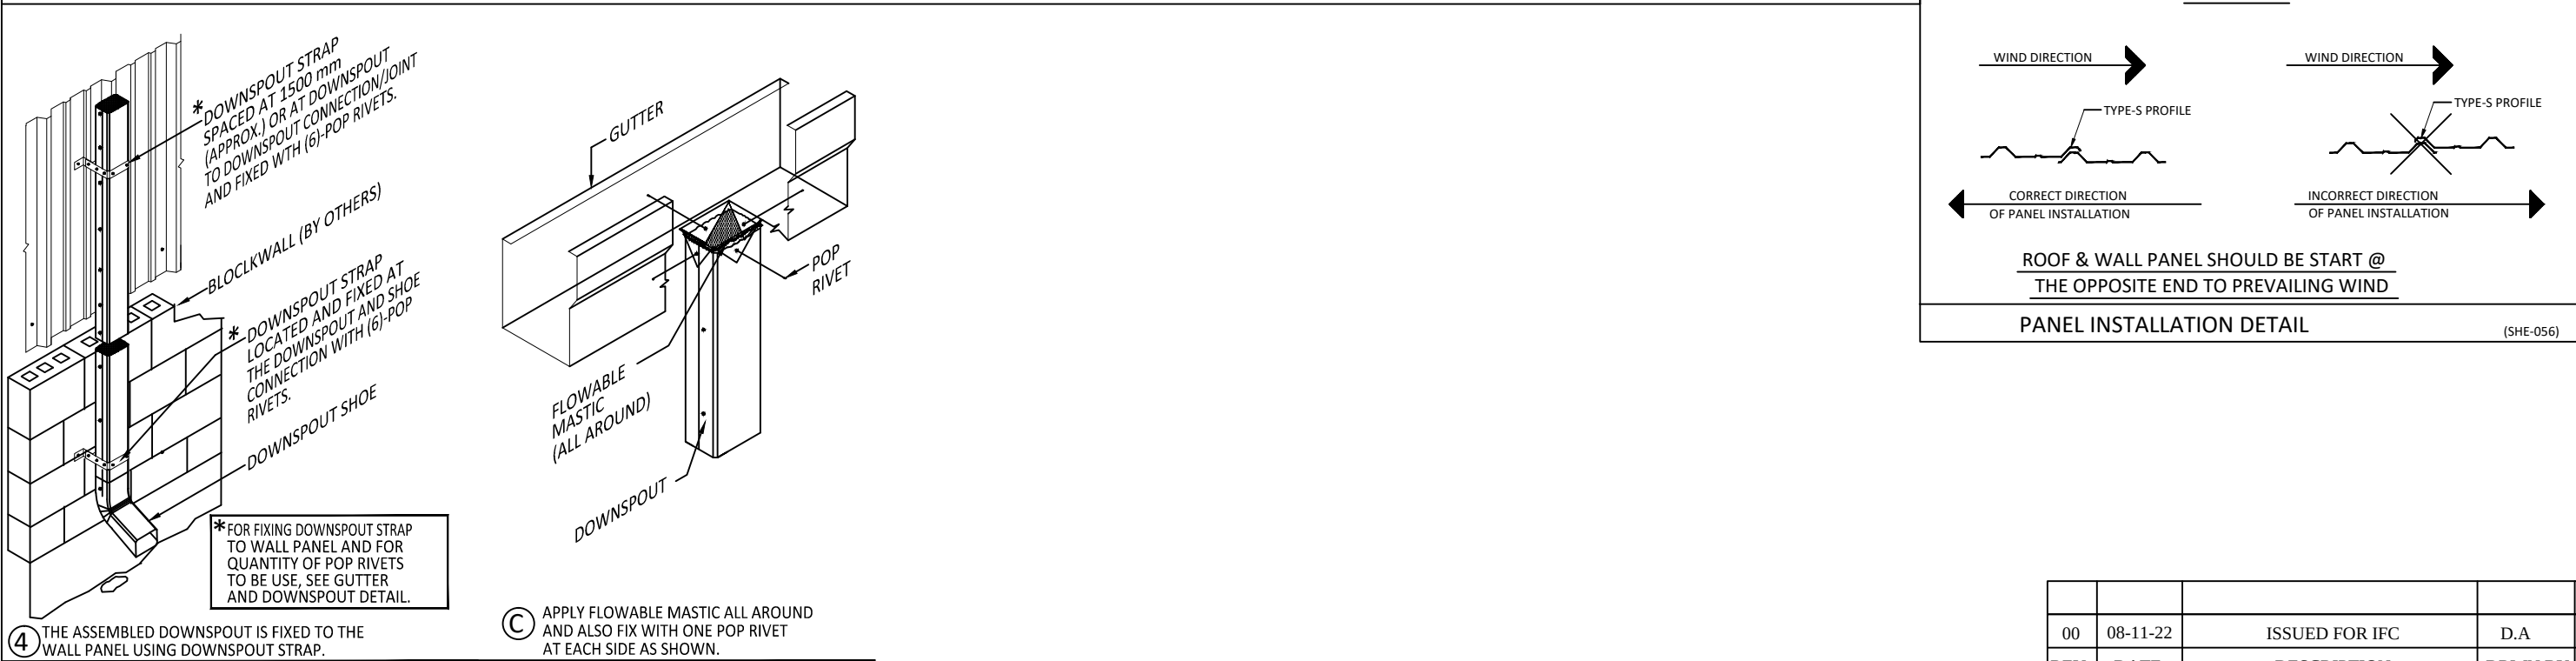

DOWNSPOUTS CONNECTION DETAIL

	SELF DRILLING FASTENERS SCHEDULE @ WALL		TEMPCON PANEL FASTENERS SCHEDULE @ WALL			
	FASTENER TYPE	USAGE	FASTENER PART NUMBER	FASTENER TYPE	USAGE	FASTENER PART NUMBER
						CARBON STEEL "CS"
FIXING SCREWS	WALL SCREW (WS)		CS-5.5x25			
			CS-5.5x45			
STITCH SCREWS	WALL SCREW (WS)		CS-4.8x16			
FIXING SCREWS	GENERAL SCREW (GS)		CS-5.5x25			
			CS-5.5x32			