



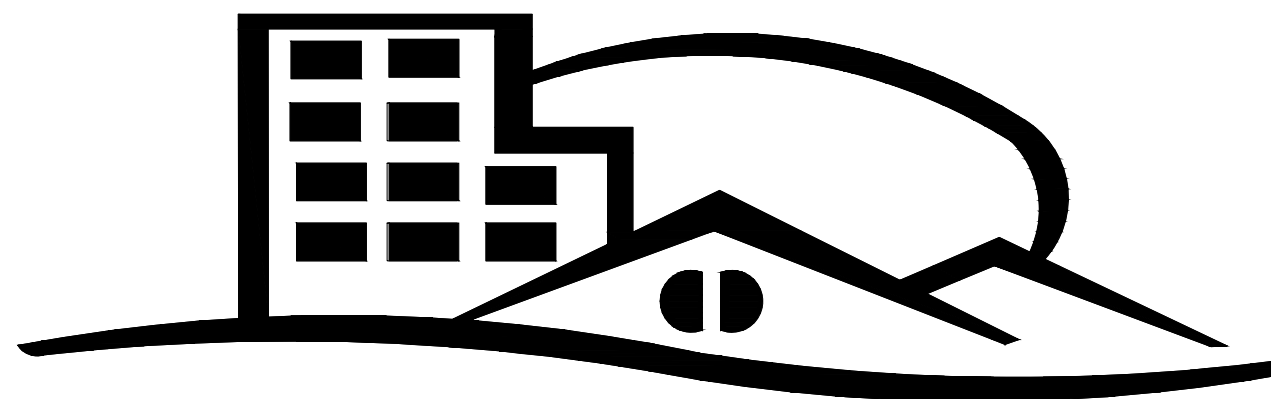


PROPOSAL NO.	MSPL-108
JOB NO.	MSPL-169

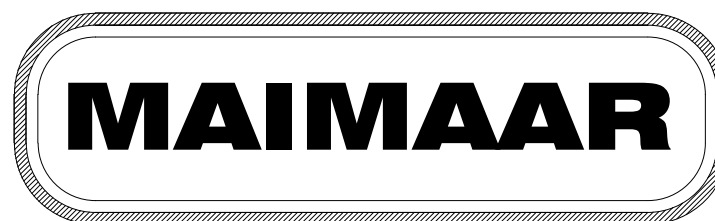

(MAIMAAR STEEL Pvt.Ltd)

238, First Floor Lalazar Commercial Area
Raiwind Road, Thokar Niaz Baig ,Lahore, Pakistan
E-mail: nasir.abbas@maimaargroup.com
E-mail: maimaar.steel@gmail.com

Website: www.maimaargroup.com
E-mail: nasir.abbas@maimaargroup.com
Mob-1 : +(92-300) 807 4017 ,+(92-333) 807 1115

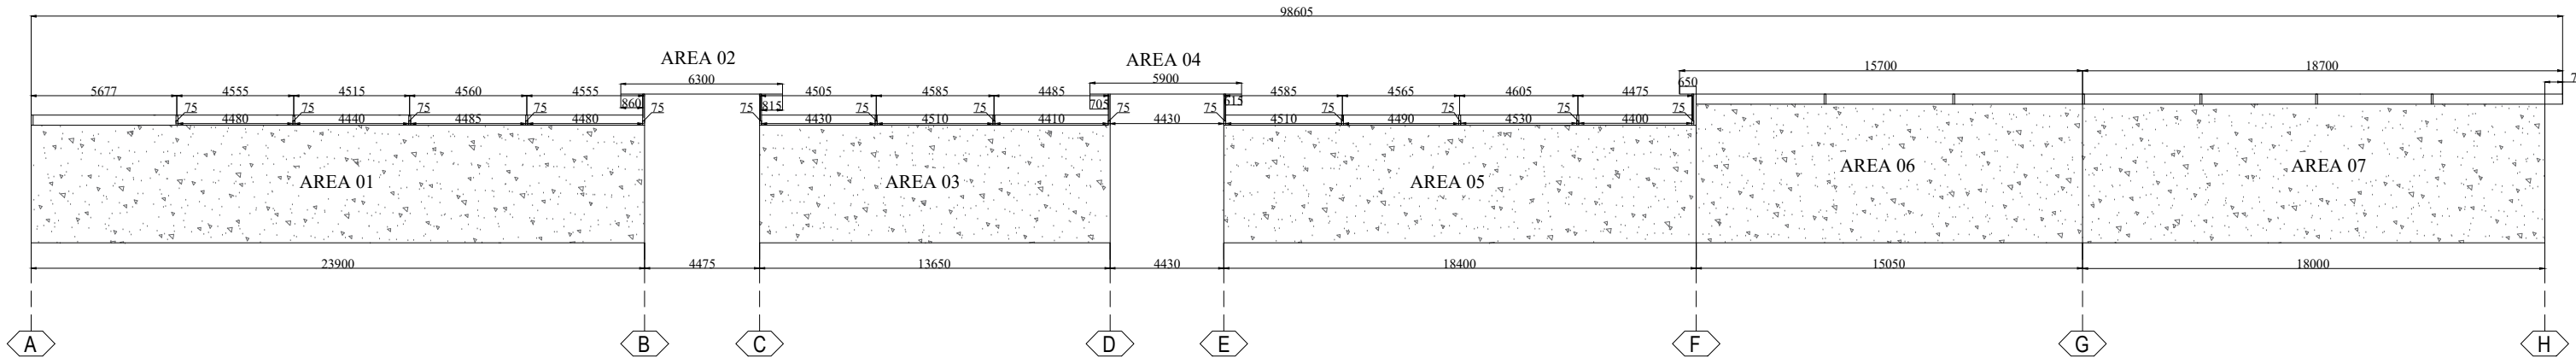

FOR APPROVAL :

IN ORDER TO SCHEDULE THIS PROJECT IN AN EFFICIENT MANNER , KINDLY RETURN THESE DRAWINGS WITH YOUR ANY CHANGES MADE AFTER THE COMMENTS MARKED IN RED APPROVAL OF THESE DRAWINGS MAY DELAY THE FABRICATION SCHEDULE AND SUBSEQUENTLY THE DELIVERY OF THE BUILDING. PLEASE TICK MARK ONLY ONE OF THE FOLLOWING

☐ " APPROVED AS IS "

☐ " APPROVED AS NOTED "

☐ " RESUBMIT AS NOTED "

APPROVE : _____

SIGNATURE: _____

DATE : _____

REV	DATE	DESCRIPTION	DRAWN BY	CHK BY	APR BY
00	15-05-25	ISSUED FOR APPROVAL	I.U	M.B	NAS

MAIMAAR

MAIMAAR STEEL Pvt.Ltd

238, Raiwind Road, Thokar Niaz Baig, Lahore, Pakistan

E-mail: nasir.abbas@maimaargroup.com

E-mail: maimaar.steel@gmail.com

Website: www.maimaargroup.com




E-mail: info@maimaargroup.com

Mob-1 : +(92-300) 807 4017 ,+(92-333) 807 1115

JOB NO./QUOTE NO.	MSPL-169	BUILDING #	01
PROJECT NAME	SUPPLY & INSTALLATION OF ROOF SHEETING		
CUSTOMER	PAECO		
JOB SITE LOCATION	KASUR		
FRONT ELEVATION			DWG NO.
			01

NOTE:-
IF THE SKYLIGHT LOCATION NEEDS TO BE CHANGED, IT SHOULD BE DONE *BEFORE ERECTION*; OTHERWISE MAIMAAR STEEL GROUP WILL NOT BE RESPONSIBLE.

FRONT ELEVATION

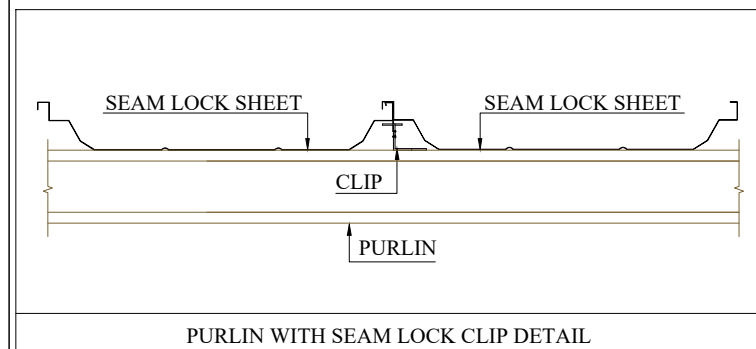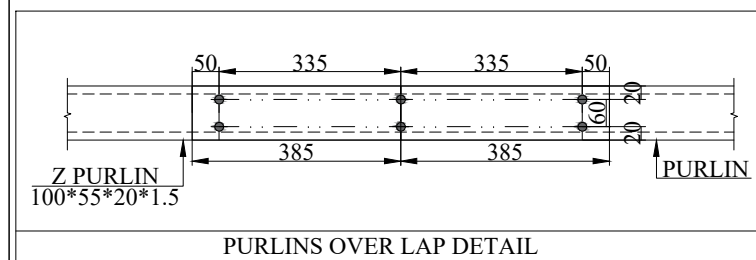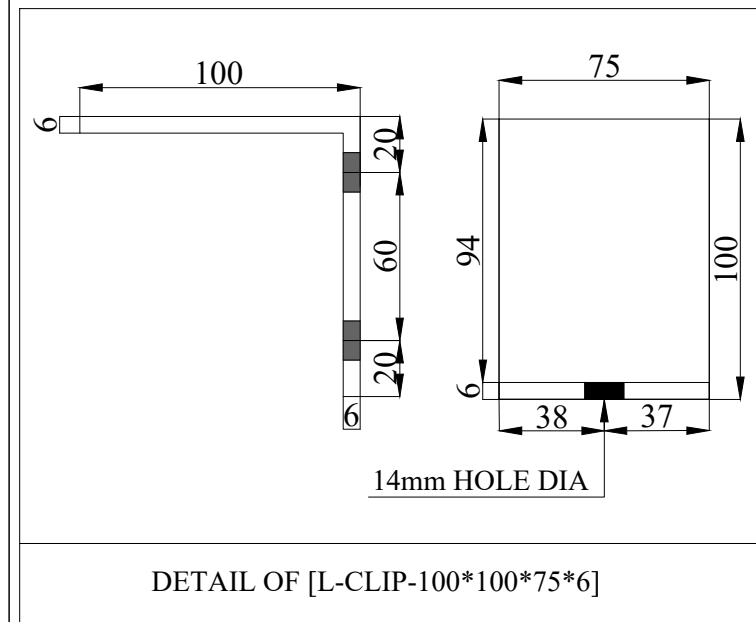

FOR APPROVAL :

IN ORDER TO SCHEDULE THIS PROJECT
IN AN EFFICIENT MANNER , KINDLY
RETURN THESE DRAWINGS WITH YOUR
ANY CHANGES MADE AFTER THE
COMMENTS MARKED IN RED

APPROVAL OF THESE DRAWINGS MAY
DELAY THE FABRICATION SCHEDULE AND
SUBSEQUENTLY THE DELIVERY OF THE
BUILDING.

PLEASE TICK MARK ONLY ONE OF THE FOLLOWING

☐	" APPROVED AS IS "
☐	" APPROVED AS NOTED "
☐	" RESUBMIT AS NOTED "

APPROVE : _____

SIGNATURE: _____


DATE : _____

REV	DATE	DESCRIPTION	DRAWN BY	CHK BY	APR BY
00	15-05-25	ISSUED FOR APPROVAL	I.U	M.B	NAS





MAIMAAR STEEL Pvt.Ltd
238, Raiwind Road, Thokar Niaz Baig, Lahore, Pakistan
E-mail: nasir.abbas@maimaargroup.com
E-mail: maimaar.steel@gmail.com
Website: www.maimaargroup.com
E-mail: info@maimaargroup.com
Mob-1 : +(92-300) 807 4017 , +(92-333) 807 1115

JOB NO./QUOTE NO.	MSPL-169	BUILDING #	01
PROJECT NAME	SUPPLY & INSTALLATION OF ROOF SHEETING		
CUSTOMER	PAECO		
JOB SITE LOCATION	KASUR		
ROOF FRAMING (AREA 01)			DWG NO.
			02

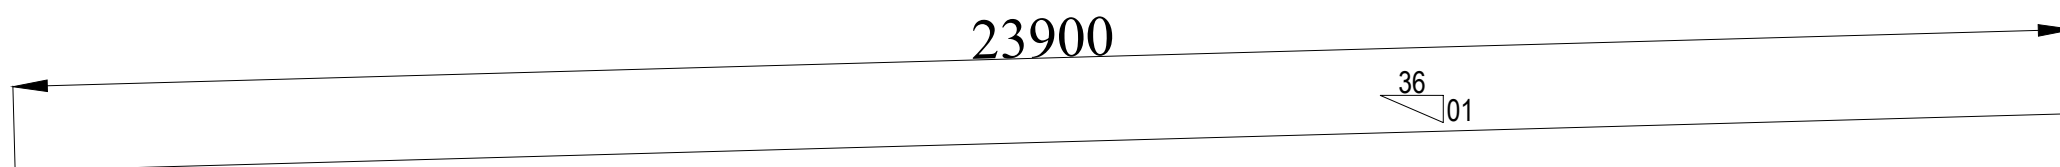

ROOF FRAMING (AREA 01)

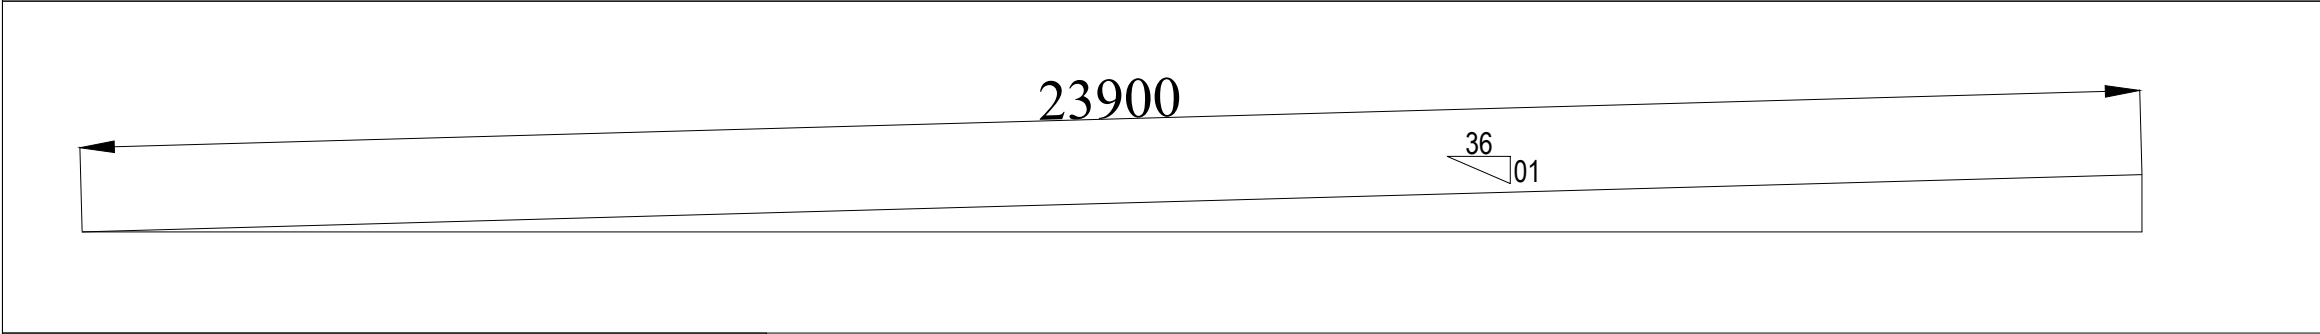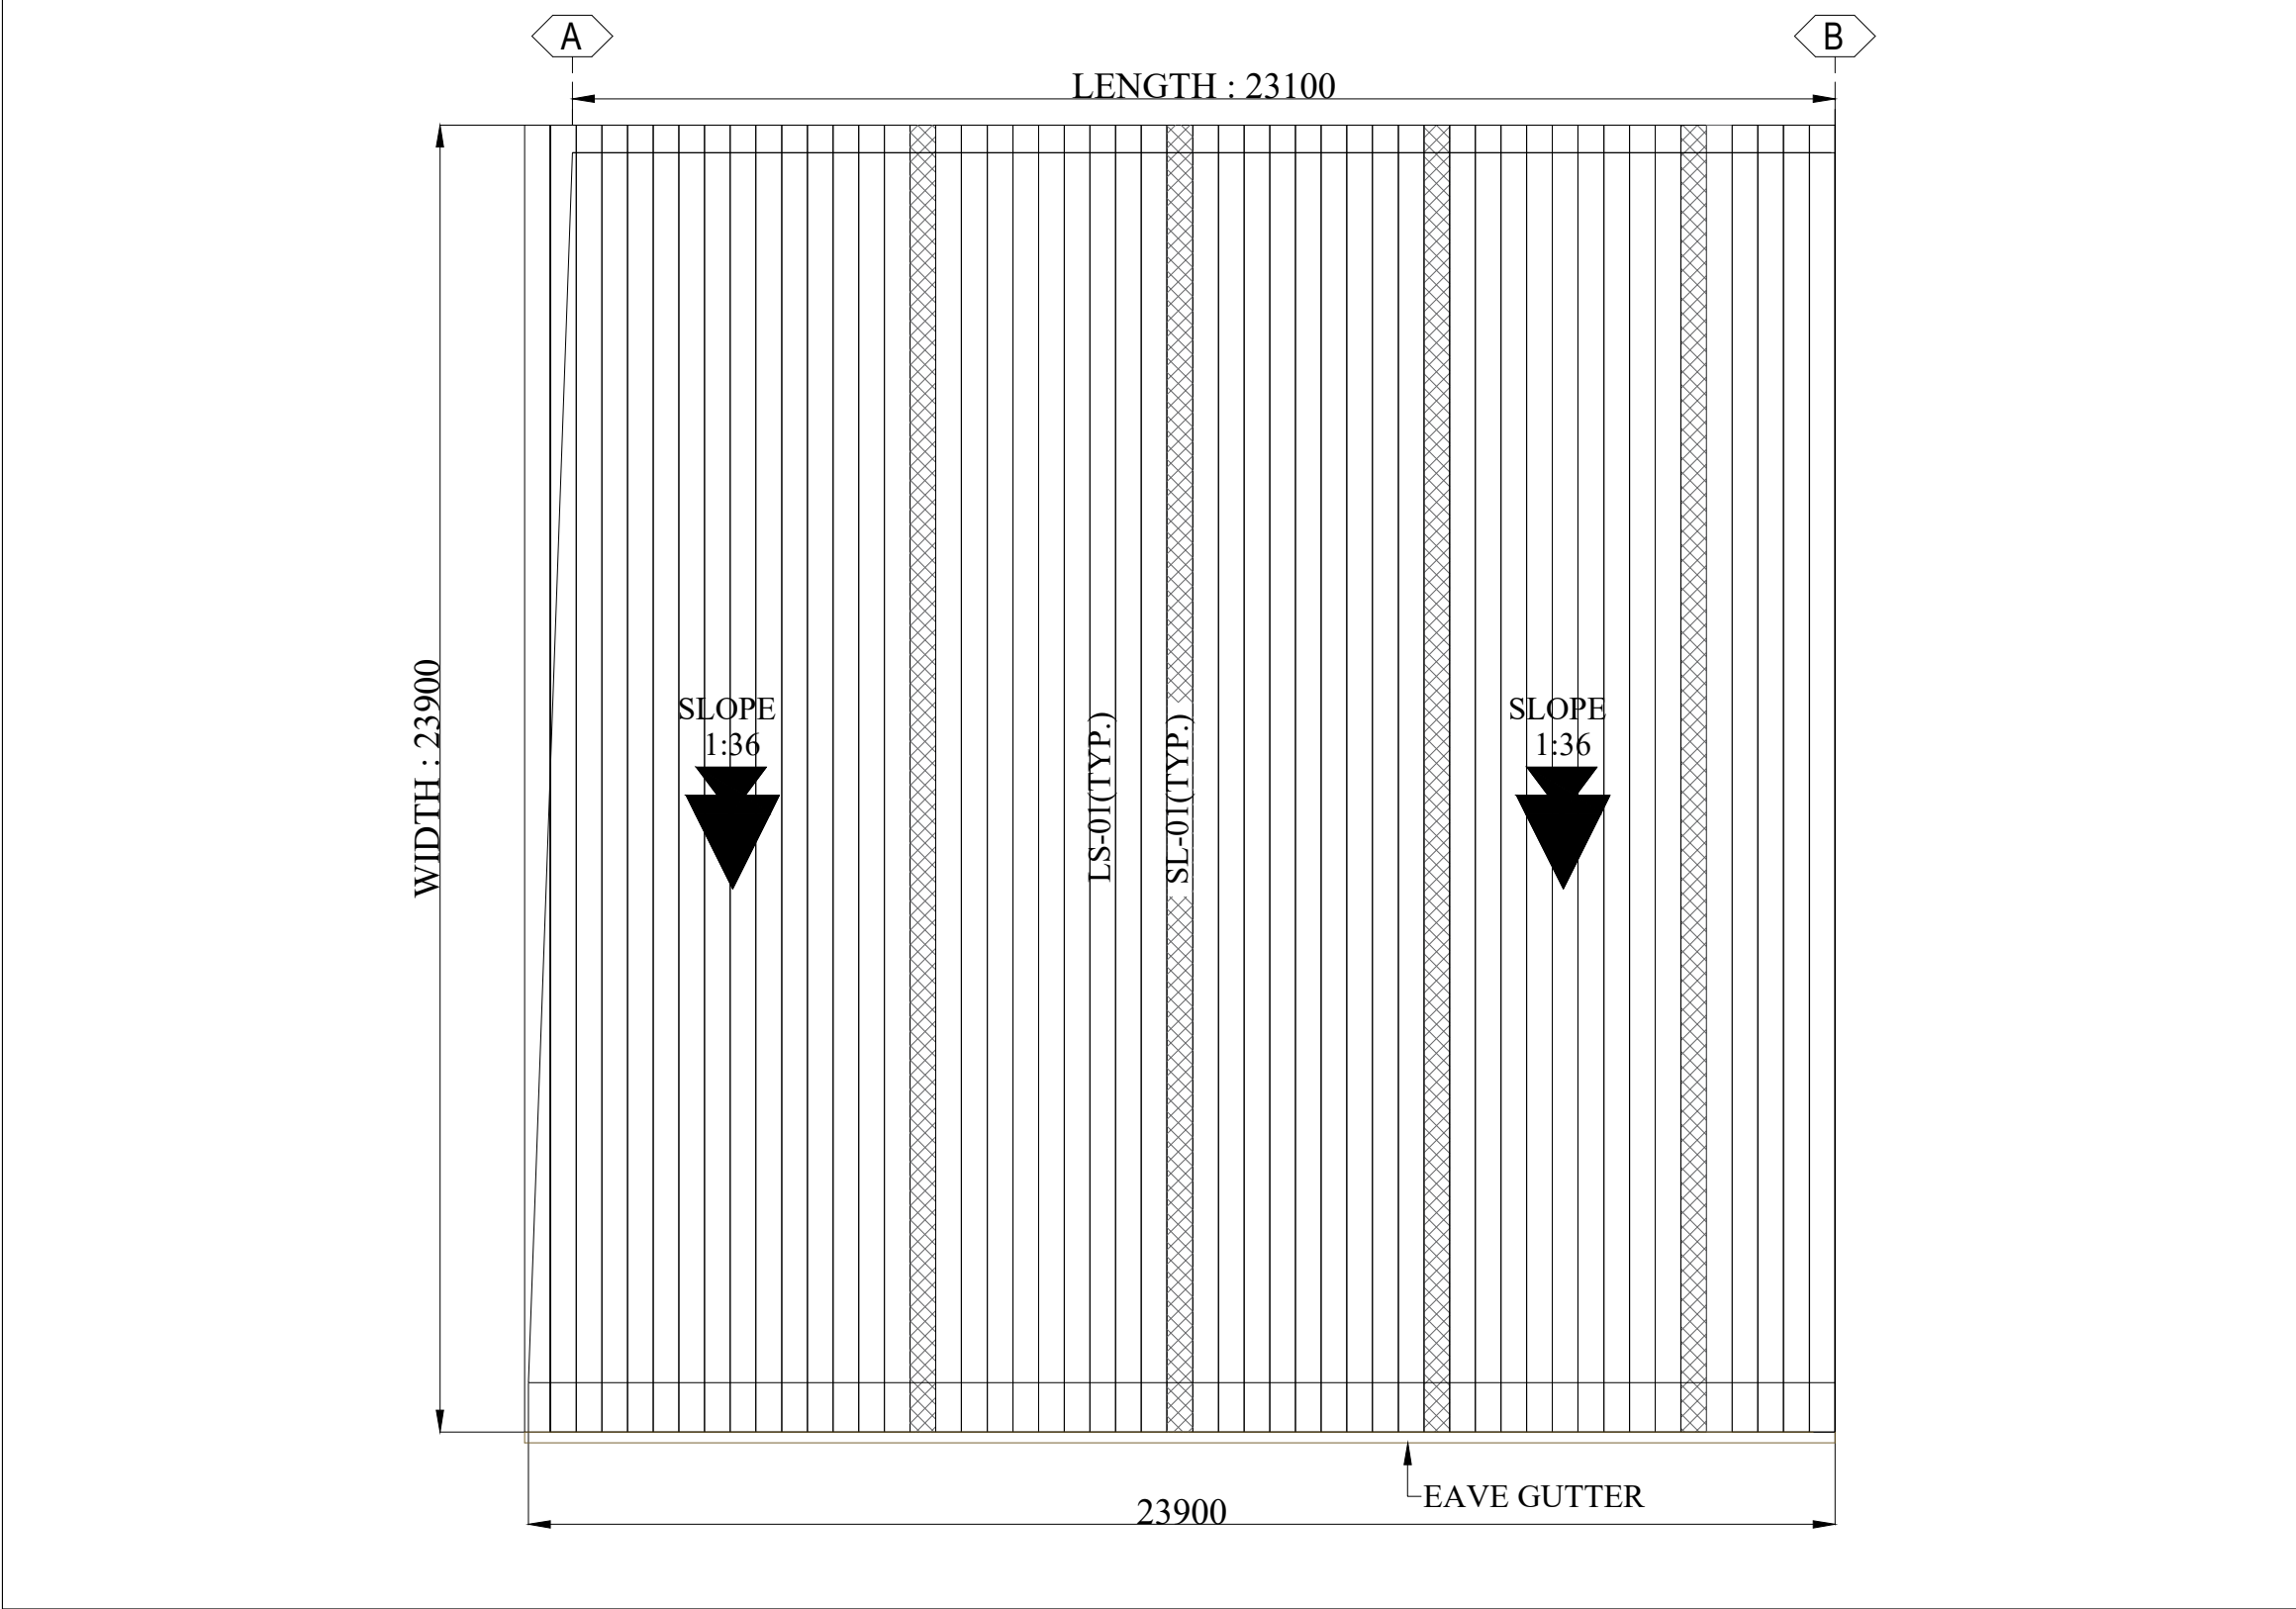

LOCKSEAM SHEETING AREA - 01				
DESCRIPTIONS	PART	LENGTH (MM)	WIDTH (MM)	QUANTITY
LOCKSEAM SHEETING	LS-01	23,900	470	47
SKY LIGHTS	SL-01	23,900	470	4

ROOF SHEETING
(AREA 01)

Length = (3M)

Thickness = 1.2mm (PPG.L)

8 NOS.

Paint Side = ▼

COLOR: OFFWHITE

EAVE GUTTER

LOCK SEAM SHEET PROFILE

SKYLIGHT PROFILE : THK. 2mm

FOR APPROVAL :

IN ORDER TO SCHEDULE THIS PROJECT IN AN EFFICIENT MANNER , KINDLY RETURN THESE DRAWINGS WITH YOUR ANY CHANGES MADE AFTER THE COMMENTS MARKED IN RED APPROVAL OF THESE DRAWINGS MAY DELAY THE FABRICATION SCHEDULE AND SUBSEQUENTLY THE DELIVERY OF THE BUILDING. PLEASE TICK MARK ONLY ONE OF THE FOLLOWING

☐ " APPROVED AS IS "

☐ " APPROVED AS NOTED "

☐ " RESUBMIT AS NOTED "

APPROVE : _____

SIGNATURE: _____



DATE : _____

REV	DATE	DESCRIPTION	DRAWN BY	CHK BY	APR BY
00	15-05-25	ISSUED FOR APPROVAL	I.U	M.B	NAS


MAIMAAR

MAIMAAR STEEL Pvt.Ltd
238, Raiwind Road, Thokar Niaz Baig, Lahore, Pakistan
E-mail: nasir.abbas@maimaargroup.com
E-mail: maimaar.steel@gmail.com
Website: www.maimaargroup.com
E-mail: info@maimaargroup.com
Mob-1 : +(92-300) 807 4017 ,+(92-333) 807 1115


JOB NO./QUOTE NO.	MSPL-169	BUILDING #	01
PROJECT NAME	SUPPLY & INSTALLATION OF ROOF SHEETING		
CUSTOMER	PAECO		
JOB SITE LOCATION	KASUR		
ROOF SHEETING (AREA 01)			
DWG NO. 03			

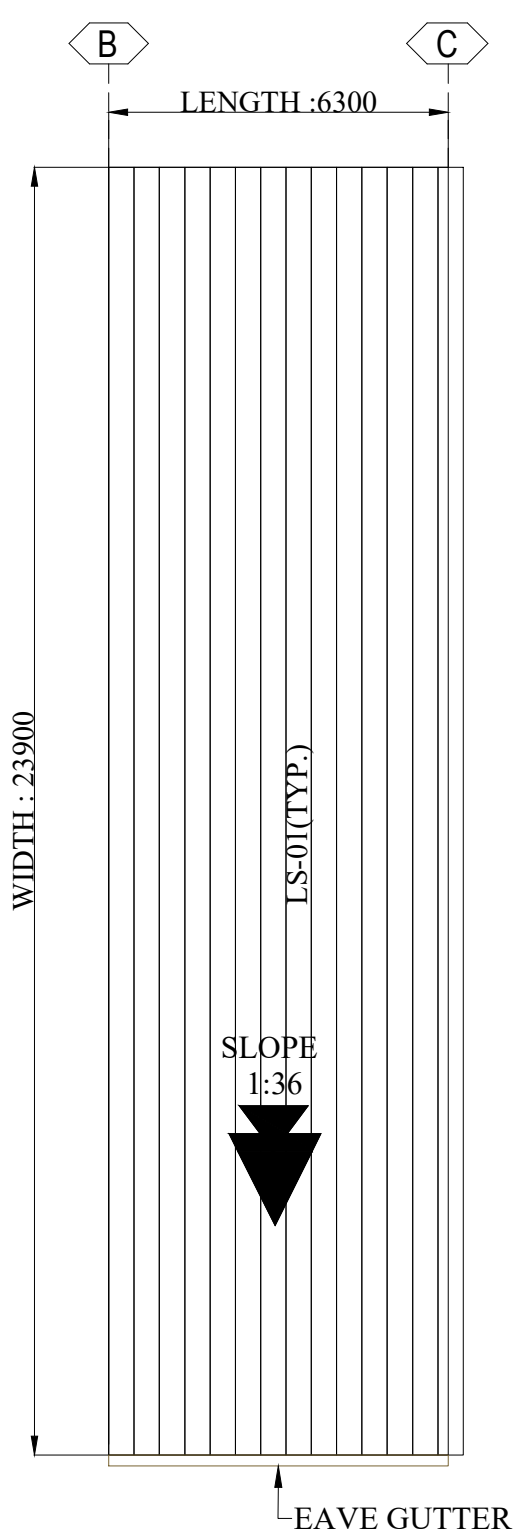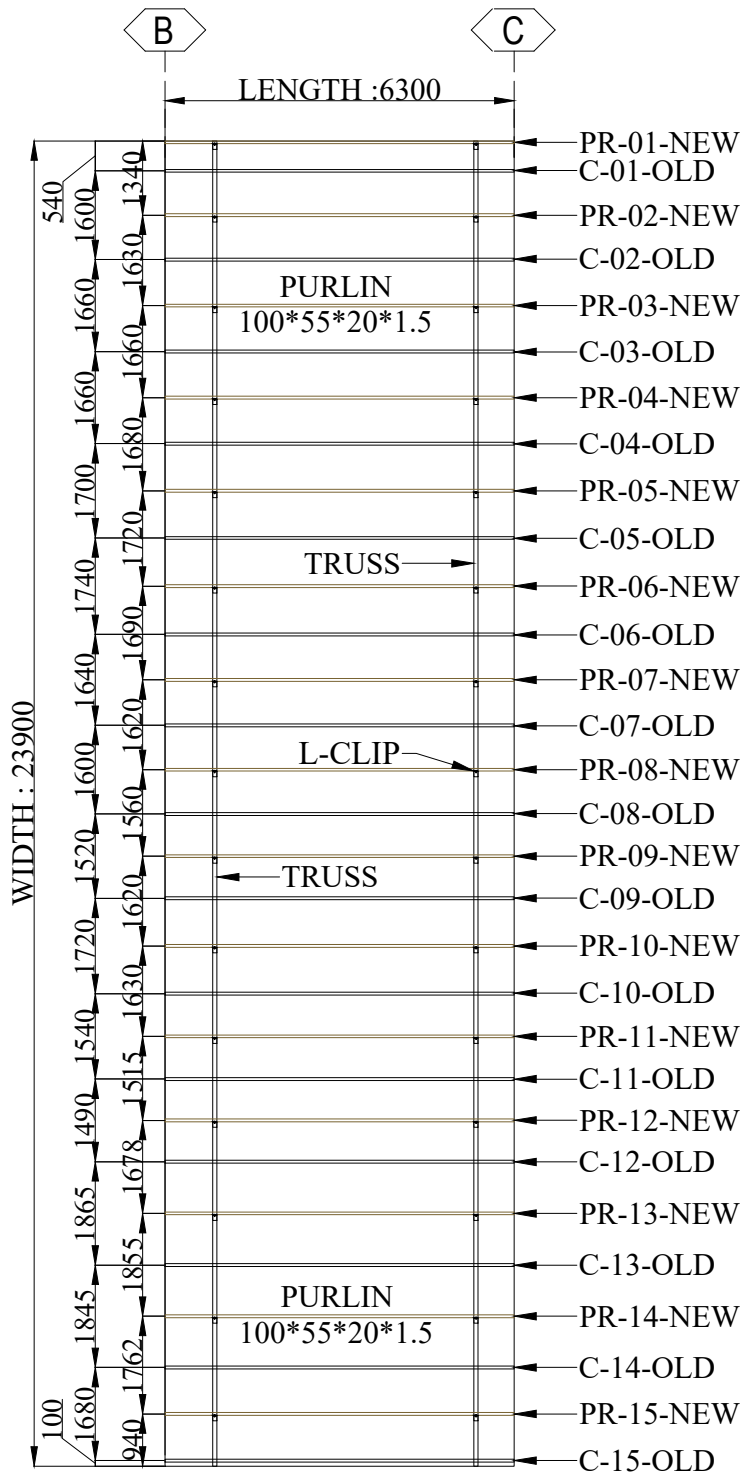

Length = (3M)
3 NOS.
Thickness = 1.2mm (PPG.L)
Paint Side = ▼
COLOR: OFFWHITE

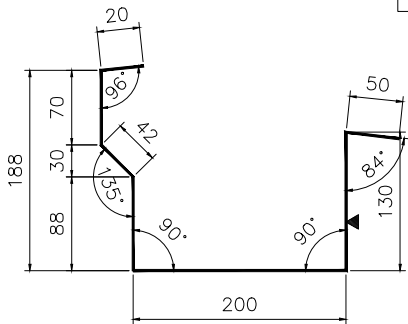

EAVE GUTTER

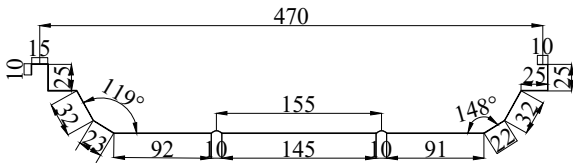

LOCK SEAM SHEET PROFILE

FOR APPROVAL :
IN ORDER TO SCHEDULE THIS PROJECT IN AN EFFICIENT MANNER , KINDLY RETURN THESE DRAWINGS WITH YOUR COMMENTS MARKED IN RED
APPROVAL OF THESE DRAWINGS MAY DELAY THE FABRICATION SCHEDULE AND SUBSEQUENTLY THE DELIVERY OF THE BUILDING.
PLEASE TICK MARK ONLY ONE OF THE FOLLOWING

☐ " APPROVED AS IS "
☐ " APPROVED AS NOTED "
☐ " RESUBMIT AS NOTED "

APPROVE : _____
SIGNATURE: _____
DATE : _____


REV	DATE	DESCRIPTION	DRAWN BY	CHK BY	APR BY
00	15-05-25	ISSUED FOR APPROVAL	I.U	M.B	NAS



JOB NO./QUOTE NO.	MSPL-169	BUILDING #	01
PROJECT NAME	SUPPLY & INSTALLATION OF ROOF SHEETING		
CUSTOMER	PAECO		
JOB SITE LOCATION	KASUR		



ROOF FRAMING &
SHEETING (AREA 02)

DWG NO.
04

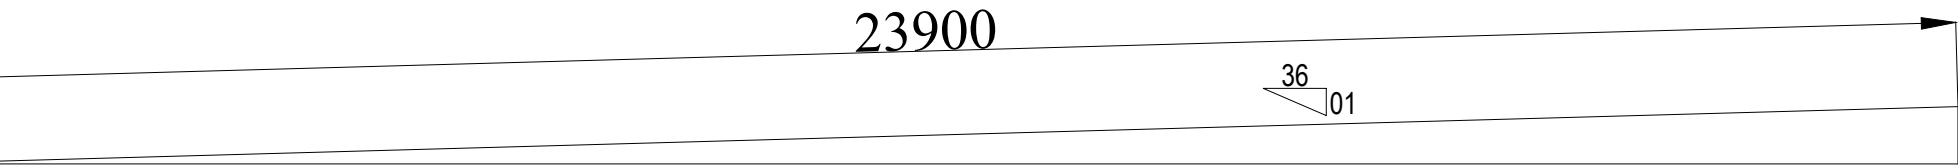


LOCKSEAM SHEETING AREA - 02				
DESCRIPTIONS	PART	LENGTH (MM)	WIDTH (MM)	QUANTITY
LOCKSEAM SHEETING	LS-01	23,900	470	14


ROOF FRAMING & SHEETING
(AREA 02)

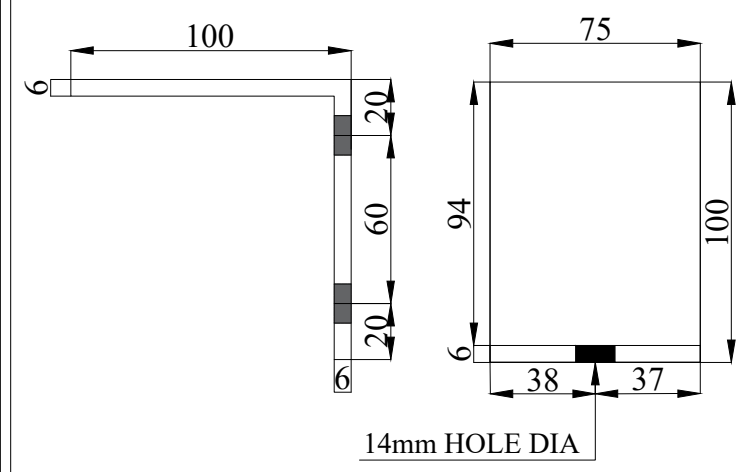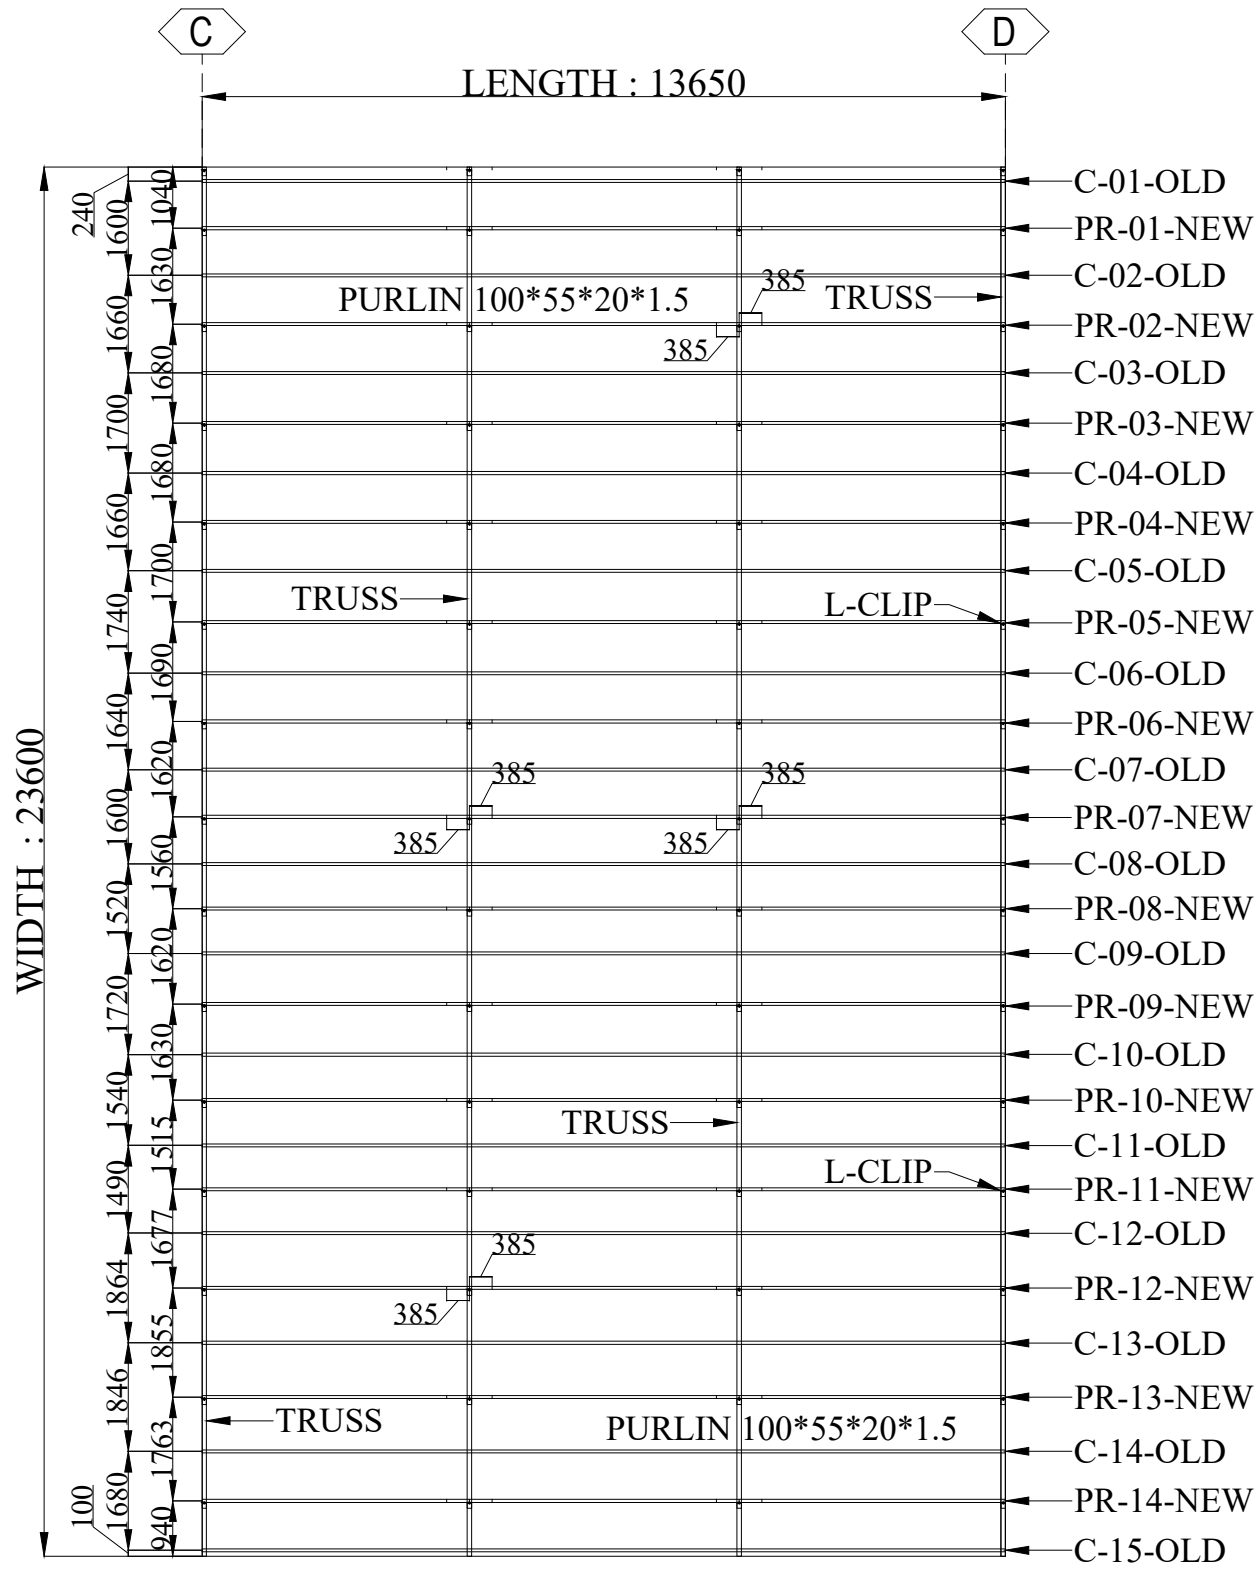

DETAIL OF [L-CLIP-100*100*75*6]

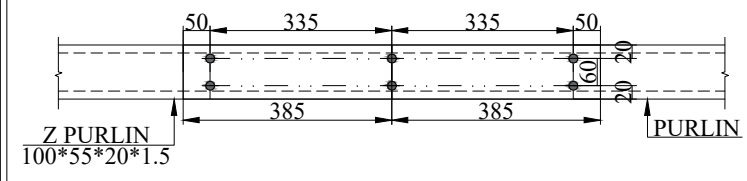

PURLINS OVER LAP DETAIL

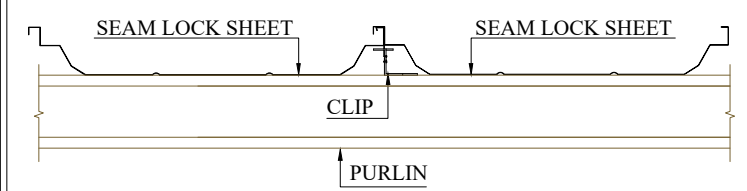

PURLIN WITH SEAM LOCK CLIP DETAIL

FOR APPROVAL :

IN ORDER TO SCHEDULE THIS PROJECT IN AN EFFICIENT MANNER , KINDLY RETURN THESE DRAWINGS WITH YOUR COMMENTS MARKED IN RED

APPROVAL OF THESE DRAWINGS MAY DELAY THE FABRICATION SCHEDULE AND SUBSEQUENTLY THE DELIVERY OF THE BUILDING.


PLEASE TICK MARK ONLY ONE OF THE FOLLOWING

☐ " APPROVED AS IS "
☐ " APPROVED AS NOTED "
☐ " RESUBMIT AS NOTED "

APPROVE : _____



SIGNATURE: _____

DATE : _____

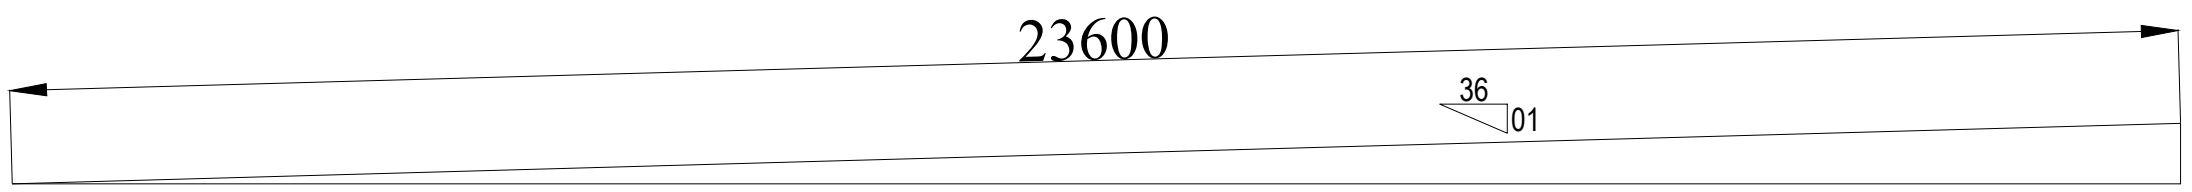

ROOF FRAMING
(AREA 03)

REV	DATE	DESCRIPTION	DRAWN BY	CHK BY	APR BY
00	15-05-25	ISSUED FOR APPROVAL	I.U	M.B	NAS
MAIMAAR MAIMAAR STEEL Pvt.Ltd 238, Raiwind Road, Thokar Niaz Baig, Lahore, Pakistan E-mail: nasir.abbas@maimaargroup.com E-mail: maimaar.steel@gmail.com Website: www.maimaargroup.com E-mail: info@maimaargroup.com Mob-1 : +(92-300) 807 4017 ,+(92-333) 807 1115					
JOB NO./QUOTE NO.		MSPL-169		BUILDING #	01
PROJECT NAME		SUPPLY & INSTALLATION OF ROOF SHEETING			
CUSTOMER		PAECO			
JOB SITE LOCATION		KASUR			
ROOF FRAMING (AREA 03)					DWG NO.
					05

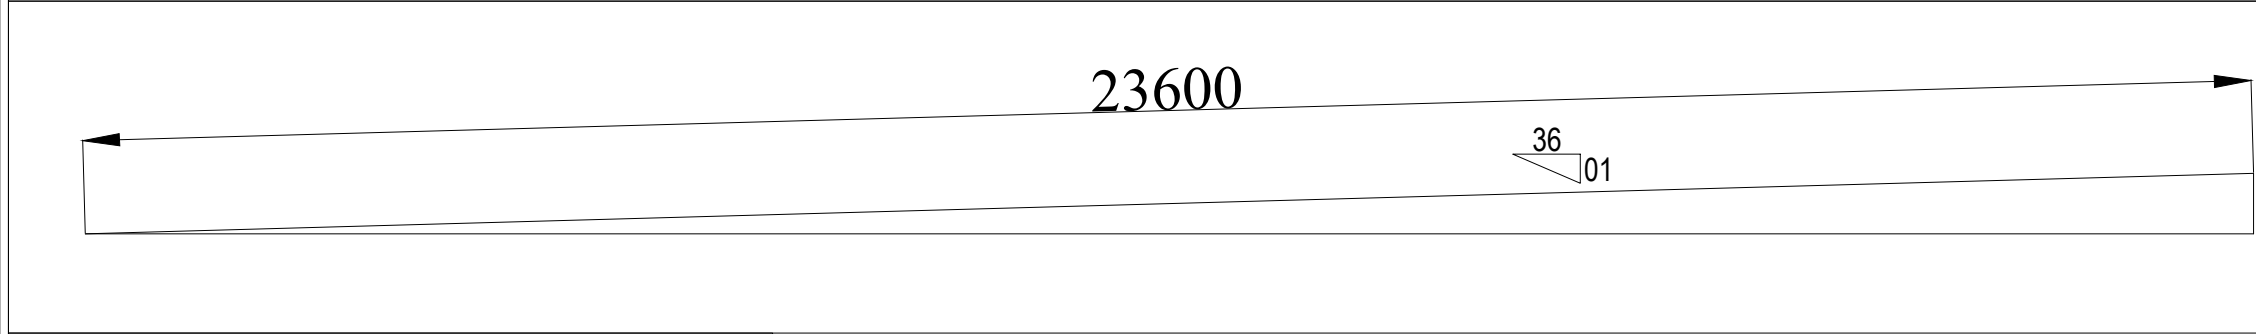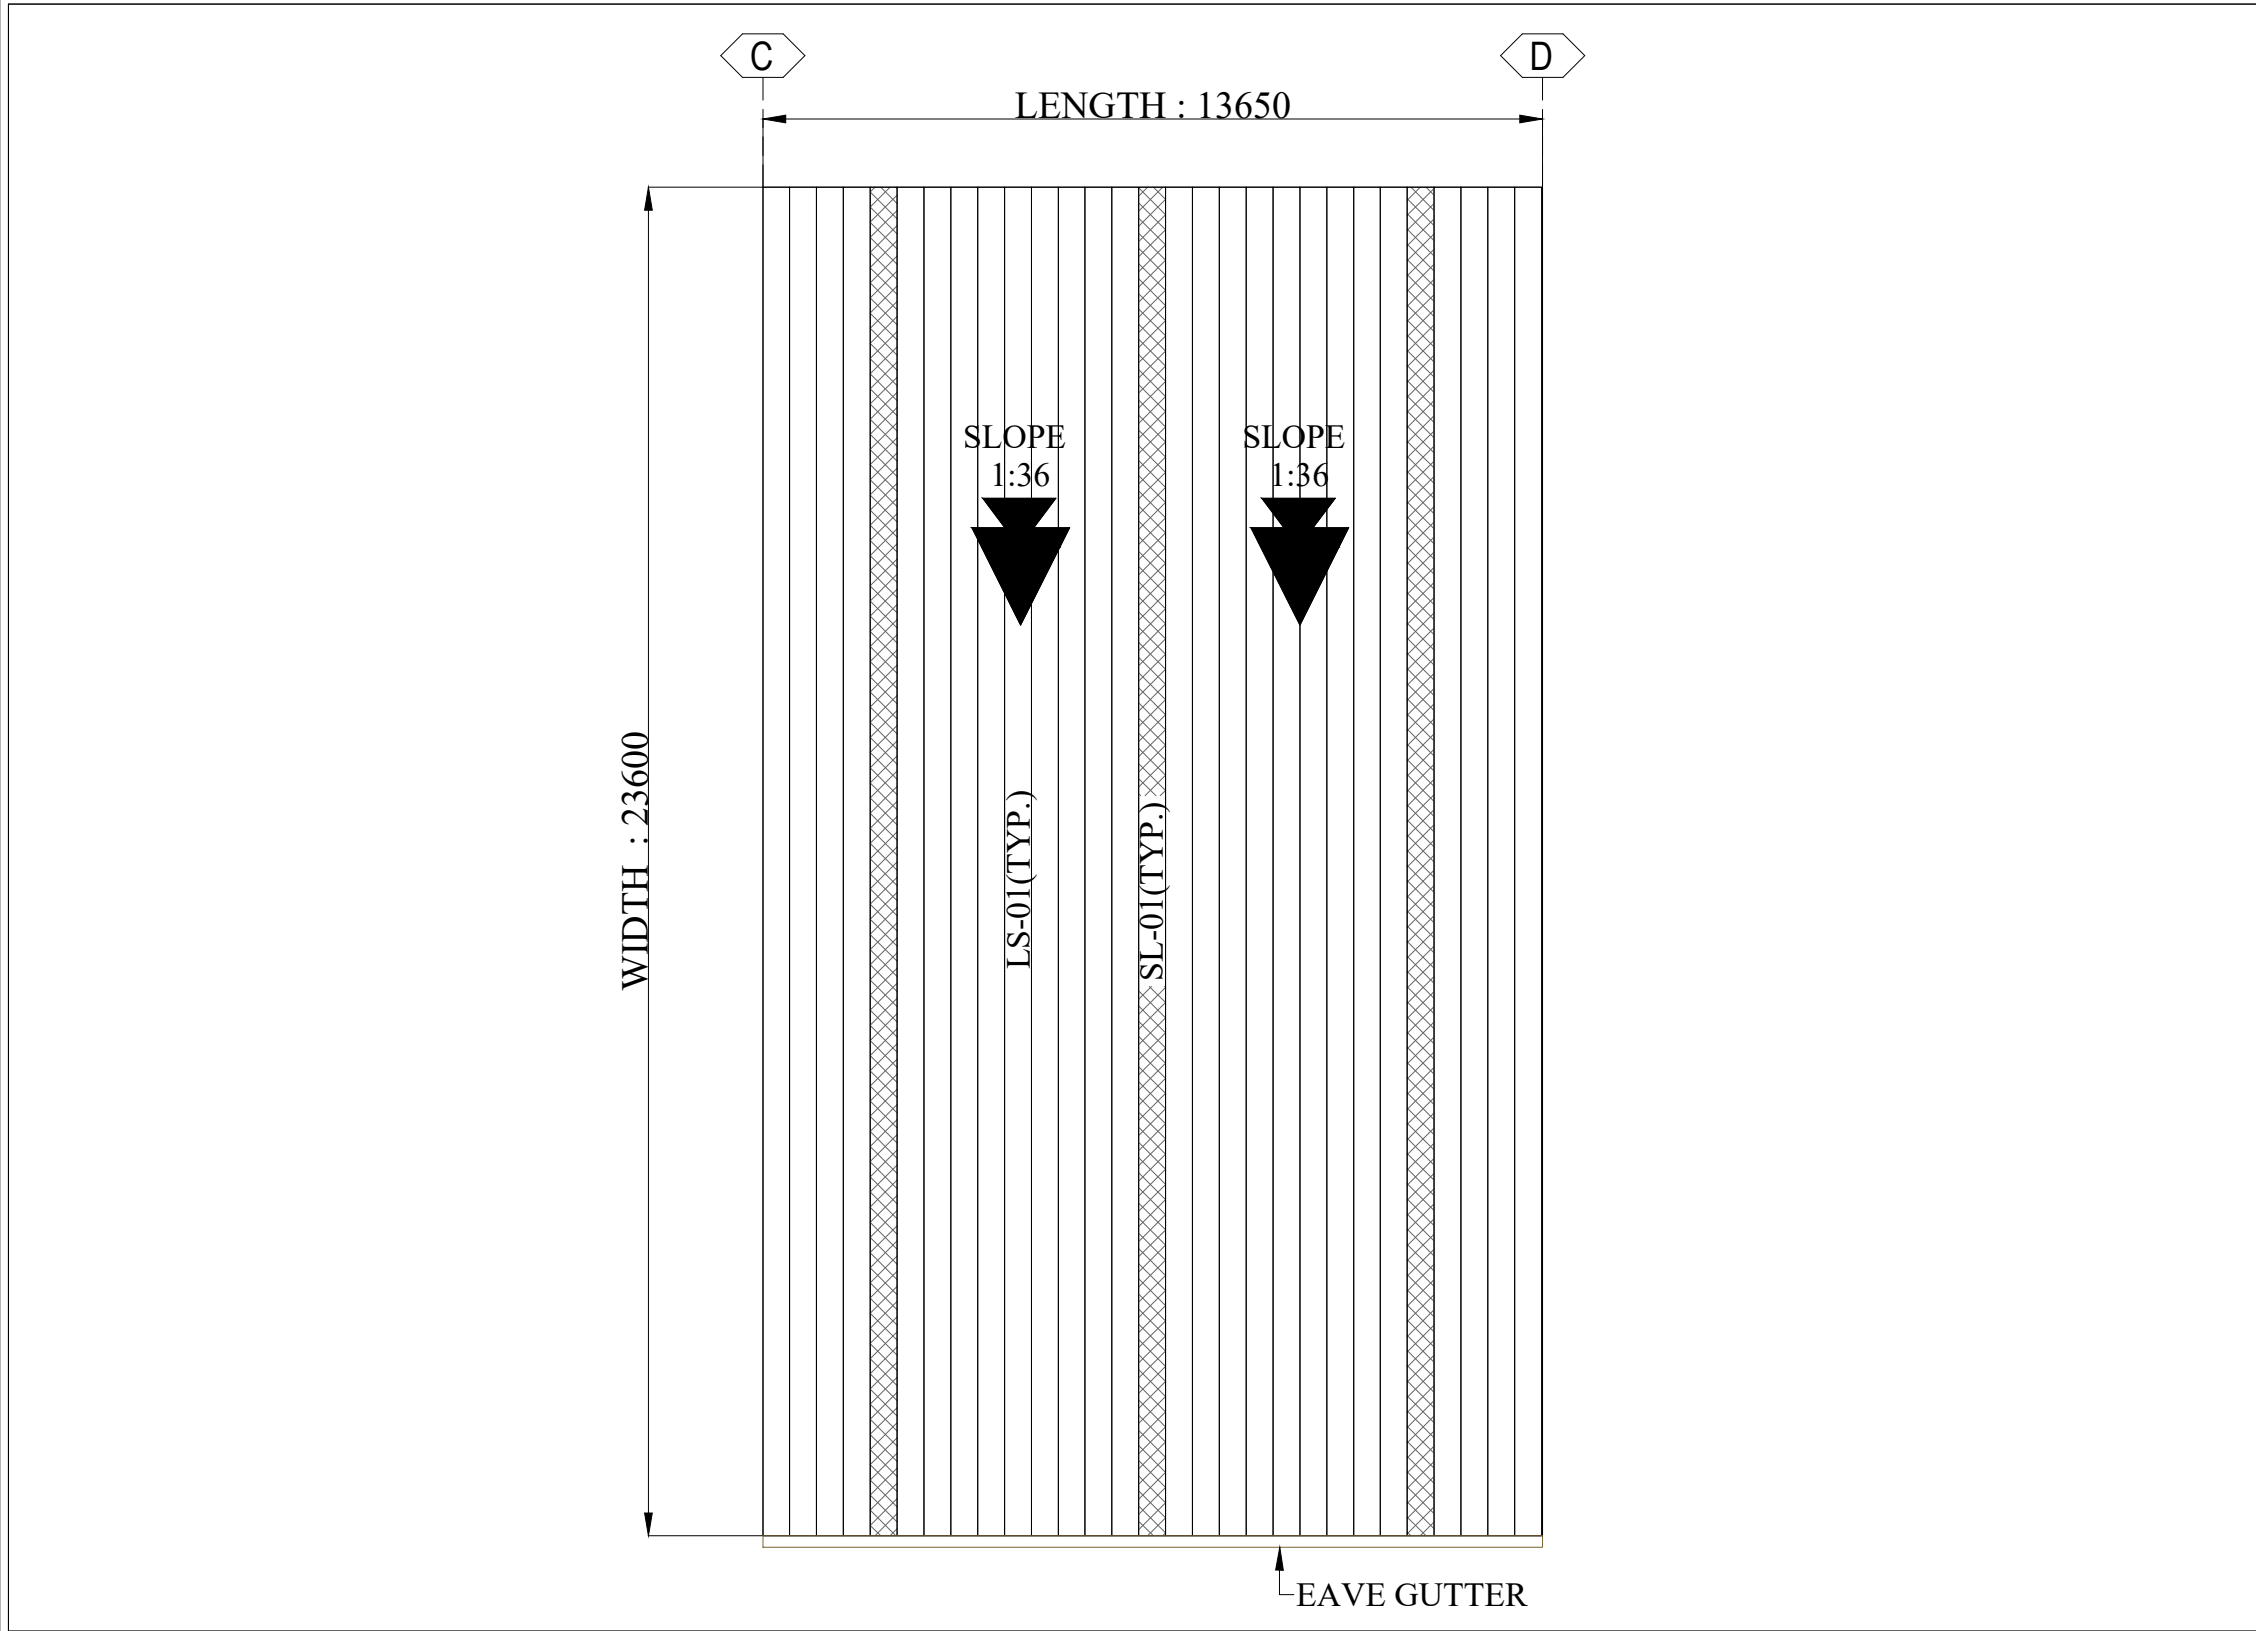

LOCKSEAM SHEETING AREA - 03				
DESCRIPTIONS	PART	LENGTH (MM)	WIDTH (MM)	QUANTITY
LOCKSEAM SHEETING	LS-01	23,600	470	26
SKY LIGHTS	SL-01	23,600	470	3

ROOF SHEETING (AREA 03)

Length = (3M)

5 NOS.

Thickness = 1.2mm (PPG.L)

Paint Side = ▼

COLOR: OFFWHITE

Diagram of the Eave Gutter profile showing dimensions: 188, 20, 30, 70, 88, 96°, 14, 90°, 50, 130, 200.

EAVE GUTTER

Diagram of the Lock Seam Sheet profile showing dimensions: 470, 15, 10, 15, 119°, 155, 148°, 92, 10, 145, 10, 91, 22, 32, 25, 25.

LOCK SEAM SHEET PROFILE

Diagram of the Skylight profile showing dimensions: 491, 24, 75, 152, 132°, 134, 36, 25, 124°, 134, 152, 100, 75.

SKYLIGHT PROFILE : THK. 2mm

FOR APPROVAL :

IN ORDER TO SCHEDULE THIS PROJECT IN AN EFFICIENT MANNER , KINDLY RETURN THESE DRAWINGS WITH YOUR COMMENTS MARKED IN RED

APPROVAL OF THESE DRAWINGS MAY DELAY THE FABRICATION SCHEDULE AND SUBSEQUENTLY THE DELIVERY OF THE BUILDING.

PLEASE TICK MARK ONLY ONE OF THE FOLLOWING

☐ " APPROVED AS IS "

☐ " APPROVED AS NOTED "

☐ " RESUBMIT AS NOTED "

APPROVE : _____

SIGNATURE: _____

DATE : _____

REV	DATE	DESCRIPTION	DRAWN BY	CHK BY	APR BY
00	15-05-25	ISSUED FOR APPROVAL	I.U	M.B	NAS



MAIMAAR

MAIMAAR STEEL Pvt.Ltd
238, Raiwind Road, Thokar Niaz Baig, Lahore, Pakistan
E-mail: nasir.abbas@maimaargroup.com
E-mail: maimaar.steel@gmail.com
Website: www.maimaargroup.com
E-mail: info@maimaargroup.com
Mob-1 : +(92-300) 807 4017 ,+(92-333) 807 1115


JOB NO./QUOTE NO.	MSPL-169	BUILDING #	01
PROJECT NAME	SUPPLY & INSTALLATION OF ROOF SHEETING		
CUSTOMER	PAECO		
JOB SITE LOCATION	KASUR		

ROOF SHEETING (AREA 03)

DWG NO.
06

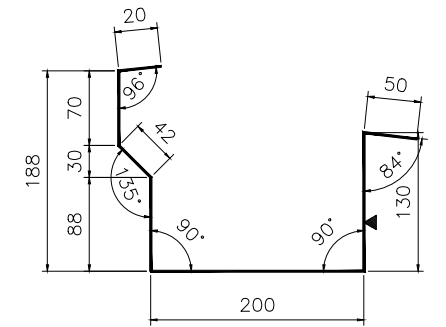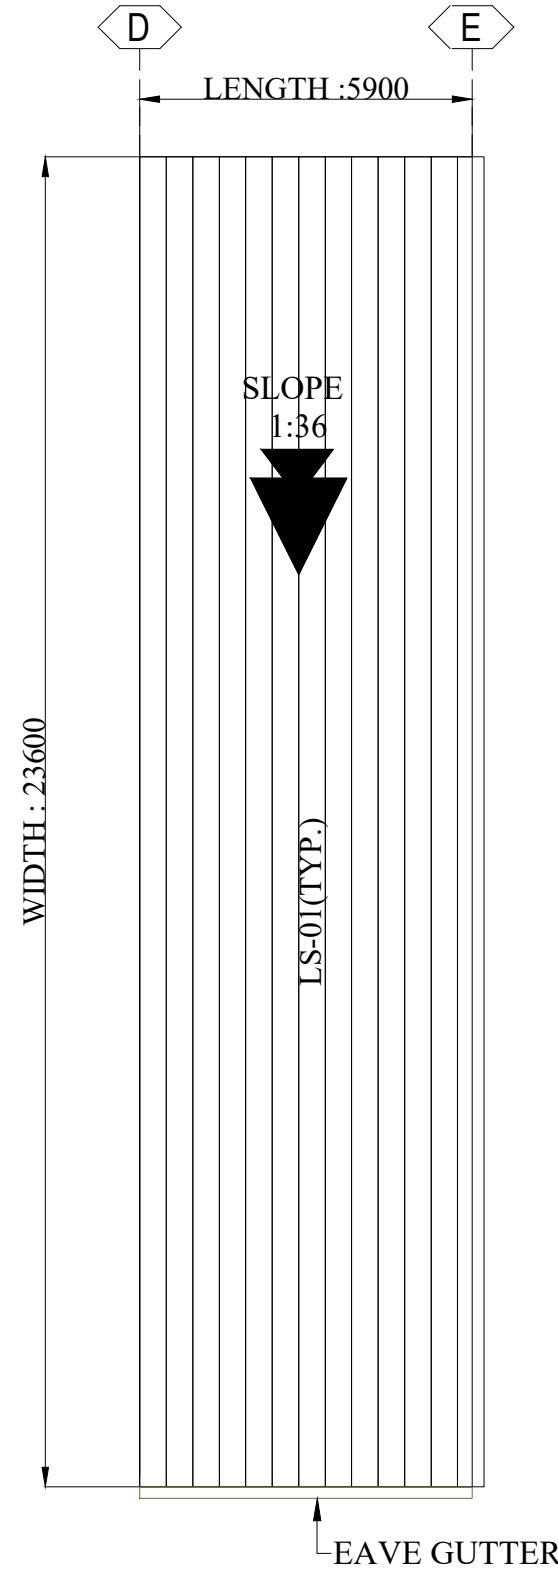

EAVE GUTTER

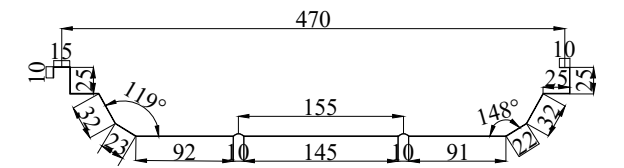

LOCK SEAM SHEET PROFILE

IN ORDER TO SCHEDULE THIS PROJECT
IN AN EFFICIENT MANNER , KINDLY
RETURN THESE DRAWINGS WITH YOUR

☐ " APPROVED AS IS "

☐ " APPROVED AS NOTED"

☐ " RESUBMIT AS NOTED "



DELAY THE FABRICATION SCHEDULE AND SIGNATURE: _____

PLEASE TICK MARK ONLY ONE OF THE FOLLOWING


JOB NO./QUOTE NO.	MSPL-169		BUILDING #	01
PROJECT NAME	SUPPLY & INSTALLATION OF ROOF SHEETING			
CUSTOMER	PAECO			
JOB SITE LOCATION	KASUR			
ROOF FRAMING & SHEETING (AREA 04)				DWG NO.
				07

LOCKSEAM SHEETING AREA - 04				
DESCRIPTIONS	PART	LENGTH (MM)	WIDTH (MM)	QUANTITY
LOCKSEAM SHEETING	LS-01	23,600	470	13


ROOF FRAMING & SHEETING (AREA 04)

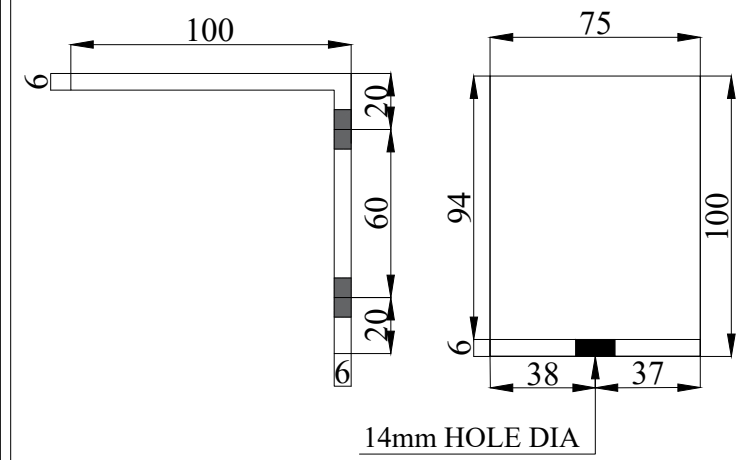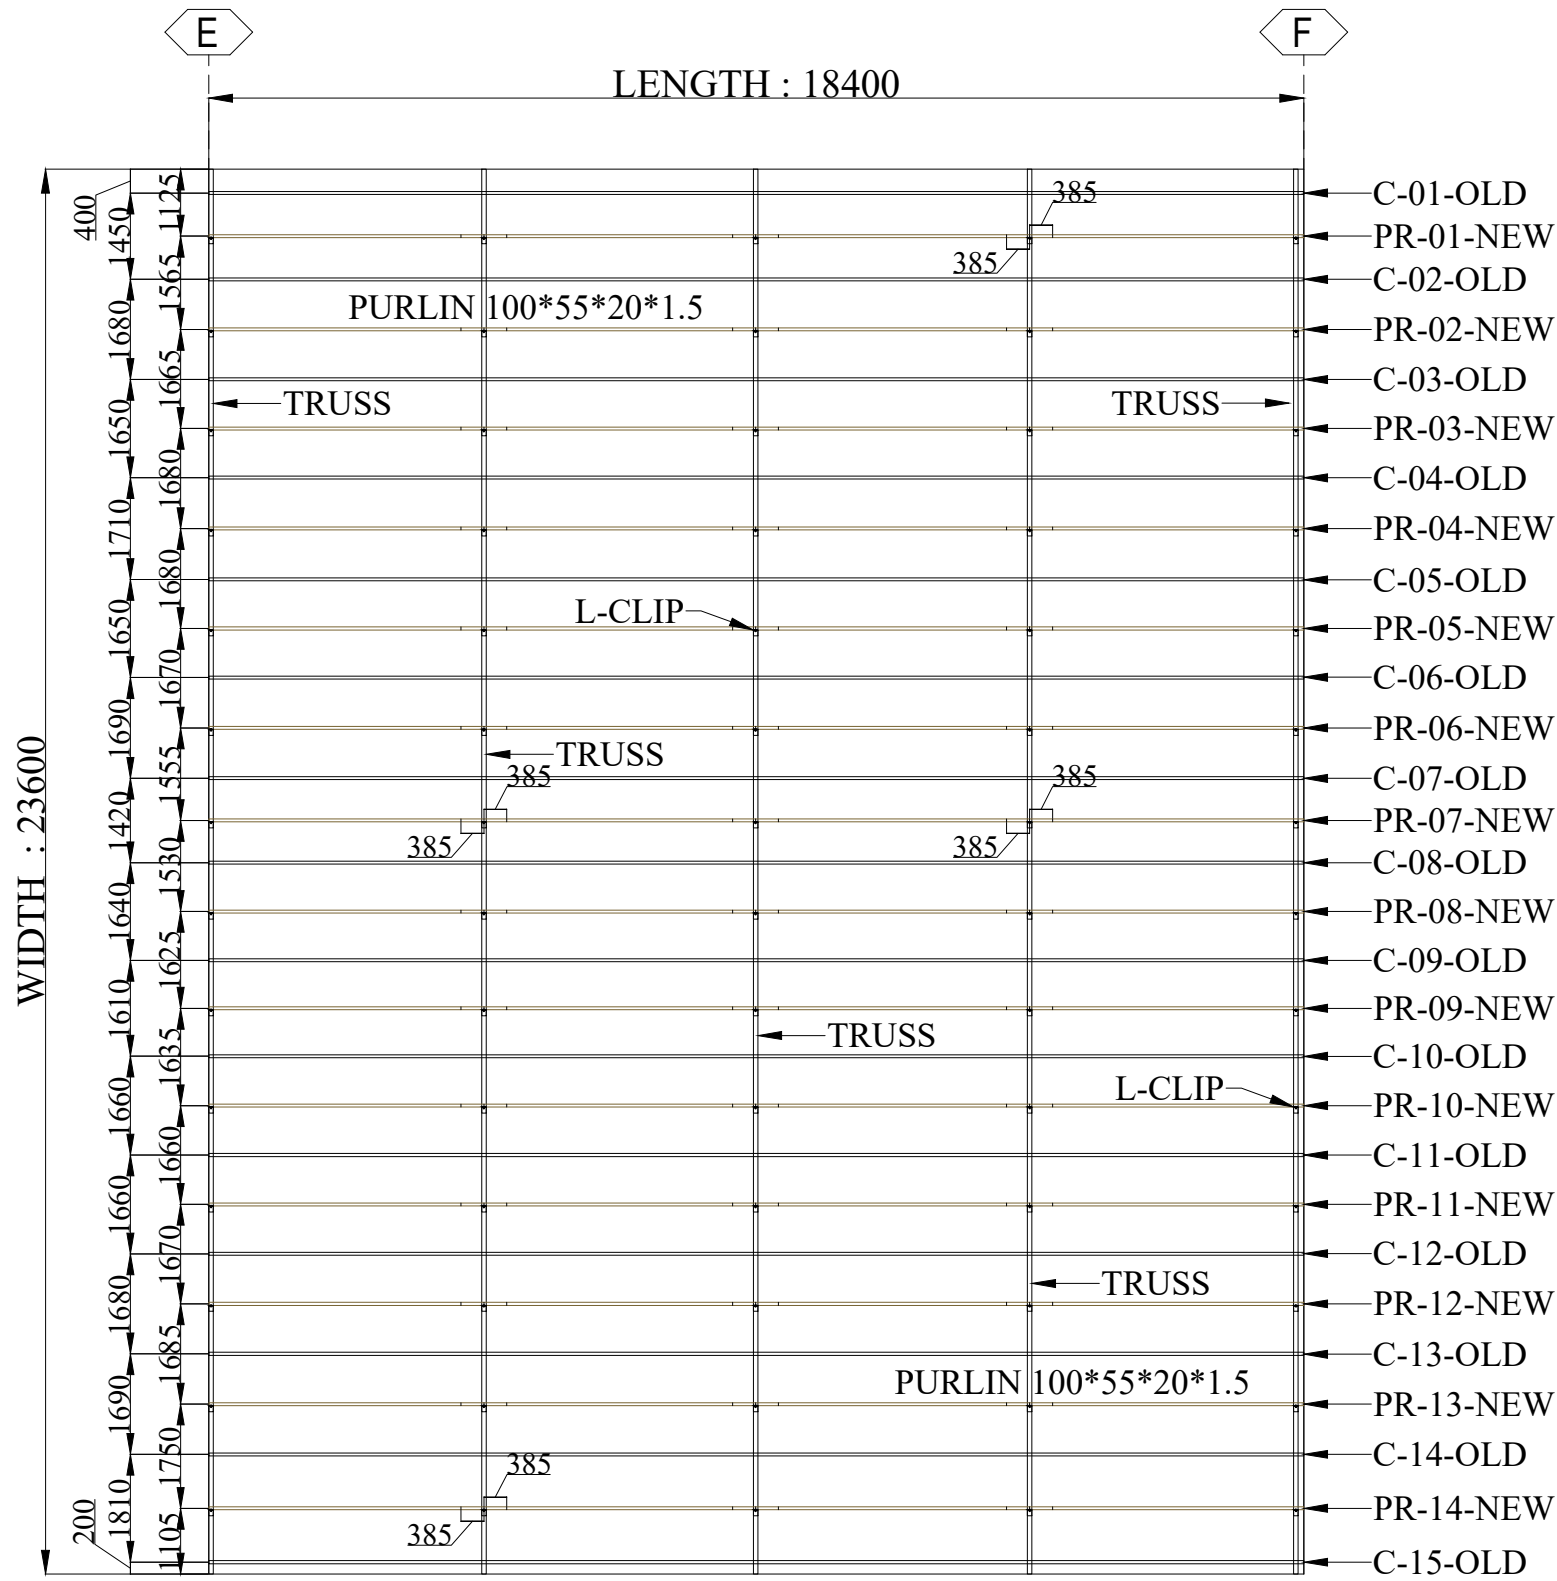

DETAIL OF [L-CLIP-100*100*75*6]

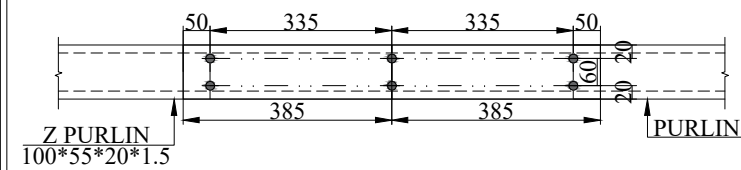

PURLINS OVER LAP DETAIL

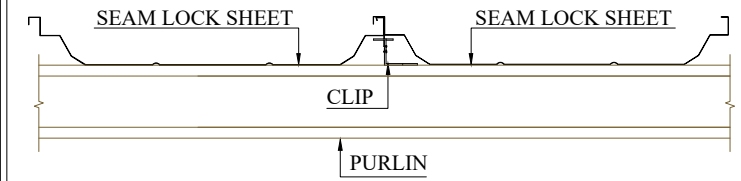


PURLIN WITH SEAM LOCK CLIP DETAIL

FOR APPROVAL :
IN ORDER TO SCHEDULE THIS PROJECT IN AN EFFICIENT MANNER , KINDLY RETURN THESE DRAWINGS WITH YOUR ANY CHANGES MADE AFTER THE COMMENTS MARKED IN RED APPROVAL OF THESE DRAWINGS MAY DELAY THE FABRICATION SCHEDULE AND SUBSEQUENTLY THE DELIVERY OF THE BUILDING. PLEASE TICK MARK ONLY ONE OF THE FOLLOWING

☐ " APPROVED AS IS "
☐ " APPROVED AS NOTED "
☐ " RESUBMIT AS NOTED "

APPROVE : _____
SIGNATURE: _____
DATE : _____

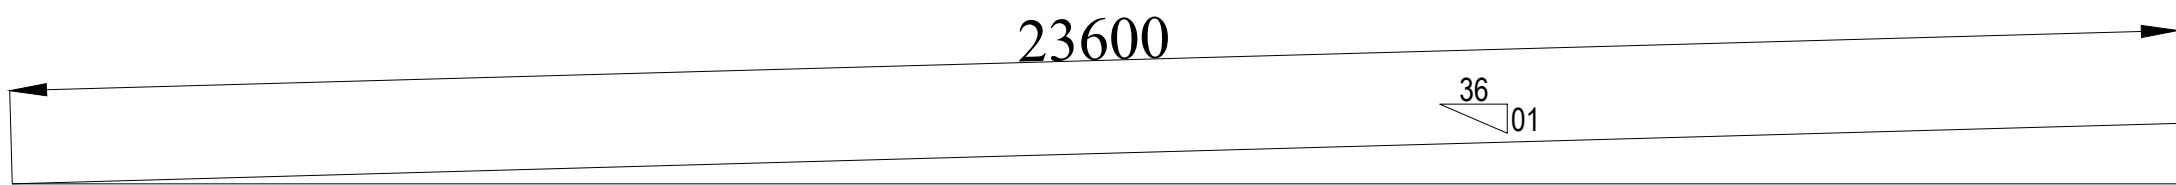

ROOF FRAMING (AREA 05)





MAIMAAR STEEL Pvt.Ltd
238, Raiwind Road, Thokar Niaz Baig, Lahore, Pakistan
E-mail: nasir.abbas@maimaargroup.com
E-mail: maimaar.steel@gmail.com
Website: www.maimaargroup.com
E-mail: info@maimaargroup.com
Mob-1 : +(92-300) 807 4017 ,+(92-333) 807 1115

JOB NO./QUOTE NO.	MSPL-169	BUILDING #	01
PROJECT NAME	SUPPLY & INSTALLATION OF ROOF SHEETING		
CUSTOMER	PAECO		
JOB SITE LOCATION	KASUR		

ROOF FRAMING (AREA 05)

DWG NO.
08

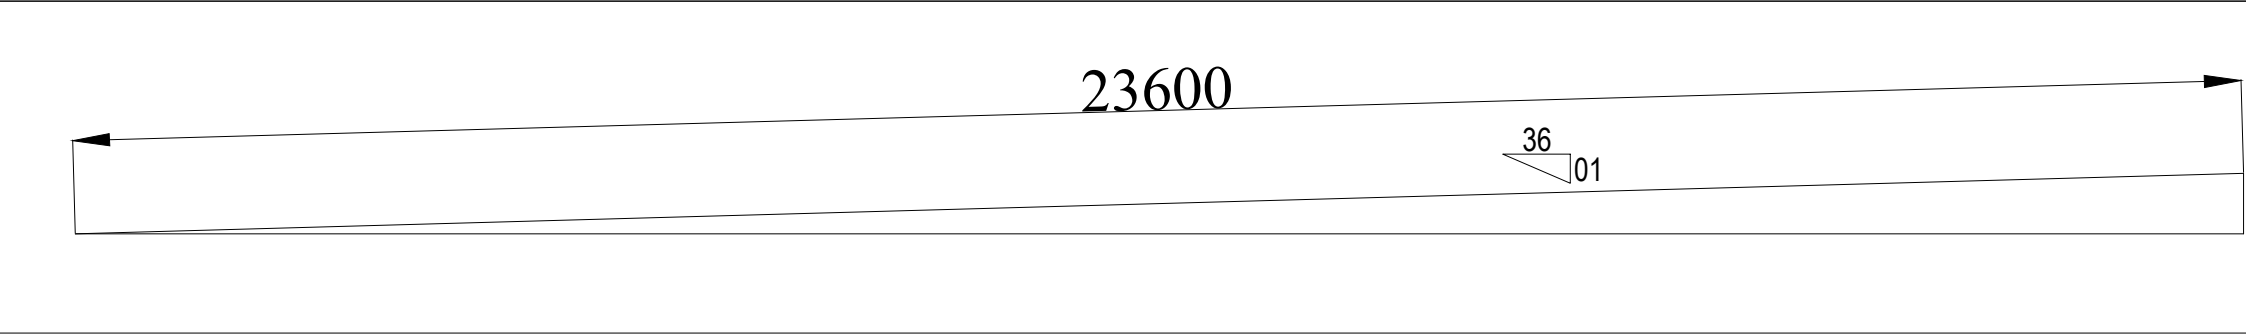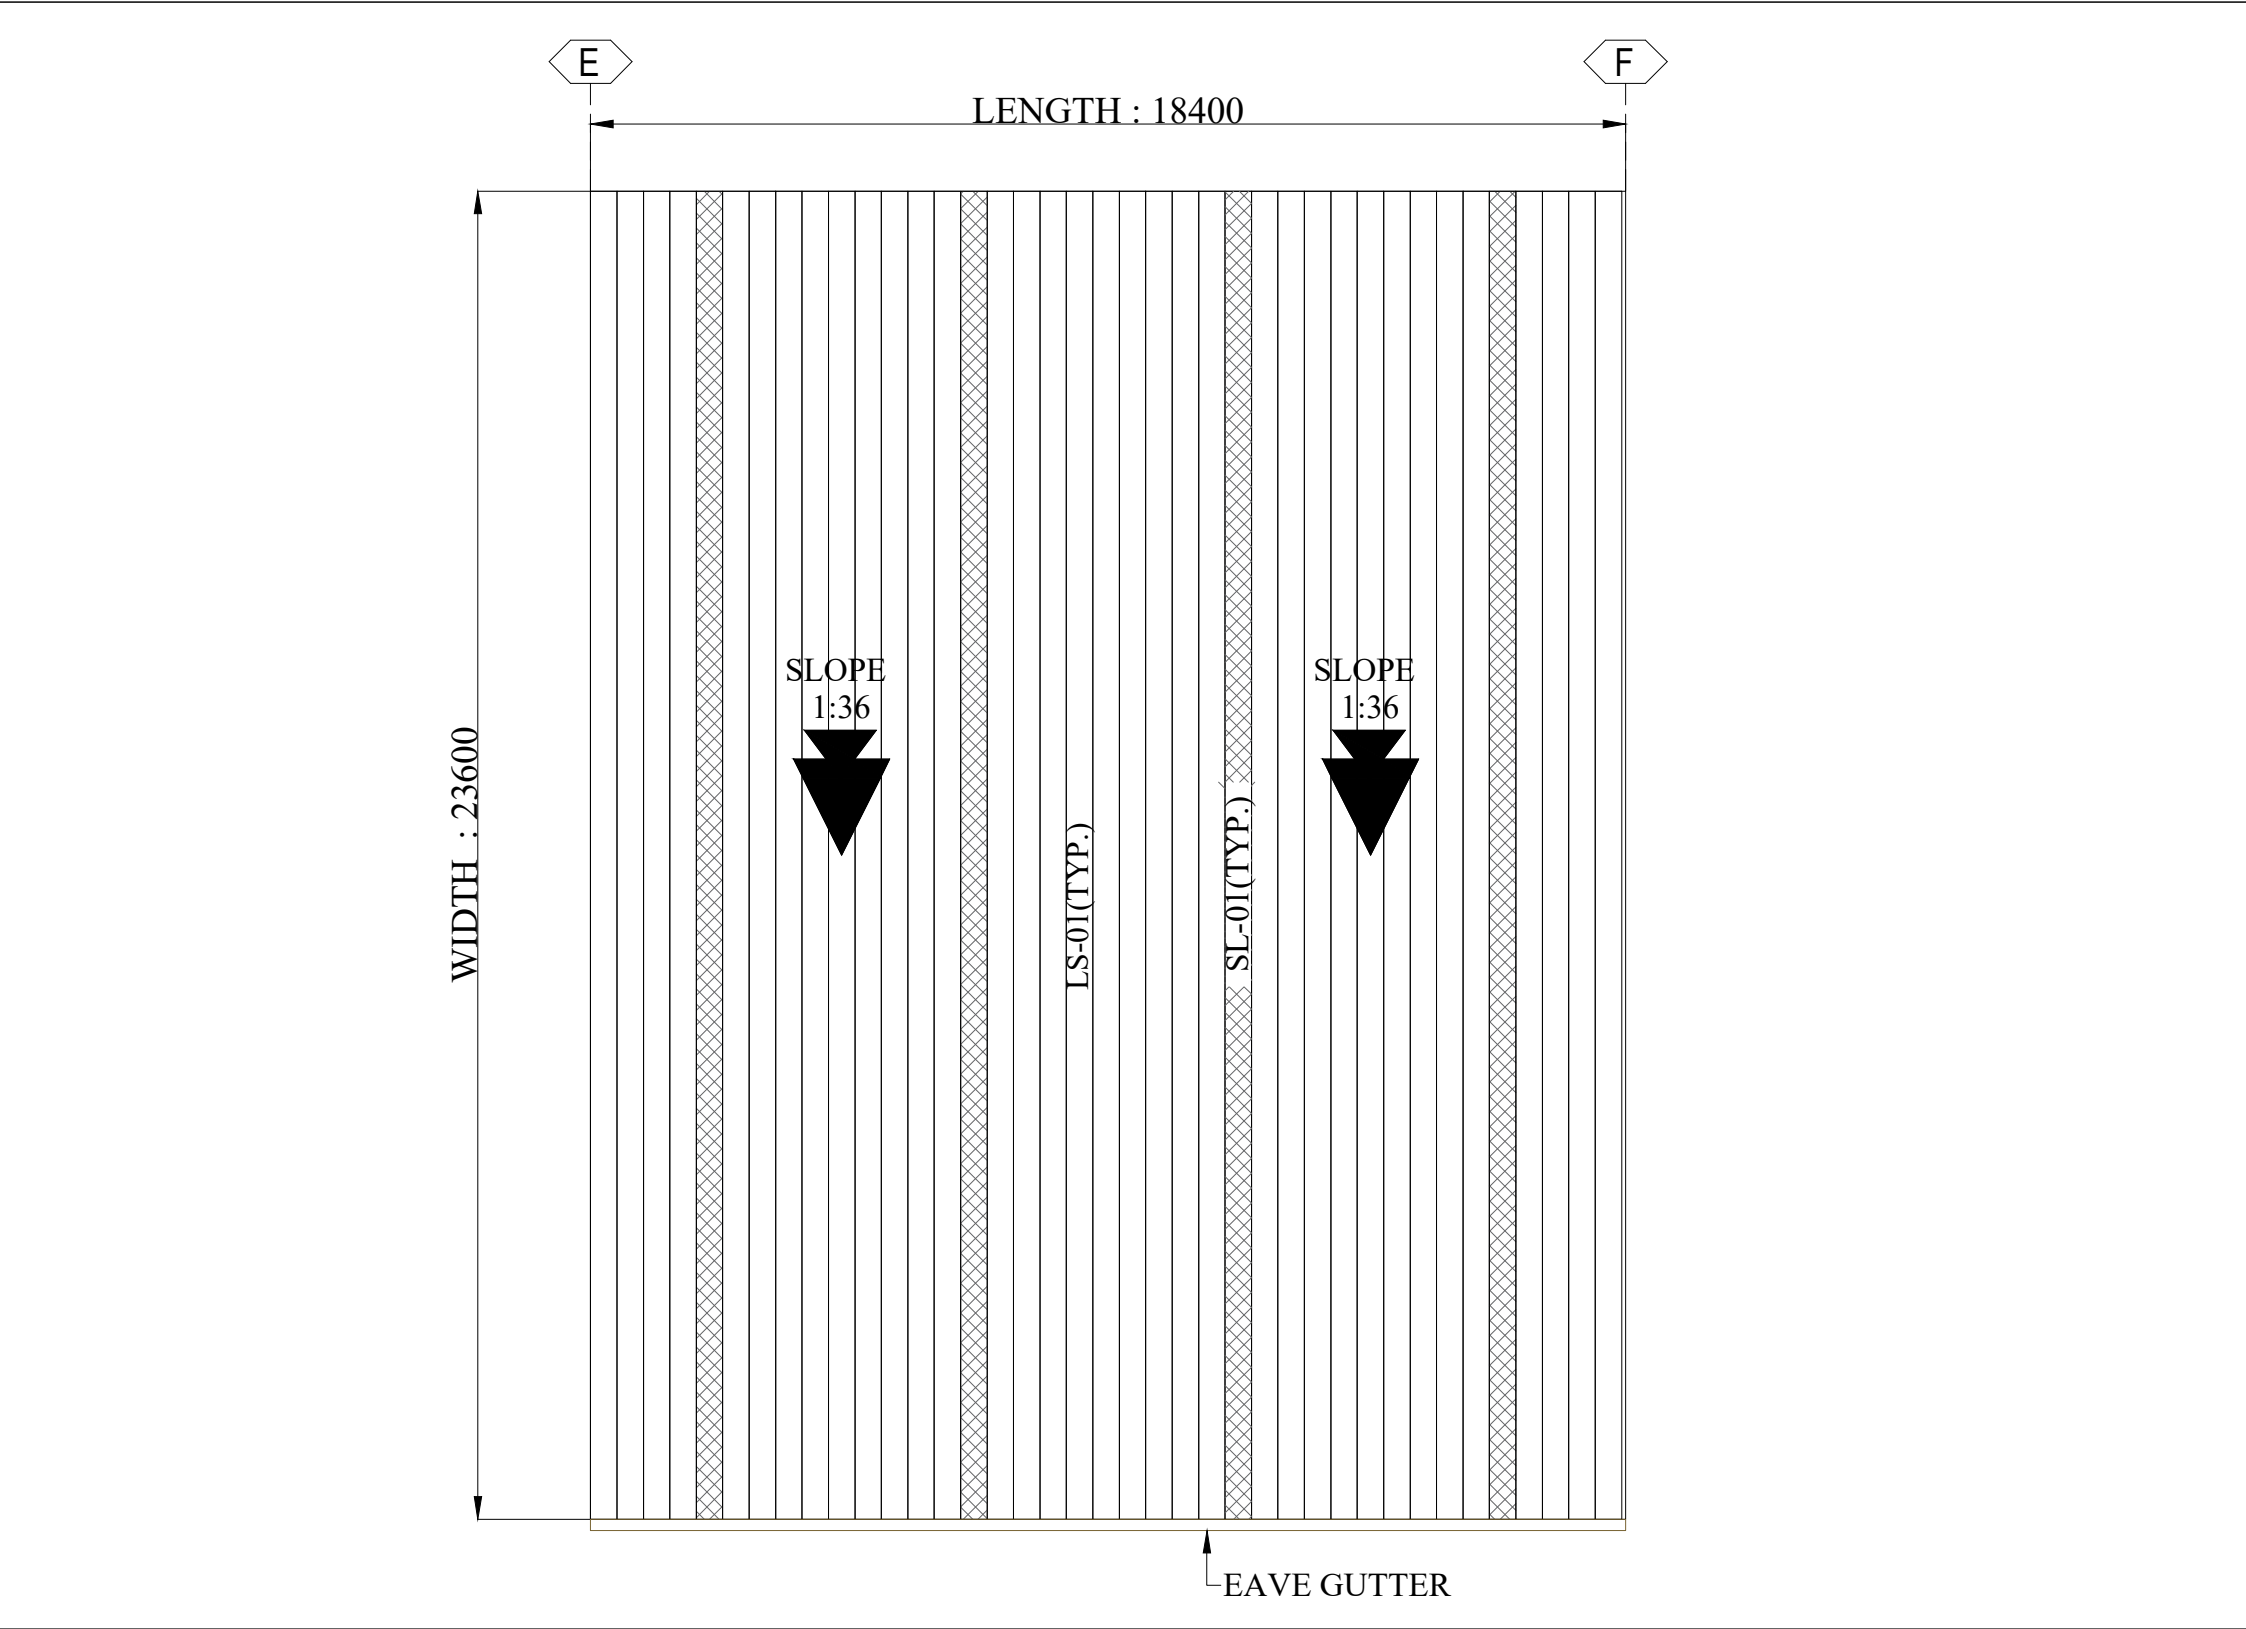

LOCKSEAM SHEETING AREA - 05				
DESCRIPTIONS	PART	LENGTH (MM)	WIDTH (MM)	QUANTITY
LOCKSEAM SHEETING	LS-01	23,600	470	35
SKY LIGHTS	SL-01	23,600	470	4

ROOF SHEETING
(AREA 05)

Length = (3M)

7 NOS.

Thickness = 1.2mm (PPG.L)

Paint Side = ▼

COLOR: OFFWHITE

Diagram of the Eave Gutter profile showing dimensions: 188, 70, 30, 88, 20, 96°, 42, 93°, 90°, 200, 90°, 50, 84°, 130.

EAVE GUTTER

Diagram of the Lock Seam Sheet profile showing dimensions: 470, 15, 10, 15, 19°, 155, 148°, 92, 10, 145, 10, 91, 22, 32, 25.

LOCK SEAM SHEET PROFILE

Diagram of the Skylight profile showing dimensions: 491, 24, 75, 152, 132°, 134, 25, 124°, 65, 134, 100, 152, 75.

SKYLIGHT PROFILE : THK. 2mm

FOR APPROVAL :

IN ORDER TO SCHEDULE THIS PROJECT IN AN EFFICIENT MANNER , KINDLY RETURN THESE DRAWINGS WITH YOUR COMMENTS MARKED IN RED

☐ " APPROVED AS IS "
☐ " APPROVED AS NOTED "
☐ " RESUBMIT AS NOTED "

APPROVAL OF THESE DRAWINGS MAY DELAY THE FABRICATION SCHEDULE AND SUBSEQUENTLY THE DELIVERY OF THE BUILDING.

APPROVE : _____
SIGNATURE: _____
DATE : _____

PLEASE TICK MARK ONLY ONE OF THE FOLLOWING

REV	DATE	DESCRIPTION	DRAWN BY	CHK BY	APR BY
00	15-05-25	ISSUED FOR APPROVAL	I.U	M.B	NAS

MAIMAAR

MAIMAAR STEEL Pvt.Ltd

238, Raiwind Road, Thokar Niaz Baig, Lahore, Pakistan

E-mail: nasir.abbas@maimaargroup.com



E-mail: maimaar.steel@gmail.com

Website: www.maimaargroup.com

E-mail: info@maimaargroup.com

Mob-1 : +(92-300) 807 4017 ,+(92-333) 807 1115

JOB NO./QUOTE NO.	MSPL-169	BUILDING #	01
PROJECT NAME	SUPPLY & INSTALLATION OF ROOF SHEETING		
CUSTOMER	PAECO		
JOB SITE LOCATION	KASUR		
ROOF SHEETING (AREA 04)			DWG NO.
			09

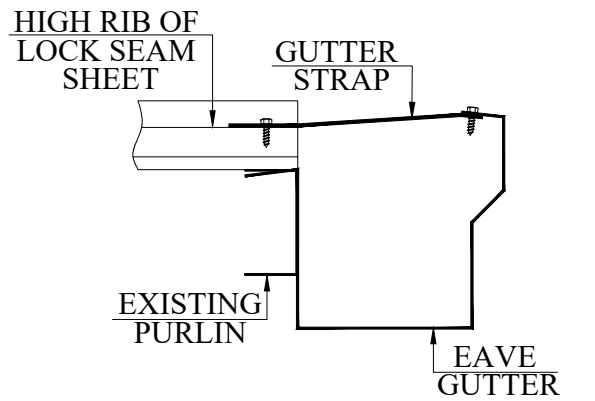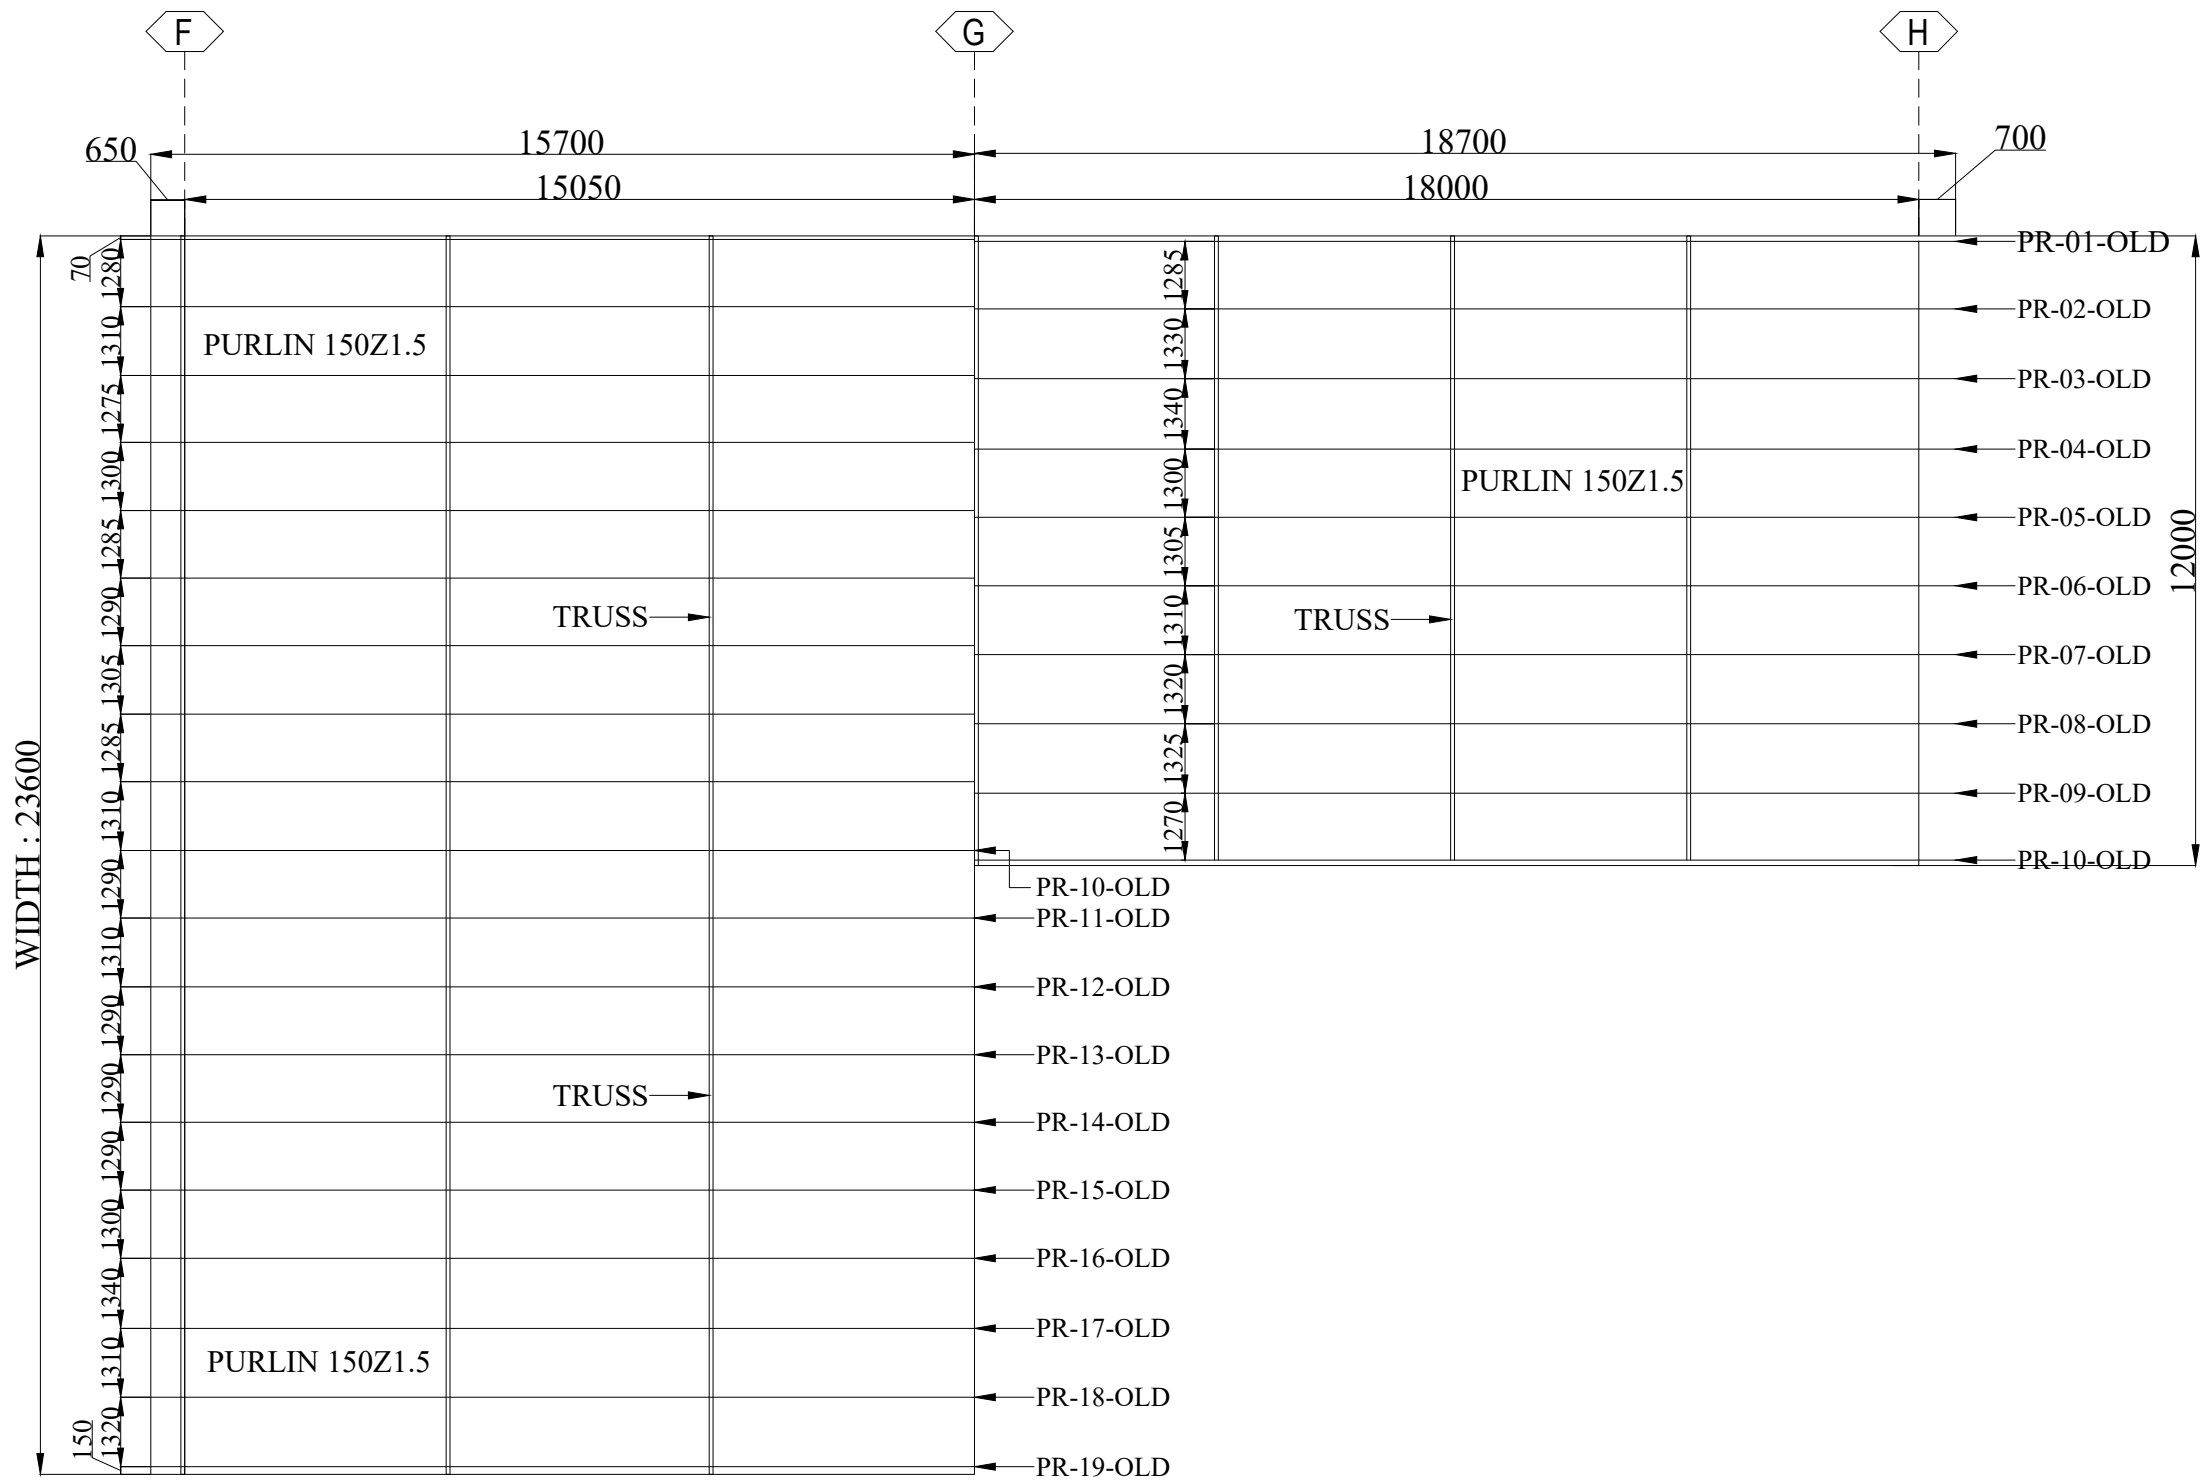

DETAIL OF EAVE GUTTER

FOR APPROVAL :
IN ORDER TO SCHEDULE THIS PROJECT IN AN EFFICIENT MANNER , KINDLY RETURN THESE DRAWINGS WITH YOUR COMMENTS MARKED IN RED
APPROVAL OF THESE DRAWINGS MAY DELAY THE FABRICATION SCHEDULE AND SUBSEQUENTLY THE DELIVERY OF THE BUILDING.
PLEASE TICK MARK ONLY ONE OF THE FOLLOWING

☐ " APPROVED AS IS "
☐ " APPROVED AS NOTED "
☐ " RESUBMIT AS NOTED "

APPROVE : _____
SIGNATURE: _____
DATE : _____

REV	DATE	DESCRIPTION	DRAWN BY	CHK BY	APR BY
00	15-05-25	ISSUED FOR APPROVAL	I.U	M.B	NAS


MAIMAAR

MAIMAAR STEEL Pvt.Ltd
238, Raiwind Road, Thokar Niaz Baig, Lahore, Pakistan
E-mail: nasir.abbas@maimaargroup.com
E-mail: maimaar.steel@gmail.com
Website: www.maimaargroup.com
E-mail: info@maimaargroup.com
Mob-1 : +(92-300) 807 4017 ,+(92-333) 807 1115

JOB NO./QUOTE NO.	MSPL-169	BUILDING #	01
PROJECT NAME	SUPPLY & INSTALLATION OF ROOF SHEETING		
CUSTOMER	PAECO		
JOB SITE LOCATION	KASUR		

ROOF FRAMING (AREA 06 & 07)

ROOF FRAMING (AREA 06 & 07)

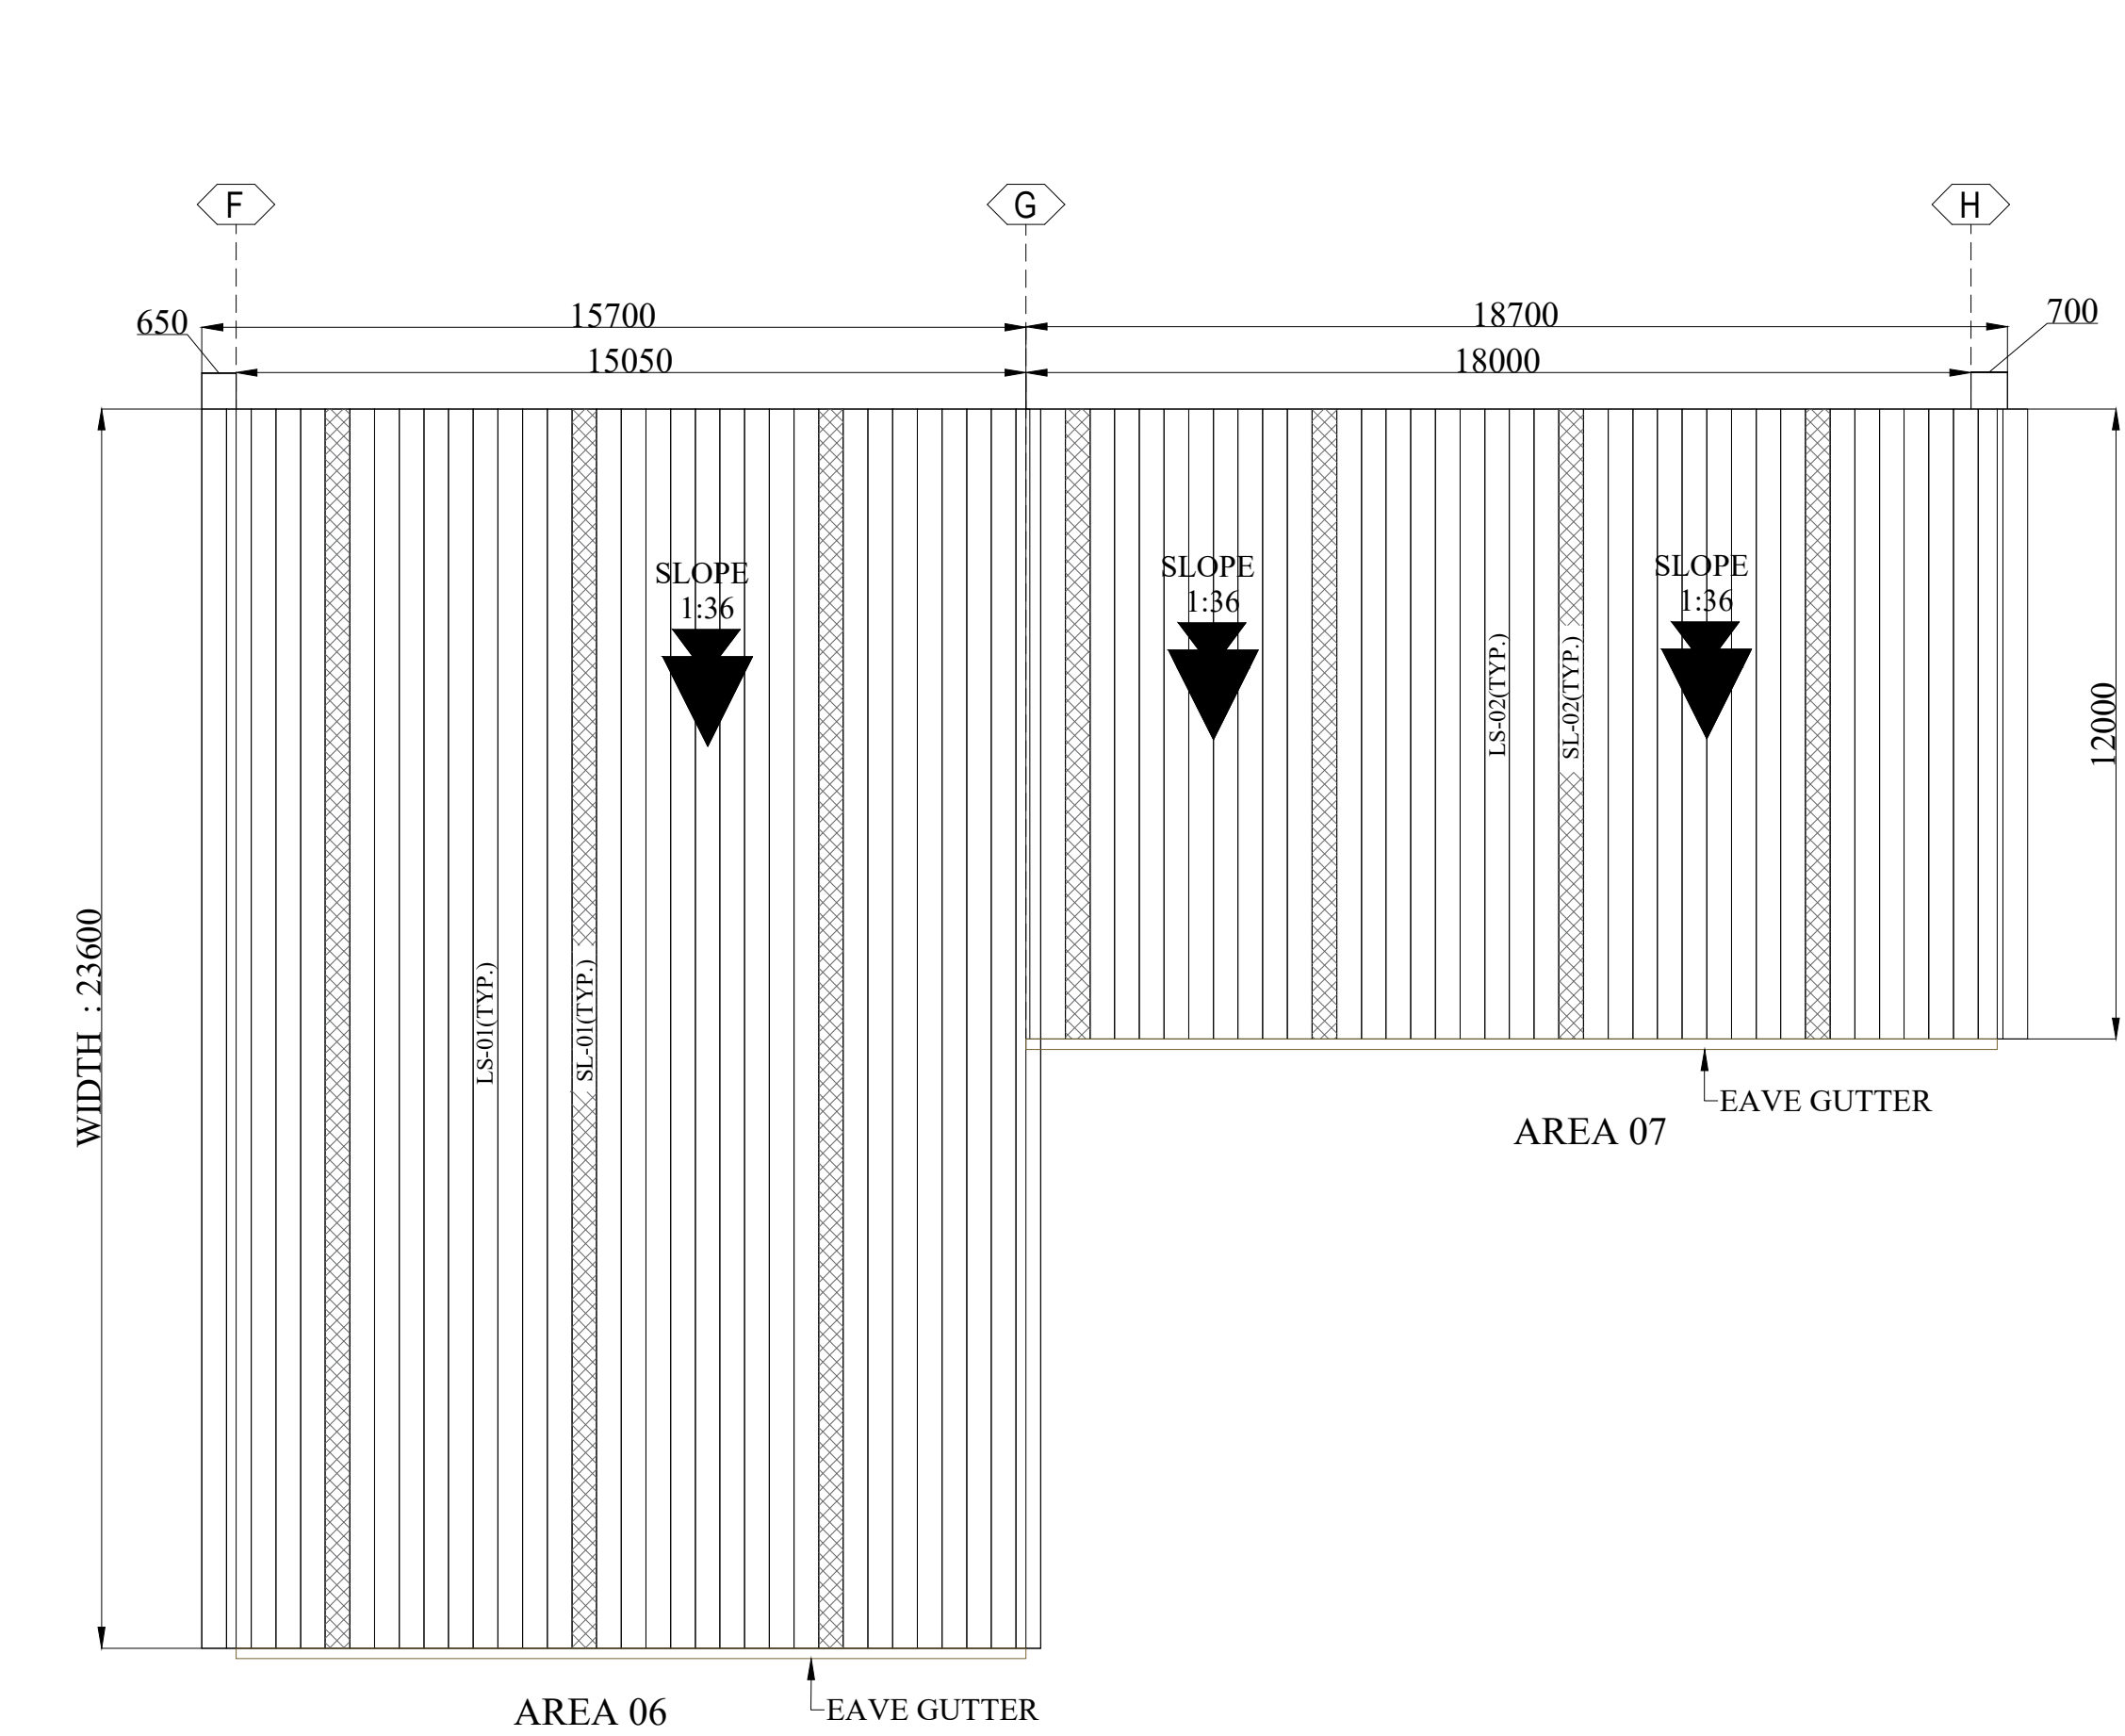

LOCKSEAM SHEETING AREA - 06 & 07				
DESCRIPTIONS	PART	LENGTH (MM)	WIDTH (MM)	QUANTITY
LOCKSEAM SHEETING	LS-01	23,600	470	31
LOCKSEAM SHEETING	LS-02	12,000	470	36
SKY LIGHT	SL-01	23,600	470	3
SKY LIGHT	SL-02	12,000	470	4

ROOF SHEETING
(AREA 06 & 07)


Length = (3M)

12 NOS.


Thickness = 1.2mm (PPG.L)

Paint Side = ▼


COLOR: OFFWHITE

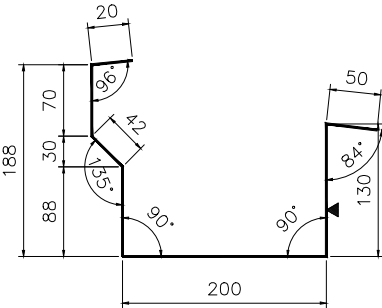

EAVE GUTTER

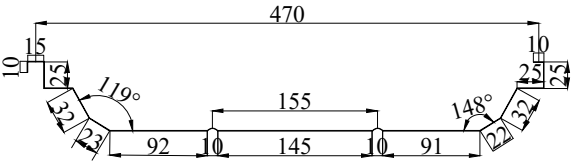

LOCK SEAM SHEET PROFILE

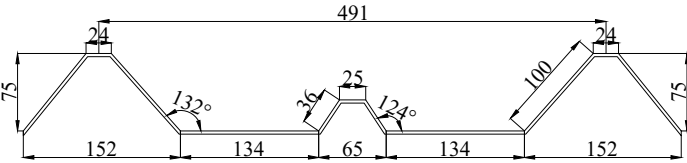

SKYLIGHT PROFILE : THK. 2mm

FOR APPROVAL :

IN ORDER TO SCHEDULE THIS PROJECT IN AN EFFICIENT MANNER , KINDLY RETURN THESE DRAWINGS WITH YOUR COMMENTS MARKED IN RED

APPROVAL OF THESE DRAWINGS MAY DELAY THE FABRICATION SCHEDULE AND SUBSEQUENTLY THE DELIVERY OF THE BUILDING.

PLEASE TICK MARK ONLY ONE OF THE FOLLOWING

☐ " APPROVED AS IS "

☐ " APPROVED AS NOTED "

☐ " RESUBMIT AS NOTED "

APPROVE : _____

SIGNATURE: _____

DATE : _____

REV	DATE	DESCRIPTION	DRAWN BY	CHK BY	APR BY
00	15-05-25	ISSUED FOR APPROVAL	I.U	M.B	NAS



MAIMAAR STEEL Pvt.Ltd
238, Raiwind Road, Thokar Niaz Baig, Lahore, Pakistan
E-mail: nasir.abbas@maimaargroup.com
E-mail: maimaar.steel@gmail.com
Website: www.maimaargroup.com
E-mail: info@maimaargroup.com
Mob-1 : +(92-300) 807 4017 ,+(92-333) 807 1115

JOB NO./QUOTE NO.	MSPL-169	BUILDING #	01
PROJECT NAME	SUPPLY & INSTALLATION OF ROOF SHEETING		
CUSTOMER	PAECO		
JOB SITE LOCATION	KASUR		