

SINGLE SLOPE – COLUMNS BOTH SIDES
BUILDING CROSS-SECTION


18.3M SPAN | C.H 10.7M | HIGH EAVE 13.4M | SLOPE 1:10

WALL SHEETING:

0.50 MM PPGI (S-TYPE) + 50MM FIBERGLASS INSULATION (12KG/M3)

ROOF SHEETING:

0.50 MM PPGI (S-TYPE) + 50MM FIBERGLASS INSULATION (12KG/M3)

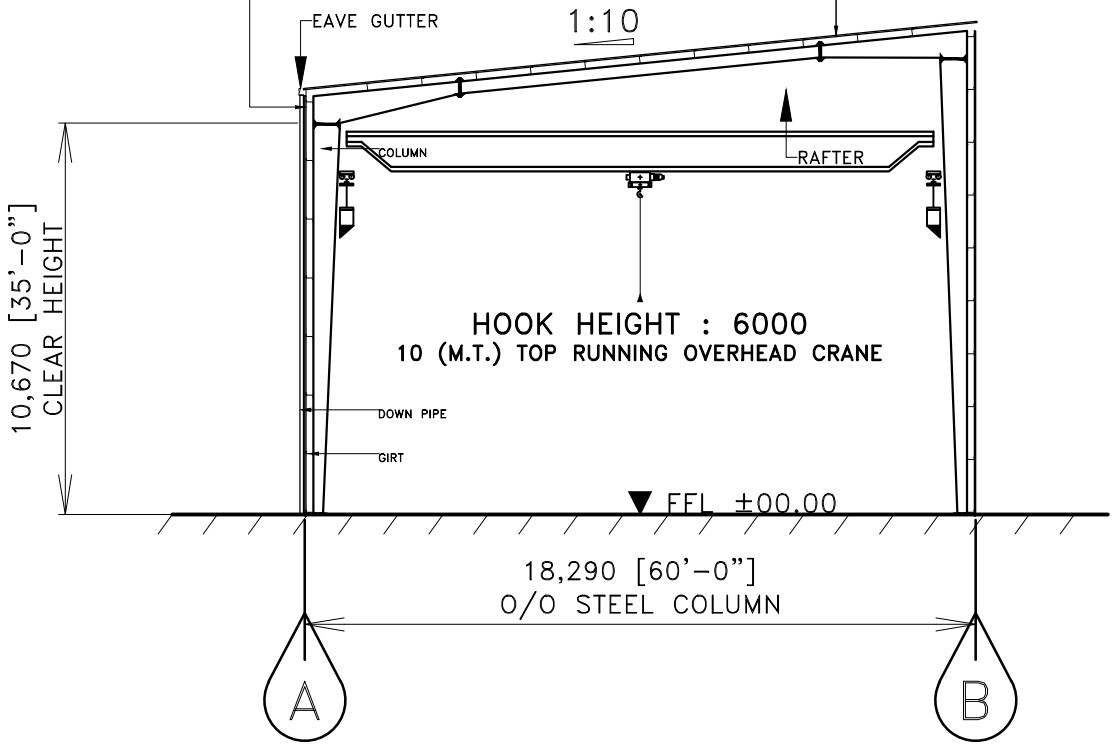

GENERAL NOTES

1. ALL DIMENSIONS ARE IN MM.
2. PROPOSAL DRAWING – NOT FOR CONSTRUCTION.
3. PROPOSAL DRAWING IS INDICATIVE ONLY; FINAL DIMENSIONS & LEVELS WILL BE SHOWN IN THE APPROVAL DRAWING AT THE DESIGN STAGE.
4. FOR DETAILED DESCRIPTION, REFER TO THE TECHNICAL & FINANCIAL PROPOSAL.

THIS DOCUMENT IS A PROPOSAL DRAWING OF
MAIMAAR STEEL (PVT) LTD – NOT FOR CONSTRUCTION

KEY BUILDING DATA

BUILDING WIDTH	18,290 MM
BUILDING LENGTH	30,480 MM
EAVE HEIGHT	11,608 MM
ROOF SLOPE	1:10
NO. OF BAYS	4

HEIGHTS, SLOPE & GRIDS AS SHOWN ON THE SECTION.

00	05-SEP-2026		M.H	YEA
REV. NO.	DATE	DSN	DRN	CHK

PROJECT NAME :
UNNAMED PROJECT

CUSTOMER :
UNNAMED CLIENT

STEEL CONTRACTOR :



MAIMAAR STEEL (PVT) LTD

LAHORE OFFICE
235, FIRST FLOOR, LALAZAR COMMERCIAL AREA,
RAIWIND ROAD, LAHORE, PAKISTAN
WEB: WWW.MAIMAARGROUP.COM
CELL : +(92-300) 807 4007

QUOTE NO. : MSPL-26-276

BLDG. NO. : 01

BLDG. NAME. :

NO. OF IDENTICAL BLDG. : 1

DRAWING TITLE :
CROSS SECTION

SCALE 1:209	SHEET SIZE A4	SHEET NO. PRO-01
----------------	------------------	---------------------