


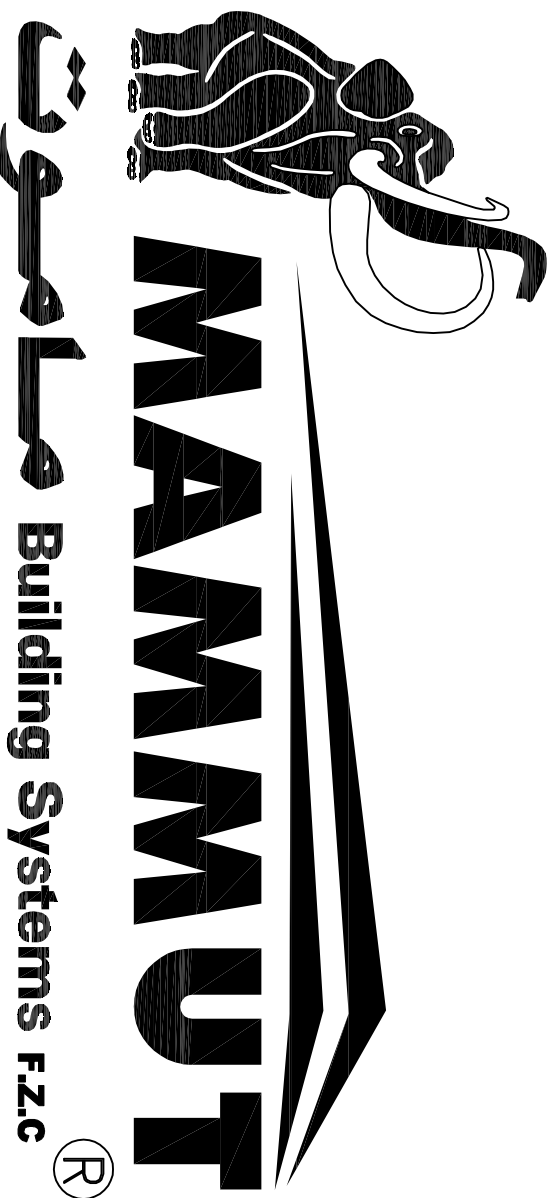

1st Floor, Q-429, Phase-II,
Defense Housing Authority
Lahore Cantt-Pakistan
Website: www.mammutgroup.com
E-mail: pksales@mammut.ae
Phone : +(92-42) 574 3066-68
Fax. : +(92-42) 589 8696

PROPOSAL DRAWING

AREA OFFICE / QUOTE NO. SENDERS:	PK-013-169
----------------------------------	------------

CUSTOMER:	
03-10-2013	
BUILDING NAME:	
WORKSHOP	
PROJECT TITLE :	
PROPOSED STEEL BUILDING	
..	
PREPARED BY : JAS	CHECKED BY : NASIR
DATE: 03-10-2013	REV.:00

- General Notes**
- All dimensions are in millimeters (mm).
 - Panel thickness is the Total Coated Thickness (TCTP).
 - All Dimensions, Levels Shown in the PROPOSAL DRAWING is indicative only, final design Dimensions, Levels will be shown in our APPROVAL DRAWING in design stage.
 - For panel description, Please refer to technical and material proposal

This document is PROPOSAL DRAWING data of MAMMUT BUILDING SYSTEMS FZC. not for construction.

THE BUILDING HAS BEEN DESIGNED TO SUPPORT THE FOLLOWING LOADS:
DEAD LOAD 15.00 KN/SQ.M.
LIVE LOAD ON FRAME 0.57 KN/SQ.M.
WIND SPEED 130.0 KPH
ADPT. COLLATERAL LOAD 0.0 KN/SQ.M.
ROOF SNOW LOAD - KN/SQ.M.
SEISMIC LOAD ZONE 2A
TEMPERATURE LOAD
RAINFALL INTENSITY 15.00 CM/HR
AS PER MBBAA 2006 METEAL BUILDING SYSTEMS MANUAL.


00	03-10-2013	JAS	NASIR
Rev No	Date	DSN	CHK
PROJECT : PROPOSED STEEL BUILDING			
CUSTOMER : 03-10-2013			
STEEL CONTRACTOR:			



MAMMUT
Building Systems FZC®

Lahore Office
1st Floor, Q-429, Phase-II,
Defense Housing Authority
Website: www.mammutgroup.com
Phone : +92-42) 574 3066-68
Fax : +92-42) 589 8896

QUOTE NO. : PK-013-169	
Bldg. No. : 01	
Bldg. Name : STEEL SHED	
No. Of Identical Bldg. : ONE	
Drawing Title : COLUMN LAY-OUT PLAN	
Scale : N.T.S.	Sheet No. 1 of 4







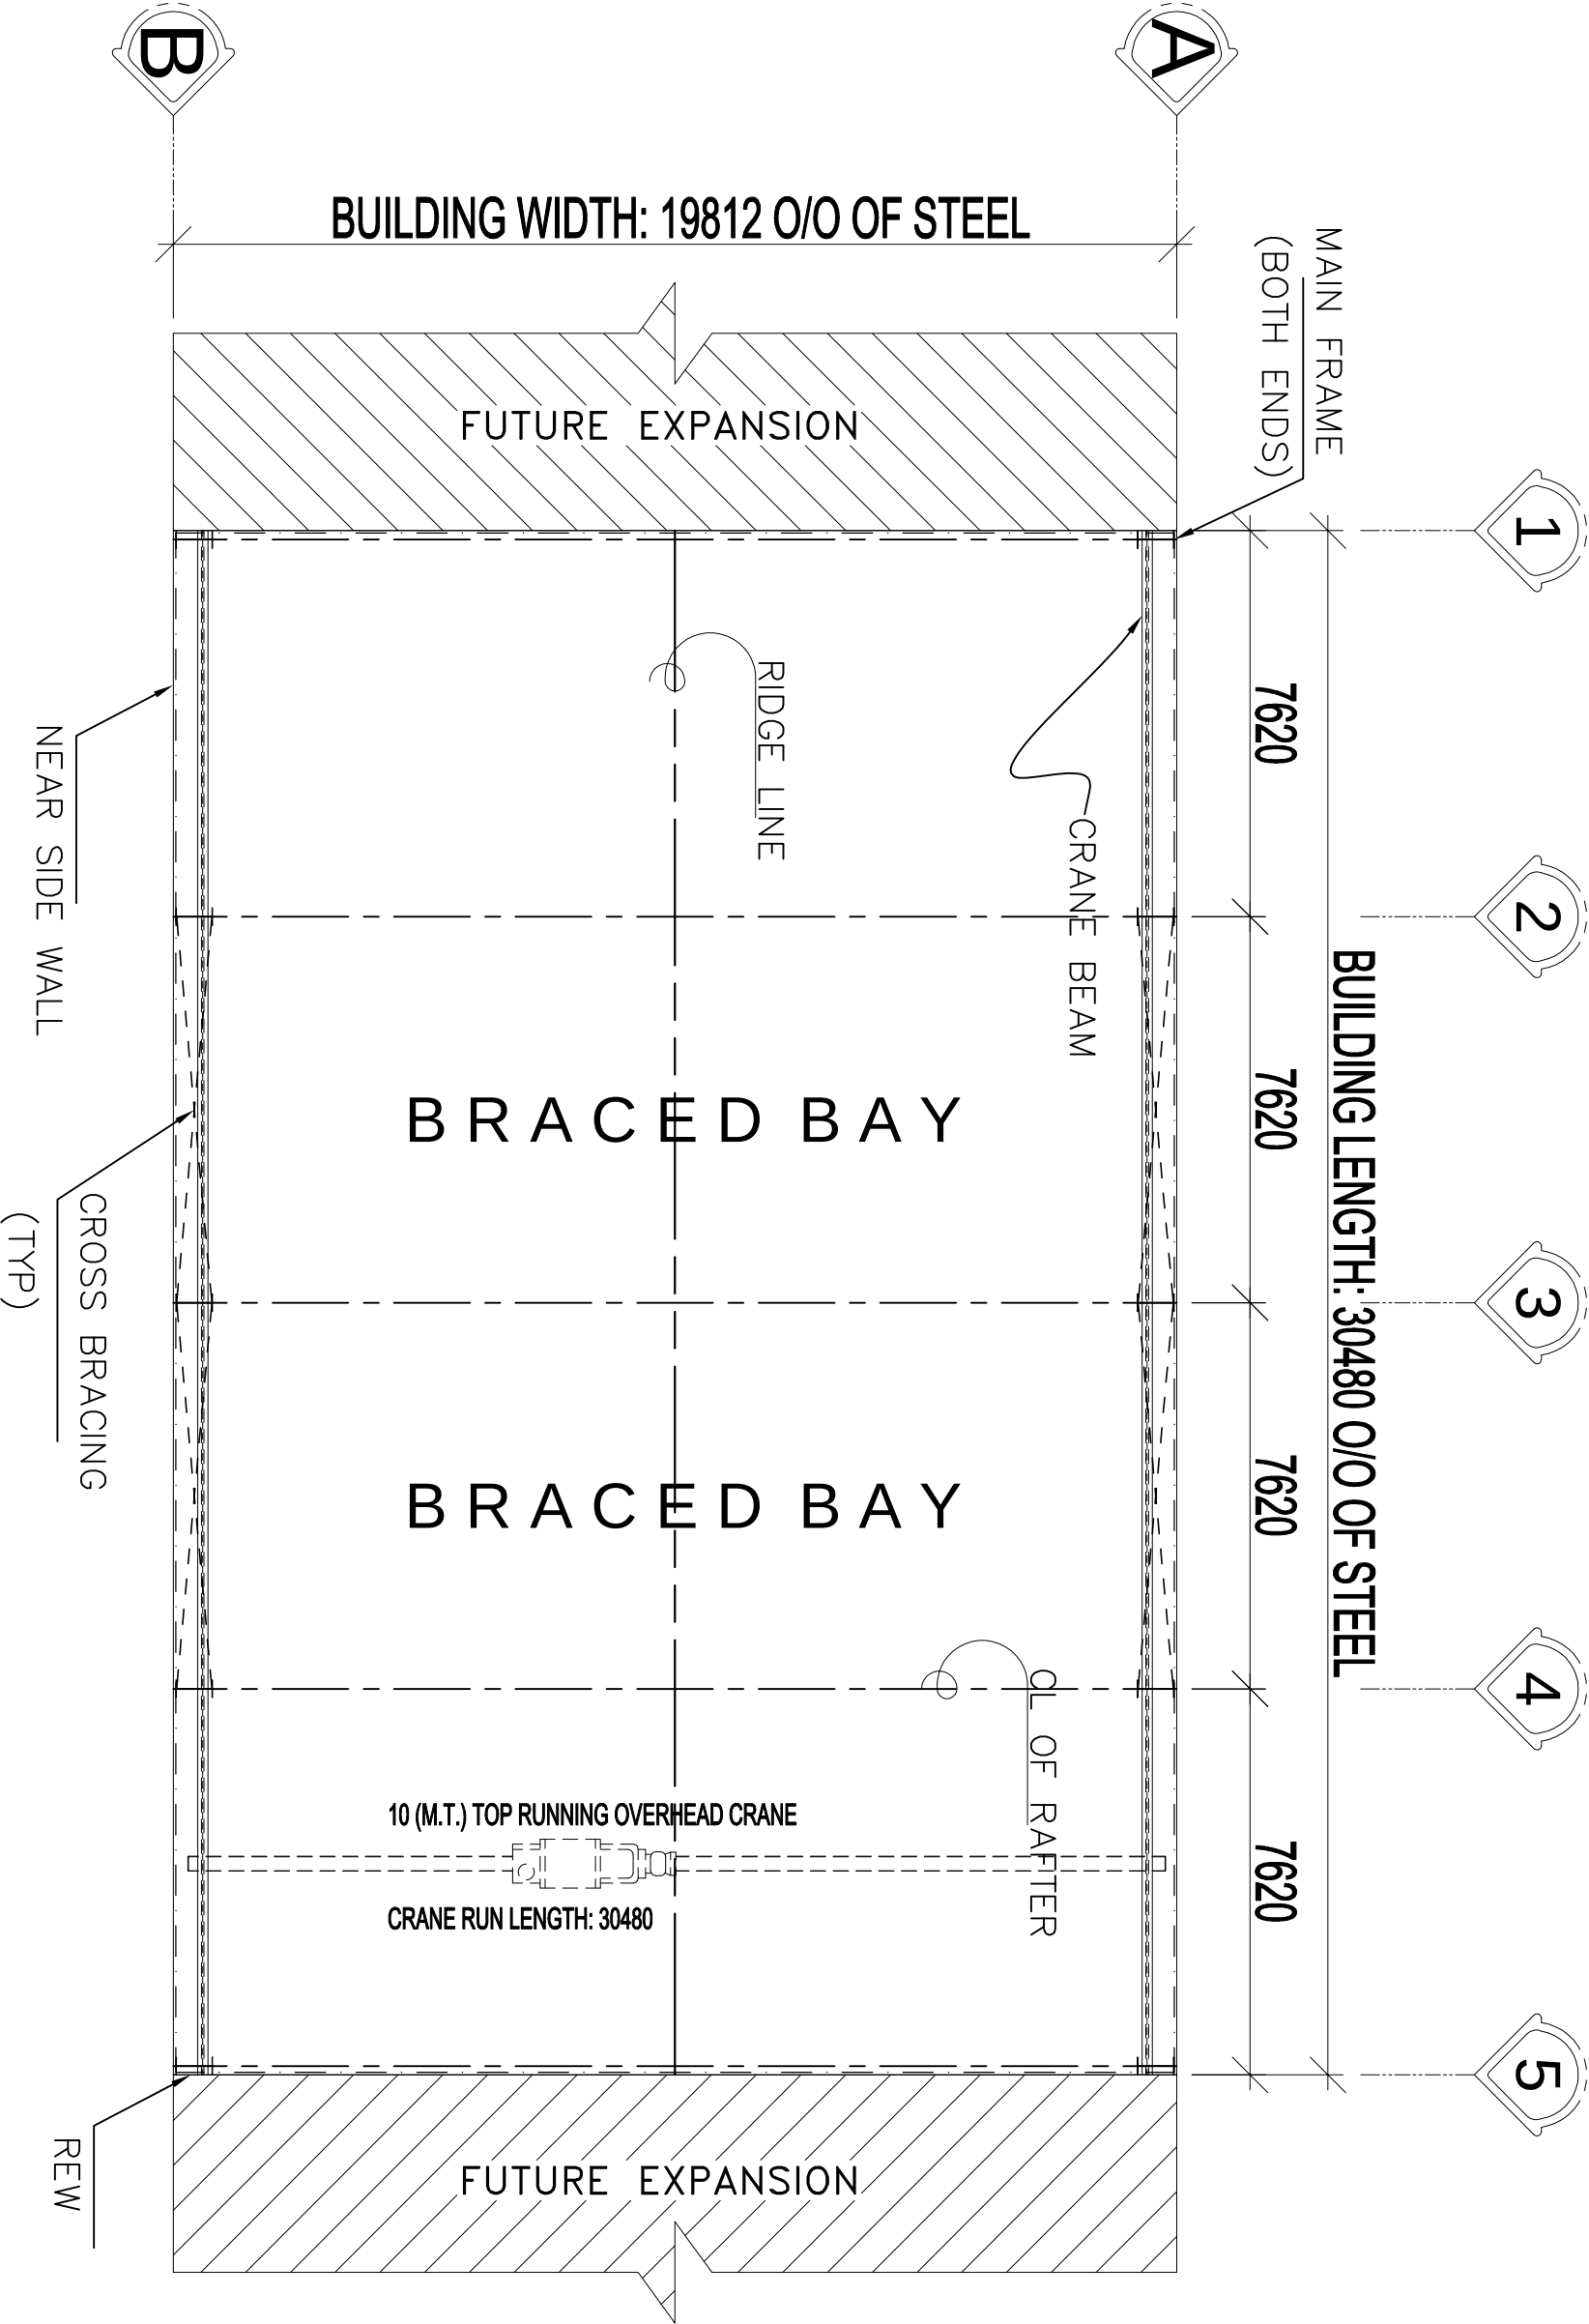


COLUMN LAY-OUT PLAN

- General Notes**
1. All dimensions are in millimeters (mm).
 2. Panel thickness is the Total Coated Thickness (TCTP).
 3. All Dimensions, Levels Shown in the PROPOSAL DRAWING is indicative only, final design Dimensions, Levels will be shown in our APPROVAL DRAWING in design stage.
 4. For panel description, Please refer to technical and material proposal

This document is PROPOSAL
DRAWING data of MAMMUT
BUILDING SYSTEMS FZC.
not for construction.

00		03-10-2013		JAS	NASIR
Rev. No.	Date	DSN	DRN	CHK	
PROJECT :					
PROPOSED STEEL BUILDING					
CUSTOMER :					
03-10-2013					
STEEL CONTRACTOR:					
 Lahore Office 1st Floor, Q-429, Phase-II, Defense Housing Authority Lahore Cantt-Haddisai Website: www.mammutgroup.com Phone : +92-42) 574 3065-68 Fax : + (92-42) 589 8896					
QUOTE NO.		: PK-013-169			
Bldg. No.		: 01			
Bldg. Name		: STEEL SHED			
No. Of Identical Bldg.		: ONE			
Drawing Title :					
ROOF SHEETING PLAN					
Scale		Sheet Size		Sheet No.	
N.T.S.		A4		1 of 4	

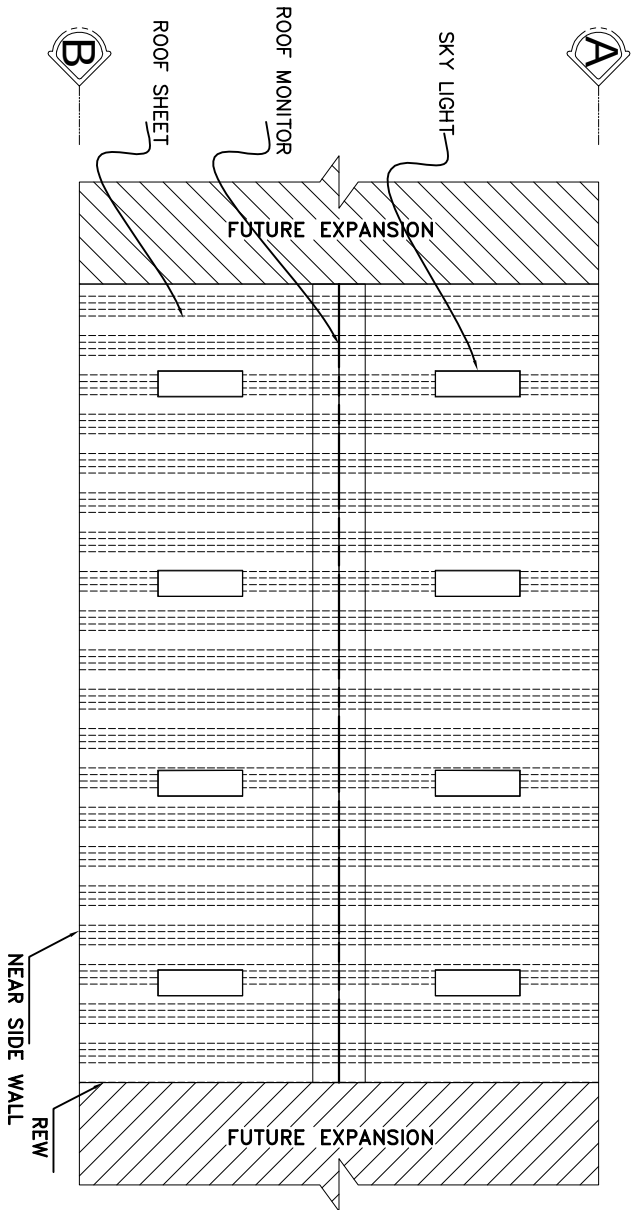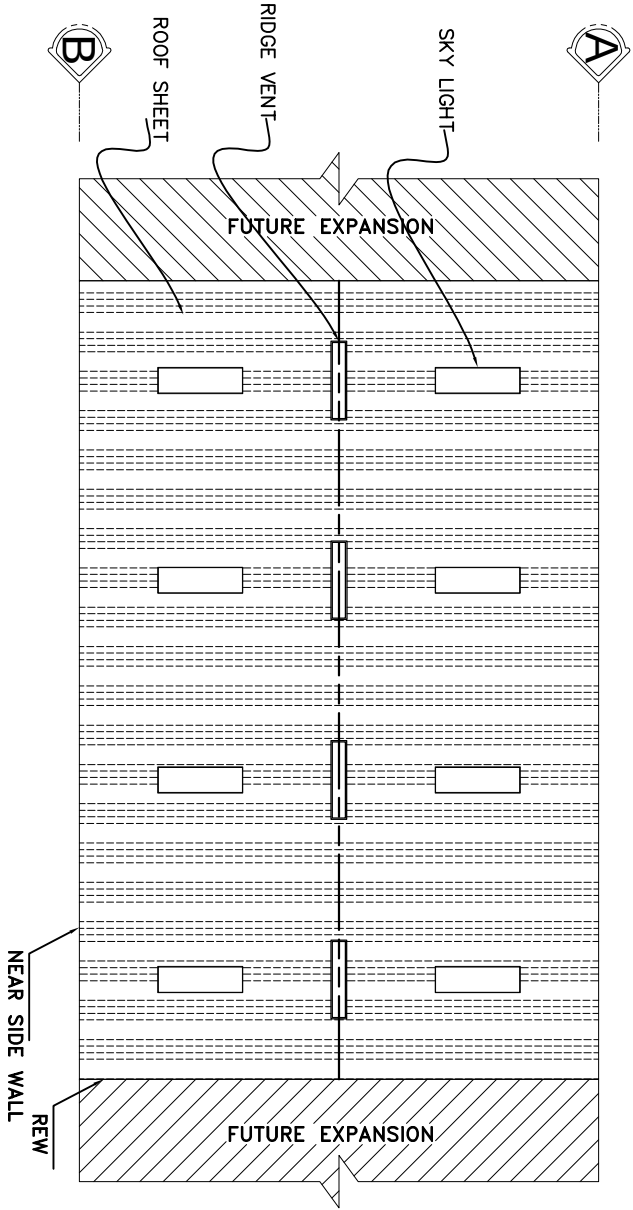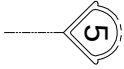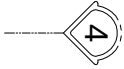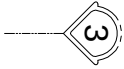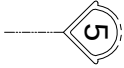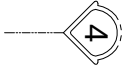


ROOF SHEETING PLAN (OPTION NO_1)

ROOF SHEETING PLAN (OPTION NO_2)

- General Notes**
1. All dimensions are in millimeters (mm).
 2. Panel thickness is the Total Coated Thickness (TCTP).
 3. All Dimensions, Levels Shown in the PROPOSAL DRAWING is indicative only, final design Dimensions, Levels will be shown in our APPROVAL DRAWING in design stage.
 4. For panel description, Please refer to technical and material proposal

This document is PROPOSAL
DRAWING data of MAMMUT
BUILDING SYSTEMS FZC.
not for construction.

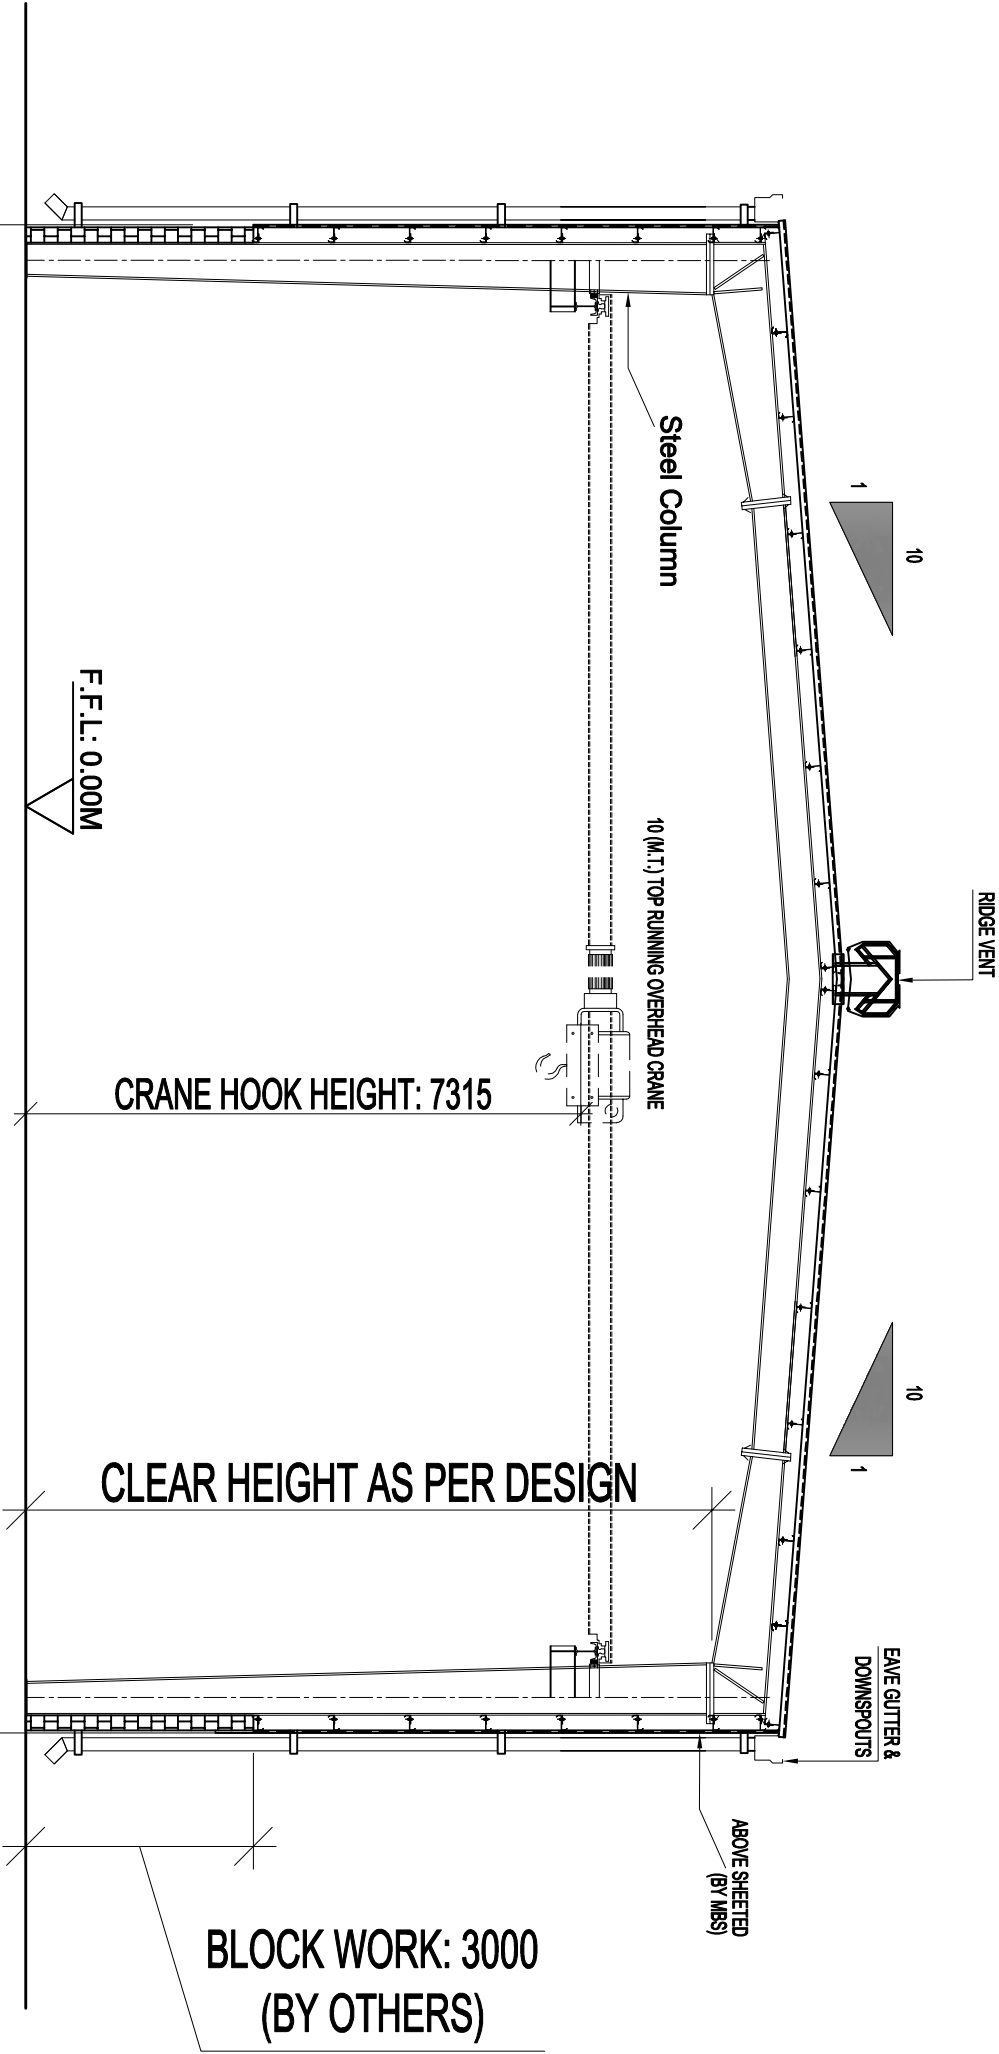


TYPICAL RIGID FRAME CROSS SECTION

AT GL 2 THRU 4 (OPTION NO_1)

00	09-10-2013	JAS	NASIR
Rev No	Date	DSN	DRN
CHK			
PROJECT :			
PROPOSED STEEL BUILDING			
CUSTOMER :			
ZEALCON ENGINEERING			
STEEL CONTRACTOR :			
MAMMUT Building Systems FZC			
Labore Office 1st Floor, Q-429, Phase-II, Defense Housing Authority Website: www.mammutgroup.com Phone : +92-42) 574 3066-68 Fax : +92-42) 589 8896			
QUOTE NO. : PK-013-169			
Bldg. No. : 01			
Bldg. Name : STEEL SHED			
No. Of Identical Bldg. : ONE			
Drawing Title :			
CROSS SECTION			
Scale	Sheet No.	Sheet No.	
N.T.S.	A4	3 of 4	

- General Notes**
1. All dimensions are in millimeters (mm).
 2. Panel thickness is the Total Coated Thickness (TCTP).
 3. All Dimensions, Levels Shown in the PROPOSAL DRAWING is indicative only, final design Dimensions, Levels will be shown in our APPROVAL DRAWING in design stage.
 4. For panel description, Please refer to technical and material proposal

This document is PROPOSAL
DRAWING data of MAMMUT
BUILDING SYSTEMS FZC.
not for construction.

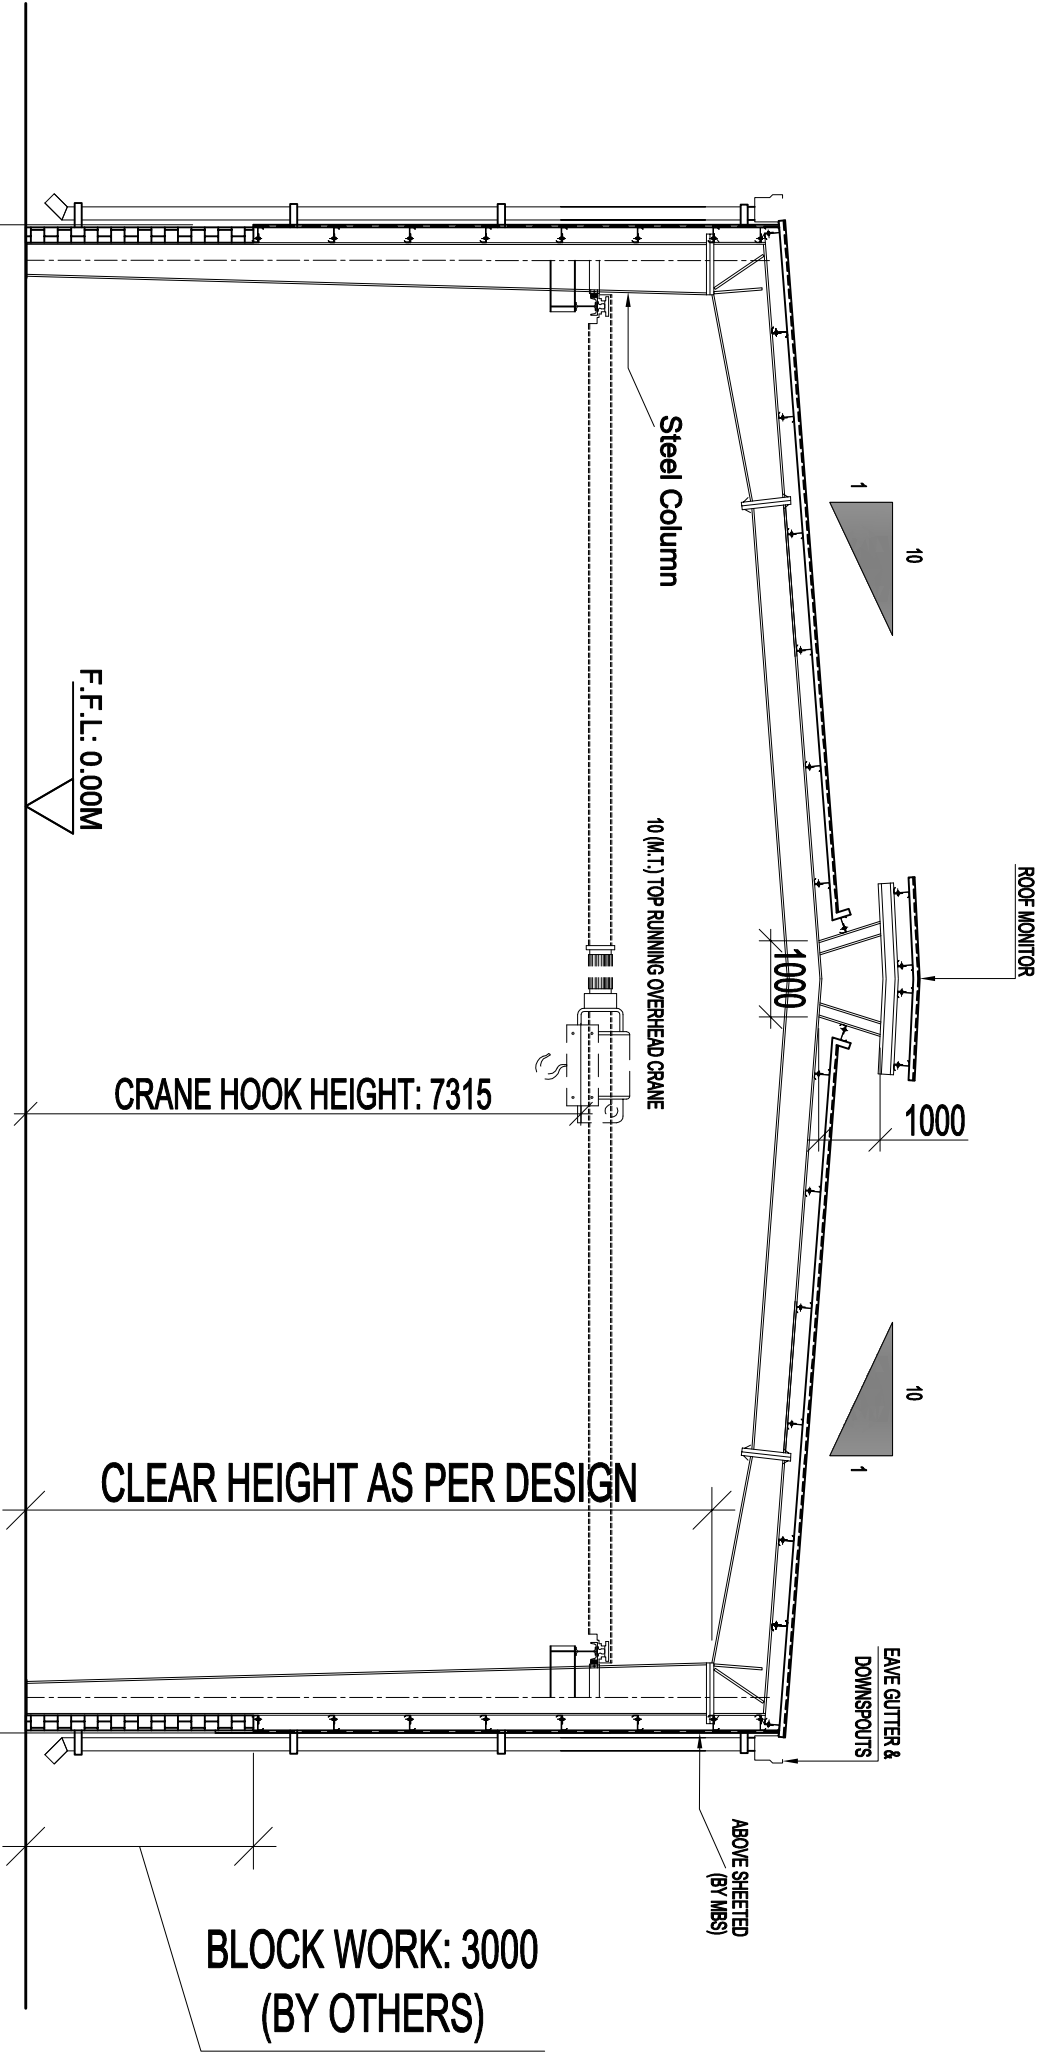

TYPICAL RIGID FRAME CROSS SECTION

AT GL 2 THRU 4 (OPTION NO_2)

00	09-10-2013	JAS	NASIR
Rev No	Date	DSN	DRN
CHK			
PROJECT :			
PROPOSED STEEL BUILDING			
CUSTOMER :			
ZEALCON ENGINEERING			
STEEL CONTRACTOR :			
MAMMUT Building Systems FZC			
Labore Office 1st Floor, Q-429, Phase-II, Defense Housing Authority Website: www.mammutgroup.com Phone : +92-42) 574 3066-68 Fax : +92-42) 589 8896			
QUOTE NO. : PK-013-169			
Bldg. No. : 01			
Bldg. Name : STEEL SHED			
No. Of Identical Bldg. : ONE			
Drawing Title :			
CROSS SECTION			
Scale	Sheet No.	Sheet No.	
N.T.S.	A4	3 of 4	